



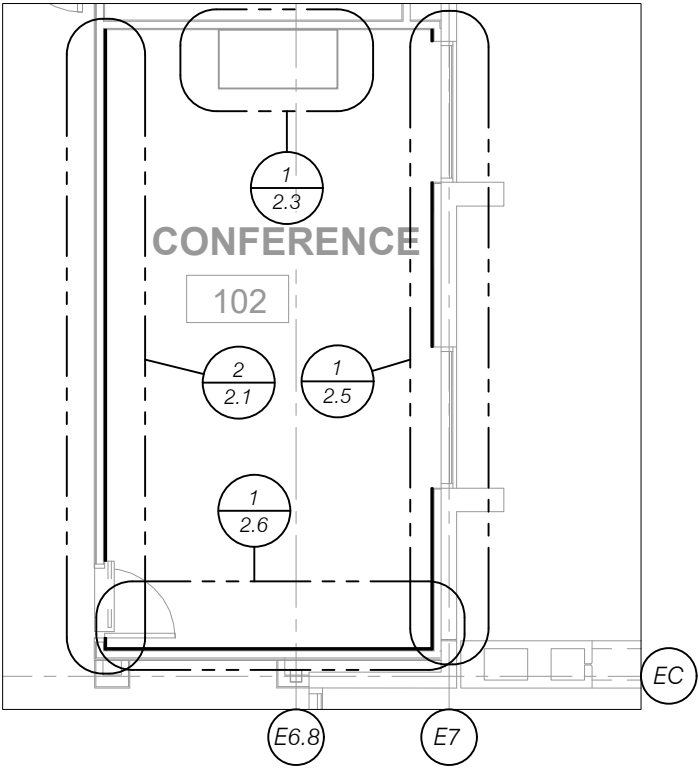

1 KEY PLAN
SCALE: NTS
ARCH REF: 1/AE101.1

NOTES	
1	ALL DIMENSIONS TO BE FIELD VERIFIED
2	GENERAL CONTRACTOR TO COORDINATE ALL FRAMING REQUIREMENTS WITH CMI
3	GENERAL CONTRACTOR TO COORDINATE ALL WALL TYPES, THICKNESSES AND ROUGH OPENINGS
4	GENERAL CONTRACTOR & ELECTRICAL CONTRACTOR TO COORDINATE ALL ELECTRICAL BOX LOCATIONS & REQUIREMENTS WITH MILLWORK DRAWINGS
5	GENERAL CONTRACTOR & ELECTRICAL CONTRACTOR TO COORDINATE ALL LIGHT FIXTURE FEED & SWITCHING LOCATIONS WITH MILLWORK DRAWINGS
6	GENERAL CONTRACTOR & PLUMBING CONTRACTOR TO COORDINATE ALL PLUMBING FIXTURES & INSTALLATION REQUIREMENTS

	MATERIALS
(PG-C)	(CR-1) FINGER JOINT PINE, DELIVERED PRIME (PREPPING, PAINTING, FILLING OF ATTACHMENT HOLES BY OTHERS)

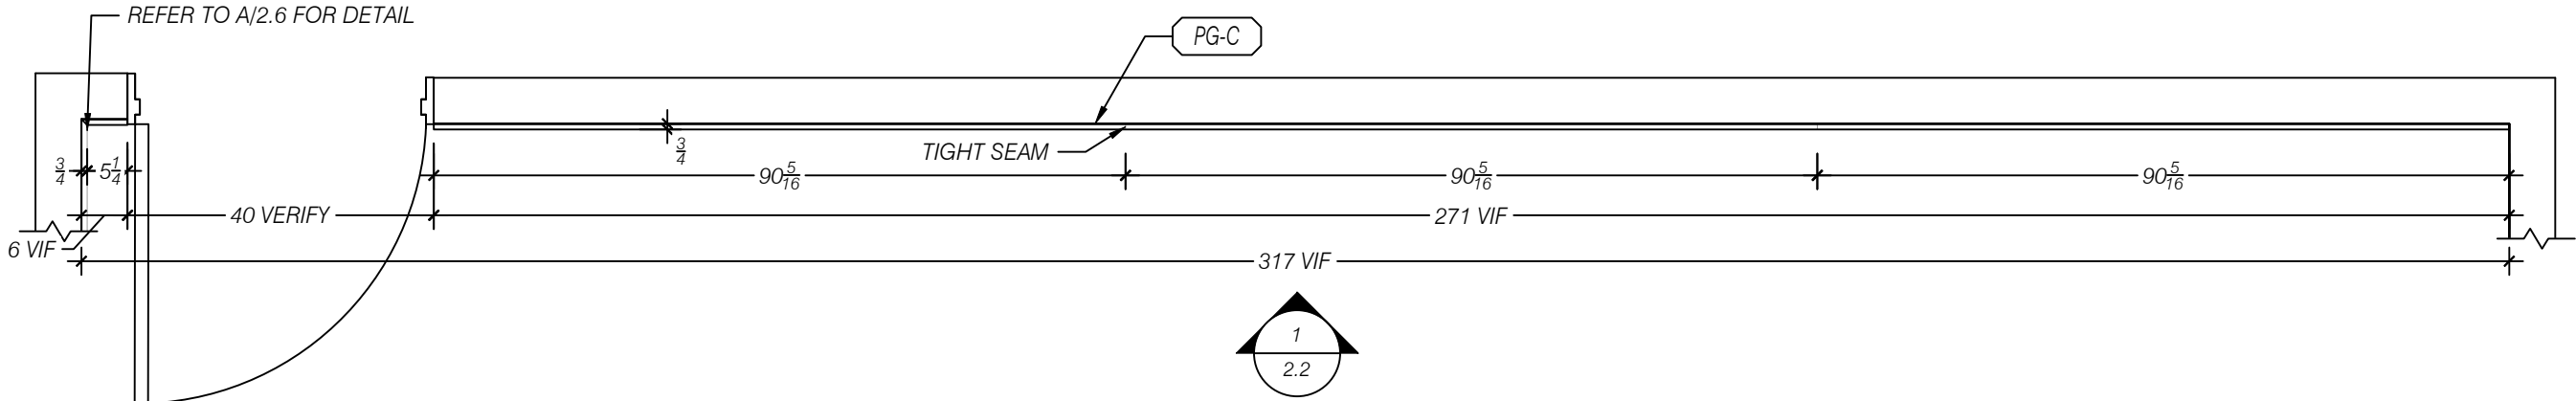

2 PLAN - CONFERENCE 102
SCALE 1:24 (1/2"=1'-0")
ARCH REF: 1/AE406



CRESTMARK
MILLWORK

5640 WEST END ROAD
ARCATA, CA 95521
PH (707) 822-4034 FAX (707) 822-5478
WWW.CRESTMARKMILLWORK.COM

DGS SREOC COSTA


MESA

CONFERENCE 102

ISSUE		BY
DATE	DESCRIPTION	
05/20/2026	REV-A FOR SUBMITTAL	Q-AS
-	-	-
-	-	-
-	-	-
-	-	-
-	-	-
SITE ADDRESS		
STREET	2301 South Shelley Circle Bldg. A & B	
CITY	Costa Mesa	
STATE	CA	ZIP 92626
JOB #:	26034	REV: A
MOD #:	2	REL: N/A
2.1		

CENTERLINE OF IN-WALL STRAPPING
(STRAPPING BY OTHERS)

30 A.F.F.

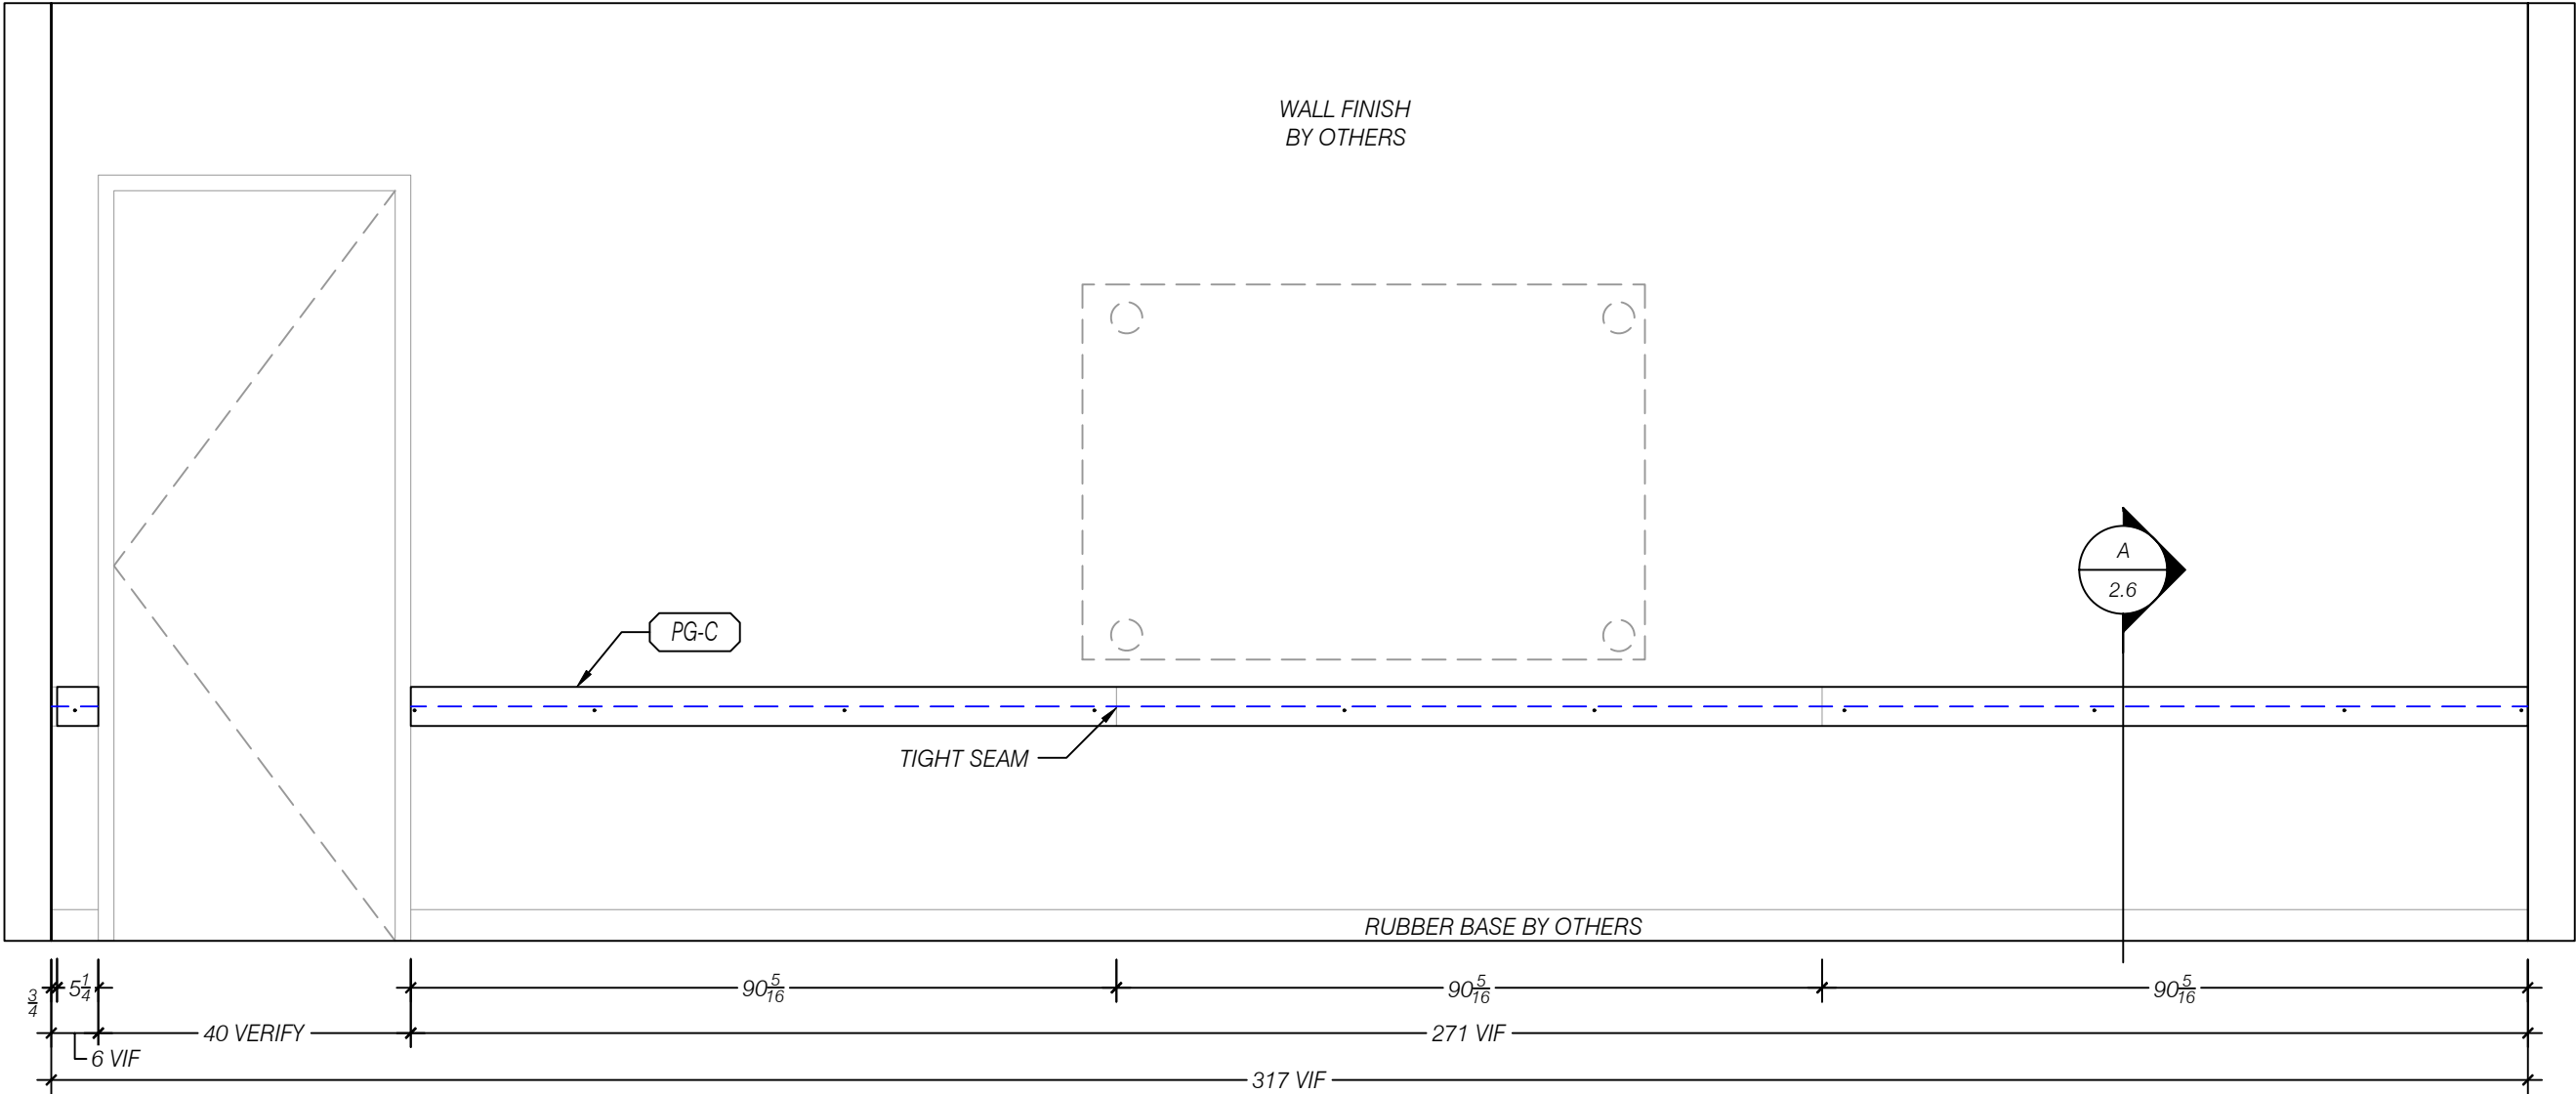

1 ELEVATION WEST - CONFERENCE 102
SCALE 1:24 (1/2"=1'-0")
ARCH REF: 9/AE406



	MATERIALS
(PG-C)	(CR-1) FINGER JOINT PINE, DELIVERED PRIME (PREPPING, PAINTING, FILLING OF ATTACHMENT HOLES BY OTHERS)



5640 WEST END ROAD
ARCATA, CA 95521
PH (707) 822-4034 FAX (707) 822-5478
WWW.CRESTMARKMILLWORK.COM

**DGS SREOC COSTA
MESA
CONFERENCE 102**

ISSUE		BY
DATE	DESCRIPTION	
05/20/2026	REV-A FOR SUBMITTAL	Q-AS
-	-	-
-	-	-
-	-	-
-	-	-
-	-	-
SITE ADDRESS		
STREET	2301 South Shelley Circle Bldg. A & B	
CITY	Costa Mesa	
STATE	CA	ZIP 92626
JOB #:	26034	REV: A
MOD #:	2	REL: N/A
2.2		

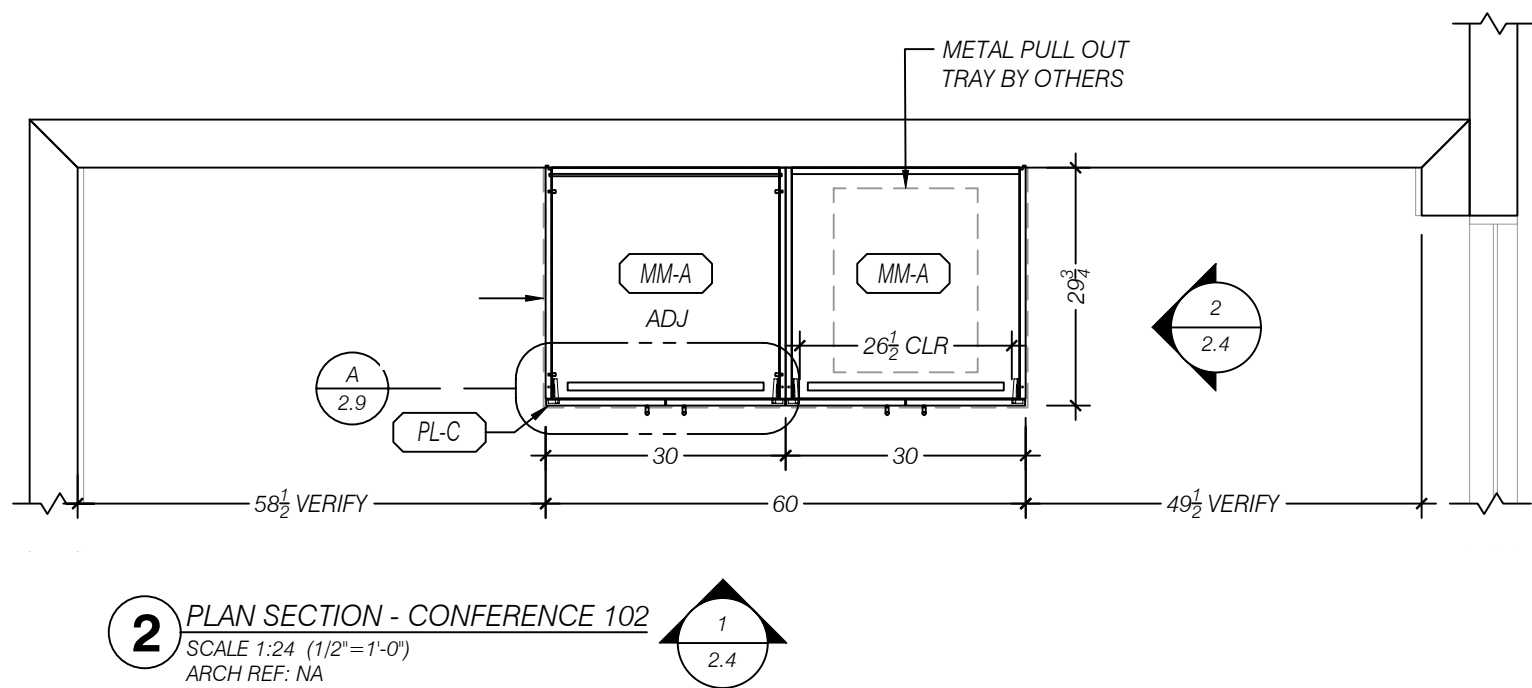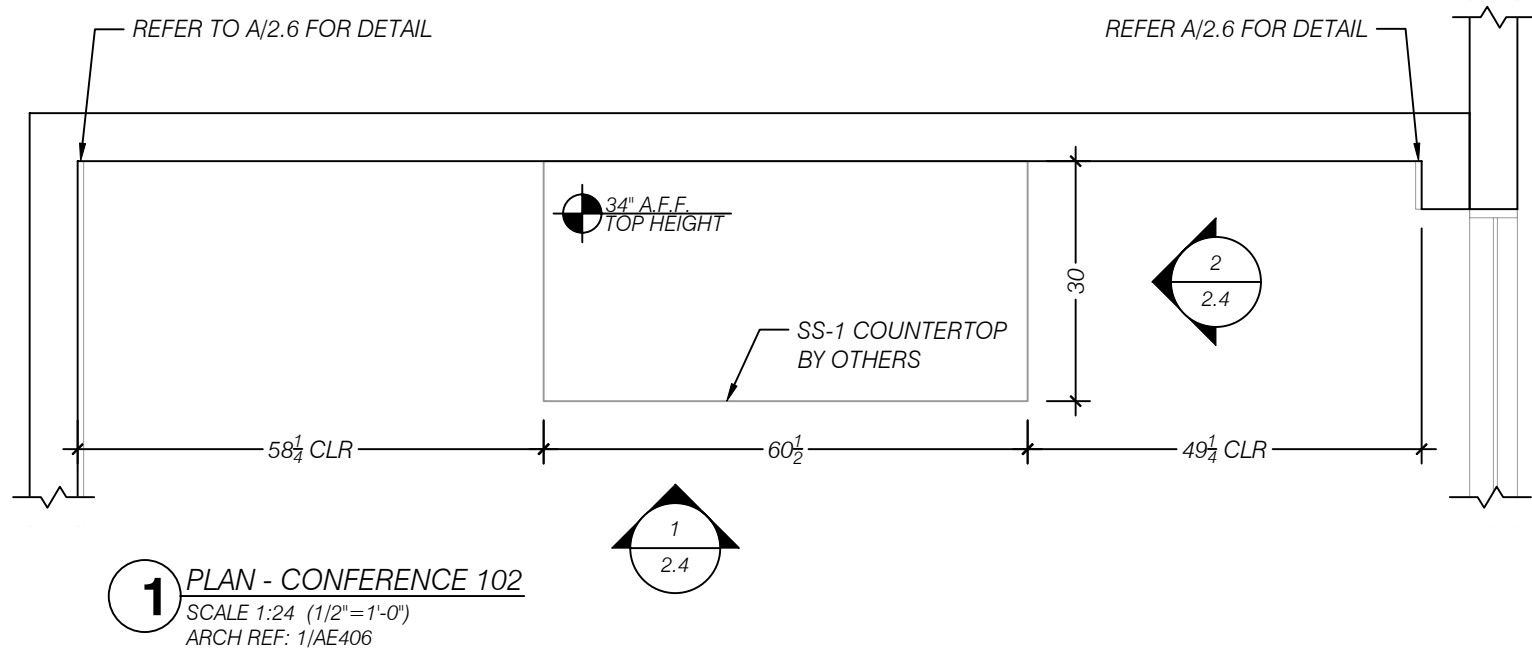

		MATERIALS
MM-A		WHITE MELAMINE
PL-C		(PL-1, WB-2) WILSONART "HARVEST MAPLE", 7953-38, FINE VELVET TEXTURE
	QTY.	HARDWARE
H-1.2	X	SALICE 0mm CLIP-ON HINGE PLATE EURO SCREW, BARGR09/16
H-1.3	X	SALICE 110° FO SOFT-CLOSE, LOGICA SILENTIA, C7J6AE9
H-3.0	X	BERENSON WIRE PULL, BN6131-2SC-P, 96mm CTC, SATIN CHROME FINISH
H-4.0	X	HAFELE SHELF SUPPORT, 282.04.711, 5mm SHELF PIN, STEEL NICKEL-PLATED
H-9.5	X	MOCKETT, GT-METAL AIR VENT GRILLE, 17"W x 4"H OPENING, MATTE BLACK FINISH W/ MESH/3

DGS SREOC COSTA


MESA

CONFERENCE 102

ISSUE				
DATE	DESCRIPTION	BY		
05/20/2026	REV-A FOR SUBMITTAL	Q-AS		
SITE ADDRESS				
STREET	2301 South Shelley Circle Bldg. A & B			
CITY	Costa Mesa			
STATE	CA	ZIP	92626	
JOB #:	26034	REV:	A	
MOD #:	2	REL:	N/A	
2.3				


CENTERLINE OF IN-WALL STRAPPING
(STRAPPING BY OTHERS)

31 A.F.F.
5 A.F.F.

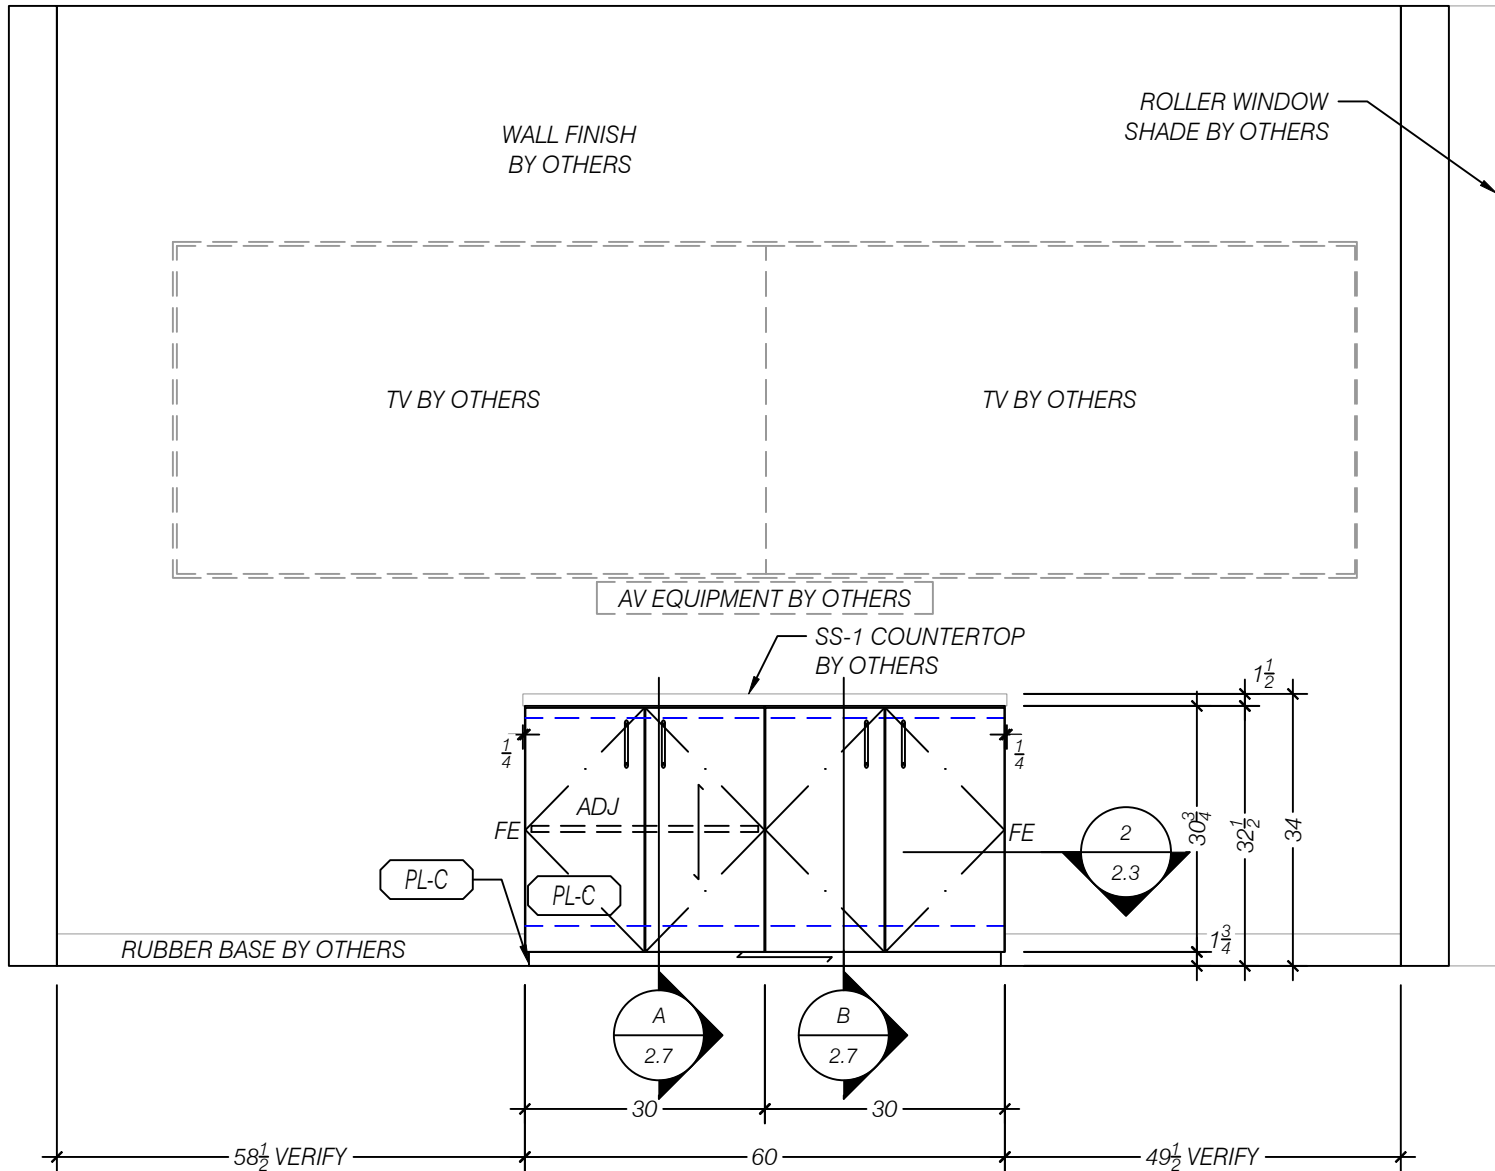

1 ELEVATION NORTH - CONFERENCE 102
SCALE 1:24 (1/2" = 1'-0")
ARCH REF: 6/AE406


		MATERIALS
(MM-A)		WHITE MELAMINE
(PL-C)		(PL-1, WB-2) WILSONART "HARVEST MAPLE", 7953-38, FINE VELVET TEXTURE
	QTY.	HARDWARE
H-1.2	X	SALICE 0mm CLIP-ON HINGE PLATE EURO SCREW, BARGR09/16
H-1.3	X	SALICE 110° FO SOFT-CLOSE, LOGICA SILENTIA, C7J6AE9
H-3.0	X	BERENSON WIRE PULL, BN6131-2SC-P, 96mm CTC, SATIN CHROME FINISH
H-4.0	X	HAFELE SHELF SUPPORT, 282.04.711, 5mm SHELF PIN, STEEL NICKEL-PLATED
H-9.5	X	MOCKETT, GT-METAL AIR VENT GRILLE, 17"W x 4"H OPENING, MATTE BLACK FINISH W/ MESH/3

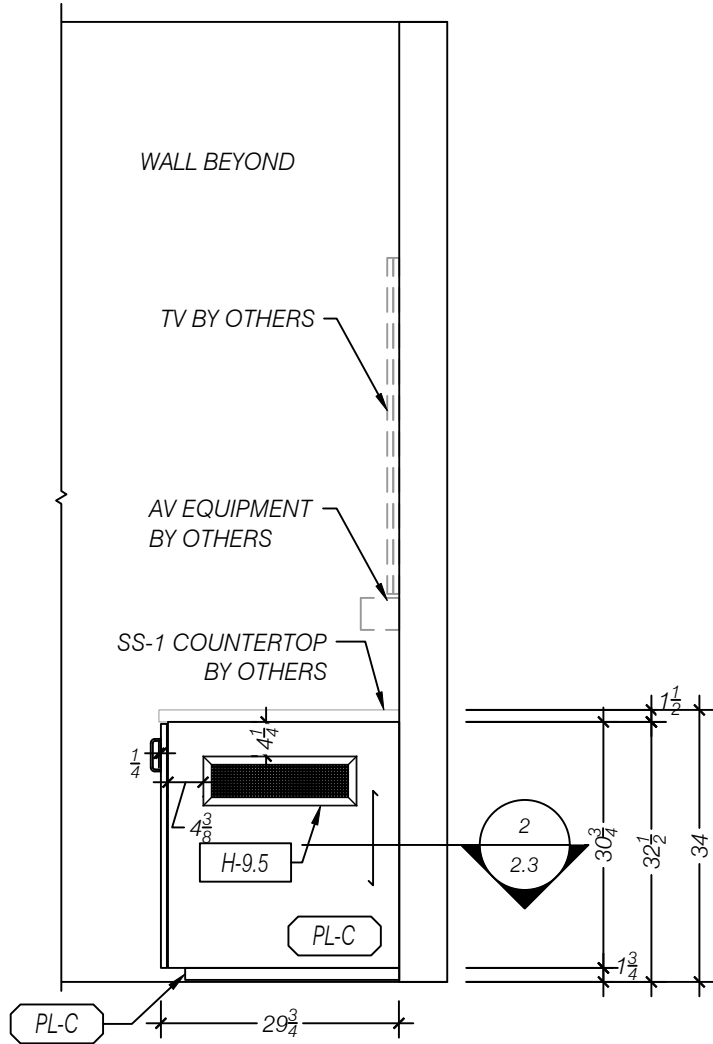



2 ELEVATION WEST - CONFERENCE 102
SCALE 1:24 (1/2" = 1'-0")
ARCH REF: NA

DGS SREOC COSTA
MESA
CONFERENCE 102

ISSUE		BY
DATE	DESCRIPTION	
05/20/2026	REV-A FOR SUBMITTAL	Q-AS
-	-	-
-	-	-
-	-	-
-	-	-
-	-	-
SITE ADDRESS		
STREET	2301 South Shelley Circle Bldg. A & B	
CITY	Costa Mesa	
STATE	CA	ZIP 92626
JOB #:	26034	REV: A
MOD #:	2	REL: N/A

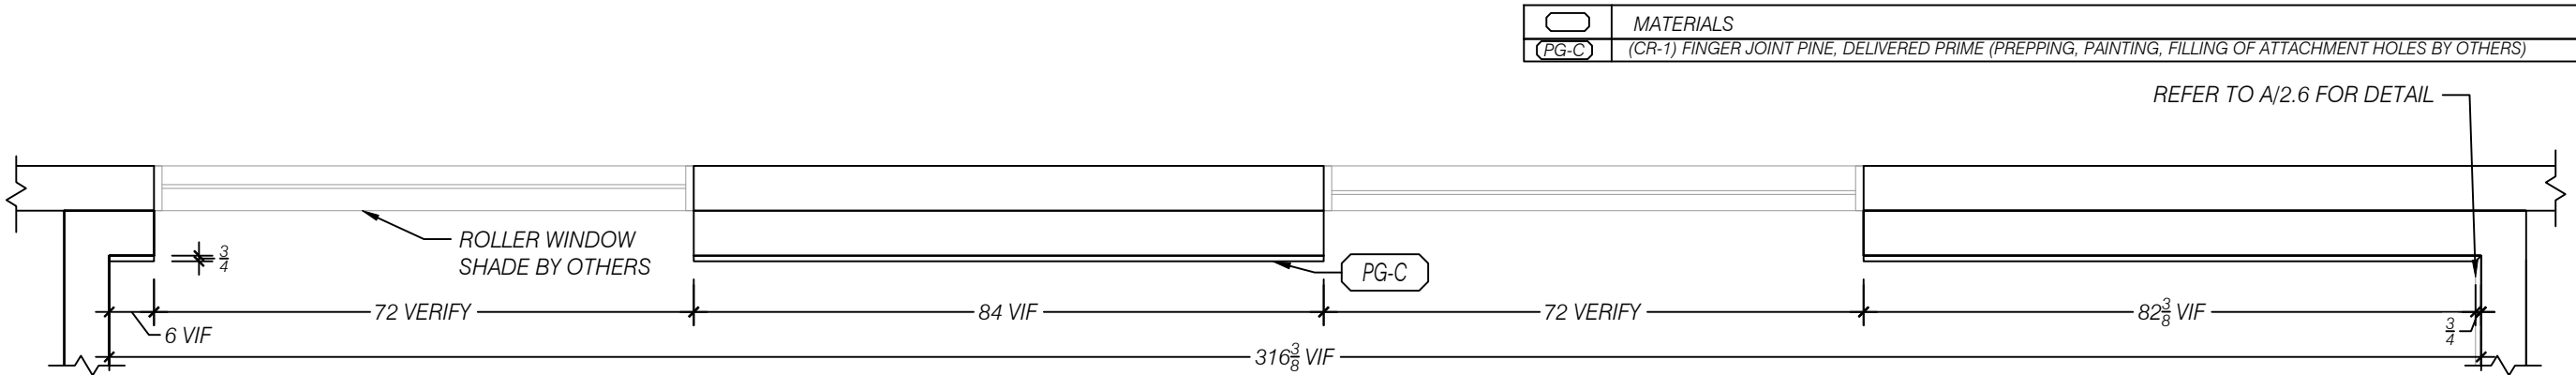

1 PLAN - CONFERENCE 102
SCALE 1:24 (1/2"=1'-0")
ARCH REF: 1/AE406

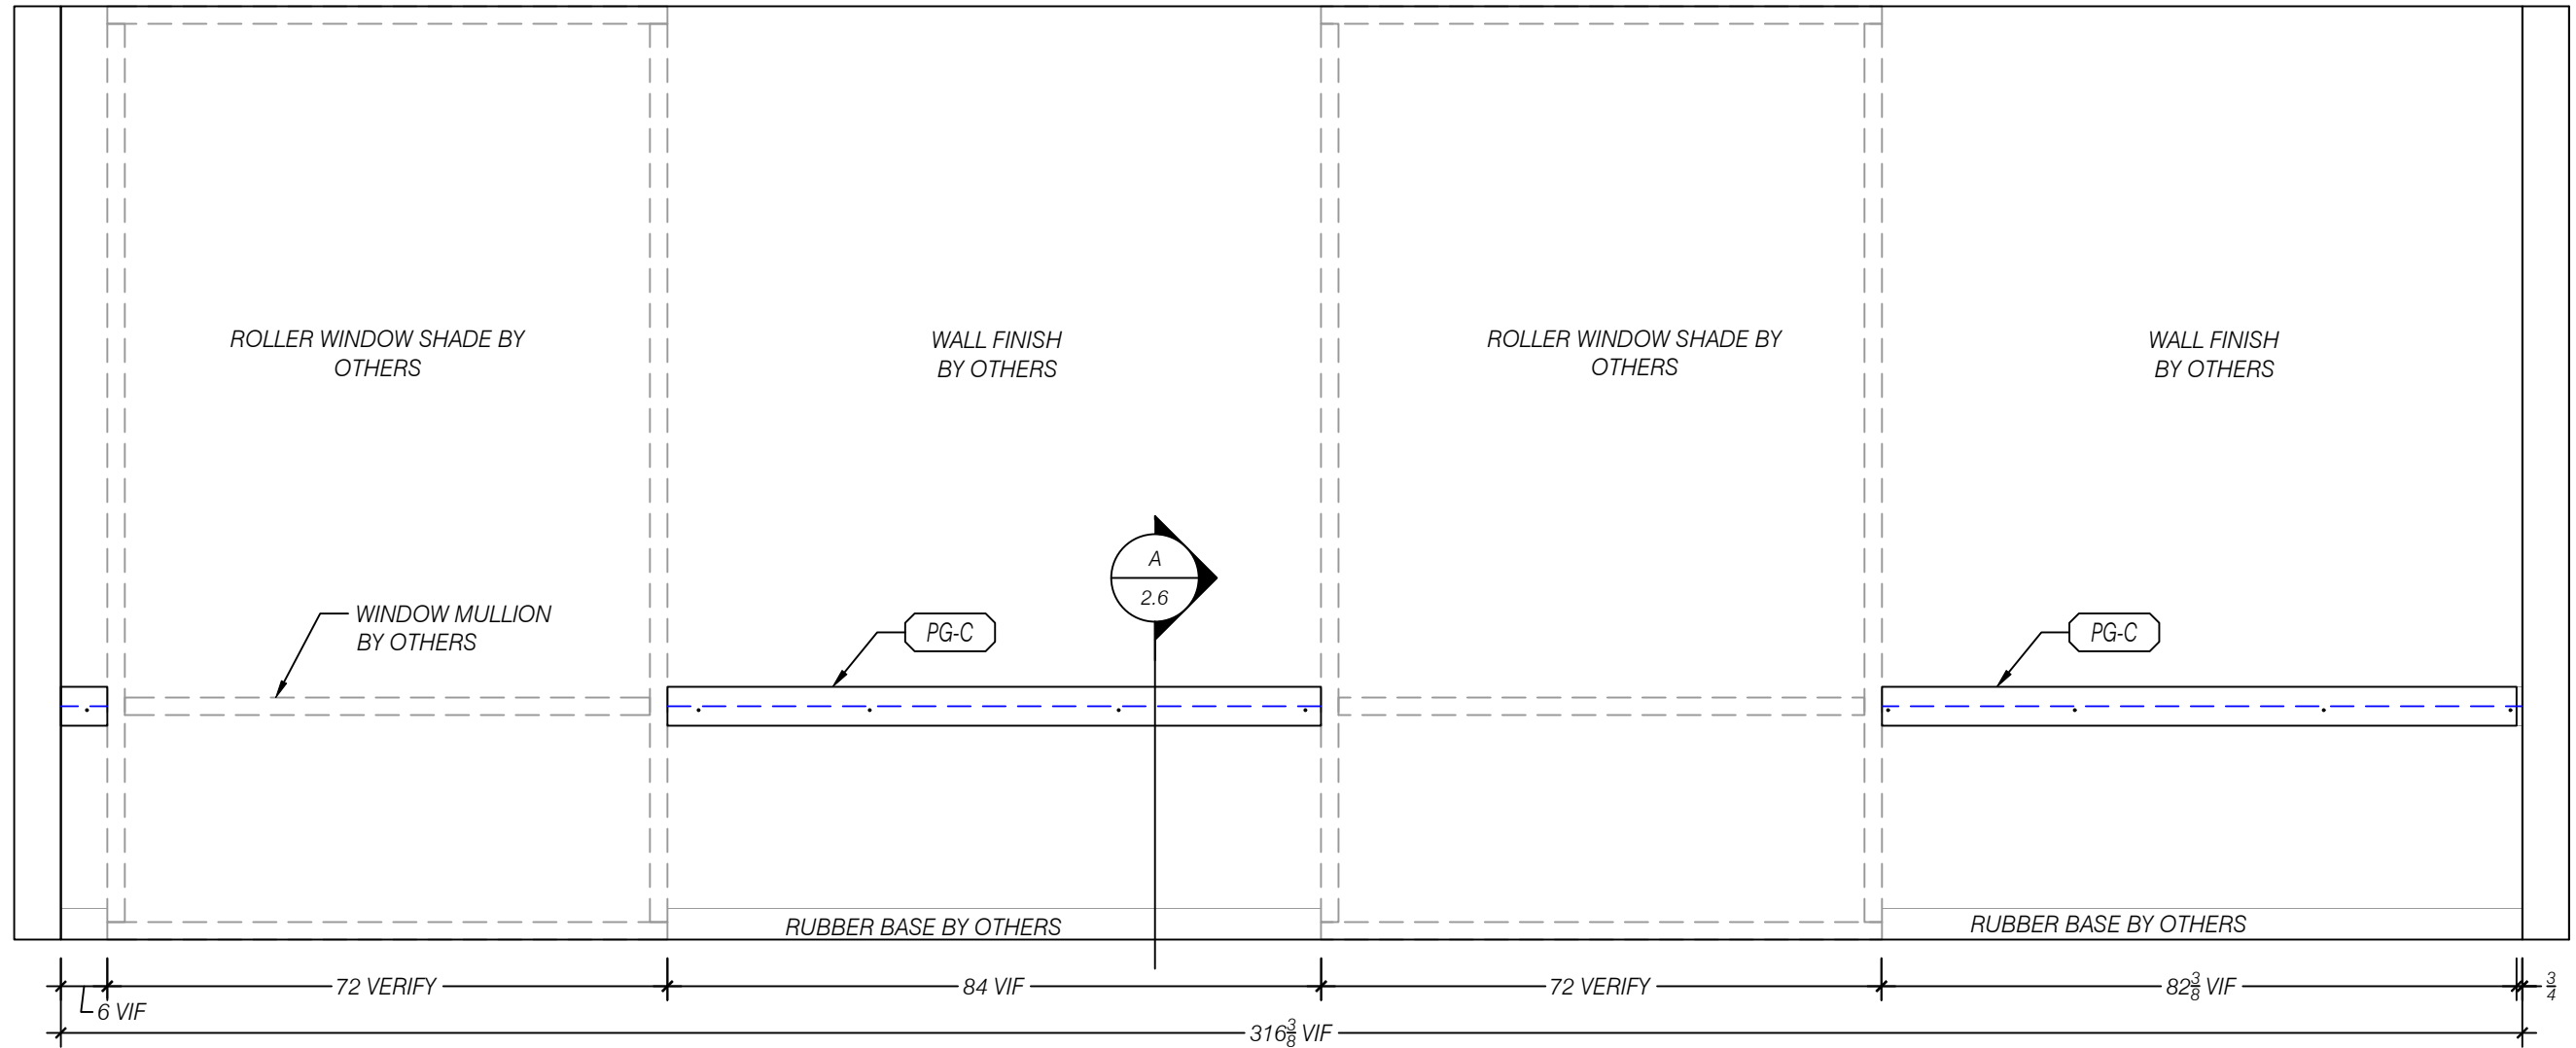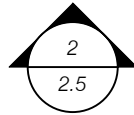

2 ELEVATION EAST - CONFERENCE 102
SCALE 1:24 (1/2"=1'-0")
ARCH REF: 7/AE406



5640 WEST END ROAD
ARCATA, CA 95521
PH (707) 822-4034 FAX (707) 822-5478
WWW.CRESTMARKMILLWORK.COM

**DGS SREOC COSTA
MESA
CONFERENCE 102**

ISSUE		BY
DATE	DESCRIPTION	
05/20/2026	REV-A FOR SUBMITTAL	Q-AS
-	-	-
-	-	-
-	-	-
-	-	-
-	-	-
SITE ADDRESS		
STREET	2301 South Shelley Circle Bldg. A & B	
CITY	Costa Mesa	
STATE	CA	ZIP 92626
JOB #:	26034	REV: A
MOD #:	2	REL: N/A
2.5		