



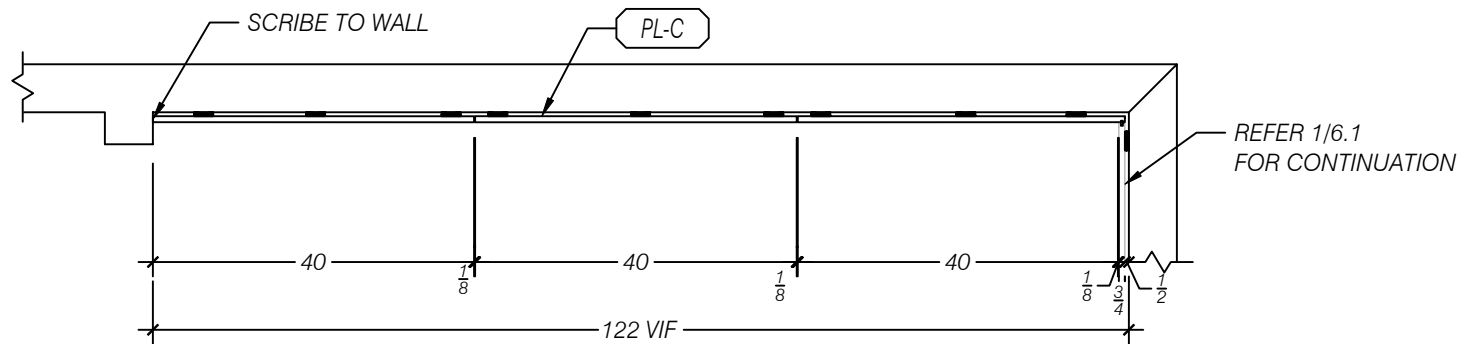

1 PLAN SECTION - BREAK ROOM 115
SCALE 1:24 (1/2"=1'-0")
ARCH REF: 1/AE407


CENTERLINE OF IN-WALL STRAPPING
(STRAPPING BY OTHERS)

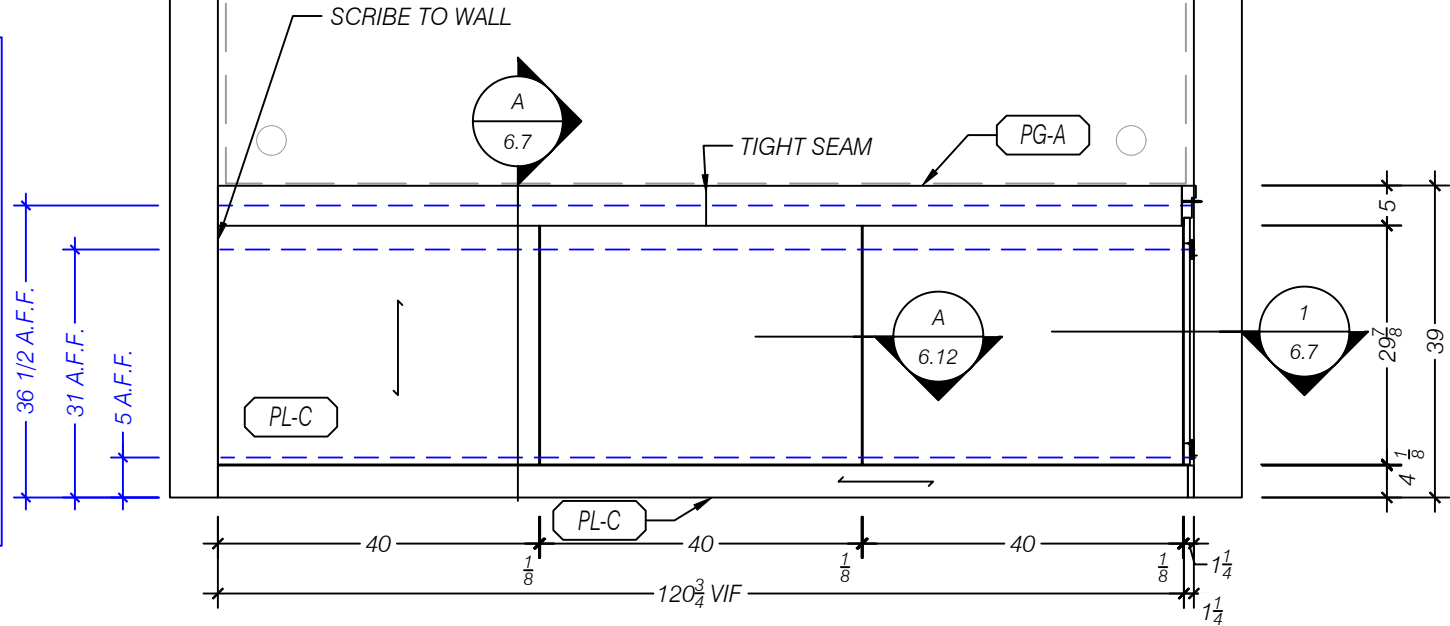

2 ELEVATION NORTH - BREAK ROOM 115
SCALE 1:24 (1/2"=1'-0")
ARCH REF: 2/AE407

	MATERIALS
(PG-A)	(CR-1) SOLID POPLAR, DELIVERED PRIMED (PREPPING, PAINTING, FILLING OF ATTACHMENT HOLES BY OTHERS)
(PL-C)	(PL-1, WB-2) WILSONART "HARVEST MAPLE", 7953-38, FINE VELVET TEXTURE
	QTY. HARDWARE
(H-7.1)	X ORANGE ALUMINUM Z-CLIP HD PANEL RAIL

CENTERLINE OF IN-WALL STRAPPING
(STRAPPING BY OTHERS)

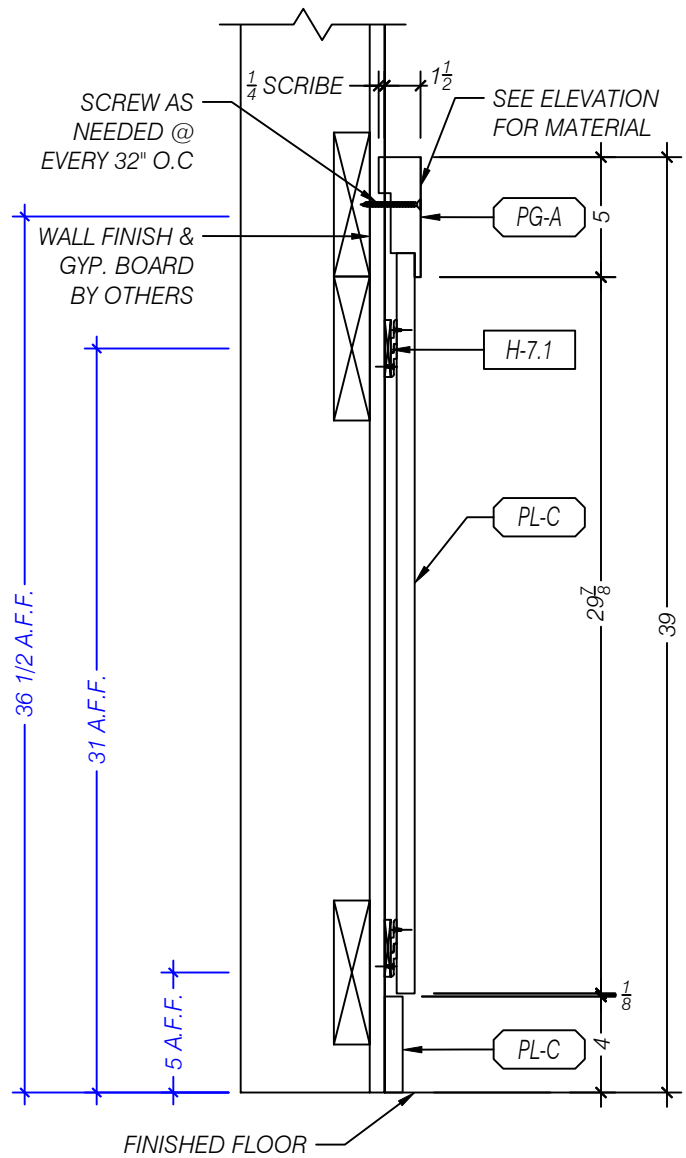

A SECTION - PANELLING
SCALE 1:24 (1/2"=1'-0")
ARCH REF: NA

DGS SREOC COSTA
MESA
BREAK ROOM 115

ISSUE	DESCRIPTION	BY
DATE	05/20/2026	Q-AS
	REV-A FOR SUBMITTAL	-
	-	-
	-	-
	-	-
	-	-

SITE ADDRESS			
STREET	2301 South Shelley Circle Bldg. A & B		
CITY	Costa Mesa		
STATE	CA	ZIP	92626
JOB #:	26034	REV:	A
MOD #:	6	REL:	N/A

6.7