



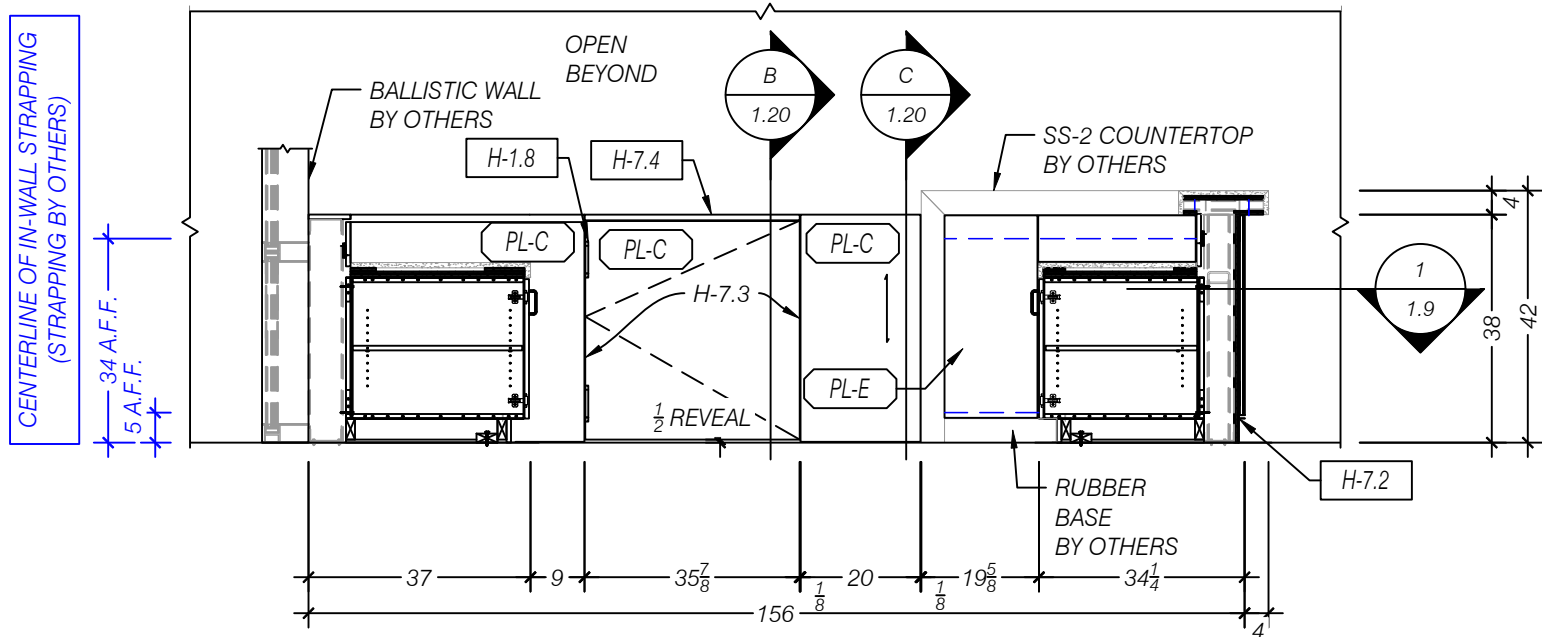

1 ELEVATION NORTH - RECEPTION
SCALE 1:32 (3/8"=1'-0")
ARCH REF: 3/AE580

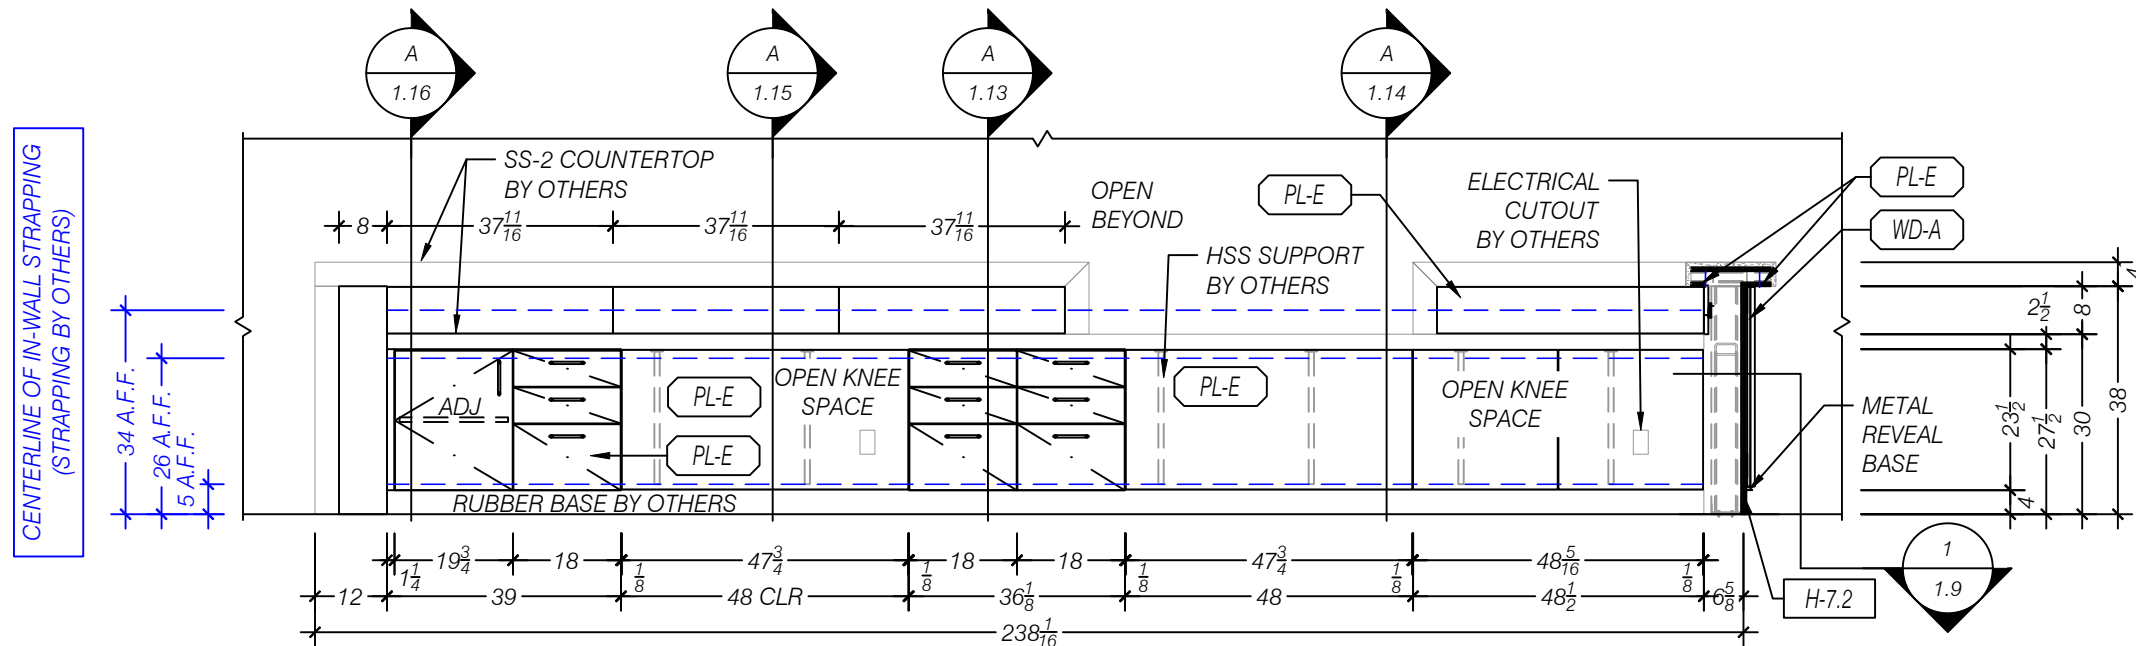

2 ELEVATION EAST - RECEPTION
SCALE 1:32 (3/8"=1'-0")
ARCH REF: 4/AE580

		MATERIALS
(MM-A)	X	WHITE MELAMINE
(PL-C)	X	(PL-1, WB-2) WILSONART "HARVEST MAPLE", 7953-38, FINE VELVET TEXTURE
(PL-E)	X	(PL-3) WILSONART "WHITE", 1570-60, FINE VELVET TEXTURE 1570-38
(WD-A)	X	(WD-1) SURFACING SOLUTIONS, MAPLE TAMBOUR HALF ROUND, PROFILE 383, 3/4"W x 5/16"H
		QTY. HARDWARE
H-1.2	X	SALICE 0mm CLIP-ON HINGE PLATE EURO SCREW, BARGR09/16
H-1.3	X	SALICE 110° FO SOFT-CLOSE, LOGICA SILENTIA, C7J6AE9
H-1.8	X	McKINNEY DOUBLE ACTING SPRING HINGE, 1001,6", SATIN CHROME FINISH
H-2.0	X	KNAPE & VOGT DRAWER SLIDES, KV8400, SIDE MOUNT, FULL EXT. 100lb LOAD RATING
H-2.1	X	KNAPE & VOGT DRAWER SLIDES, KV8600, SIDE MOUNT, FULL EXT. 150lb LOAD RATING
H-3.0	X	BERENSON WIRE PULL, BN6131-2SC-P, 96mm CTC, SATIN CHROME FINISH
H-4.0	X	HAFELE SHELF SUPPORT, 282.04.711, 5mm SHELF PIN, STEEL NICKEL-PLATED
H-6.0	X	MOCKETT TG FLIP-TOP SERIES DESK GROMMET, 2"Ø, COLOR T.B.D.
H-7.1	X	ORANGE ALUMINUM Z-CLIP HD PANEL RAIL
H-7.2	X	FRY REGLET MILLWORK REVEAL, 1" PANEL, 1/2" REVEAL, MWRB50P100, POWDER COATED
H-7.3	X	EAGLE ALUMINUM 1/8" CORNER ACCENT, MILL FINISH
H-7.4	X	McMASTER CARR ALUMINUM CHANNEL, 9001K74, 2"W x 1"H, MILL FINISH
H-8.0	X	KEKU CLIP, BLACK FINISH

DGS SREOC COSTA
MESA
RECEPTION

ISSUE		BY
DATE	DESCRIPTION	Q-AS
05/20/2026	REV-A FOR SUBMITTAL	-
-	-	-
-	-	-
-	-	-
-	-	-

SITE ADDRESS			
STREET	2301 South Shelley Circle BLDG. A & B		
CITY	Costa Mesa		
STATE	CA	ZIP	92626
JOB #:	26034	REV:	A
MOD #:	1	REL:	N/A