

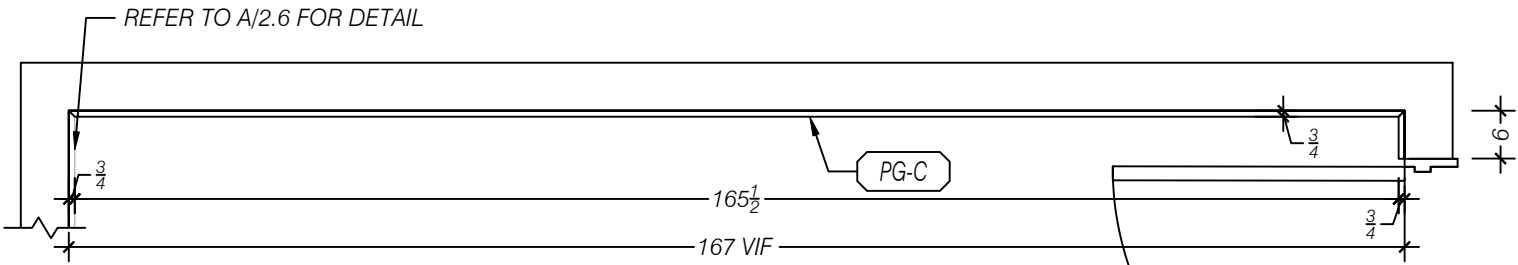



	MATERIALS
	(CR-1) FINGER JOINT PINE, DELIVERED PRIME (PREPPING, PAINTING, FILLING OF ATTACHMENT HOLES BY OTHERS)

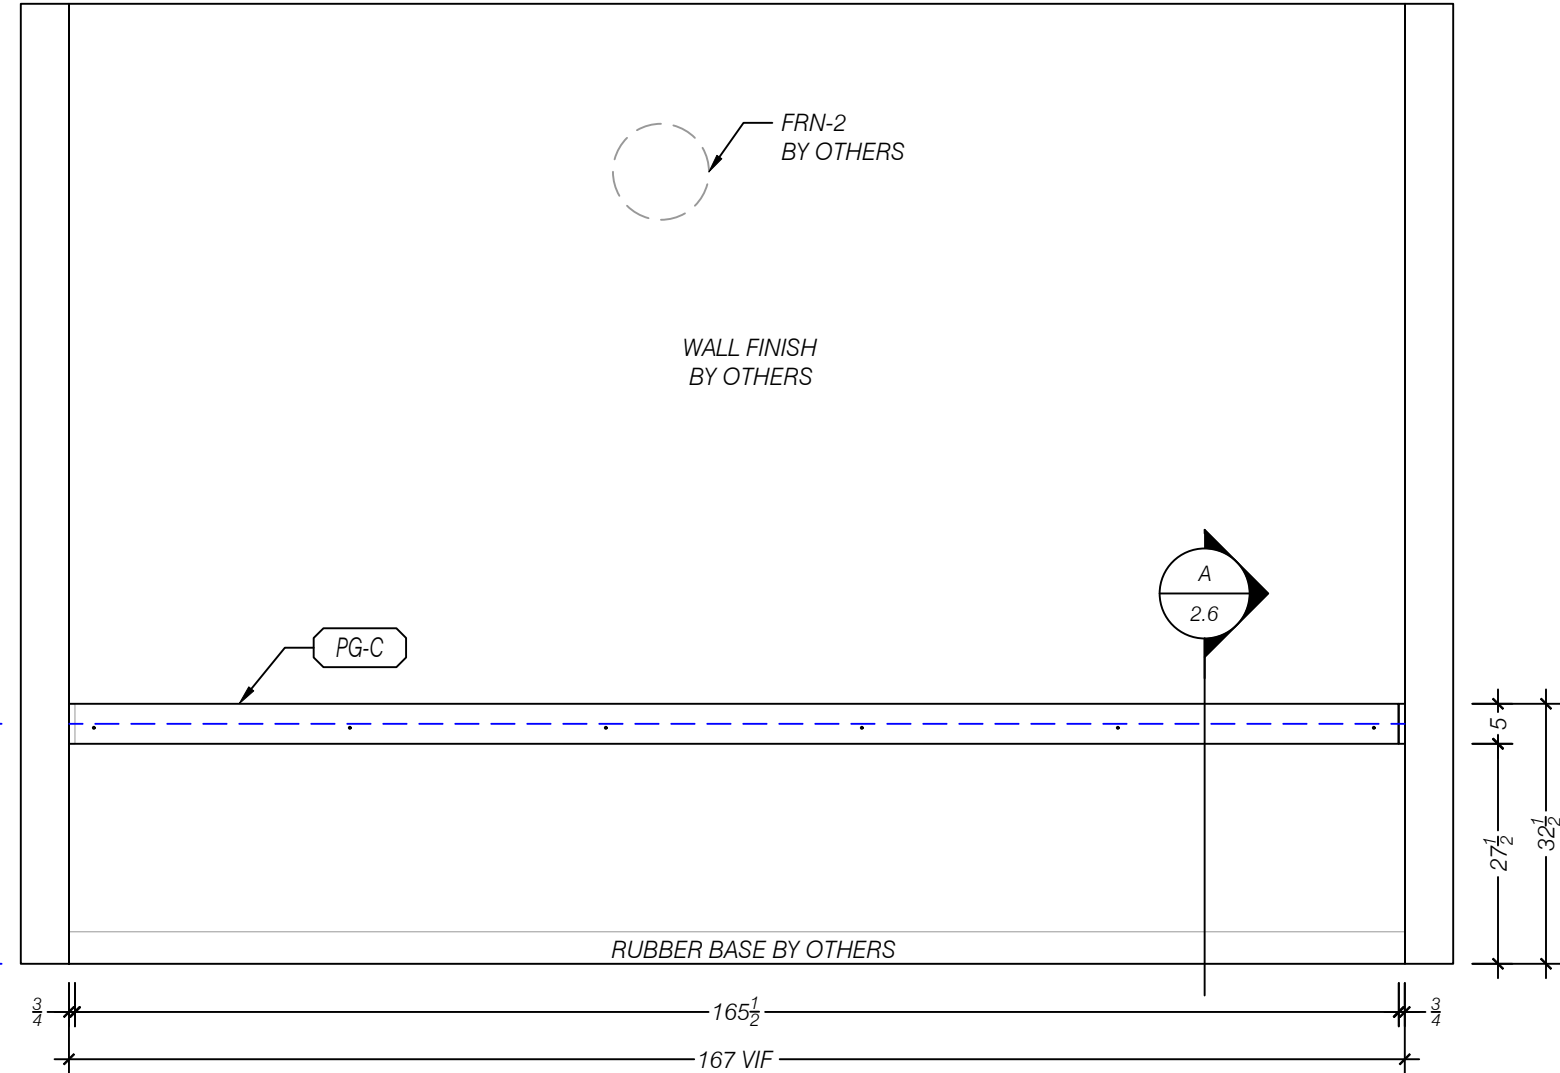

1 PLAN - CONFERENCE 102
SCALE 1:24 (1/2"=1'-0")
ARCH REF: 1/AE406

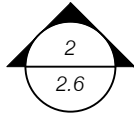

2 ELEVATION SOUTH - CONFERENCE 102
SCALE 1:24 (1/2"=1'-0")
ARCH REF: 8/AE406

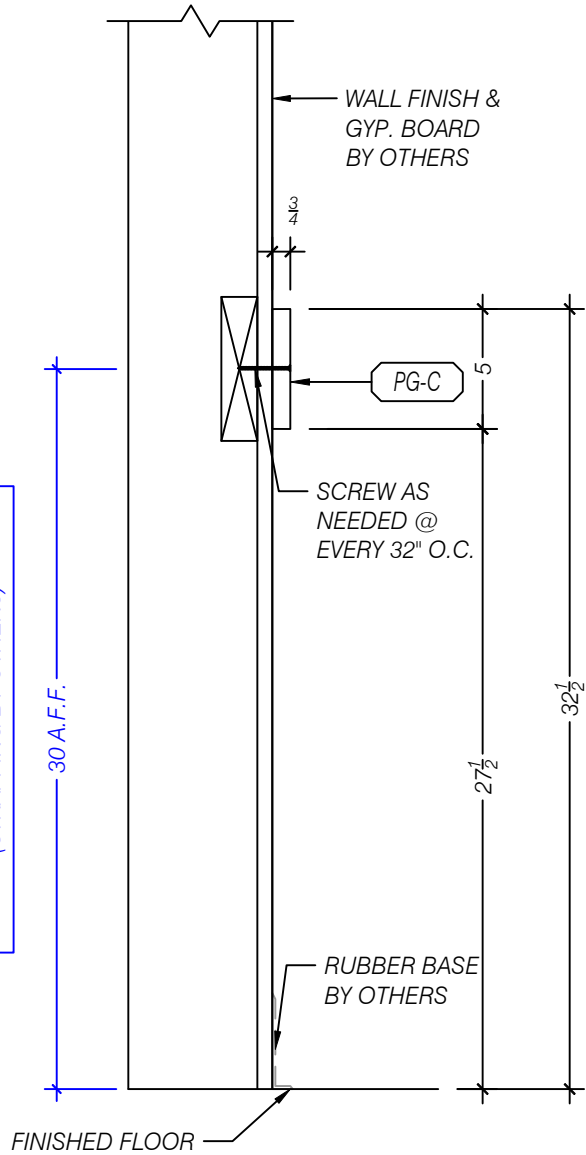

A SECTION - CHAIR RAIL
SCALE 1:8 (1 1/2"=1'-0")
ARCH REF: 3/AE585



5640 WEST END ROAD
ARCATA, CA 95521
PH (707) 822-4034 FAX (707) 822-5478
WWW.CRESTMARKMILLWORK.COM

**DGS SREOC COSTA
MESA
CONFERENCE 102**

ISSUE		BY
DATE	DESCRIPTION	
05/20/2026	REV-A FOR SUBMITTAL	Q-AS
-	-	-
-	-	-
-	-	-
-	-	-
-	-	-
SITE ADDRESS		
STREET	2301 South Shelley Circle Bldg. A & B	
CITY	Costa Mesa	
STATE	CA	ZIP 92626
JOB #:	26034	REV: A
MOD #:	2	REL: N/A

2.6

© CRESTMARK MILLWORK, INC.