


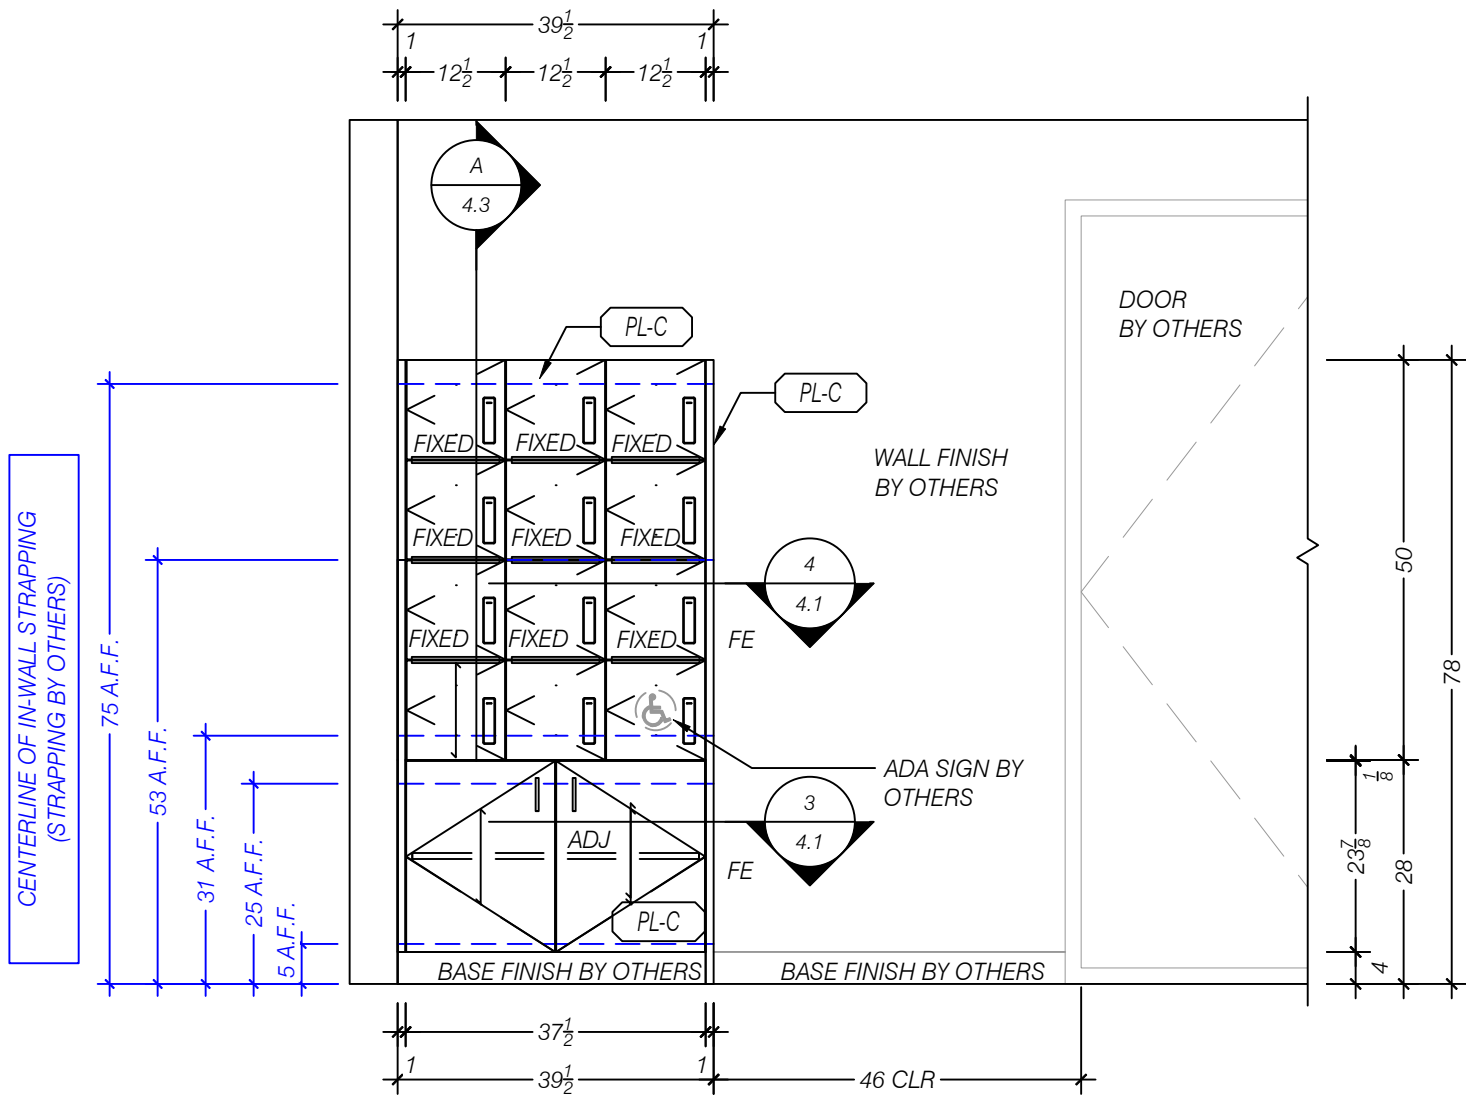

1 ELEVATION NORTH - WELLNESS 112
SCALE 1:24 (1/2" = 1'-0")
ARCH REF: 11/AE406

MATERIALS		
(MM-A)	WHITE MELAMINE	
(PL-C)	(PL-1, WB-2) WILSONART "HARVEST MAPLE", 7953-38, FINE VELVET TEXTURE	
QTY.	HARDWARE	
H-1.2	X	SALICE 0mm CLIP-ON HINGE PLATE EURO SCREW, BARGR09/16
H-1.3	X	SALICE 110° FO SOFT-CLOSE, LOGICA SILENTIA, C7J6AE9
H-3.0	X	BERENSON WIRE PULL, BN6131-2SC-P, 96mm CTC, SATIN CHROME FINISH
H-4.0	X	HAFELE SHELF SUPPORT, 282.04.711, 5mm SHELF PIN, STEEL NICKEL-PLATED
H-5.5	X	KITLOCK ELECTRONIC LOCKER LOCK, KL1100 RFID, BLACK FINISH



DGS SREOC COSTA
MESA
WELLNESS 112

ISSUE		BY
DATE	DESCRIPTION	
05/20/2026	REV-A FOR SUBMITTAL	Q-AS
-	-	-
-	-	-
-	-	-
-	-	-

SITE ADDRESS			
STREET	2301 South Shelley Circle Bldg. A & B		
CITY	Costa Mesa		
STATE	CA	ZIP	92626
JOB #:	26034	REV:	A
MOD #:	4	REL:	N/A