


PLUMBING SCHEDULE (BY OTHERS)				
ARCH. TAG	MAKE	MODEL	FINISH	COMMENTS
HS-1	ELKAY	D11515	POLISHED CHROME	SINK
HS-1	CHICAGO	#2302-GN8AE3ABCP	POLISHED CHROME	FAUCET
TA-5	SLOAN	BE - 200	POLISHED CHROME	SOAP DISPENSER

MATERIALS	
(MM-A)	WHITE MELAMINE
(PL-C)	(PL-1, WB-2) WILSONART "HARVEST MAPLE", 7953-38, FINE VELVET TEXTURE
QTY.	HARDWARE
H-1.2	X SALICE 0mm CLIP-ON HINGE PLATE EURO SCREW, BARGR09/16
H-1.3	X SALICE 110° FO SOFT-CLOSE, LOGICA SILENTIA, C7J6AE9
H-4.1.1	X BRACKET, A&M CFLAT 21 (2.0)
H-9.1	X GRAINGER - GRAB CATCH - 4PE50, STEEL

EQUIPMENT SCHEDULE BY OTHERS				
ARCH. TAG	MAKE	MODEL	FINISH	COMMENTS
REF-2	SUMMIT APPLIANCE	FF6BK2SS	STAINLESS	REFRIGERATOR

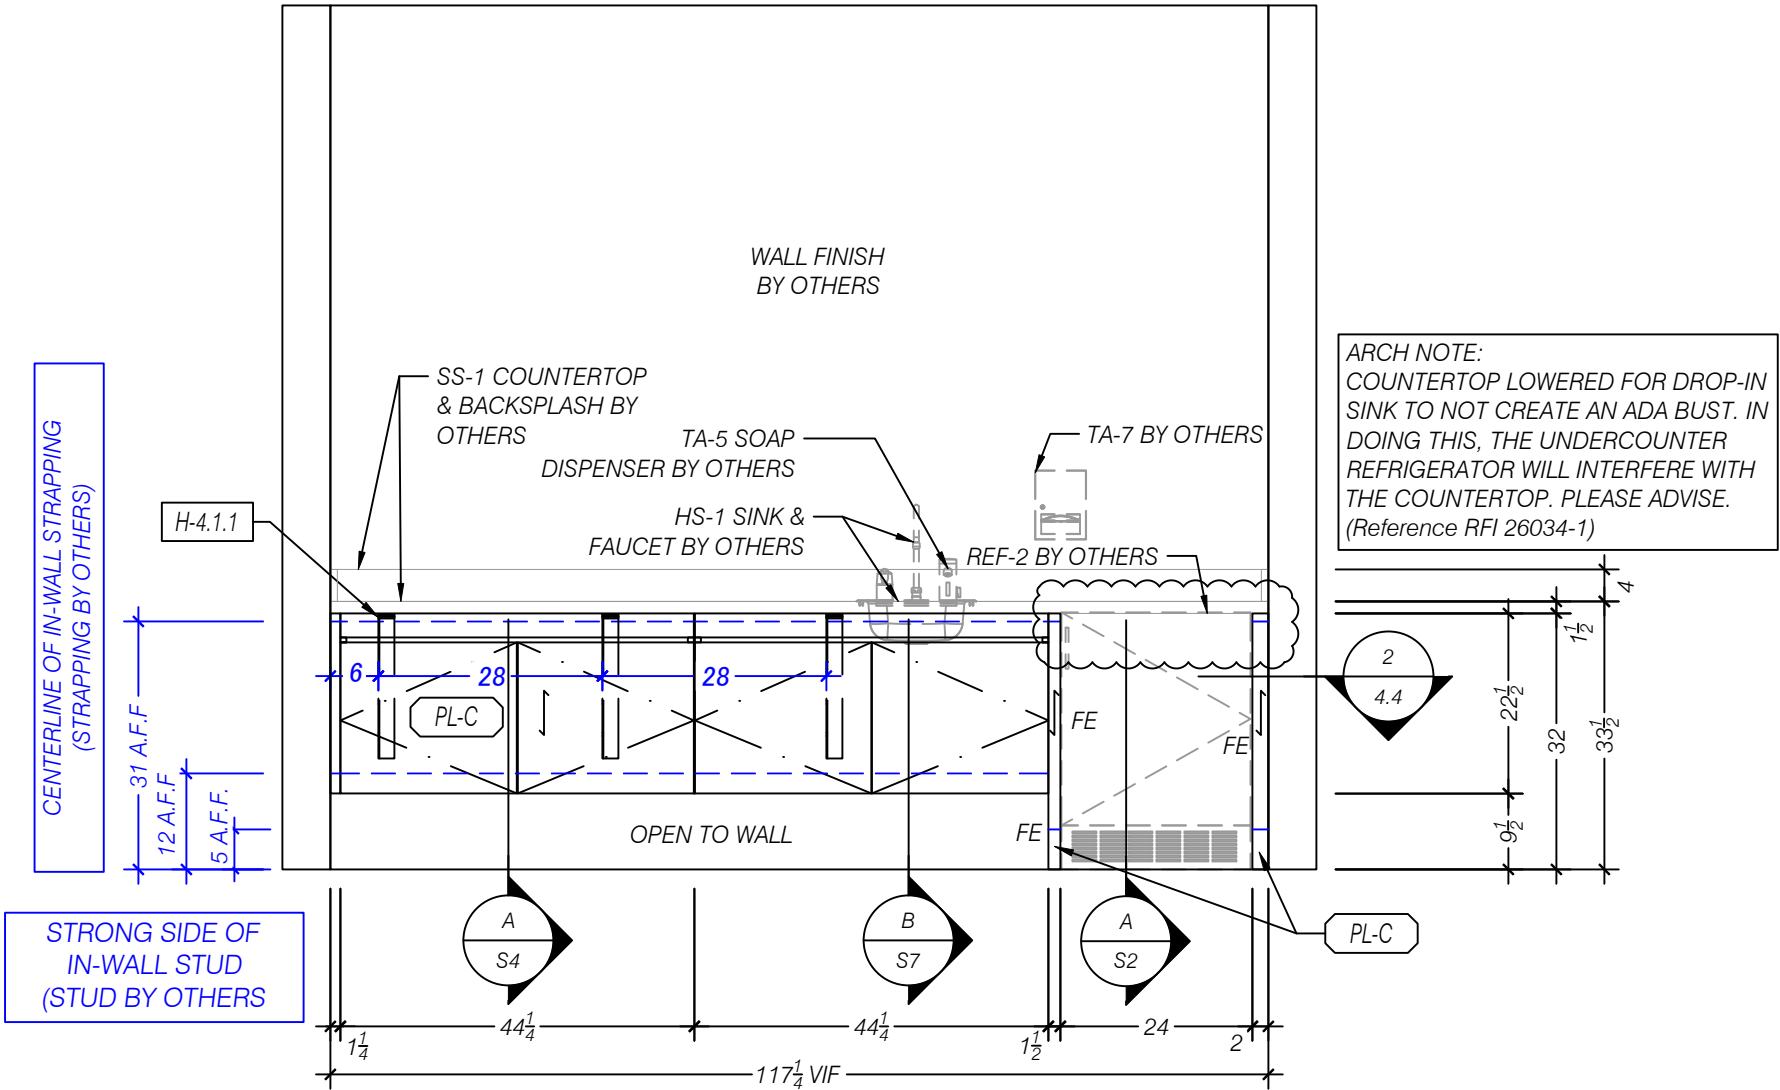

1 ELEVATION SOUTH - WELLNESS 112
SCALE 1:24 (1/2"=1'-0")
ARCH REF: 13/AE406

DGS SREOC COSTA
MESA
WELLNESS 112

ISSUE				
DATE	DESCRIPTION	BY		
05/20/2026	REV-A FOR SUBMITTAL	Q-AS	-	-
-	-	-	-	-
-	-	-	-	-
-	-	-	-	-
-	-	-	-	-
SITE ADDRESS				
STREET		2301 South Shelley Circle Bldg. A & B		
CITY		Costa Mesa		
STATE	CA	ZIP	92626	
JOB #:		26034	REV: A	
MOD #:		4	REL: N/A	