



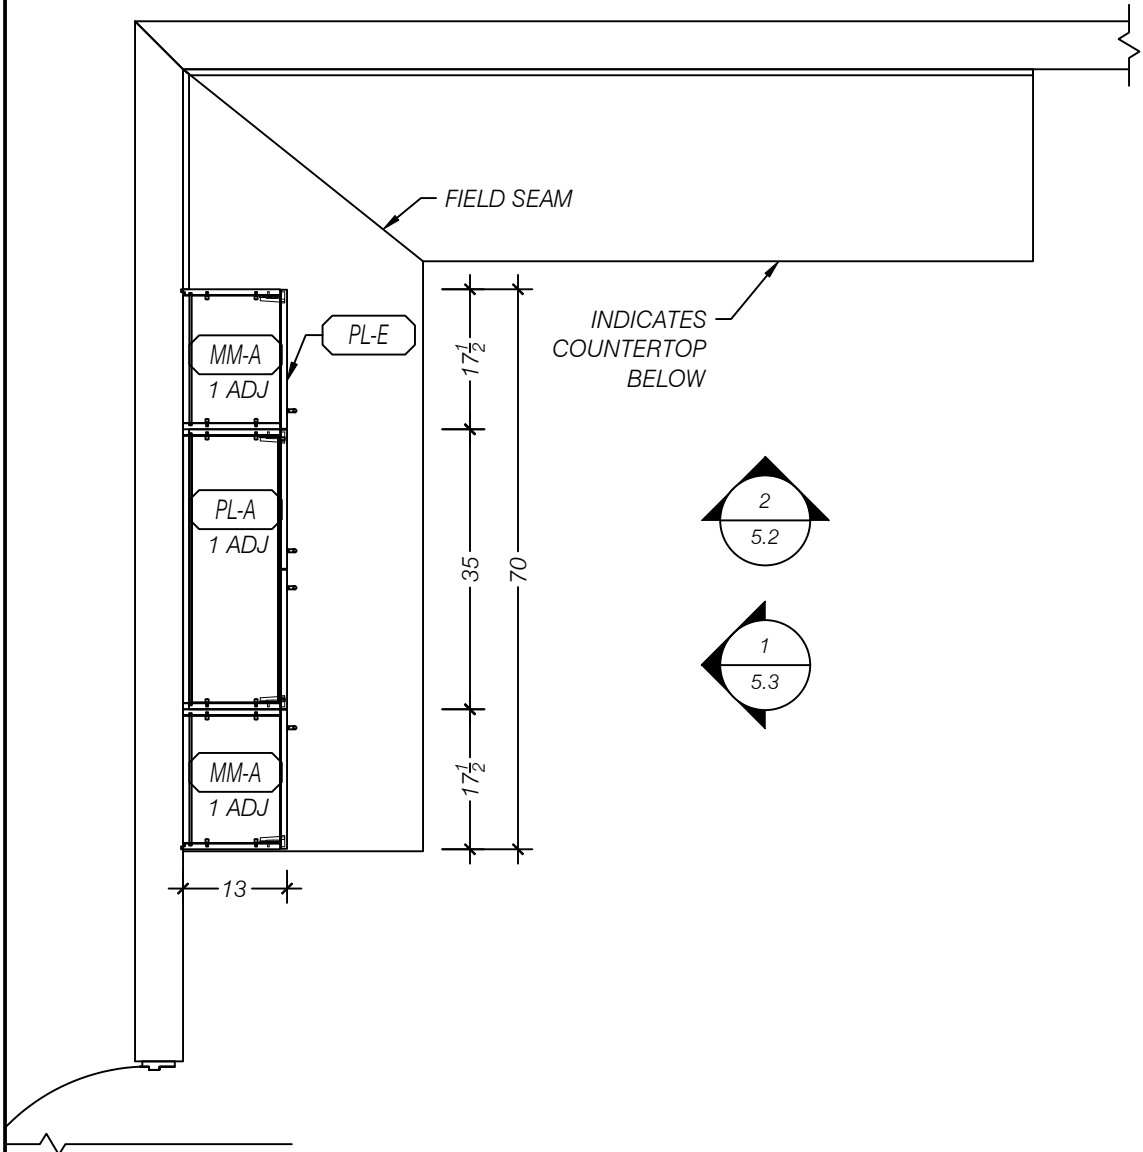

1 PLAN SECTION WALL - MEDIA CONTROL 113
SCALE 1:24 (1/2"=1'-0")
ARCH REF: NA

		MATERIALS
		(MM-A) WHITE MELAMINE
		(PL-A) WHITE CAB LINER
		(PL-D) (PL-2) PIONITE "FOLKSTONE GRAY", SG241-SD, TEXTURED/SUEDE FINISH
		(PL-E) (PL-3) WILSONART "WHITE", 1570-60, FINE VELVET TEXTURE 1570-38
		(PL-F) (PL-4) WILSONART "CARBON MESH", 4880-38, FINE VELVET TEXTURE
	QTY.	HARDWARE
	X	(H-1.2) SALICE 0mm CLIP-ON HINGE PLATE EURO SCREW, BARGR09/16
	X	(H-1.3) SALICE 110° FO SOFT-CLOSE, LOGICA SILENTIA, C7J6AE9
	X	(H-2.0) KNAPE & VOGT DRAWER SLIDES, KV8400, SIDE MOUNT, FULL EXT. 100lb LOAD RATING
	X	(H-2.1) KNAPE & VOGT DRAWER SLIDES, KV8600, SIDE MOUNT, FULL EXT. 150lb LOAD RATING
	X	(H-3.0) BERENSON WIRE PULL, BN6131-2SC-P, 96mm CTC, SATIN CHROME FINISH
	X	(H-4.0) HAFELE SHELF SUPPORT, 282.04.711, 5mm SHELF PIN, STEEL NICKEL-PLATED
	X	(H-4.1.1) BRACKET, A&M CFLAT 21 (2.0)
	X	(H-4.1.2) BRACKET, A&M CFLAT 24 (2.0)
	X	(H-7.0) 1/8" x 1-1/4" x 1-1/4" ALUMINUM L-ANGLE, MILL FINISH

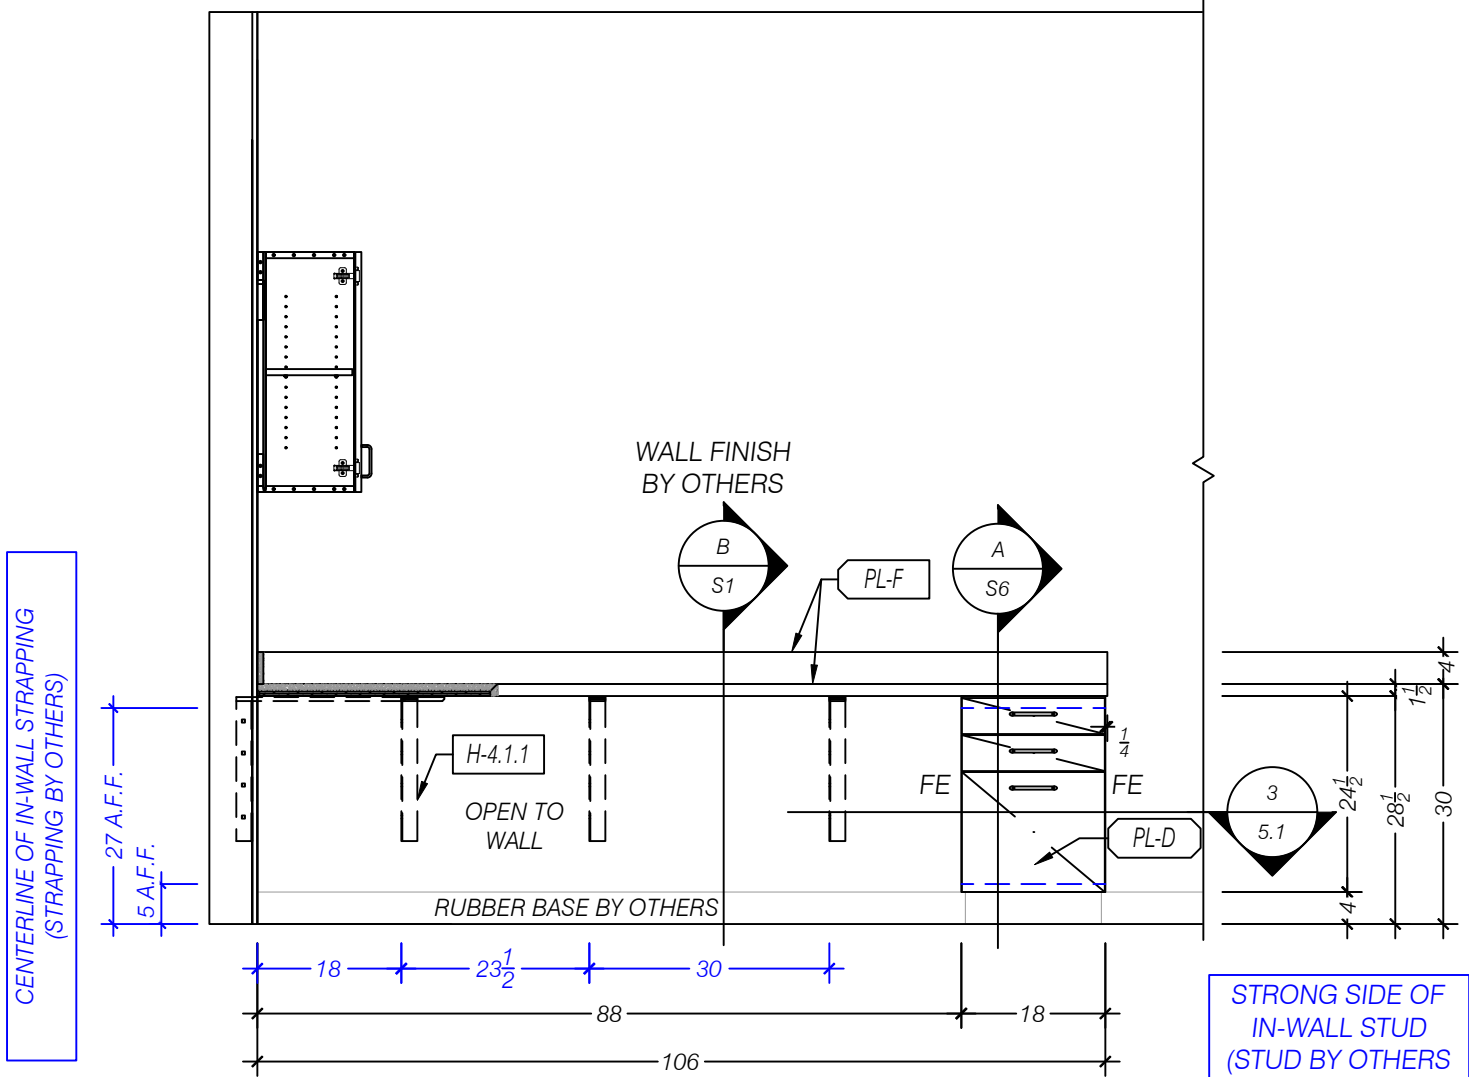

2 ELEVATION SOUTH - MEDIA CONTROL 113
SCALE 1:24 (1/2"=1'-0")
ARCH REF: 8/AE408

5640 WEST END ROAD
ARCATA, CA 95521
PH (707) 822-4034 FAX (707) 822-5478
WWW.CRESTMILLWORK.COM

DGS SREOC COSTA
MESA
MEDIA CONTROL 113

ISSUE	DATE	DESCRIPTION	BY
	05/20/2026	REV-A FOR SUBMITTAL	Q-AS
			-
			-
			-
			-
			-

SITE ADDRESS			
STREET	CITY	STATE	ZIP
2301 South Shelley Circle Bldg. A & B	Costa Mesa	CA	92626

JOB #:	26034	REV:	A
MOD #:	5	REL:	N/A

5.2