

# DGS SREOC Costa Mesa

2301 South Shelley Circle Bldg A & B, Costa Mesa, CA 92626

## Architectural Millwork & Casework Submittal

### Project Info

Job Number:


26034

Submittal Date:

05/05/2026

Submittal Revision:

A

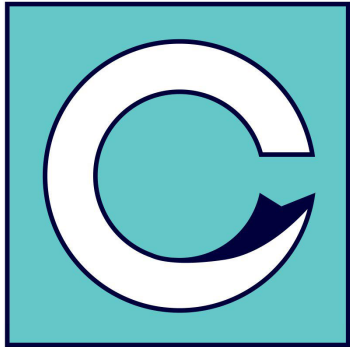

CRESTMARK  
MILLWORK

### Project Team

| Millwork                          |               |                              |
|-----------------------------------|---------------|------------------------------|
| Company: Crestmark Millwork, Inc. |               |                              |
| Address: 5640 West End Road       |               |                              |
| City: Arcata                      | State: CA     | Zip: 95521                   |
| License: 909262                   |               |                              |
| Phone: (707) 822-4034             |               | Fax: (707) 822-5478          |
| Contact List:                     | Name:         | E-Mail:                      |
| Estimator                         | Lee Phillips  | leep@crestmarkmillwork.com   |
| Project Manager                   | Evan Newbanks | evann@crestmarkmillwork.com  |
| Field PM                          | Nick DeLeon   | nickdl@crestmarkmillwork.com |

| Architect                             |           |            |
|---------------------------------------|-----------|------------|
| Company: DGA Architects               |           |            |
| Address: 2550 Fifth Avenue, Suite 115 |           |            |
| City: San Diego                       | State: CA | Zip: 92103 |
| License:                              |           |            |
| Phone: (619) 685-3990                 |           | Fax:       |
| Contact List:                         | Name:     | E-Mail:    |
| ---                                   | ---       | ---        |
| ---                                   | ---       | ---        |
| ---                                   | ---       | ---        |

| Interior Designer |        |         |
|-------------------|--------|---------|
| Company:          |        |         |
| Address:          |        |         |
| City:             | State: | Zip:    |
| License:          |        |         |
| Phone:            |        | Fax:    |
| Contact List:     | Name:  | E-Mail: |
| ---               | ---    | ---     |
| ---               | ---    | ---     |
| ---               | ---    | ---     |

| Installer     |        |         |
|---------------|--------|---------|
| Company:      |        |         |
| Address:      |        |         |
| City:         | State: | Zip:    |
| License:      |        |         |
| Phone:        |        | Fax:    |
| Contact List: | Name:  | E-Mail: |
| ---           | ---    | ---     |
| ---           | ---    | ---     |
| ---           | ---    | ---     |

| General Contractor           |                |                   |
|------------------------------|----------------|-------------------|
| Company: Turner Construction |                |                   |
| Address: 1720 8th Street     |                |                   |
| City: Sacramento             | State: CA      | Zip: 95811        |
| License:                     |                |                   |
| Phone:                       |                | Fax:              |
| Contact List:                | Name:          | E-Mail:           |
| Senior PM                    | Shawna Brierly | sbrierly@tcco.com |
| Project Executive            | Joseph Pobanz  | jpobanz@tcco.com  |
| Superintendent               |                |                   |

| General Notes |   |
|---------------|---|
| 1             | All dimensions to be field verified.   |
| 2             | General Contractor (GC) to coordinate all framing requirements with Crestmark Millwork, Inc. (CMI).                                                                                                 |
| 3             | GC to coordinate all wall types, thickness and rough openings.   |
| 4             | GC and electrical contractor to coordinate all electrical box locations and requirements with millwork drawings.                                                                                    |
| 5             | GC and electrical contractor to coordinate all light fixture feed and switching locations with millwork drawings.                                                                                   |
| 6             | GC and plumbing contractor to coordinate all plumbing fixtures, locations, and installation requirements.                                                                                           |
| 7             | All in-wall/ceiling blocking and supports for cabinetry, millwork and countertop anchorage by others. CMI is not responsible for missing or incorrect blocking heights taken from unapproved plans. |
| 8             | In-field priming and painting by others UON, including filling and sanding of fastener holes in running trims.                                                                                      |
| 9             | Casework shelf spans to comply with AWS manual unless otherwise specified and approved by the architect.                                                                                            |
| 10            | All cabinet construction shall be based on the latest edition of NAAWS Manual where applicable.   |
| 11            | All rubber, vinyl, tile, stone or specialty baseboard to be supplied by others UON.   |
| 12            | Lock locations and quantities supplied only where indicated in approved plans.   |
| 13            | Shelf locations and quantities supplied only where indicated in approved plans.   |

### Installation Requirements

|   |   |
|---|---|
|   | Per Architectural Woodwork Standards (AWS), it is the responsibility of the general contractor (GC) to insure the following required site conditions:   |
| 1 | Walls, ceilings, floors and openings must be level, plumb, straight, in-line, and square. In the absence of floor tolerances in the contract documents, variance of a cabinet's toe base height is not a defect. Casework is required to be installed level. Shimming of toe base not to exceed 12.5mm (½") is acceptable. Floor variations exceeding this amount shall be corrected before cabinets are installed. Wall panel installations are subject to the same tolerances at wall or ceiling. Correction is not the responsibility of the manufacturer or installer. |
| 2 | Prior to delivery and installation of architectural woodwork, casework and related millwork to the jobsite, the building environment shall be stabilized to provide conditions that will maintain a relative humidity between 25% and 55%.   |
| 3 | Areas to receive architectural woodwork must be fully enclosed with windows installed and glazed, exterior doors in place, HVAC systems operational, and temporary openings closed. All plaster, wet grinding, and concrete work shall be fully dry.   |
| 4 | A secure storage area must be provided within the building that is flat and level, clean, dry, well ventilated, protected from direct sunlight, and broom clean.   |
| 5 | Unless specified as part of the installer's contract, it is the responsibility of the GC to furnish and install structural, blocking, or anchorage which become part of the walls, floors, or ceilings, as required for architectural woodwork installation.   |
| 6 | All metal backing strips welded to steel studs shall be as specified and/or detailed on architectural/design drawings to show locations and gauge of thickness of these items.   |
| 7 | Should the architect, designer, or engineer omit details calling for the general contractor to supply necessary blocking or backing strips in the wall, either through inadvertence or otherwise, the architectural woodwork installer shall not proceed with installation until such time as the blocking is installed by others. The owner or owner's GC is responsible for placing blocking acceptable to the woodwork installer prior to installation with no penalty to the woodwork manufacturer or installer.                                                       |
| 8 | All preparatory work done by others shall be subject to inspection by the architectural woodwork installer and may be accepted or rejected prior to commencing installation.   |
| 9 | Rough opening which are installed by others prior to commencement of installation shall be built square, in plane, and to the proper dimensions.   |

### Woodwork Institute Certification

| Scope               | Grade | Label Req |
|---------------------|-------|-----------|
| Shop Drawings       |       |           |
| Countertops         |       |           |
| Cabinets            |       |           |
| Doors               |       |           |
| Installation        |       |           |
| Reviewed By:        |       |           |
| WI Project Number:  |       |           |
| Certification Date: |       |           |
| Certification Label |       |           |

### Regulatory Information

|                                                              |
|--------------------------------------------------------------|
| ADA Cabinetry Shall Comply With 2010 ADA Standards           |
| -Section 304: Turning Space                                  |
| -Section 305: Clear Floor Or Ground Space                    |
| -Section 306: Toe And Knee Clearance                         |
| -Section 308: Reach Ranges                                   |
| -Section 804: Kitchens And Kitchenettes                      |
| -Section 902: Dining Surfaces And Work Surfaces              |
| -Section 904: Check Out Aisles And Service Counters          |
| ADA Cabinetry Shall Comply With Chapter 11B 2022 CBC         |
| -Section 11B-212: Kitchens, Kitchenettes, Wet Bars And Sinks |
| -Section 11B-306: Toe And Knee Clearance                     |
| -Section 11B-902: Dining Surfaces And Work Surfaces          |
| -Section 11B-904: Check-Out Aisles & Sales/Service Counters  |

| Module # | Sheet #    | Description                | Module # | Sheet # | Description                             | Module # | Sheet # | Description      |
|----------|------------|----------------------------|----------|---------|-----------------------------------------|----------|---------|------------------|
|          | ARF        | ARCHITECT RESPONSE FORM    | 4        | 4.3     | WELLNESS 112                            |          | S9      | SECTION DETAILS  |
|          | SPECS PAGE | SPECIFICATIONS             | 4        | 4.4     | WELLNESS 112                            |          | S10     | SECTION DETAILS  |
|          | SCHEDULES  | SCHEDULES                  | 4        | 4.5     | WELLNESS 112                            |          | S11     | SECTION DETAILS  |
|          | FP.1       | OVERALL FLOOR PLAN LEVEL 1 | 4        | 4.6     | WELLNESS 112                            |          | D1      | ENLARGED DETAILS |
| 1        | 1.1        | LOBBY 100                  | 5        | 5.1     | MEDIA CONTROL 113                       |          | D2      | ENLARGED DETAILS |
| 1        | 1.2        | LOBBY 100                  | 5        | 5.2     | MEDIA CONTROL 113                       |          | D3      | ENLARGED DETAILS |
| 1        | 1.3        | LOBBY 100                  | 5        | 5.3     | MEDIA CONTROL 113                       |          | D4      | ENLARGED DETAILS |
| 1        | 1.4        | LOBBY 100                  | 6        | 6.1     | BREAK ROOM 115                          |          | D5      | ENLARGED DETAILS |
| 1        | 1.5        | LOBBY 100                  | 6        | 6.2     | BREAK ROOM 115                          |          |         |                  |
| 1        | 1.6        | LOBBY 100                  | 6        | 6.3     | BREAK ROOM 115                          |          |         |                  |
| 1        | 1.7        | LOBBY 100                  | 6        | 6.4     | BREAK ROOM 115                          |          |         |                  |
| 1        | 1.8        | RECEPTION                  | 6        | 6.5     | BREAK ROOM 115                          |          |         |                  |
| 1        | 1.9        | RECEPTION                  | 6        | 6.6     | BREAK ROOM 115                          |          |         |                  |
| 1        | 1.10       | RECEPTION                  | 6        | 6.7     | BREAK ROOM 115                          |          |         |                  |
| 1        | 1.11       | RECEPTION                  | 6        | 6.8     | BREAK ROOM 115                          |          |         |                  |
| 1        | 1.12       | RECEPTION                  | 6        | 6.9     | BREAK ROOM 115                          |          |         |                  |
| 1        | 1.13       | RECEPTION                  | 6        | 6.10    | BREAK ROOM 115                          |          |         |                  |
| 1        | 1.14       | RECEPTION                  | 6        | 6.11    | BREAK ROOM 115                          |          |         |                  |
| 1        | 1.15       | RECEPTION                  | 7        | 7.1     | EMERGENCY OPERATIONS CENTER 120         |          |         |                  |
| 1        | 1.16       | RECEPTION                  | 7        | 7.2     | EMERGENCY OPERATIONS CENTER 120         |          |         |                  |
| 1        | 1.17       | RECEPTION                  | 7        | 7.3     | EMERGENCY OPERATIONS CENTER 120         |          |         |                  |
| 1        | 1.18       | RECEPTION                  | 7        | 7.4     | EMERGENCY OPERATIONS CENTER 120         |          |         |                  |
| 1        | 1.19       | RECEPTION                  | 7        | 7.5     | EMERGENCY OPERATIONS CENTER 120         |          |         |                  |
| 1        | 1.20       | RECEPTION                  | 7        | 7.6     | EMERGENCY OPERATIONS CENTER 120         |          |         |                  |
| 1        | 1.21       | RECEPTION                  | 8        | 8.1     | BREAKOUT 121,122,123 & 124              |          |         |                  |
| 1        | 1.22       | RECEPTION                  | 8        | 8.2     | BREAKOUT 121,122,123 & 124              |          |         |                  |
| 1        | 1.23       | RECEPTION                  | 9        | 9.1     | AV COORDINATION ROOM 126                |          |         |                  |
| 2        | 2.1        | CONFERENCE 102             | 9        | 9.2     | AV COORDINATION ROOM 126                |          |         |                  |
| 2        | 2.2        | CONFERENCE 103             | 10       | 10.1.   | TRANING / MULTI-PURPOSE ROOMS 132 & 134 |          |         |                  |
| 2        | 2.3        | CONFERENCE 102             | 10       | 10.2    | TRANING / MULTI-PURPOSE ROOMS 132 & 134 |          |         |                  |
| 2        | 2.4        | CONFERENCE 102             | 10       | 10.3    | TRANING / MULTI-PURPOSE ROOMS 132 & 134 |          |         |                  |
| 2        | 2.5        | CONFERENCE 102             |          |         |                                         |          |         |                  |
| 2        | 2.6        | CONFERENCE 102             |          | S1      | SECTION DETAILS                         |          |         |                  |
| 2        | 2.7        | CONFERENCE 102             |          | S2      | SECTION DETAILS                         |          |         |                  |
| 2        | 2.8        | CONFERENCE 102             |          | S3      | SECTION DETAILS                         |          |         |                  |
| 2        | 2.9        | CONFERENCE 102             |          | S4      | SECTION DETAILS                         |          |         |                  |
| 2        | 2.10       | CONFERENCE 102             |          | S5      | SECTION DETAILS                         |          |         |                  |
| 3        | 3.1        | ALL GENDER 103             |          | S6      | SECTION DETAILS                         |          |         |                  |
| 4        | 4.1        | WELLNESS 112               |          | S7      | SECTION DETAILS                         |          |         |                  |
| 4        | 4.2        | WELLNESS 112               |          | S8      | SECTION DETAILS                         |          |         |                  |



5640 WEST END ROAD  
ARCATA, CA 95521  
PH (707) 822-4034 FAX (707) 822-5478  
WWW.CRESTMARKMILLWORK.COM

DGS SREOC COSTA

MESA

INDEX

| ISSUE        |                                       | BY                  |       |     |  |  |  |
|--------------|---------------------------------------|---------------------|-------|-----|--|--|--|
|              |                                       | DESCRIPTION         | Q-AS  |     |  |  |  |
| DATE         | 05/05/2026                            | REV-A FOR SUBMITTAL |       |     |  |  |  |
|              |                                       |                     |       |     |  |  |  |
|              |                                       |                     |       |     |  |  |  |
| SITE ADDRESS |                                       |                     |       |     |  |  |  |
| STREET       | 2301 South Shelley Circle BLDG. A & B |                     |       |     |  |  |  |
| CITY         | Costa Mesa                            |                     |       |     |  |  |  |
| STATE        | CA                                    | ZIP                 | 92626 |     |  |  |  |
| JOB #:       | 26034                                 |                     | REV:  | A   |  |  |  |
| MOD #:       | -                                     |                     | REL:  | N/A |  |  |  |
| INDEX        |                                       |                     |       |     |  |  |  |

| BASIS OF DESIGN                |            |
|--------------------------------|------------|
| PLAN LOG                       |            |
| DOCUMENT NAME                  | DATE       |
| Architectural - 2026-01-16 IFC | 01/16/2026 |
|                                |            |
|                                |            |

NAAWS COMPLIANCE REQUIREMENTS

|                |   |
|----------------|---|
| GRADE          | N.A.A.W.S. 4.0, CUSTOM GRADE PER FUNDAMENTAL GENERAL REQUIREMENTS SECTION 2.4.11, PG. 57 & SECTION 10, PGS. 147-184 |
| CONSTRUCTION   | N.A.A.W.S. 4.0, FRAMELESS, PER RESOURCE GUIDE - PG. 455 FG. RG-229                                                  |
| DOORS/DRAWERS  | N.A.A.W.S. 4.0, FLUSH OVERLAY PER SECTION 10.6 SUBSET 8.1 - PG. 164                                                 |
| GRAIN/PATTERNS | N.A.A.W.S. 4.0, CUSTOM GRADE PER RESOURCE GUIDE - PG. 457 FG. RG-240                                                |
| JOINERY        | N.A.A.W.S. 4.0, DOWEL JOINERY PER SECTION 10.6 SUBSET 22 - PG. 178                                                  |
| SCRIBES        | N.A.A.W.S. 4.0, CABINETRY ADJACENT TO WALLS WILL BE SCRIBED (1-1/2" MAX.) PER SECTION 10.6 SUBSET 23 - PG. 181      |
| WALL ANCHORAGE | N.A.A.W.S. 4.0, CASEWORK WALL ANCHORAGE PER SECTION 14.10 SUBSET 5 - PGS. 220-222                                   |

MATERIAL SPECIFICATIONS

CASE BODY

|                  |   |
|------------------|---|
| CORE MATERIAL    | 3/4" INDUSTRIAL GRADE PARTICLEBOARD, NAUF, FSC, CARB 2 COMPLIANT                                        |
| EXPOSED EXTERIOR | HIGH PRESSURE PLASTIC LAMINATE (SEE COLOR SCHEDULE)                                                     |
| EXPOSED INTERIOR | HIGH PRESSURE PLASTIC LAMINATE (SEE COLOR SCHEDULE)                                                     |
| SEMI-EXPOSED     | 3/4" MM-A (SEE COLOR SCHEDULE)                                                                          |
| CABINET BACKS    | 1/4" MM-A (SEE COLOR SCHEDULE)                                                                          |
| EDGEBANDING      | HIGH PRESSURE PLASTIC LAMINATE TO MATCH CASEWORK EXTERIOR (U.N.O.)                                      |
| TOE KICKS        | PRESSURE TREATED LUMBER W/ RESILIENT BASE OVER 3/4" EXTERIOR GRADE PLYWOOD, RESILIENT BASE BY OTHERS    |
| SHELVING         | ADJUSTABLE = 3/4" MM-A & G2S HPDL @ SPANS > 30", FIXED = 3/4" MM-A, IN ACCORDANCE WITH 40LBS/SF LOADING |

WALL PANELS & PARTITIONS

|               |                                                                    |
|---------------|--------------------------------------------------------------------|
| CORE MATERIAL | 3/4" INDUSTRIAL GRADE PARTICLEBOARD, NAUF, FSC, CARB 2 COMPLIANT   |
| EXTERIOR FACE | HIGH PRESSURE PLASTIC LAMINATE (SEE COLOR SCHEDULE)                |
| INTERIOR FACE | BALANCED BACKER                                                    |
| EDGEBANDING   | HIGH PRESSURE PLASTIC LAMINATE TO MATCH CASEWORK EXTERIOR (U.N.O.) |

DOOR & DRAWER FRONTS

|               |                                                                    |
|---------------|--------------------------------------------------------------------|
| CORE MATERIAL | 3/4" INDUSTRIAL GRADE PARTICLEBOARD, NAUF, FSC, CARB 2 COMPLIANT   |
| EXTERIOR FACE | HIGH PRESSURE PLASTIC LAMINATE (SEE COLOR SCHEDULE)                |
| INTERIOR FACE | HIGH PRESSURE PLASTIC LAMINATE (SEE COLOR SCHEDULE PL-A)           |
| EDGEBANDING   | HIGH PRESSURE PLASTIC LAMINATE TO MATCH CASEWORK EXTERIOR (U.N.O.) |

| MATERIAL SPECIFICATIONS CONT.   |                                                                              |
|---------------------------------|------------------------------------------------------------------------------|
| DRAWER BOXES                    |                                                                              |
| BOX MATERIAL                    | 5/8" MM-A FRONT/BACK/SIDES, 1/4" BOTTOM (1/2" @ SPANS > 30")                 |
| JOINERY TYPE                    | DOWEL JOINT W/ 8MM X 30MM WD DOWELS, BOTTOMS DADOED INTO ALL 4 SIDES         |
| EDGEBANDING                     | 1MM PVC OF MFG RECOMMENDED COMPATIBLE COLOR OR PATTERN (U.N.O.)              |
| WALL SHELVES                    |                                                                              |
| CORE MATERIAL                   |                                                                              |
| EXPOSED SURFACES                |                                                                              |
| EDGEBANDING                     |                                                                              |
| COUNTERTOPS                     |                                                                              |
| GRADE                           | N.A.A.W.S CUSTOM GRADE, SECTION 11.3 SUBSET 1.4, PAGE 187                    |
| CORE MATERIAL                   | 3/4" INDUSTRIAL GRADE PARTICLEBOARD, NAUF, FSC, CARB 2 COMPLIANT             |
| LAMINATE TOPS                   | HIGH PRESSURE PLASTIC LAMINATE (SEE COLOR SCHEDULE)                          |
| FRONT EDGE                      | EASED EDGE                                                                   |
| SS/MTL TOPS                     | BY OTHERS                                                                    |
| SUB TOPS                        | PLYWOOD, NAUF, CARB 2 COMPLIANT                                              |
| DIE WALL & TRANSACTION COUNTERS |                                                                              |
| STRUCTURE                       |                                                                              |
| PANEL CORES                     | 3/4" INDUSTRIAL GRADE PARTICLEBOARD, NAUF, FSC, CARB 2 COMPLIANT             |
| PANEL FACE                      | HIGH PRESSURE PLASTIC LAMINATE (SEE COLOR SCHEDULE) & WD-A OVER 1/2" PLYWOOD |
| PANEL BACK                      | BALANCED BACKER                                                              |
| EDGEBANDING                     | HIGH PRESSURE PLASTIC LAMINATE TO MATCH CASEWORK EXTERIOR (U.N.O.)           |
| BASE                            | FRY REGLET MILLWORK REVEAL (SEE HARDWARE SCHEDULE H-7.2)                     |
| DESK SURFACE                    | BY OTHERS                                                                    |
| TRANSACTION TOP                 | BY OTHERS                                                                    |



5640 WEST END ROAD  
ARCATA, CA 95521  
PH (707) 822-4034 FAX (707) 822-5478  
WWW.CRESTMILLWORK.COM

DGS SREOC COSTA  
MESA  
SPECIFICATIONS

|              |                                       |                     |       |      |   |  |  |  |
|--------------|---------------------------------------|---------------------|-------|------|---|--|--|--|
| ISSUE        | DATE                                  | 05/05/2026          | BY    | Q-AS |   |  |  |  |
|              | DESCRIPTION                           | REV-A FOR SUBMITTAL |       |      |   |  |  |  |
|              |                                       |                     |       |      |   |  |  |  |
|              |                                       |                     |       |      |   |  |  |  |
|              |                                       |                     |       |      |   |  |  |  |
| SITE ADDRESS |                                       |                     |       |      |   |  |  |  |
| STREET       | 2301 South Shelley Circle Bldg. A & B |                     |       |      |   |  |  |  |
| CITY         | Costa Mesa                            |                     |       |      |   |  |  |  |
| STATE        | CA                                    | ZIP                 | 92626 |      |   |  |  |  |
| JOB #:       | 26034                                 |                     |       | REV: | A |  |  |  |
| MOD #:       |                                       |                     |       | REL: | 1 |  |  |  |
| SPEC PAGE    |                                       |                     |       |      |   |  |  |  |

| MATERIAL SCHEDULE |   |
|-------------------|---|
| TAG               | DESCRIPTION                                                                                           |
| MM-A              | WHITE MELAMINE                                                                                        |
| PL-A              | WHITE CAB LINER                                                                                       |
| PL-C              | (PL-1, WB-2) WILSONART "HARVEST MAPLE", 7953-38, FINE VELVET TEXTURE                                  |
| PL-D              | (PL-2) PIONITE "FOLKSTONE GRAY", SG241-SD, TEXTURED/SUEDE FINISH                                      |
| PL-E              | (PL-3) WILSONART "WHITE", 1570-60, FINE VELVET TEXTURE 1570-38                                        |
| PL-F              | (PL-4) WILSONART "CARBON MESH", 4880-38, FINE VELVET TEXTURE                                          |
| PL-G              | (PL-5) WILSONART "FRENCH LINEN", 5016-38, FINE VELVET TEXTURE                                         |
| PG-A              | (CR-1) SOLID POPLAR, DELIVERED PRIMED (PREPPING, PAINTING, FILLING OF ATTACHMENT HOLES BY OTHERS)     |
| PG-B              | (WB-1) MDF, DELIVERED PRIMED (PREPPING, PAINTING, FILLING OF ATTACHMENT HOLES BY OTHERS)              |
| PG-C              | (CR-1) FINGER JOINT PINE, DELIVERED PRIME (PREPPING, PAINTING, FILLING OF ATTACHMENT HOLES BY OTHERS) |
| WD-A              | (WD-1) SURFACING SOLUTIONS, MAPLE TAMBOUR HALF ROUND, PROFILE 383, 3/4"W x 5/16"H                     |
| GL-A              | 1/4" CLEAR TEMPERED GLASS                                                                             |

| HARDWARE SCHEDULE |                                                                                   |
|-------------------|-----------------------------------------------------------------------------------|
| TAG               | DESCRIPTION                                                                       |
| H-1.2             | SALICE 0mm CLIP-ON HINGE PLATE EURO SCREW, BARGR09/16                             |
| H-1.3             | SALICE 110° FO SOFT-CLOSE, LOGICA SILENTIA, C7J6AE9                               |
| H-1.4             | SALICE 155° FO SOFT-CLOSE, LOGICA SILENTIA, C2JKAЕ9                               |
| H-1.8             | MCKINNEY DOUBLE ACTING SPRING HINGE,1001, 6", SATIN CHROME FINISH                 |
| H-2.0             | KNAPE & VOGT DRAWER SLIDES, KV8400, SIDE MOUNT, FULL EXT. 100lb LOAD RATING       |
| H-2.1             | KNAPE & VOGT DRAWER SLIDES, KV8600, SIDE MOUNT, FULL EXT. 150lb LOAD RATING       |
| H-3.0             | BERENSON WIRE PULL, BN6131-2SC-P, 96mm CTC, SATIN CHROME FINISH                   |
| H-4.0             | HAFELE SHELF SUPPORT, 282.04.711, 5mm SHELF PIN, STEEL NICKEL-PLATED              |
| H-4.1.1           | BRACKET, A&M CFLAT 21 (2.0)                                                       |
| H-4.1.2           | BRACKET, A&M CFLAT 24 (2.0)                                                       |
| H-4.6             | KNAPE & VOGT 80 SERIES SHELF STANDARDS & 180 SERIES 10" BRACKETS, WHITE FINISH    |
| H-5.0             | OLYMPUS DEADBOLT LOCK, 100DR, US26D SATIN CHROME FINISH                           |
| H-5.1             | OLYMPUS DEADBOLT LOCK, 200DW, US26D SATIN CHROME FINISH                           |
| H-5.5             | KITLOCK ELECTRONIC LOCKER LOCK, KL1100 RFID, BLACK FINISH                         |
| H-6.0             | MOCKETT TG FLIP-TOP SERIES DESK GROMMET, 2"Ø, COLOR T.B.D.                        |
| H-7.0             | 1/8" x 1-1/4" x 1-1/4" ALUMINUM L-ANGLE, MILL FINISH                              |
| H-7.1             | ORANGE ALUMINUM Z-CLIP HD PANEL RAIL                                              |
| H-7.2             | FRY REGLET MILLWORK REVEAL, 1" PANEL, 1/2" REVEAL, MWRB50P100, POWDER COATED      |
| H-7.3             | EAGLE ALUMINUM 1/8" CORNER ACCENT, MILL FINISH                                    |
| H-7.4             | McMASTER CARR ALUMINUM CHANNEL, 9001K664, 1-3/4"W x 1"H, MILL FINISH              |
| H-8.0             | KEKU CLIP, BLACK FINISH                                                           |
| H-9.0             | EPCO - ELBOW CATCH - 1018-N, BRIGHT NICKEL FINISH                                 |
| H-9.1             | GRAINGER - GRAB CATCH - 4PE50, STEEL                                              |
| H-9.2             | EZ KICK, ADA SINK MODESTY PANEL BRACKET, DDLMPB-WH, POWDER COATED WHITE FINISH    |
| H-9.4             | KNAPE & VOGT ROLL-EZY BALL-BEARING TRACK, 72"L                                    |
| H-9.5             | MOCKETT, GT-METAL AIR VENT GRILLE, 17"Wx4H" OPENING, MATTE BLACK FINISH W/ MESH/3 |
| H-9.6             | KNAPE & VOGT RATCHET LOCK, 965K 50 NP, POLISHED NICKEL FINISH                     |

| WOOD & FINISHING SPECIFICATIONS |           |               |                                     |                |              |                      |                        |                 |         |
|---------------------------------|-----------|---------------|-------------------------------------|----------------|--------------|----------------------|------------------------|-----------------|---------|
| MATERIAL TAG                    | SLICE/CUT | COATING       |                                     | GRAIN MATCHING |              |                      |                        |                 |         |
|                                 |           | STAIN         | FINISH                              | LEAVES         | WITHIN PANEL | INTER-PANEL VERTICAL | INTER-PANEL HORIZONTAL | DOORS & DRAWERS | SPECIAL |
| WD-A                            | PLAIN     | TO MATCH PL-1 | 2 COATS OF WATER-BASED POLYURETHANE | NONE           | NONE         | NONE                 | NONE                   | NONE            | NONE    |



CRESTMILLWORK

5640 WEST END ROAD  
ARCATA, CA 95521  
PH (707) 822-4034 FAX (707) 822-5478  
WWW.CRESTMILLWORK.COM

DGS SREOC COSTA  
MESA  
SCHEDULES

|              |                                       |                    |       |   |  |  |
|--------------|---------------------------------------|--------------------|-------|---|--|--|
| ISSUE        | DATE                                  | 05/05/2026         |       |   |  |  |
|              | DESCRIPTION                           | REVA FOR SUBMITTAL |       |   |  |  |
|              | BY                                    | Q-AS               |       |   |  |  |
|              |                                       |                    |       |   |  |  |
|              |                                       |                    |       |   |  |  |
| SITE ADDRESS |                                       |                    |       |   |  |  |
| STREET       | 2301 South Shelley Circle Bldg. A & B |                    |       |   |  |  |
| CITY         | Costa Mesa                            |                    |       |   |  |  |
| STATE        | CA                                    | ZIP                | 92626 |   |  |  |
| JOB #:       | 26034                                 |                    | REV:  | A |  |  |
| MOD #:       |                                       |                    | REL:  | 1 |  |  |
| SCHEDULES    |                                       |                    |       |   |  |  |

CHANGES / DISCREPANCIES - ARCHITECT RESPONSE REQUIRED PER NAAWS

Global Issues

Global Issues

Mod Specific

Mod Specific

MOD 1 (1.2), (1.9), (1.16)

- GROMMET LOCATION TO BE VERIFIED IN FIELD.
- ARCH PLAN SHOWS AN 18" WIDE PANEL NEAR TO THE DOOR SWING ON THE LEFT SIDE, IN ORDER TO MAINTAIN OVERALL WIDTH OF 160". THE PANEL WIDTH WAS INCREASED BY 2". PLEASE CONFIRM.
- COUNTERTOP DROP LIP REDUCED TO PROVIDED LEVELING ROOM BETWEEN ADA MINIMUM AND BOTTOM EDGE OF DROP LIP.
- PLEASE CONFIRM THE LOCK LOCATION.

MOD 2 (2.8)

- THE AV SUPPLIER TO MAKE SURE THE METAL PULLOUT TRAY WILL WORK PLEASE CONFIRM.

MOD 4 (4.5)

- COUNTERTOP LOWERED FOR DROP-IN SINK TO NOT CREATE AN ADA BUST. IN DOING THIS, THE UNDERCOUNTER REFRIGERATOR WILL INTERFERE WITH THE COUNTERTOP. PLEASE ADVISE. (Reference RFI 26034-1).

MOD 5 (5.1)

- THE ENLARGED PLAN VIEW (1/AE408) CALLS FOR THE SOUTH COUNTERTOP DEPTH TO BE 24" MAX WHILE THE ELEVATION (8/AE408) CALLS FOR 30" DEEP. PLEASE ADVISE.

MOD 6 (6.4), (6.10)

- MW-1 CALLS FOR A BUILT IN MICROWAVE WHICH REQUIRES A TRIM KIT THAT'S 30"W x 18"H. THE MICROWAVE CABINET IS DRAWN AT 28"W x 30"H. PLEASE ADVISE WHICH CABINETS WE CAN CHANGE.
- Z-CLIP INSTALLATION METHOD BEING USED FOR THE WALL PANELING. PLEASE CONFIRM THIS IS ACCEPTABLE.
- THERE COULD BE A POTENTIAL CONFLICT BETWEEN SINK AND BACKSPLASH. PLEASE ADVISE.
- DUE TO PRESENCE OF DROP-IN SINK (MODEL) WE HAVE REDUCED THE COUNTER HEIGHT TO 33-5/8" IN ORDER TO ACHIEVE THE POTENTIAL ADA COMPLIANCE & ALLOWING ENOUGH SPACE FOR APPLIANCE. PLEASE CONFIRM.

MOD 7 (7.5)

- WE HAVE PROVIDED THE 20" DEPTH CABINET BASED ON THE ARCH PLAN AE101.1.PLEASE CONFORIM.

SECTION (S6)

- FAUCET IS OUT OF ADA REACH COMPLIANCE PLEASE ADVISE.
- SINK CONFLICT WITH BACKSPLASH. PLEASE CONFIRM.
- SINK CONFIGURATION APPEARS TO CONFLICT WITH ADA CLEARANCE.

SECTION (S7)

- SINK CONFLICT WITH BACKSPLASH. PLEASE CONFIRM.




CRESTMARK  
MILLWORK

5640 WEST END ROAD  
ARCATA, CA 95521  
PH (707) 822-4034 FAX (707) 822-5478  
WWW.CRESTMARKMILLWORK.COM

DGS SREOC COSTA  
MESA

|              |                                       |                     |       |   |  |  |  |
|--------------|---------------------------------------|---------------------|-------|---|--|--|--|
| ISSUE        |                                       | DATE                | BY    |   |  |  |  |
|              |                                       | 05/05/2026          | Q-AS  |   |  |  |  |
| DESCRIPTION  |                                       | REV-A FOR SUBMITTAL |       |   |  |  |  |
|              |                                       |                     |       |   |  |  |  |
|              |                                       |                     |       |   |  |  |  |
|              |                                       |                     |       |   |  |  |  |
|              |                                       |                     |       |   |  |  |  |
| SITE ADDRESS |                                       |                     |       |   |  |  |  |
| STREET       | 2301 South Shelley Circle Bldg. A & B |                     |       |   |  |  |  |
| CITY         | Costa Mesa                            |                     |       |   |  |  |  |
| STATE        | CA                                    | ZIP                 | 92626 |   |  |  |  |
| JOB #:       | 26034                                 |                     | REV:  | A |  |  |  |
| MOD #:       |                                       |                     | REL:  |   |  |  |  |
| ARF          |                                       |                     |       |   |  |  |  |

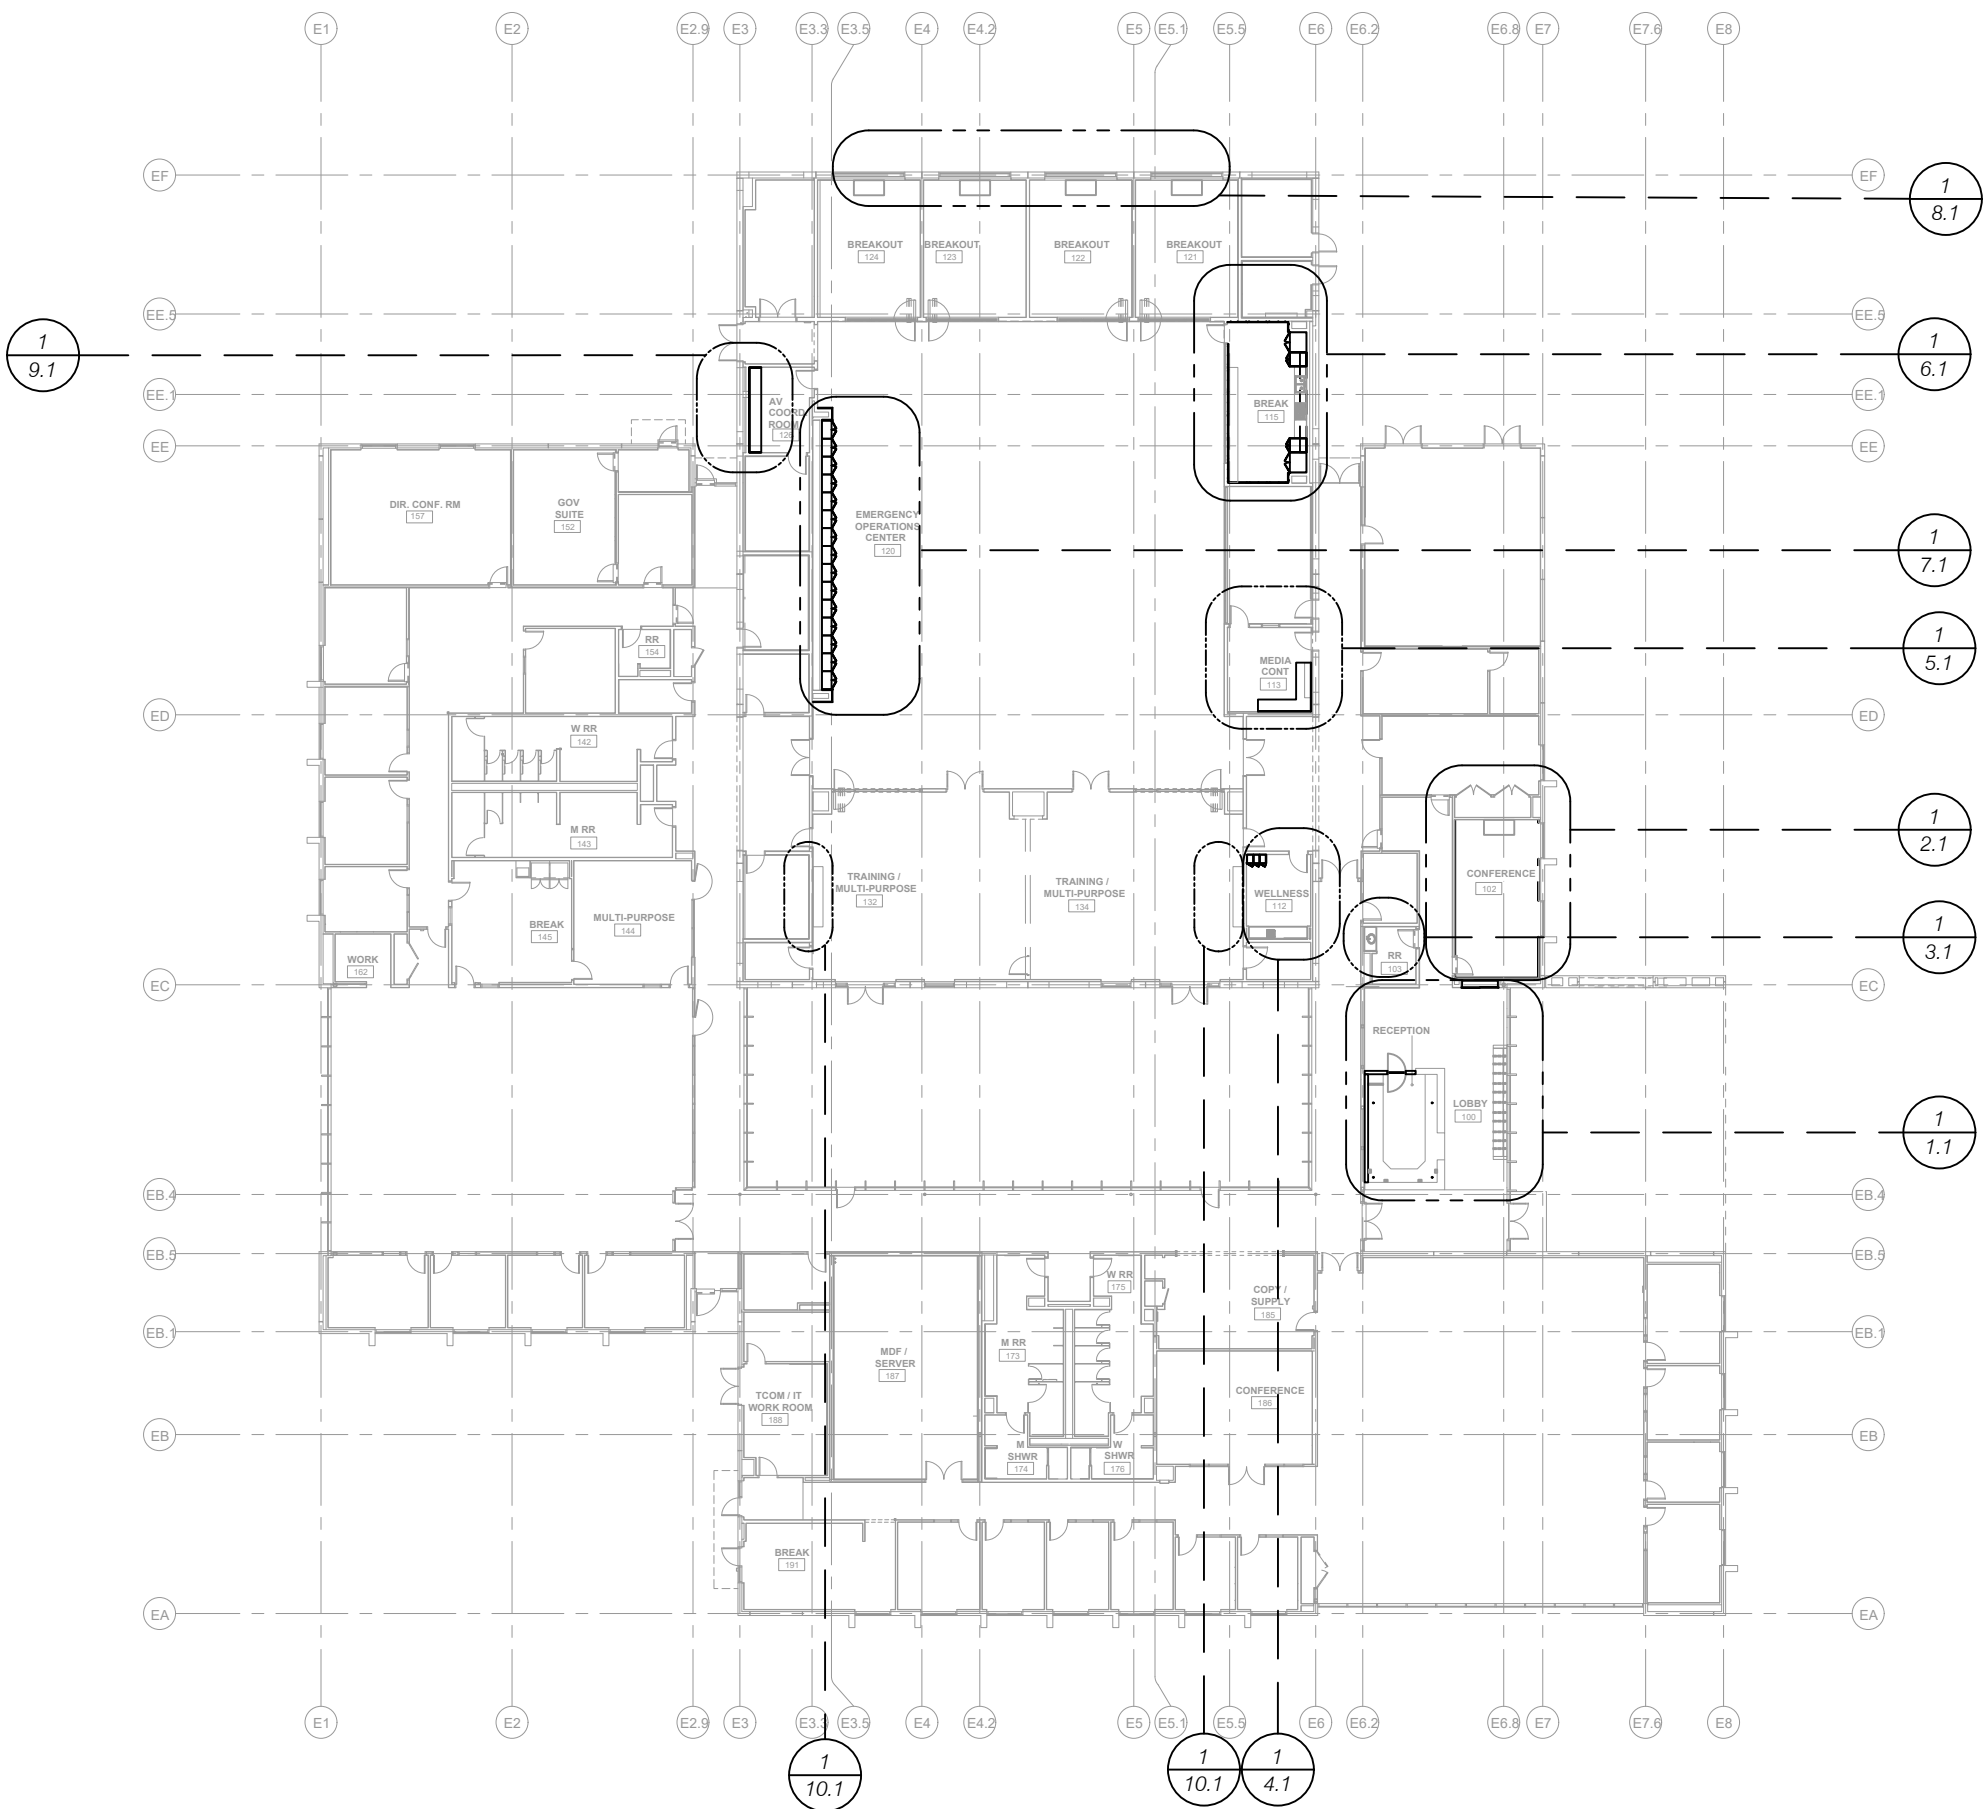


**1** OVERALL FLOOR PLAN - LEVEL - 1  
SCALE: NTS  
ARCH REF: 1/ AE101



5640 WEST END ROAD  
ARCATA, CA 95521  
PH (707) 822-4034 FAX (707) 822-5478  
WWW.CRESTMARKMILLWORK.COM

# DGS SREOC COSTA MESA FLOOR PLAN


| ISSUE        |                                       | BY        |
|--------------|---------------------------------------|-----------|
| DATE         | DESCRIPTION                           |           |
| 05/05/2026   | REV-A FOR SUBMITTAL                   | Q-AS      |
| -            | -                                     | -         |
| -            | -                                     | -         |
| SITE ADDRESS |                                       |           |
| STREET       | 2301 South Shelley Circle Bldg. A & B |           |
| CITY         | Costa Mesa                            |           |
| STATE        | CA                                    | ZIP 92626 |
| JOB #:       | 26034                                 | REV: A    |
| MOD #:       | ----                                  | REL: N/A  |
| FP.1         |                                       |           |

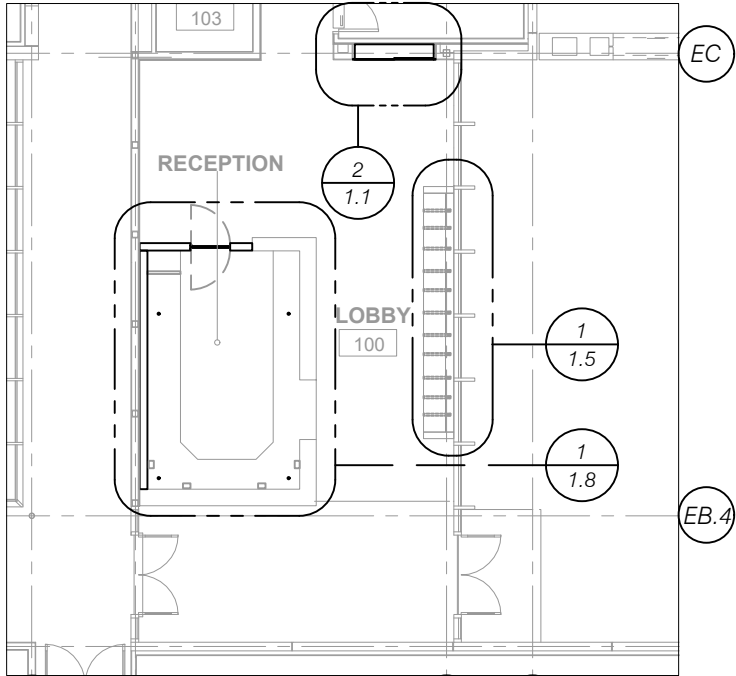


**1** KEY PLAN  
SCALE: NTS  
ARCH REF: 1/AE101.1

| NOTES |   |
|-------|---|
| 1     | ALL DIMENSIONS TO BE FIELD VERIFIED                                                                                          |
| 2     | GENERAL CONTRACTOR TO COORDINATE ALL FRAMING REQUIREMENTS WITH CMI                                                           |
| 3     | GENERAL CONTRACTOR TO COORDINATE ALL WALL TYPES, THICKNESSES AND ROUGH OPENINGS                                              |
| 4     | GENERAL CONTRACTOR & ELECTRICAL CONTRACTOR TO COORDINATE ALL ELECTRICAL BOX LOCATIONS & REQUIREMENTS WITH MILLWORK DRAWINGS  |
| 5     | GENERAL CONTRACTOR & ELECTRICAL CONTRACTOR TO COORDINATE ALL LIGHT FIXTURE FEED & SWITCHING LOCATIONS WITH MILLWORK DRAWINGS |
| 6     | GENERAL CONTRACTOR & PLUMBING CONTRACTOR TO COORDINATE ALL PLUMBING FIXTURES & INSTALLATION REQUIREMENTS                     |

| MATERIALS |              |                                                                                |
|-----------|--------------|--------------------------------------------------------------------------------|
| PL-C      | (PL-1, WB-2) | WILSONART "HARVEST MAPLE", 7953-38, FINE VELVET TEXTURE                        |
| PL-D      | (PL-2)       | PIONITE "FOLKSTONE GRAY", SG241-SD, TEXTURED/SUEDE FINISH                      |
| PL-E      | (PL-3)       | WILSONART "WHITE", 1570-60, MATTE FINISH                                       |
| GL-A      |              | 1/4" CLEAR TEMPERED GLASS                                                      |
| QTY.      |              | HARDWARE                                                                       |
| H-4.6     | X            | KNAPE & VOGT 80 SERIES SHELF STANDARDS & 180 SERIES 10" BRACKETS, WHITE FINISH |
| H-9.4     | X            | KNAPE & VOGT ROLL - EZY BALL - BEARING TRACK, 72" L                            |
| H-9.6     | X            | KNAPE & VOGT RATCHET LOCK, 965K 50 NP, POLISHED NICKEL FINISH                  |

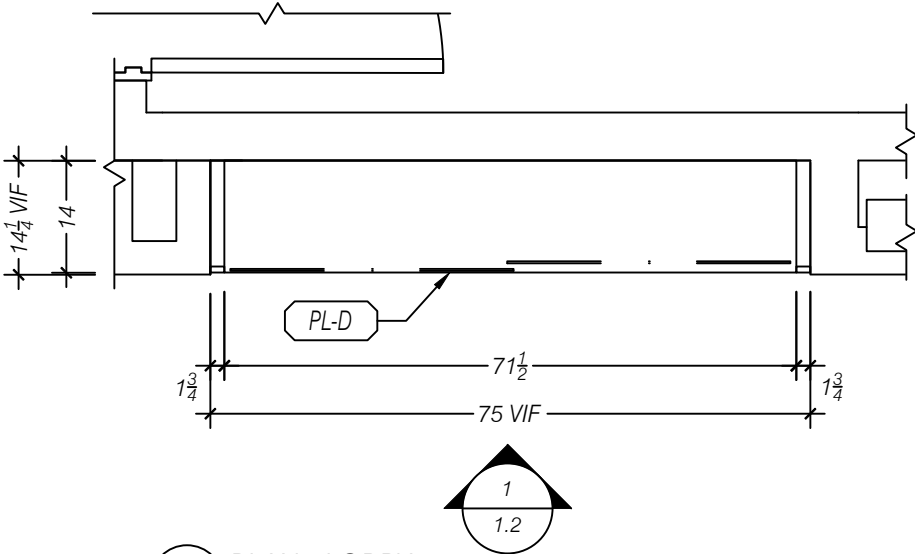


**2** PLAN - LOBBY 100  
SCALE 1:24 (1/2" = 1'-0")  
ARCH REF: 1/AE401

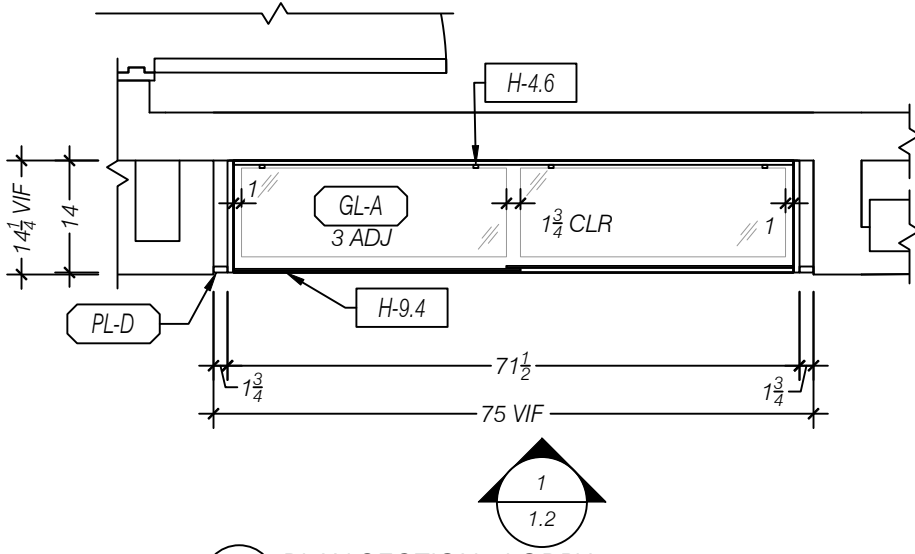

**3** PLAN SECTION - LOBBY 100  
SCALE 1:24 (1/2" = 1'-0")  
ARCH REF: 5/AE582

**DGS SREOC COSTA**  
**MESA**  
**LOBBY 100**

| ISSUE       |  | BY   | DATE                | SITE ADDRESS                          |  |  |  |  |
|-------------|--|------|---------------------|---------------------------------------|--|--|--|--|
| DESCRIPTION |  | Q-AS | REV-A FOR SUBMITTAL | 2301 South Shelley Circle BLDG. A & B |  |  |  |  |
|             |  | -    | -                   | Costa Mesa                            |  |  |  |  |
|             |  | -    | -                   | CA 92626                              |  |  |  |  |
|             |  | -    | -                   | JOB #: 26034 REV: A                   |  |  |  |  |
|             |  | -    | -                   | MOD #: 1 REL: N/A                     |  |  |  |  |
|             |  | -    | -                   | <b>1.1</b>                            |  |  |  |  |

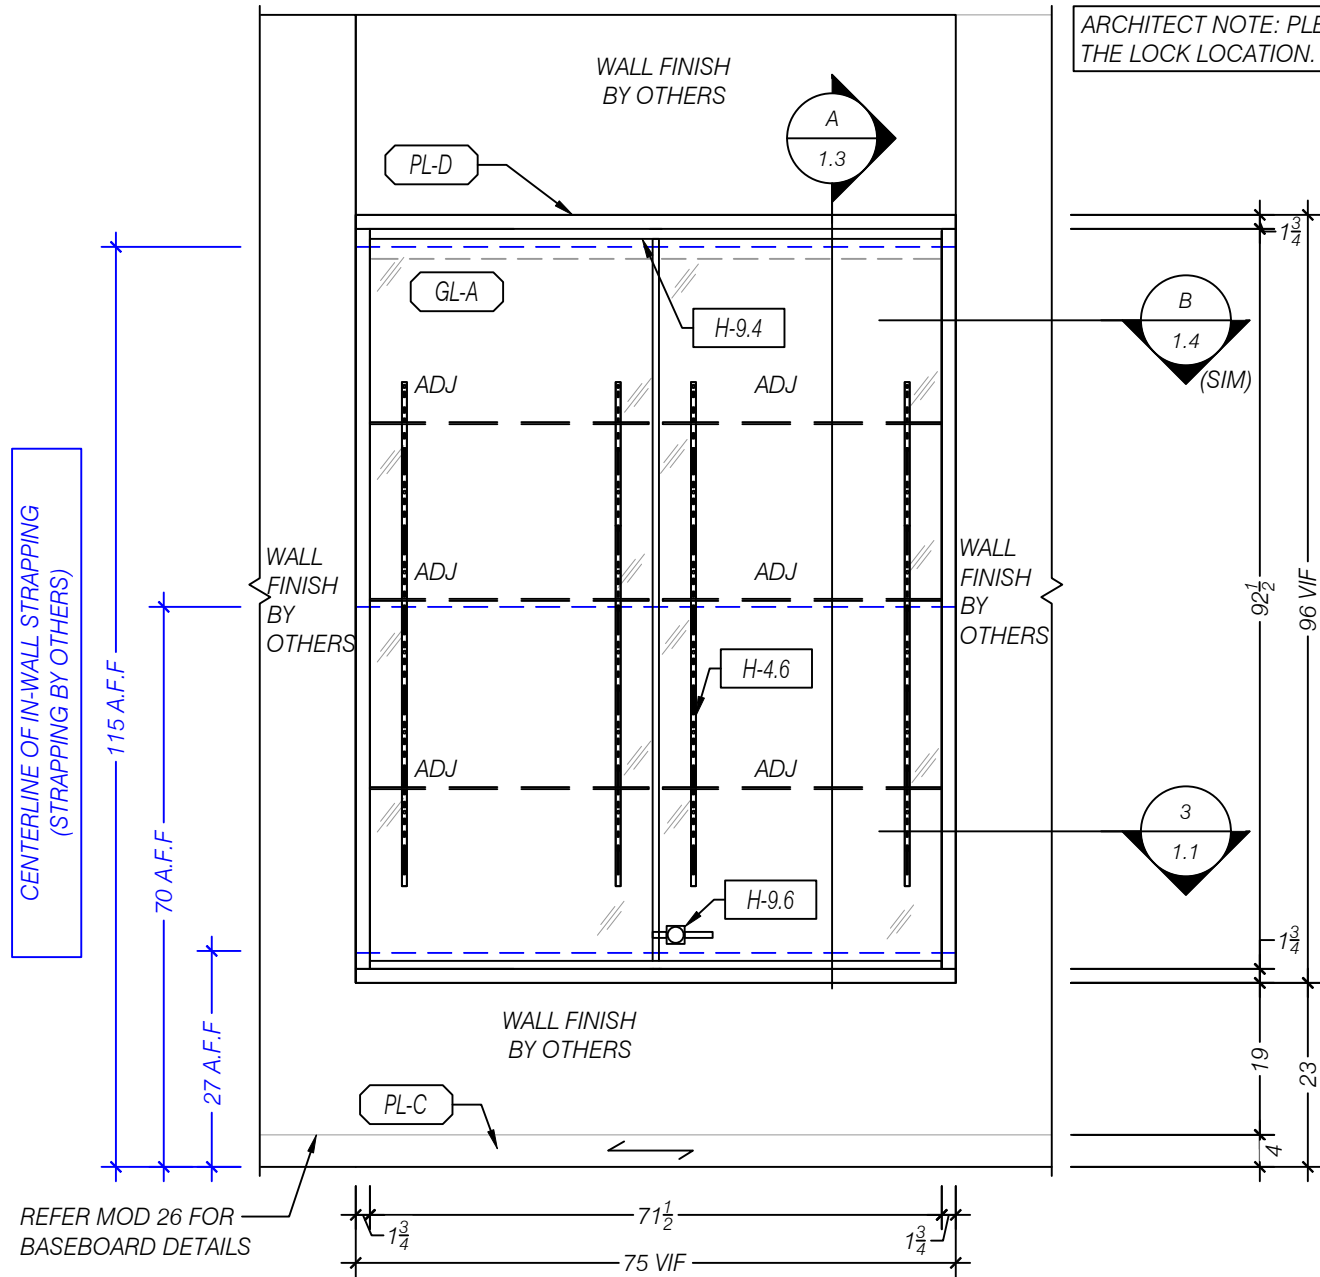


**1** ELEVATION NORTH - LOBBY 100  
SCALE 1:24 (1/2"=1'-0")  
ARCH REF: 3/AE401

|                  |                                                                      |                                                                                |
|------------------|----------------------------------------------------------------------|--------------------------------------------------------------------------------|
| <div></div>      | MATERIALS                                                            |                                                                                |
| <div>PL-C</div>  | (PL-1, WB-2) WILSONART "HARVEST MAPLE", 7953-38, FINE VELVET TEXTURE |                                                                                |
| <div>PL-D</div>  | (PL-2) PIONITE "FOLKSTONE GRAY", SG241-SD, TEXTURED/SUEDE FINISH     |                                                                                |
| <div>PL-E</div>  | (PL-3) WILSONART "WHITE", 1570-60, MATTE FINISH                      |                                                                                |
| <div>GL-A</div>  | 1/4" CLEAR TEMPERED GLASS                                            |                                                                                |
| <div></div>      | QTY.                                                                 | HARDWARE                                                                       |
| <div>H-4.6</div> | X                                                                    | KNAPE & VOGT 80 SERIES SHELF STANDARDS & 180 SERIES 10" BRACKETS, WHITE FINISH |
| <div>H-9.4</div> | X                                                                    | KNAPE & VOGT ROLL - EZY BALL - BEARING TRACK, 72" L                            |
| <div>H-9.6</div> | X                                                                    | KNAPE & VOGT RATCHET LOCK, 965K 50 NP, POLISHED NICKEL FINISH                  |

DGS SREOC COSTA  
MESA  
LOBBY 100

| ISSUE        |                                       | BY        |
|--------------|---------------------------------------|-----------|
| DATE         | DESCRIPTION                           |           |
| 05/05/2026   | REV-A FOR SUBMITTAL                   | Q-AS      |
| -            | -                                     | -         |
| -            | -                                     | -         |
| SITE ADDRESS |                                       |           |
| STREET       | 2301 South Shelley Circle BLDG. A & B |           |
| CITY         | Costa Mesa                            |           |
| STATE        | CA                                    | ZIP 92626 |
| JOB #:       | 26034                                 | REV: A    |
| MOD #:       | 1                                     | REL: N/A  |
| 1.2          |                                       |           |

|       | MATERIALS                 |                                                                                |
|-------|---------------------------|--------------------------------------------------------------------------------|
| PL-C  | (PL-1, WB-2)              | WILSONART "HARVEST MAPLE", 7953-38, FINE VELVET TEXTURE                        |
| PL-D  | (PL-2)                    | PIONITE "FOLKSTONE GRAY", SG241-SD, TEXTURED/SUEDE FINISH                      |
| PL-E  | (PL-3)                    | WILSONART "WHITE", 1570-60, MATTE FINISH                                       |
| GL-A  | 1/4" CLEAR TEMPERED GLASS |                                                                                |
|       | QTY.                      | HARDWARE                                                                       |
| H-4.6 | X                         | KNAPE & VOGT 80 SERIES SHELF STANDARDS & 180 SERIES 10" BRACKETS, WHITE FINISH |
| H-9.4 | X                         | KNAPE & VOGT ROLL - EZY BALL - BEARING TRACK, 72" L                            |
| H-9.6 | X                         | KNAPE & VOGT RATCHET LOCK, 965K 50 NP, POLISHED NICKEL FINISH                  |

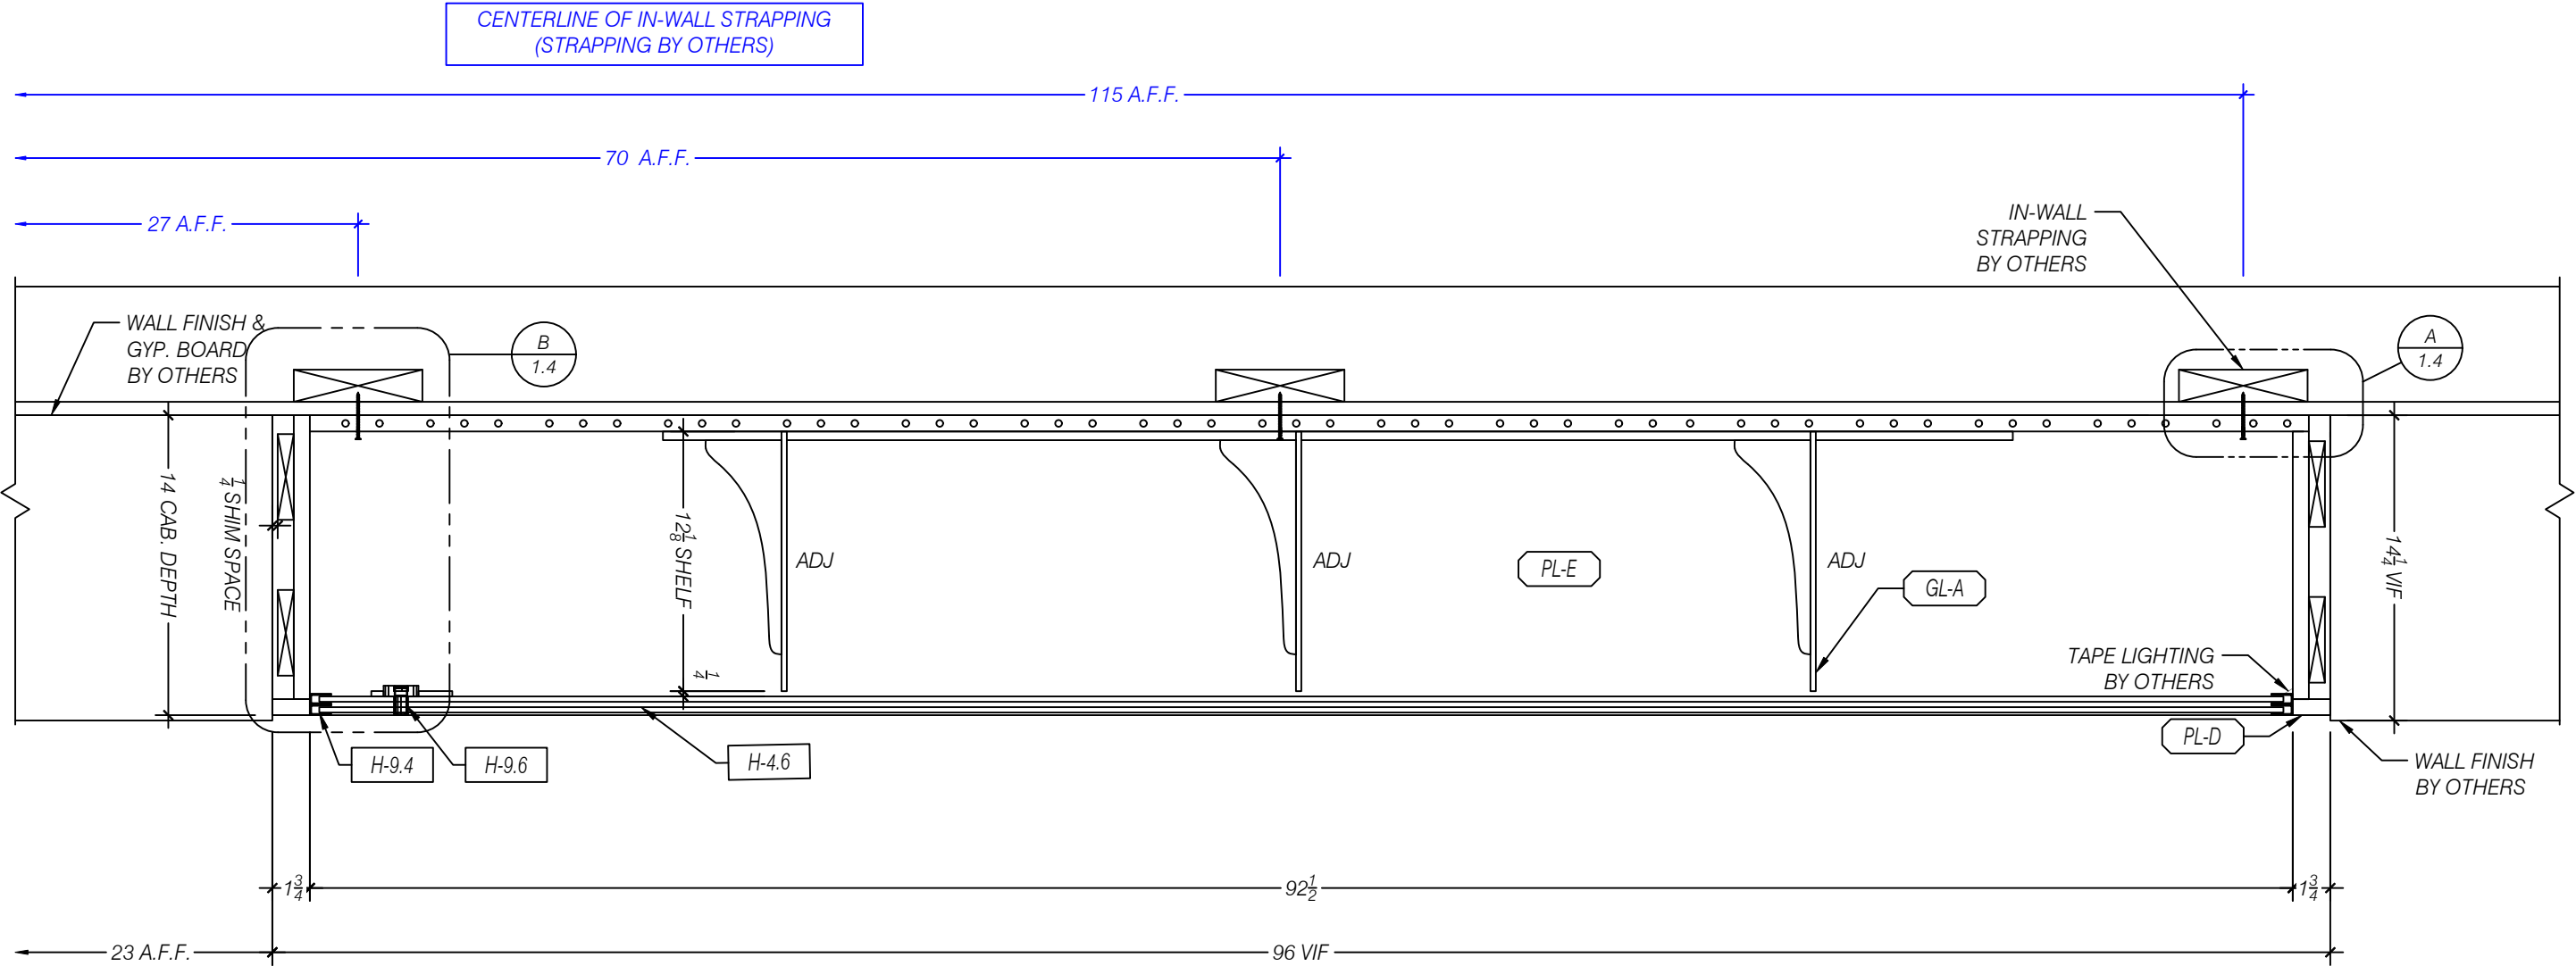

**A** SECTION - UPPER CABINET w/ SLIDING DOOR  
SCALE 1:8 (1 1/2"=1'-0")  
ARCH REF: 10/AE582




5640 WEST END ROAD  
ARCATA, CA 95521  
PH (707) 822-4034 FAX (707) 822-5478  
WWW.CRESTMARKMILLWORK.COM

**DGS SREOC COSTA**  
**MESA**  
**LOBBY 100**

| ISSUE      |                     | BY   |
|------------|---------------------|------|
| DATE       | DESCRIPTION         | Q-AS |
| 05/05/2026 | REV-A FOR SUBMITTAL | -    |
| -          | -                   | -    |
| -          | -                   | -    |
| -          | -                   | -    |
| -          | -                   | -    |


| SITE ADDRESS |                                       |      |       |
|--------------|---------------------------------------|------|-------|
| STREET       | 2301 South Shelley Circle BLDG. A & B |      |       |
| CITY         | Costa Mesa                            |      |       |
| STATE        | CA                                    | ZIP  | 92626 |
| JOB #:       | 26034                                 | REV: | A     |
| MOD #:       | 1                                     | REL: | N/A   |

SHIMMING/SURFACE BLOCKING IS THE RESPONSIBILITY OF THE INSTALLER  
SURFACE BLOCKING/WALL CLEATS/Z-CLIPS WILL BE PROVIDED BY CRESTMARK (U.O.N.)  
CRESTMARK IS NOT RESPONSIBLE FOR GAPS DUE TO IRREGULAR WALL SURFACES  
IN THE EVENT OF EXTREME GAPS, A SURFACE MOUNT FLAT MOLDING WILL BE USED (U.O.N.)

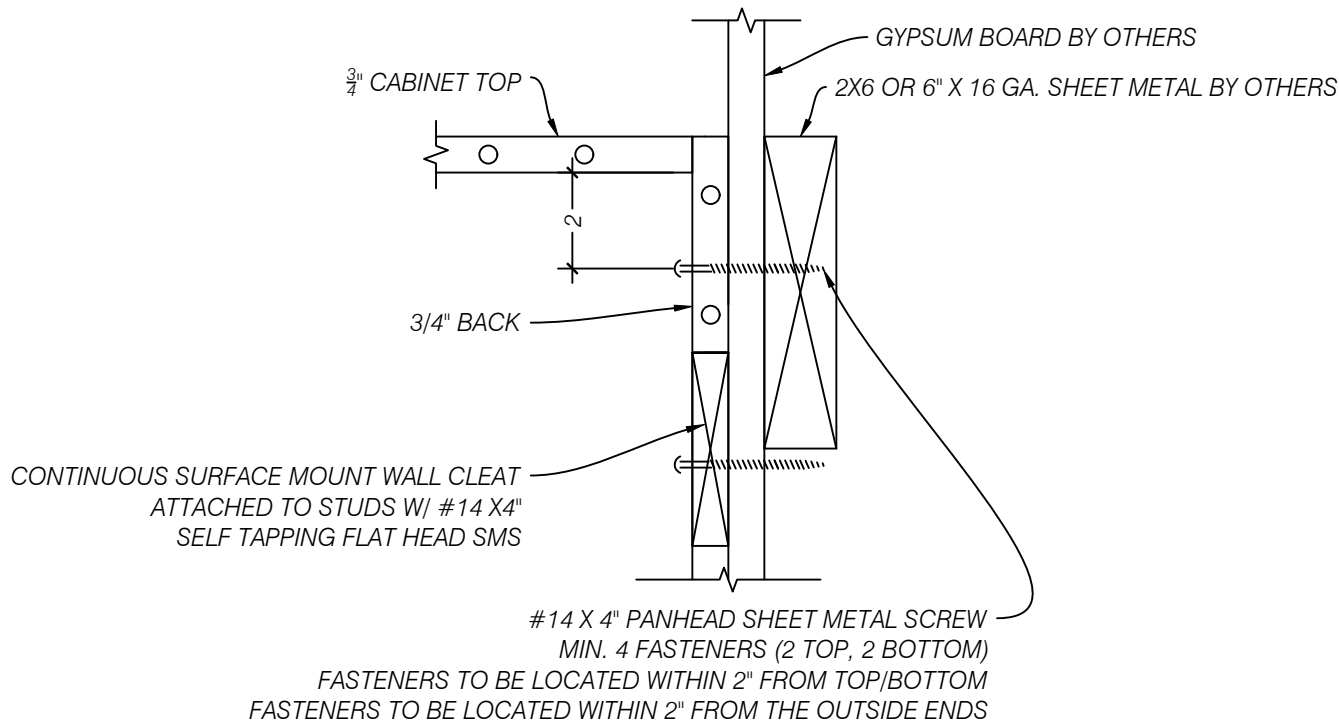

**A** ENLARGED DETAIL - THICK BACK WALL CABINET ATTACHMENT @ WALL  
SCALE 1:4 (3"=1'-0")  
ARCH REF: NA

|                  |      | MATERIALS                                                                      |
|------------------|------|--------------------------------------------------------------------------------|
| <div>PL-C</div>  |      | (PL-1, WB-2) WILSONART "HARVEST MAPLE", 7953-38, FINE VELVET TEXTURE           |
| <div>PL-D</div>  |      | (PL-2) PIONITE "FOLKSTONE GRAY", SG241-SD, TEXTURED/SUEDE FINISH               |
| <div>PL-E</div>  |      | (PL-3) WILSONART "WHITE", 1570-60, MATTE FINISH                                |
| <div>GL-A</div>  |      | 1/4" CLEAR TEMPERED GLASS                                                      |
|                  | QTY. | HARDWARE                                                                       |
| <div>H-4.6</div> | X    | KNAPE & VOGT 80 SERIES SHELF STANDARDS & 180 SERIES 10" BRACKETS, WHITE FINISH |
| <div>H-9.4</div> | X    | KNAPE & VOGT ROLL - EZY BALL - BEARING TRACK, 72" L                            |
| <div>H-9.6</div> | X    | KNAPE & VOGT RATCHET LOCK, 965K 50 NP, POLISHED NICKEL FINISH                  |

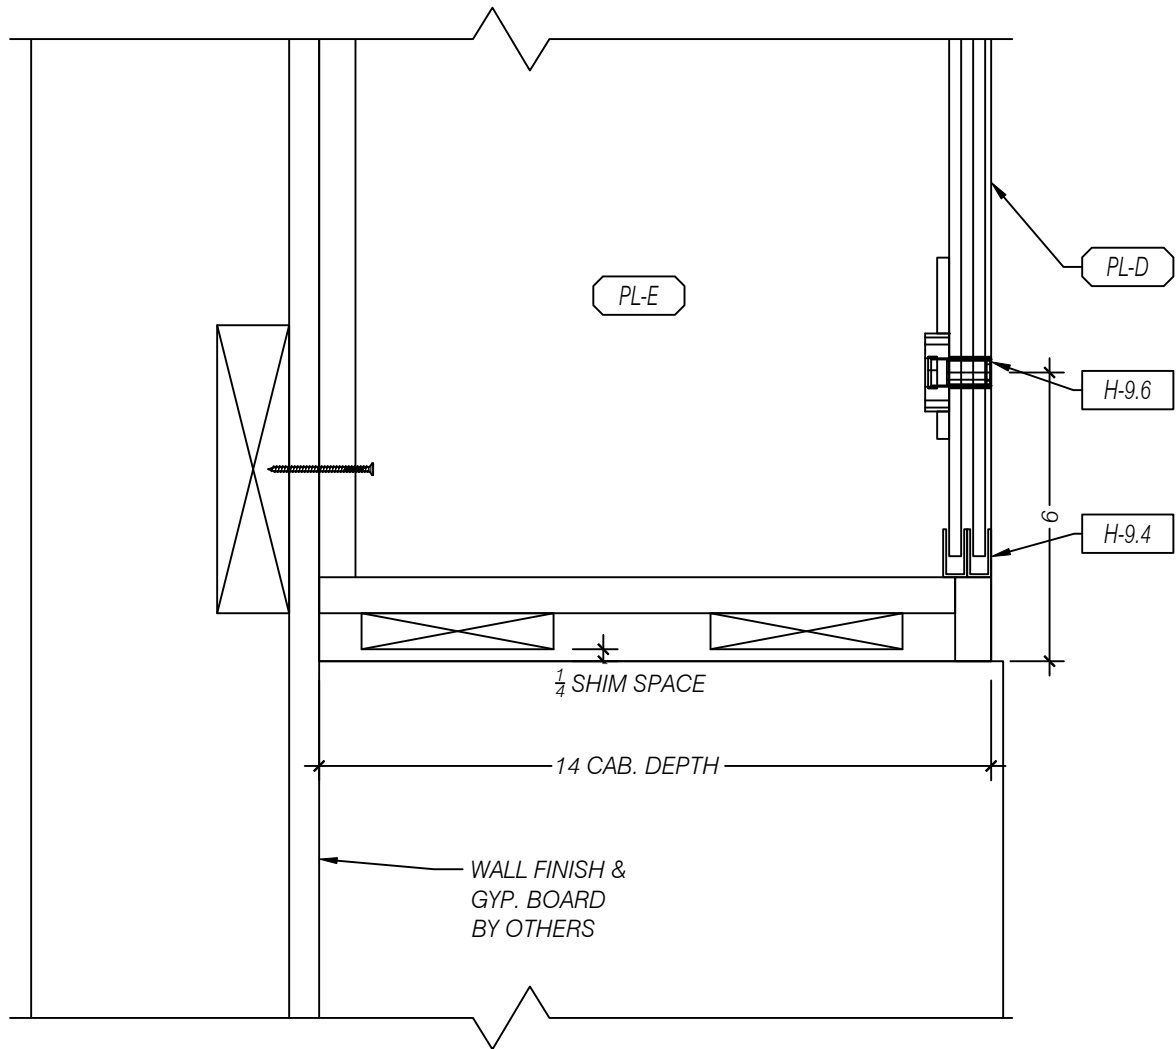


**B** ENLARGED DETAIL - SLIDING DOOR w/ TRIM  
SCALE 1:4 (3"=1'-0")  
ARCH REF: NA

DGS SREOC COSTA



MESA

LOBBY 100

| ISSUE        |                                       |      | BY    |     |  |  |
|--------------|---------------------------------------|------|-------|-----|--|--|
| DATE         | DESCRIPTION                           | Q-AS |       |     |  |  |
| 05/05/2026   | REV-A FOR SUBMITTAL                   |      |       |     |  |  |
|              |                                       |      |       |     |  |  |
|              |                                       |      |       |     |  |  |
|              |                                       |      |       |     |  |  |
|              |                                       |      |       |     |  |  |
| SITE ADDRESS |                                       |      |       |     |  |  |
| STREET       | 2301 South Shelley Circle BLDG. A & B |      |       |     |  |  |
| CITY         | Costa Mesa                            |      |       |     |  |  |
| STATE        | CA                                    | ZIP  | 92626 |     |  |  |
| JOB #:       | 26034                                 |      | REV:  | A   |  |  |
| MOD #:       | 1                                     |      | REL:  | N/A |  |  |
| 1.4          |                                       |      |       |     |  |  |

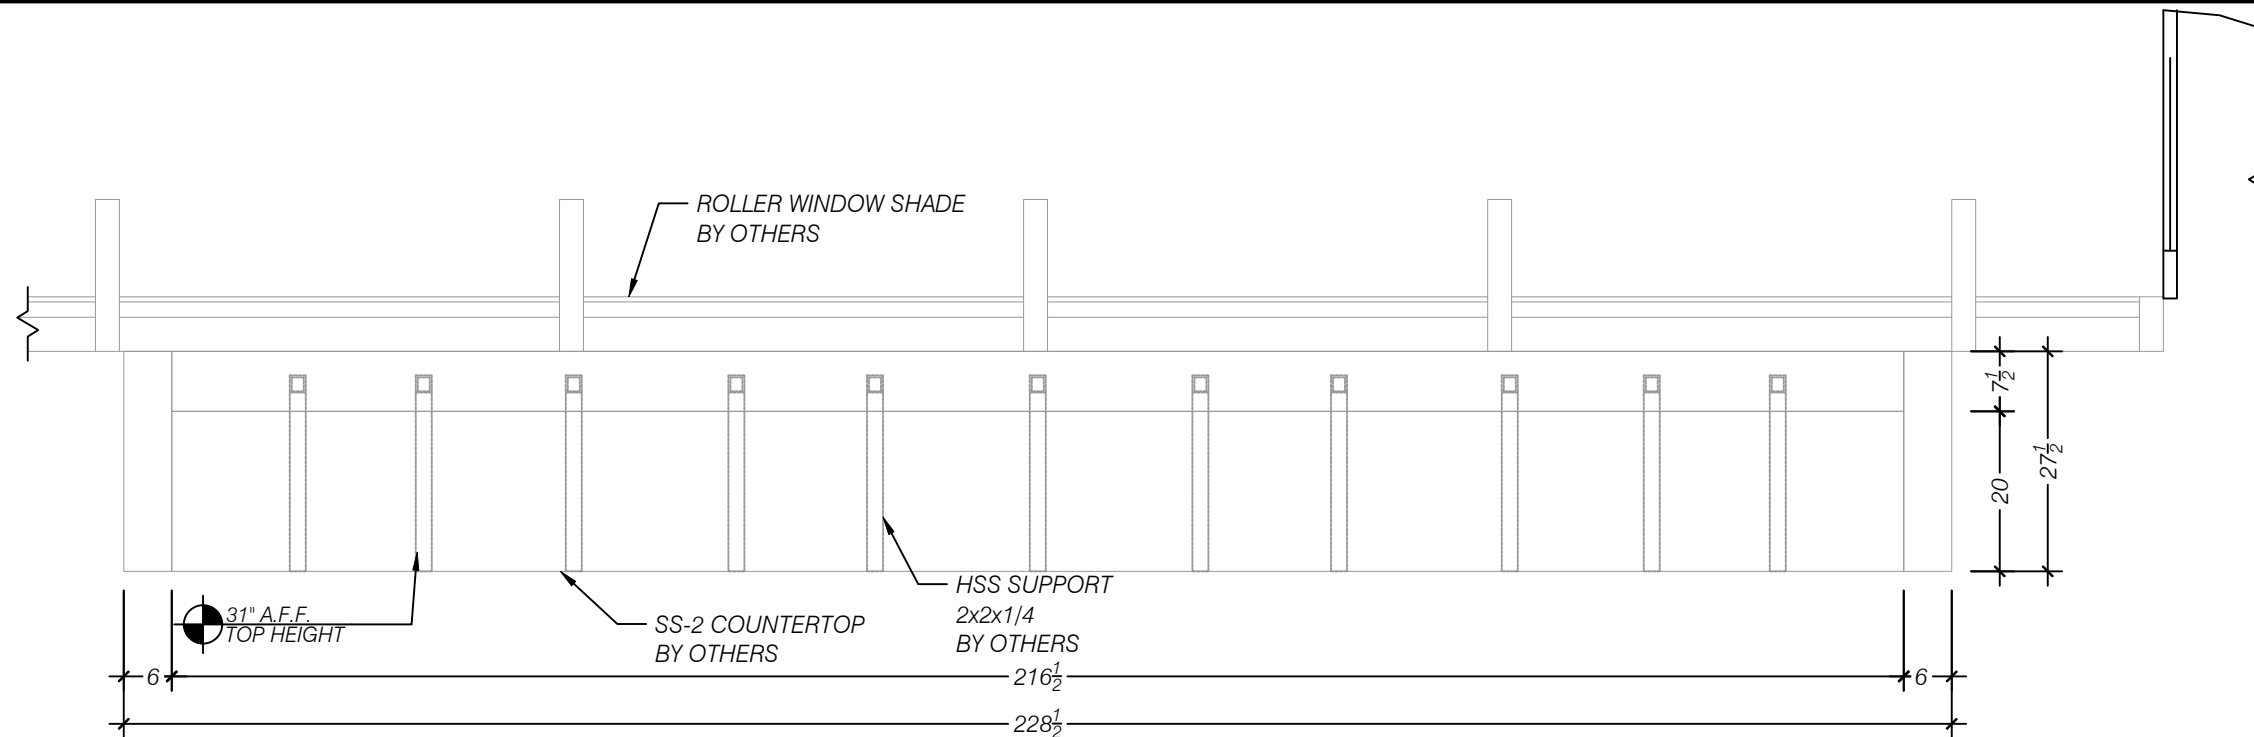

**1** PLAN - LOBBY 100  
SCALE 1:24 (1/2"=1'-0")  
ARCH REF: 1/ AE401

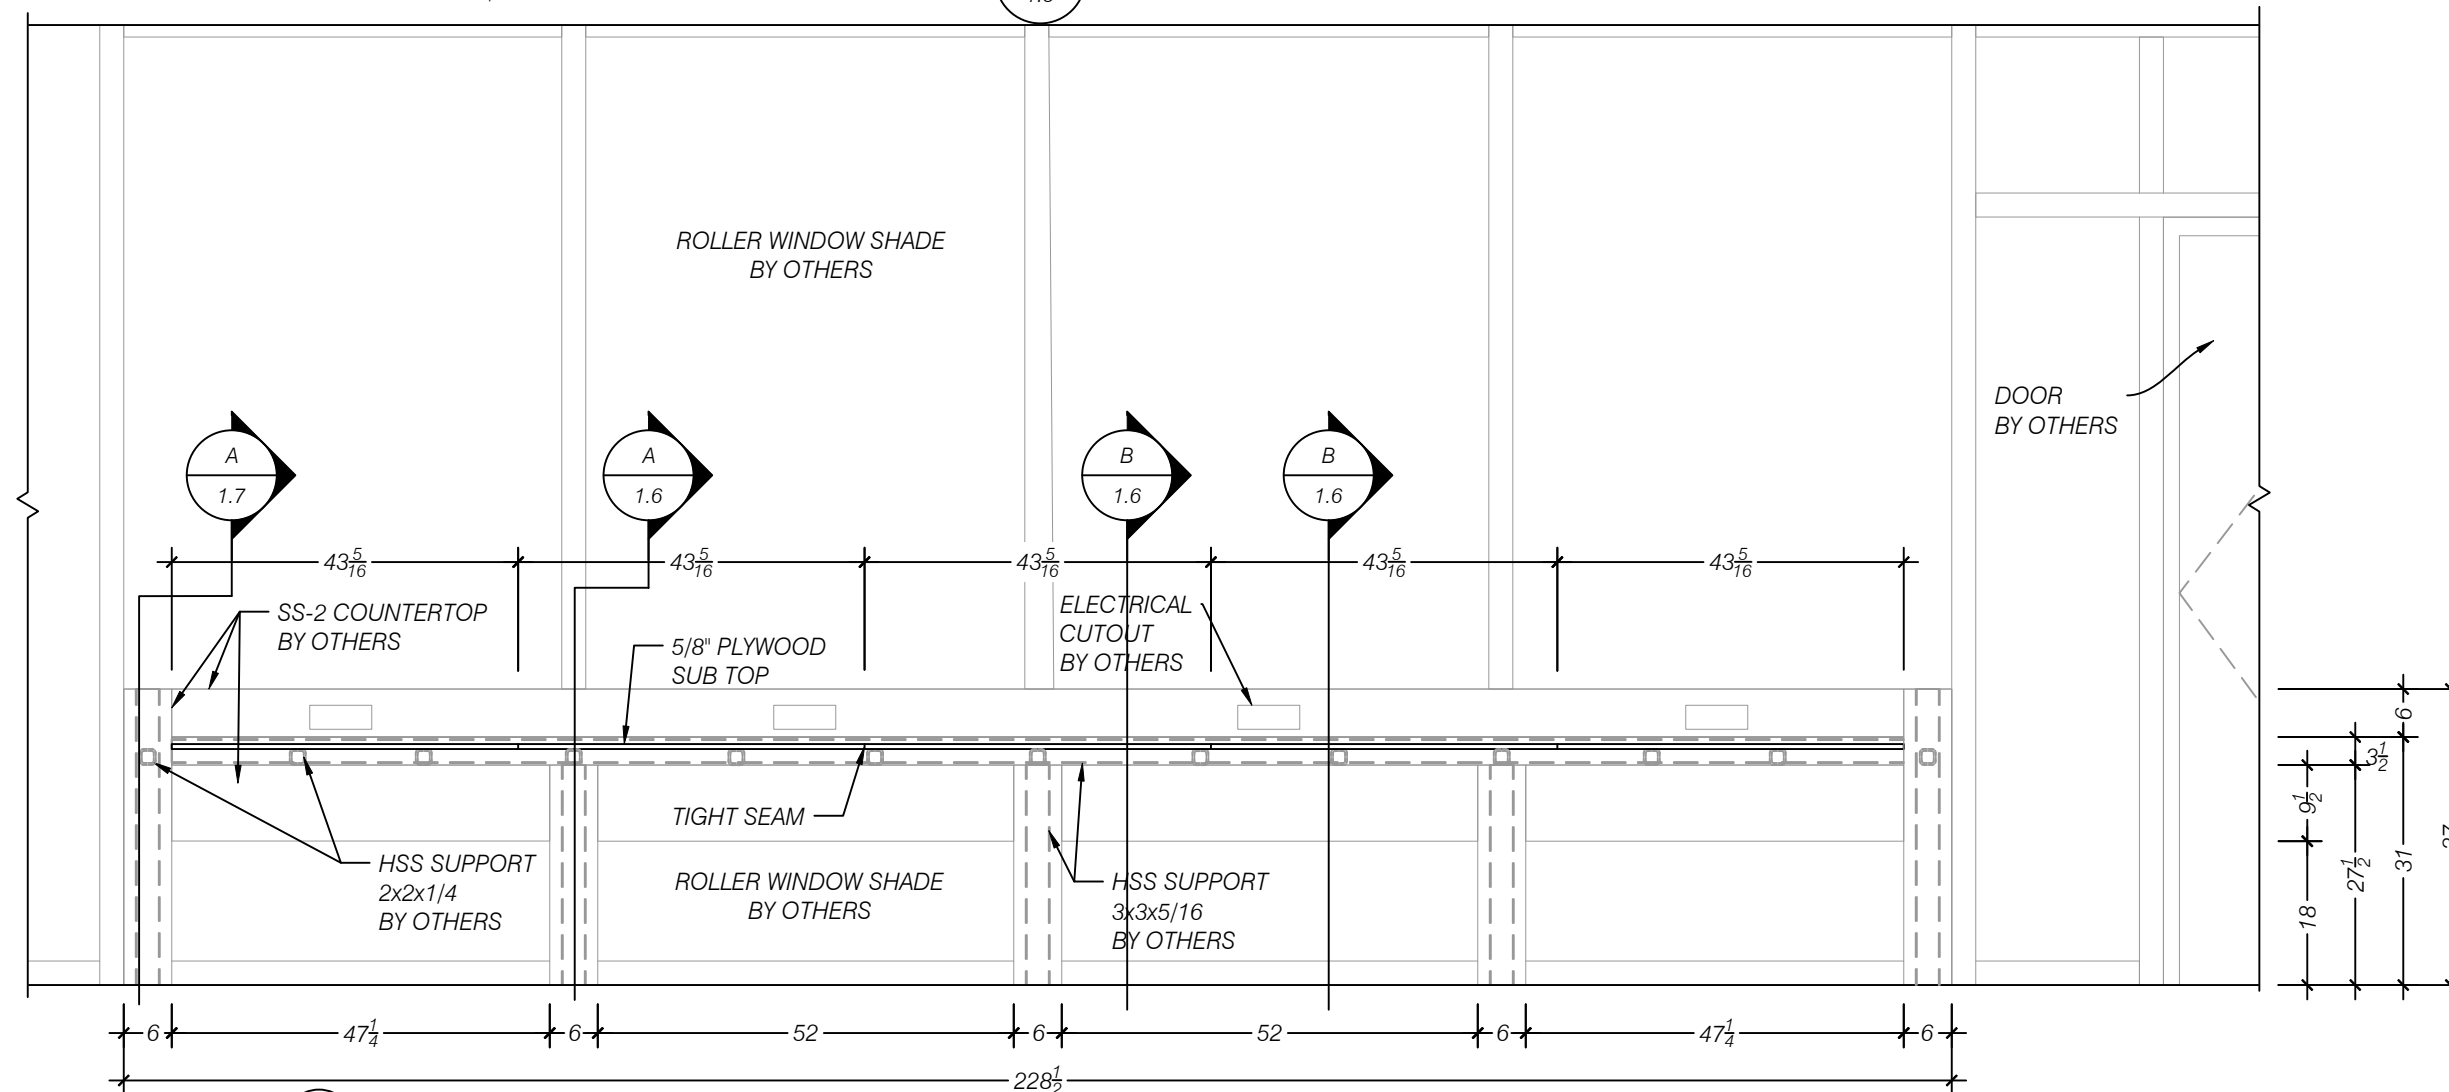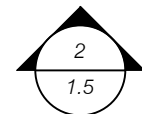



**2** ELEVATION EAST - LOBBY 100  
SCALE 1:24 (1/2"=1'-0")  
ARCH REF: 6/AE401

**DGS SREOC COSTA**  
**MESA**  
**LOBBY 100**

| ISSUE      |                     | BY   |
|------------|---------------------|------|
| DATE       | DESCRIPTION         |      |
| 05/05/2026 | REV-A FOR SUBMITTAL | Q-AS |
| -          | -                   | -    |
| -          | -                   | -    |
| -          | -                   | -    |
| -          | -                   | -    |

| SITE ADDRESS |                                       |      |       |
|--------------|---------------------------------------|------|-------|
| STREET       | 2301 South Shelley Circle BLDG. A & B |      |       |
| CITY         | Costa Mesa                            |      |       |
| STATE        | CA                                    | ZIP  | 92626 |
| JOB #:       | 26034                                 | REV: | A     |
| MOD #:       | 1                                     | REL: | N/A   |

**1.5**

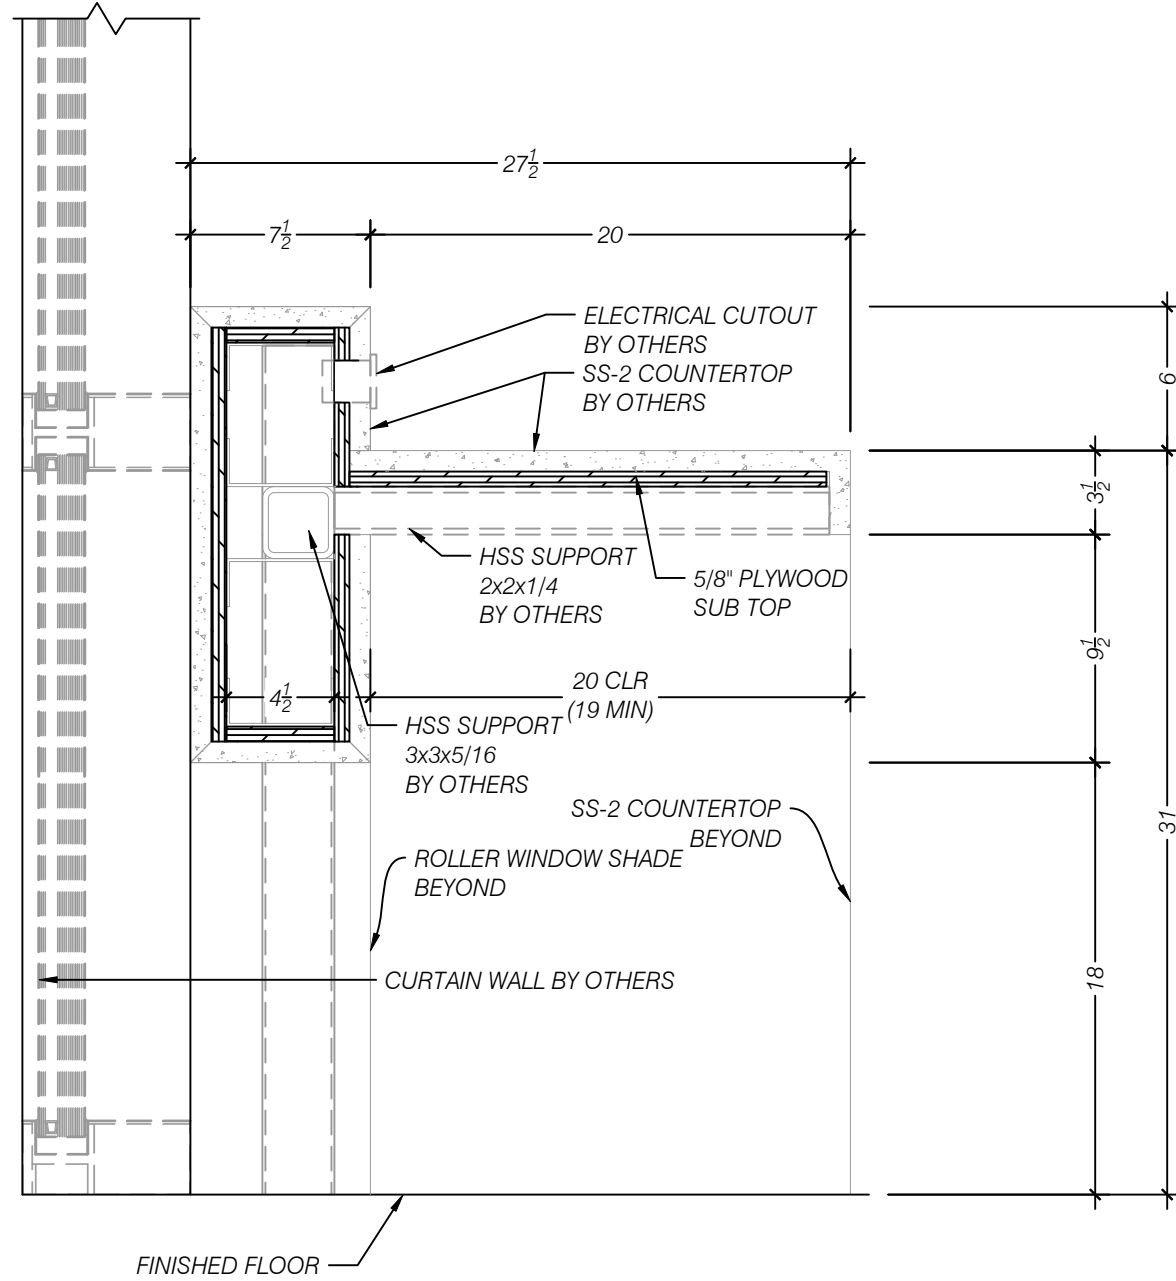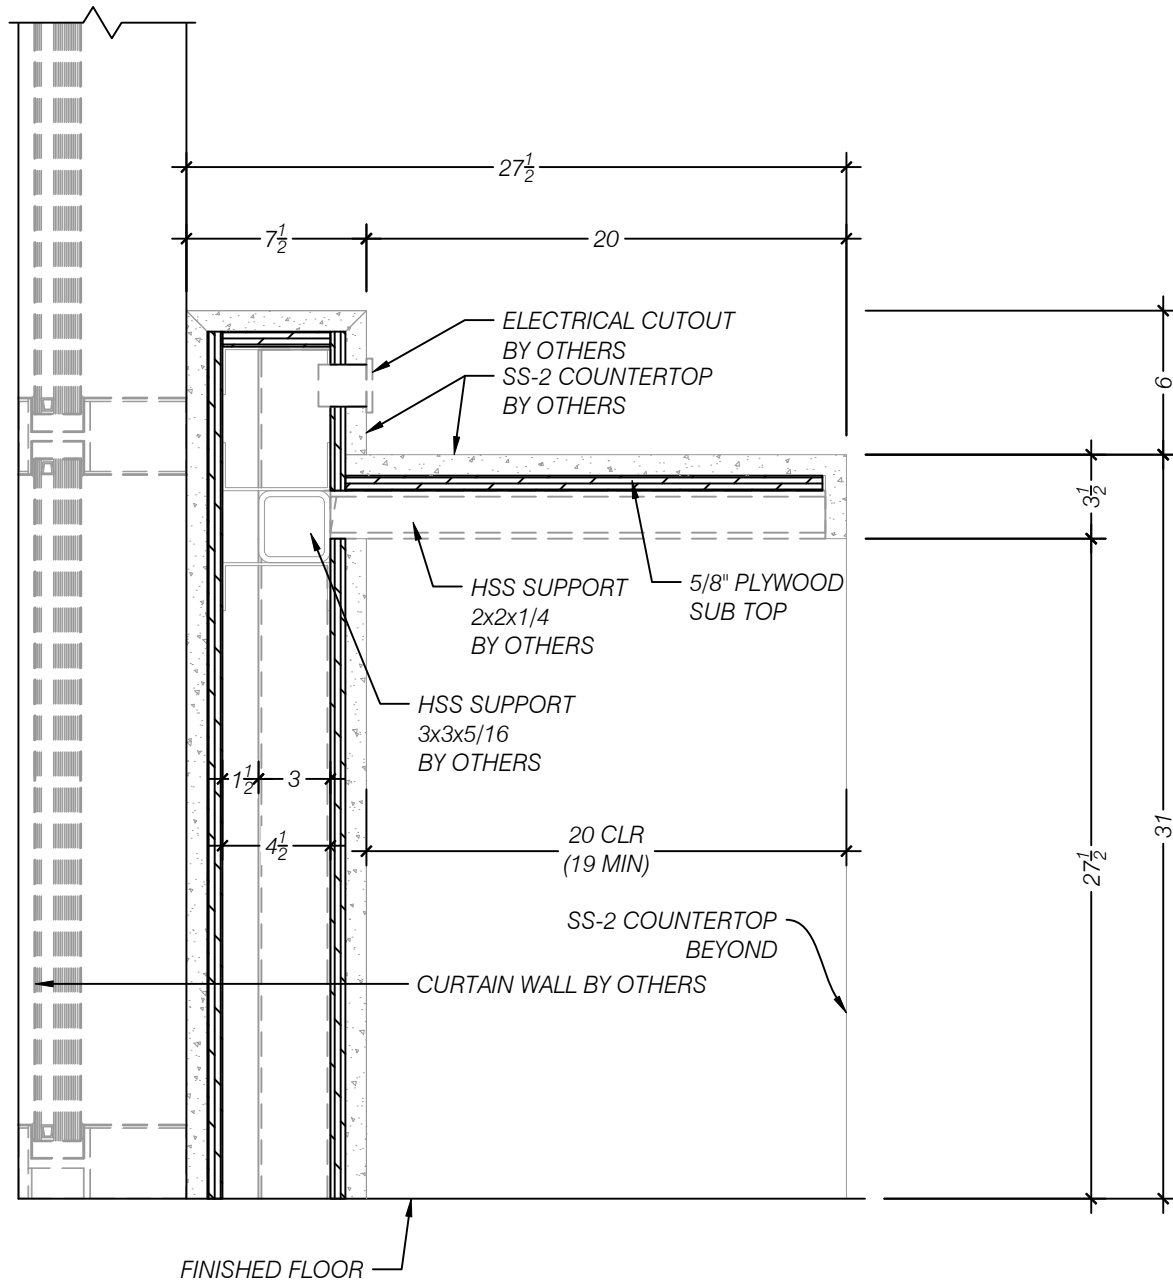

**DGS SREOC COSTA**  
**MESA**  
**LOBBY 100**

| DATE       | DESCRIPTION         | BY   |
|------------|---------------------|------|
| 05/05/2026 | REV-A FOR SUBMITTAL | Q-AS |
| -          | -                   | -    |
| -          | -                   | -    |
| -          | -                   | -    |
| -          | -                   | -    |

| SITE ADDRESS |                                       |      |       |
|--------------|---------------------------------------|------|-------|
| STREET       | 2301 South Shelley Circle BLDG. A & B |      |       |
| CITY         | Costa Mesa                            |      |       |
| STATE        | CA                                    | ZIP  | 92626 |
| JOB #:       | 26034                                 | REV: | A     |
| MOD #:       | 1                                     | REL: | N/A   |


DGS SREOC COSTA

MESA

LOBBY 100

| ISSUE      |                     |      |
|------------|---------------------|------|
| DATE       | DESCRIPTION         | BY   |
| 05/05/2026 | REV-A FOR SUBMITTAL | Q-AS |
| -          | -                   | -    |
| -          | -                   | -    |
| SITE ADDRESS |                                       |      |       |
|--------------|---------------------------------------|------|-------|
| STREET       | 2301 South Shelley Circle BLDG. A & B |      |       |
| CITY         | Costa Mesa                            |      |       |
| STATE        | CA                                    | ZIP  | 92626 |
| JOB #:       | 26034                                 | REV: | A     |
| MOD #:       | 1                                     | REL: | N/A   |

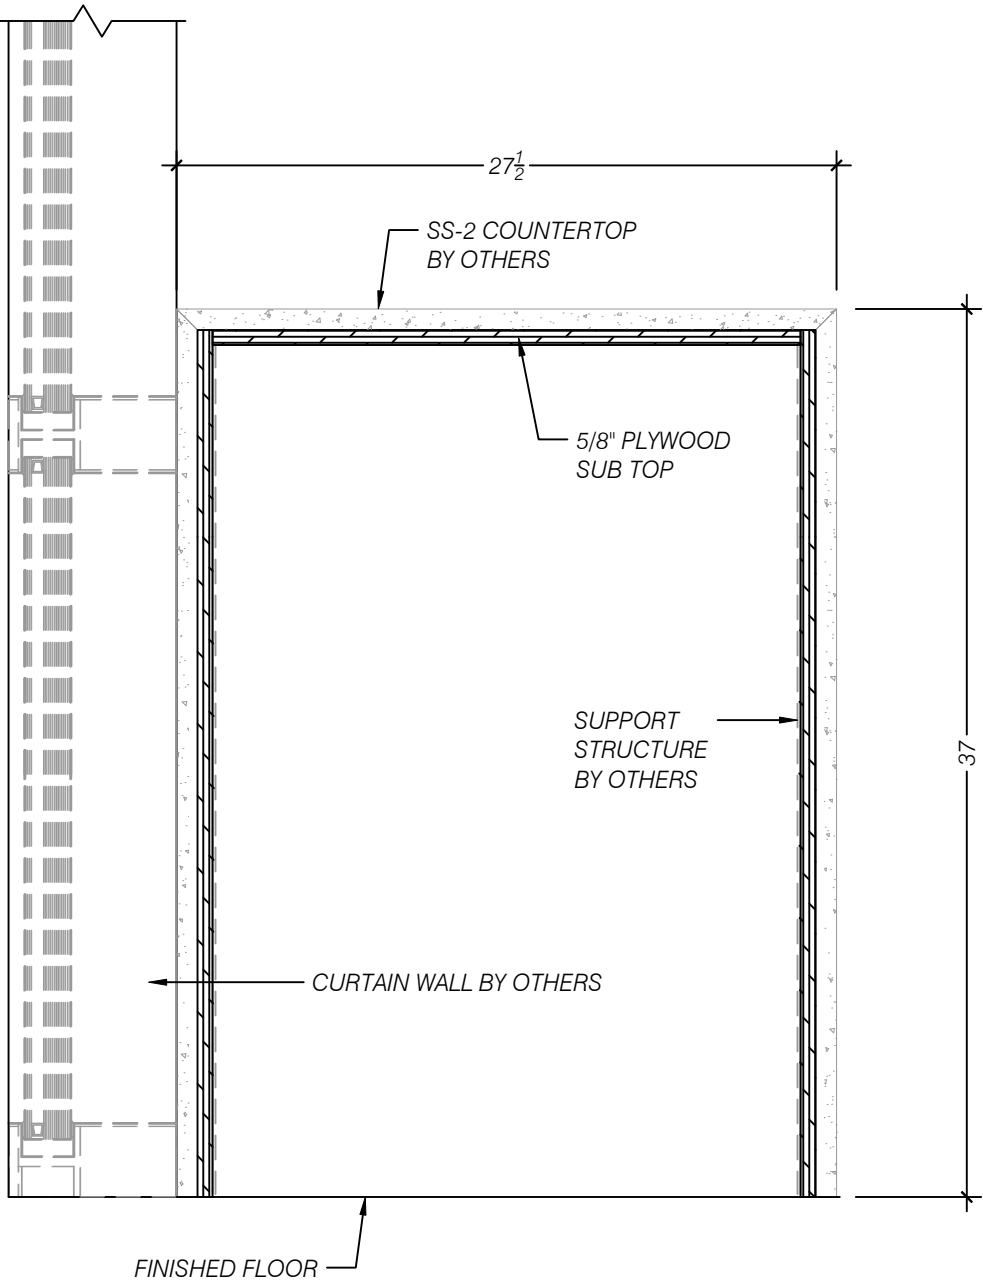


A

SECTION - COUNTERTOP @ MULLION

SCALE 1:8 (1 1/2"=1'-0")

ARCH REF: NA

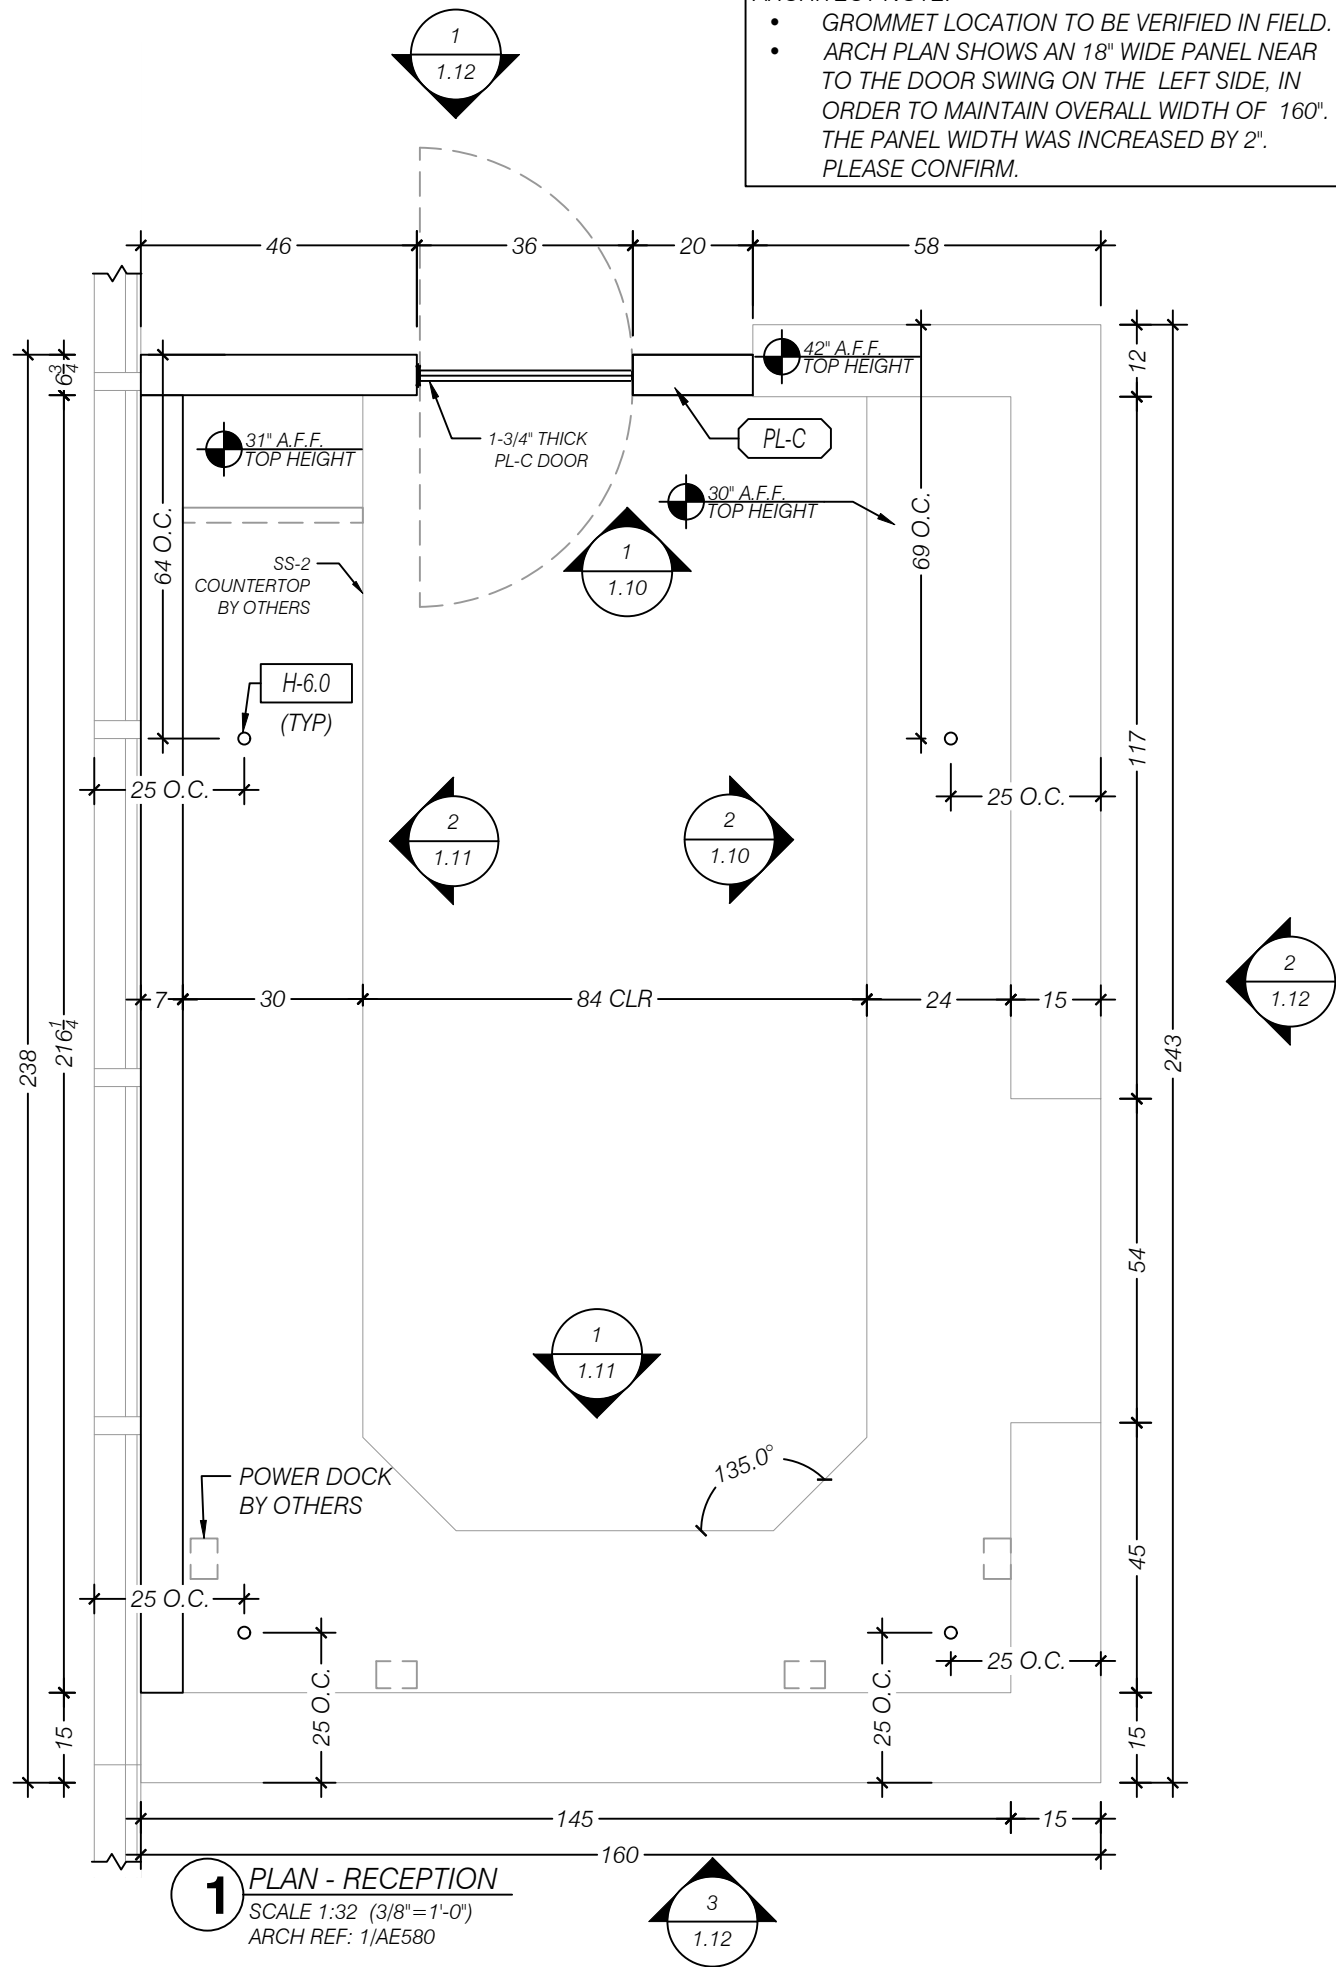


|        |      | MATERIALS                                                                         |
|--------|------|-----------------------------------------------------------------------------------|
| (MM-A) |      | WHITE MELAMINE                                                                    |
| (PL-C) |      | (PL-1, WB-2) WILSONART "HARVEST MAPLE", 7953-38, FINE VELVET TEXTURE              |
| (PL-E) |      | (PL-3) WILSONART "WHITE", 1570-60, FINE VELVET TEXTURE 1570-38                    |
| (WD-A) |      | (WD-1) SURFACING SOLUTIONS, MAPLE TAMBOUR HALF ROUND, PROFILE 383, 3/4"W x 5/16"H |
|        | QTY. | HARDWARE                                                                          |
| H-1.2  | X    | SALICE 0mm CLIP-ON HINGE PLATE EURO SCREW, BARGR09/16                             |
| H-1.3  | X    | SALICE 110° FO SOFT-CLOSE, LOGICA SILENTIA, C7J6AE9                               |
| H-1.8  | X    | MC KINNEY DOUBLE ACTING SPRING HINGE, 1001,6",SATIN CHROME FINISH                 |
| H-2.0  | X    | KNAPE & VOGT DRAWER SLIDES, KV8400, SIDE MOUNT, FULL EXT. 100lb LOAD RATING       |
| H-2.1  | X    | KNAPE & VOGT DRAWER SLIDES, KV8600, SIDE MOUNT, FULL EXT. 150lb LOAD RATING       |
| H-3.0  | X    | BERENSON WIRE PULL, BN6131-2SC-P, 96mm CTC, SATIN CHROME FINISH                   |
| H-4.0  | X    | HAFELE SHELF SUPPORT, 282.04.711, 5mm SHELF PIN, STEEL NICKEL-PLATED              |
| H-6.0  | X    | MOCKETT TG FLIP-TOP SERIES DESK GROMMET, 2"Ø, COLOR T.B.D.                        |
| H-7.1  | X    | ORANGE ALUMINUM Z-CLIP HD PANEL RAIL                                              |
| H-7.2  | X    | FRY REGLET MILLWORK REVEAL, 1" PANEL, 1/2" REVEAL, MWRB50P100, POWDER COATED      |
| H-7.3  | X    | EAGLE ALUMINUM 1/8" CORNER ACCENT, MILL FINISH                                    |
| H-7.4  | X    | McMASTER CARR ALUMINUM CHANNEL, 9001K664, 1-3/4"W x 1"H, MILL FINISH              |
| H-8.0  | X    | KEKU CLIP, BLACK FINISH                                                           |

DGS SREOC COSTA

MESA

RECEPTION

| ISSUE        |                                       |      |       |  |
|--------------|---------------------------------------|------|-------|--|
| DATE         | DESCRIPTION                           | BY   |       |  |
| 05/05/2026   | REV-A FOR SUBMITTAL                   | Q-AS |       |  |
|              |                                       |      |       |  |
|              |                                       |      |       |  |
|              |                                       |      |       |  |
|              |                                       |      |       |  |
| SITE ADDRESS |                                       |      |       |  |
| STREET       | 2301 South Shelley Circle BLDG. A & B |      |       |  |
| CITY         | Costa Mesa                            |      |       |  |
| STATE        | CA                                    | ZIP  | 92626 |  |
| JOB #:       | 26034                                 | REV: | A     |  |
| MOD #:       | 1                                     | REL: | N/A   |  |
| 1.8          |                                       |      |       |  |

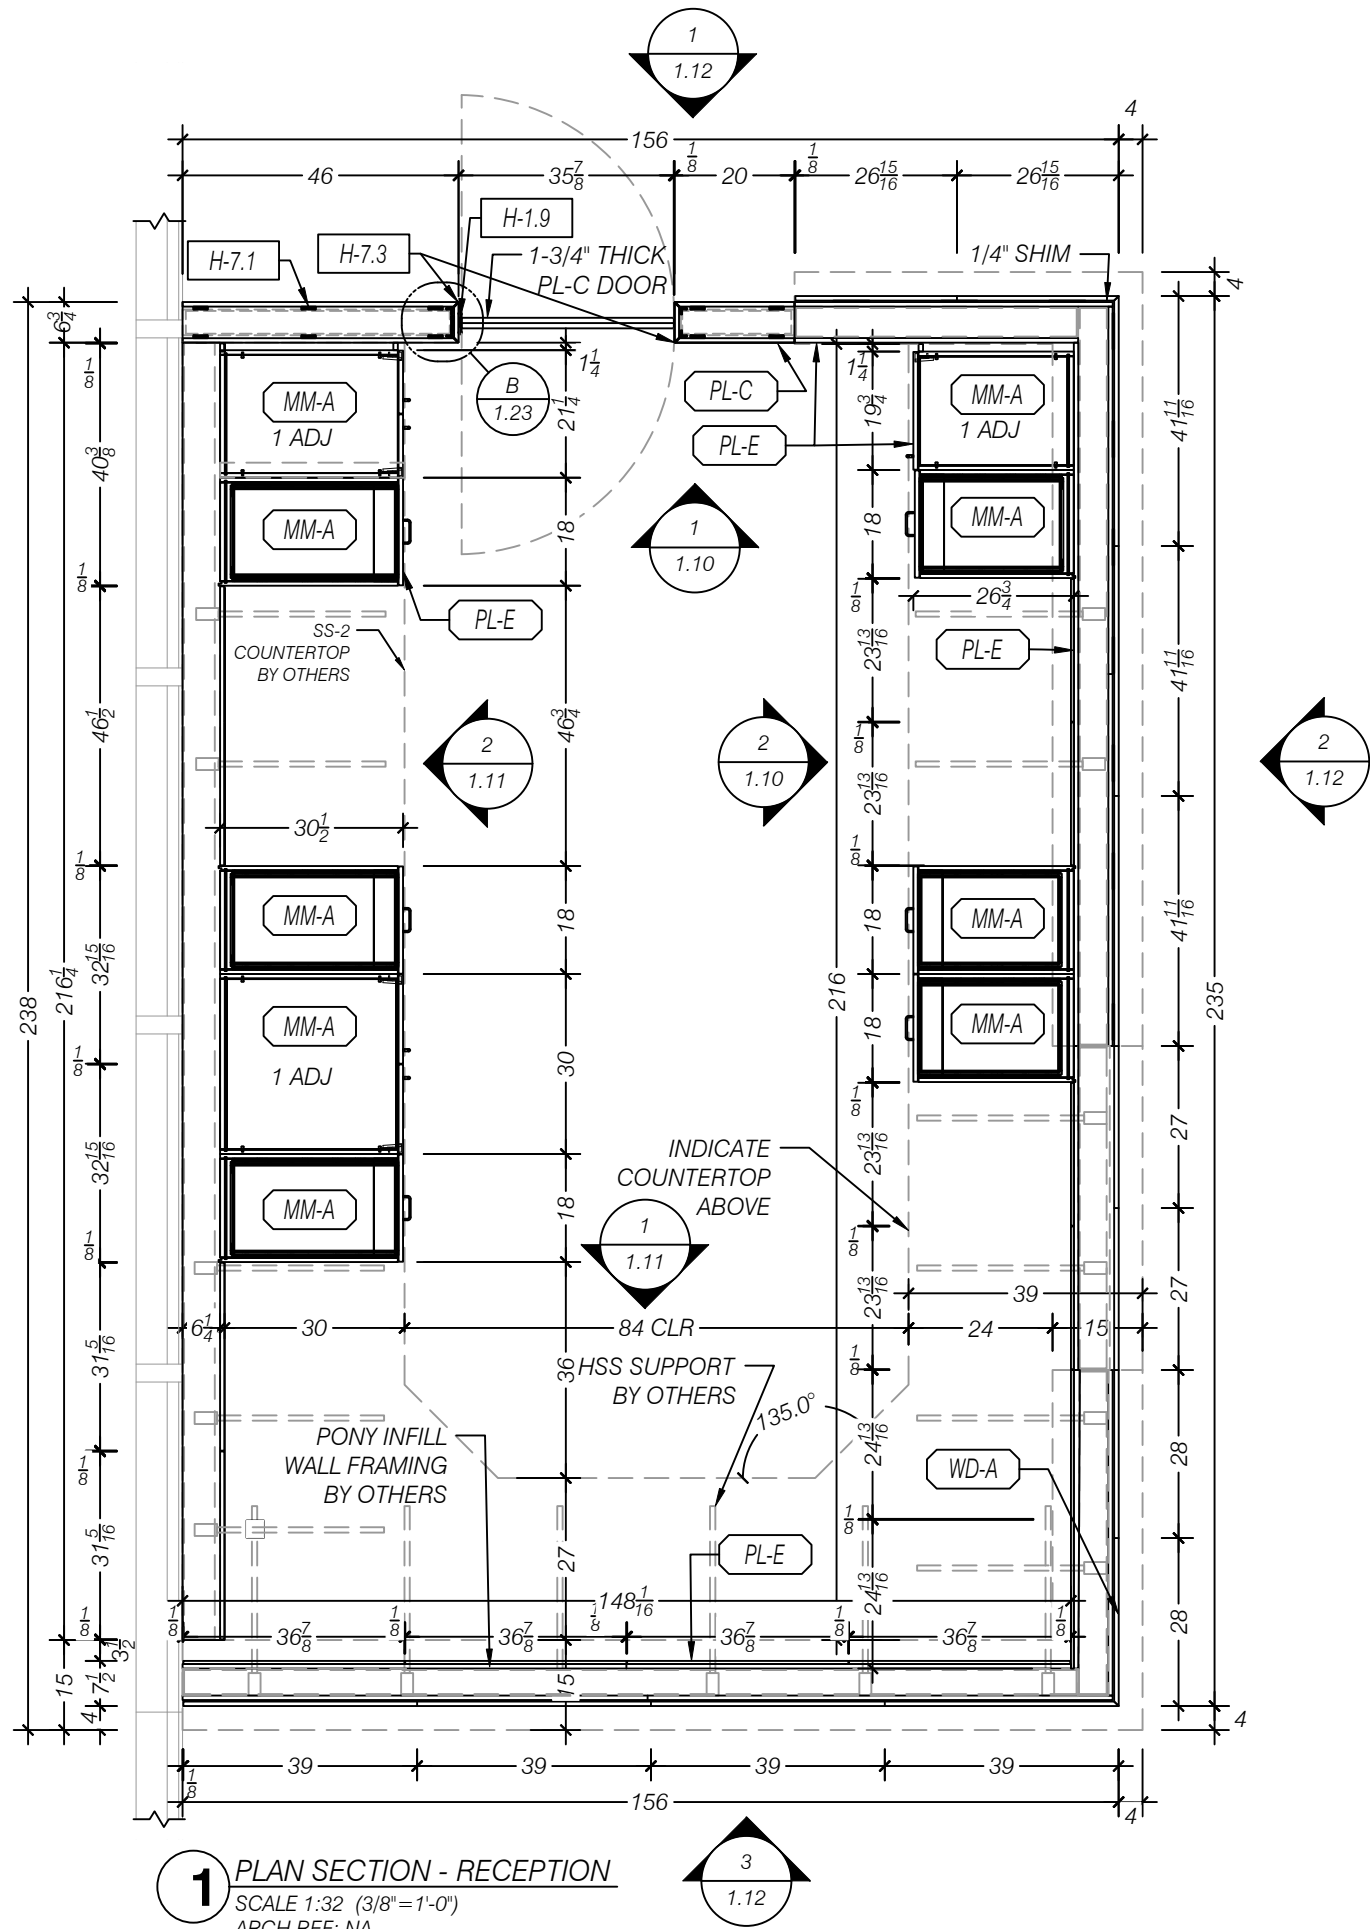


|       |      | MATERIALS                                                                         |
|-------|------|-----------------------------------------------------------------------------------|
| MM-A  |      | WHITE MELAMINE                                                                    |
| PL-C  |      | (PL-1, WB-2) WILSONART "HARVEST MAPLE", 7953-38, FINE VELVET TEXTURE              |
| PL-E  |      | (PL-3) WILSONART "WHITE", 1570-60, FINE VELVET TEXTURE 1570-38                    |
| WD-A  |      | (WD-1) SURFACING SOLUTIONS, MAPLE TAMBOUR HALF ROUND, PROFILE 383, 3/4"W x 5/16"H |
|       | QTY. | HARDWARE                                                                          |
| H-1.2 | X    | SALICE 0mm CLIP-ON HINGE PLATE EURO SCREW, BARGR09/16                             |
| H-1.3 | X    | SALICE 110° FO SOFT-CLOSE, LOGICA SILENTIA, C7J6AE9                               |
| H-1.8 | X    | MC KINNEY DOUBLE ACTING SPRING HINGE, 1001,6",SATIN CHROME FINISH                 |
| H-2.0 | X    | KNAPE & VOGT DRAWER SLIDES, KV8400, SIDE MOUNT, FULL EXT. 100lb LOAD RATING       |
| H-2.1 | X    | KNAPE & VOGT DRAWER SLIDES, KV8600, SIDE MOUNT, FULL EXT. 150lb LOAD RATING       |
| H-3.0 | X    | BERENSON WIRE PULL, BN6131-2SC-P, 96mm CTC, SATIN CHROME FINISH                   |
| H-4.0 | X    | HAFELE SHELF SUPPORT, 282.04.711, 5mm SHELF PIN, STEEL NICKEL-PLATED              |
| H-6.0 | X    | MOCKETT TG FLIP-TOP SERIES DESK GROMMET, 2"Ø, COLOR T.B.D.                        |
| H-7.1 | X    | ORANGE ALUMINUM Z-CLIP HD PANEL RAIL                                              |
| H-7.2 | X    | FRY REGLET MILLWORK REVEAL, 1" PANEL, 1/2" REVEAL, MWRB50P100, POWDER COATED      |
| H-7.3 | X    | EAGLE ALUMINUM 1/8" CORNER ACCENT, MILL FINISH                                    |
| H-7.4 | X    | McMASTER CARR ALUMINUM CHANNEL, 9001K664, 1-3/4"W x 1"H, MILL FINISH              |
| H-8.0 | X    | KEKU CLIP, BLACK FINISH                                                           |

DGS SREOC COSTA

MESA


RECEPTION

| ISSUE        |                                       | BY        |
|--------------|---------------------------------------|-----------|
| DATE         | DESCRIPTION                           | Q-AS      |
| 05/05/2026   | REV-A FOR SUBMITTAL                   | -         |
| -            | -                                     | -         |
| -            | -                                     | -         |
| -            | -                                     | -         |
| -            | -                                     | -         |
| SITE ADDRESS |                                       |           |
| STREET       | 2301 South Shelley Circle BLDG. A & B |           |
| CITY         | Costa Mesa                            |           |
| STATE        | CA                                    | ZIP 92626 |
| JOB #:       | 26034                                 | REV: A    |
| MOD #:       | 1                                     | REL: N/A  |
| 1.9          |                                       |           |

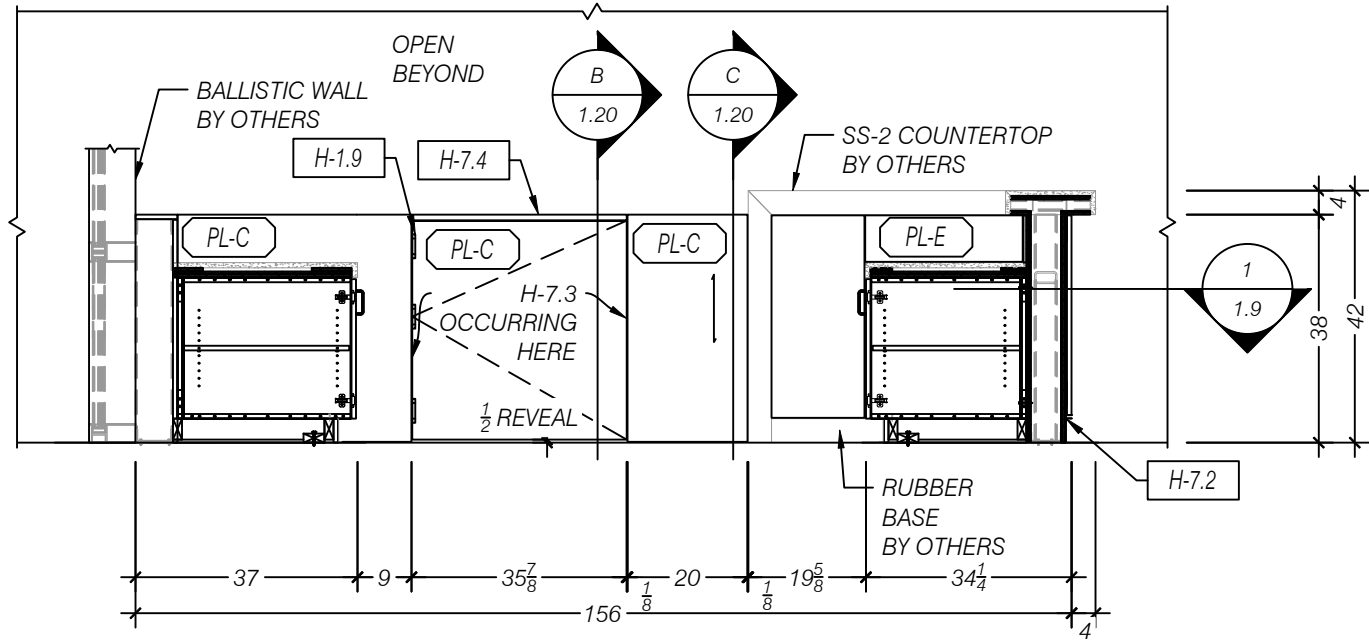

**1** ELEVATION NORTH - RECEPTION  
SCALE 1:24 (1/2"=1'-0")  
ARCH REF: 3/AE580

CENTERLINE OF IN-WALL STRAPPING  
(STRAPPING BY OTHERS)

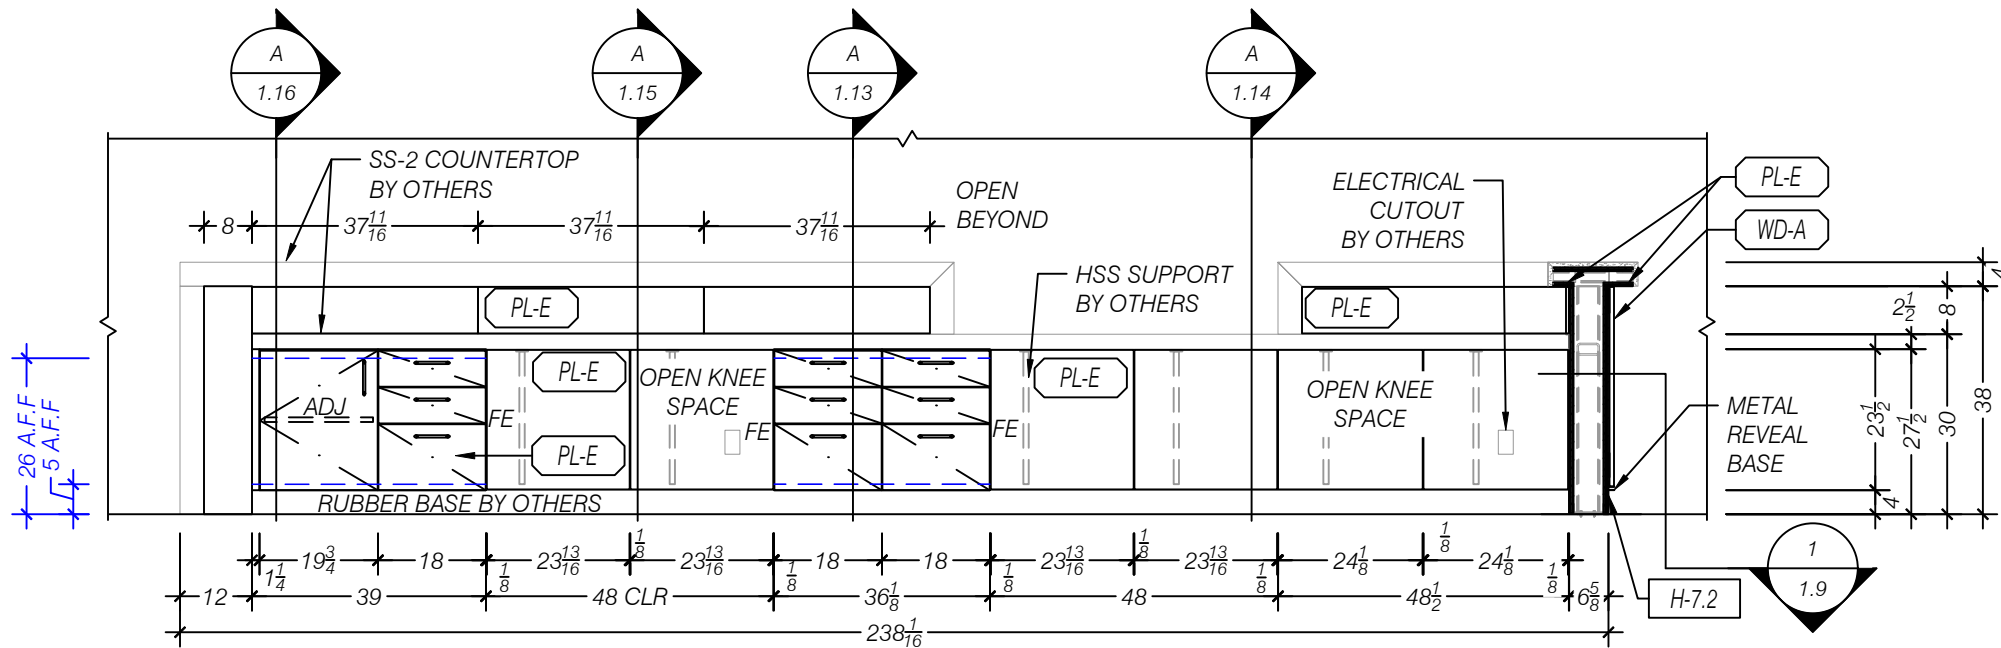


**2** ELEVATION EAST - RECEPTION  
SCALE 1:24 (1/2"=1'-0")  
ARCH REF: 4/AE580

| MATERIALS     |   |                                                                                   |
|---------------|---|-----------------------------------------------------------------------------------|
| (MM-A)        | X | WHITE MELAMINE                                                                    |
| (PL-C)        | X | (PL-1, WB-2) WILSONART "HARVEST MAPLE", 7953-38, FINE VELVET TEXTURE              |
| (PL-E)        | X | (PL-3) WILSONART "WHITE", 1570-60, FINE VELVET TEXTURE 1570-38                    |
| (WD-A)        | X | (WD-1) SURFACING SOLUTIONS, MAPLE TAMBOUR HALF ROUND, PROFILE 383, 3/4"W x 5/16"H |
| QTY. HARDWARE |   |                                                                                   |
| H-1.2         | X | SALICE 0mm CLIP-ON HINGE PLATE EURO SCREW, BARGR09/16                             |
| H-1.3         | X | SALICE 110° FO SOFT-CLOSE, LOGICA SILENTIA, C7J6AE9                               |
| H-1.8         | X | MC KINNEY DOUBLE ACTING SPRING HINGE, 1001,6",SATIN CHROME FINISH                 |
| H-2.0         | X | KNAPE & VOGT DRAWER SLIDES, KV8400, SIDE MOUNT, FULL EXT. 100lb LOAD RATING       |
| H-2.1         | X | KNAPE & VOGT DRAWER SLIDES, KV8600, SIDE MOUNT, FULL EXT. 150lb LOAD RATING       |
| H-3.0         | X | BERENSON WIRE PULL, BN6131-2SC-P, 96mm CTC, SATIN CHROME FINISH                   |
| H-4.0         | X | HAFELE SHELF SUPPORT, 282.04.711, 5mm SHELF PIN, STEEL NICKEL-PLATED              |
| H-6.0         | X | MOCKETT TG FLIP-TOP SERIES DESK GROMMET, 2"Ø, COLOR T.B.D.                        |
| H-7.1         | X | ORANGE ALUMINUM Z-CLIP HD PANEL RAIL                                              |
| H-7.2         | X | FRY REGLET MILLWORK REVEAL, 1" PANEL, 1/2" REVEAL, MWRB50P100, POWDER COATED      |
| H-7.3         | X | EAGLE ALUMINUM 1/8" CORNER ACCENT, MILL FINISH                                    |
| H-7.4         | X | McMASTER CARR ALUMINUM CHANNEL, 9001K664, 1-3/4"W x 1"H, MILL FINISH              |
| H-8.0         | X | KEKU CLIP, BLACK FINISH                                                           |


**DGS SREOC COSTA**  
**MESA**  
**RECEPTION**

| ISSUE        |                                       | BY        |
|--------------|---------------------------------------|-----------|
| DATE         | DESCRIPTION                           | Q-AS      |
| 05/05/2026   | REV-A FOR SUBMITTAL                   | -         |
| -            | -                                     | -         |
| -            | -                                     | -         |
| -            | -                                     | -         |
| -            | -                                     | -         |
| SITE ADDRESS |                                       |           |
| STREET       | 2301 South Shelley Circle BLDG. A & B |           |
| CITY         | Costa Mesa                            |           |
| STATE        | CA                                    | ZIP 92626 |
| JOB #:       | 26034                                 | REV: A    |
| MOD #:       | 1                                     | REL: N/A  |
| <b>1.10</b>  |                                       |           |

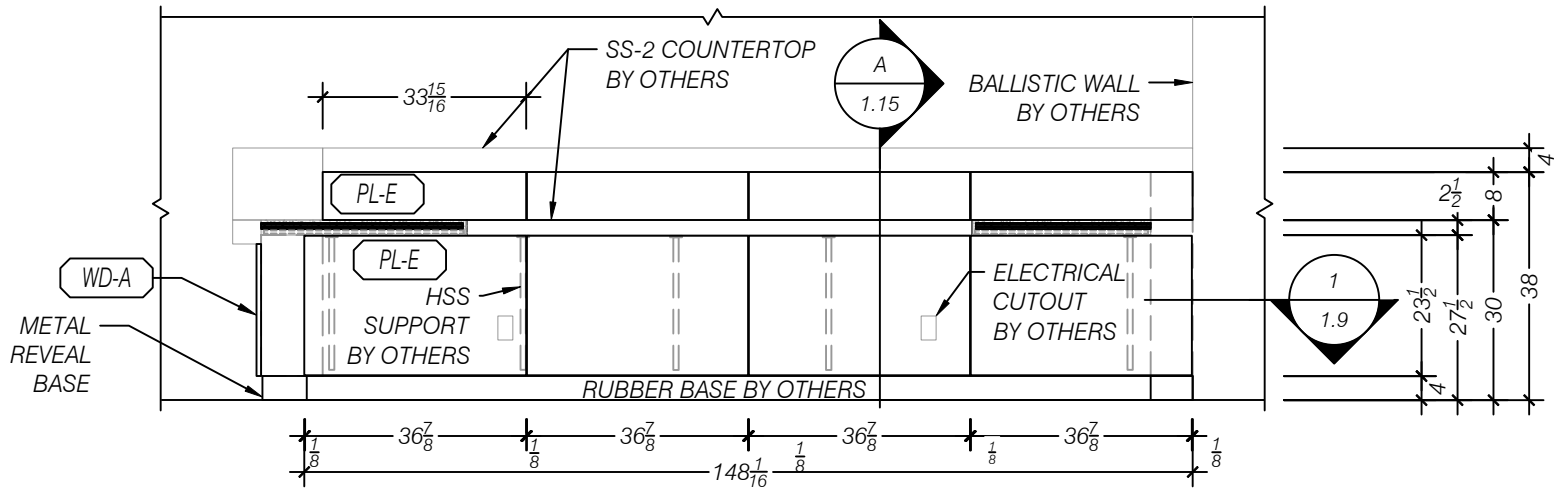

|        |      | MATERIALS                                                                         |
|--------|------|-----------------------------------------------------------------------------------|
| (MM-A) |      | WHITE MELAMINE                                                                    |
| (PL-C) |      | (PL-1, WB-2) WILSONART "HARVEST MAPLE", 7953-38, FINE VELVET TEXTURE              |
| (PL-E) |      | (PL-3) WILSONART "WHITE", 1570-60, FINE VELVET TEXTURE 1570-38                    |
| (WD-A) |      | (WD-1) SURFACING SOLUTIONS, MAPLE TAMBOUR HALF ROUND, PROFILE 383, 3/4"W x 5/16"H |
|        | QTY. | HARDWARE                                                                          |
| H-1.2  | X    | SALICE 0mm CLIP-ON HINGE PLATE EURO SCREW, BARGR09/16                             |
| H-1.3  | X    | SALICE 110° FO SOFT-CLOSE, LOGICA SILENTIA, C7J6AE9                               |
| H-1.8  | X    | MC KINNEY DOUBLE ACTING SPRING HINGE, 1001,6",SATIN CHROME FINISH                 |
| H-2.0  | X    | KNAPE & VOGT DRAWER SLIDES, KV8400, SIDE MOUNT, FULL EXT. 100lb LOAD RATING       |
| H-2.1  | X    | KNAPE & VOGT DRAWER SLIDES, KV8600, SIDE MOUNT, FULL EXT. 150lb LOAD RATING       |
| H-3.0  | X    | BERENSON WIRE PULL, BN6131-2SC-P, 96mm CTC, SATIN CHROME FINISH                   |
| H-4.0  | X    | HAFELE SHELF SUPPORT, 282.04.711, 5mm SHELF PIN, STEEL NICKEL-PLATED              |
| H-6.0  | X    | MOCKETT TG FLIP-TOP SERIES DESK GROMMET, 2"Ø, COLOR T.B.D.                        |
| H-7.1  | X    | ORANGE ALUMINUM Z-CLIP HD PANEL RAIL                                              |
| H-7.2  | X    | FRY REGLET MILLWORK REVEAL, 1" PANEL, 1/2" REVEAL, MWRB50P100, POWDER COATED      |
| H-7.3  | X    | EAGLE ALUMINUM 1/8" CORNER ACCENT, MILL FINISH                                    |
| H-7.4  | X    | McMASTER CARR ALUMINUM CHANNEL, 9001K664, 1-3/4"W x 1"H, MILL FINISH              |
| H-8.0  | X    | KEKU CLIP, BLACK FINISH                                                           |

1 ELEVATION SOUTH - RECEPTION  
SCALE 1:24 (1/2"=1'-0")  
ARCH REF: 5/AE580

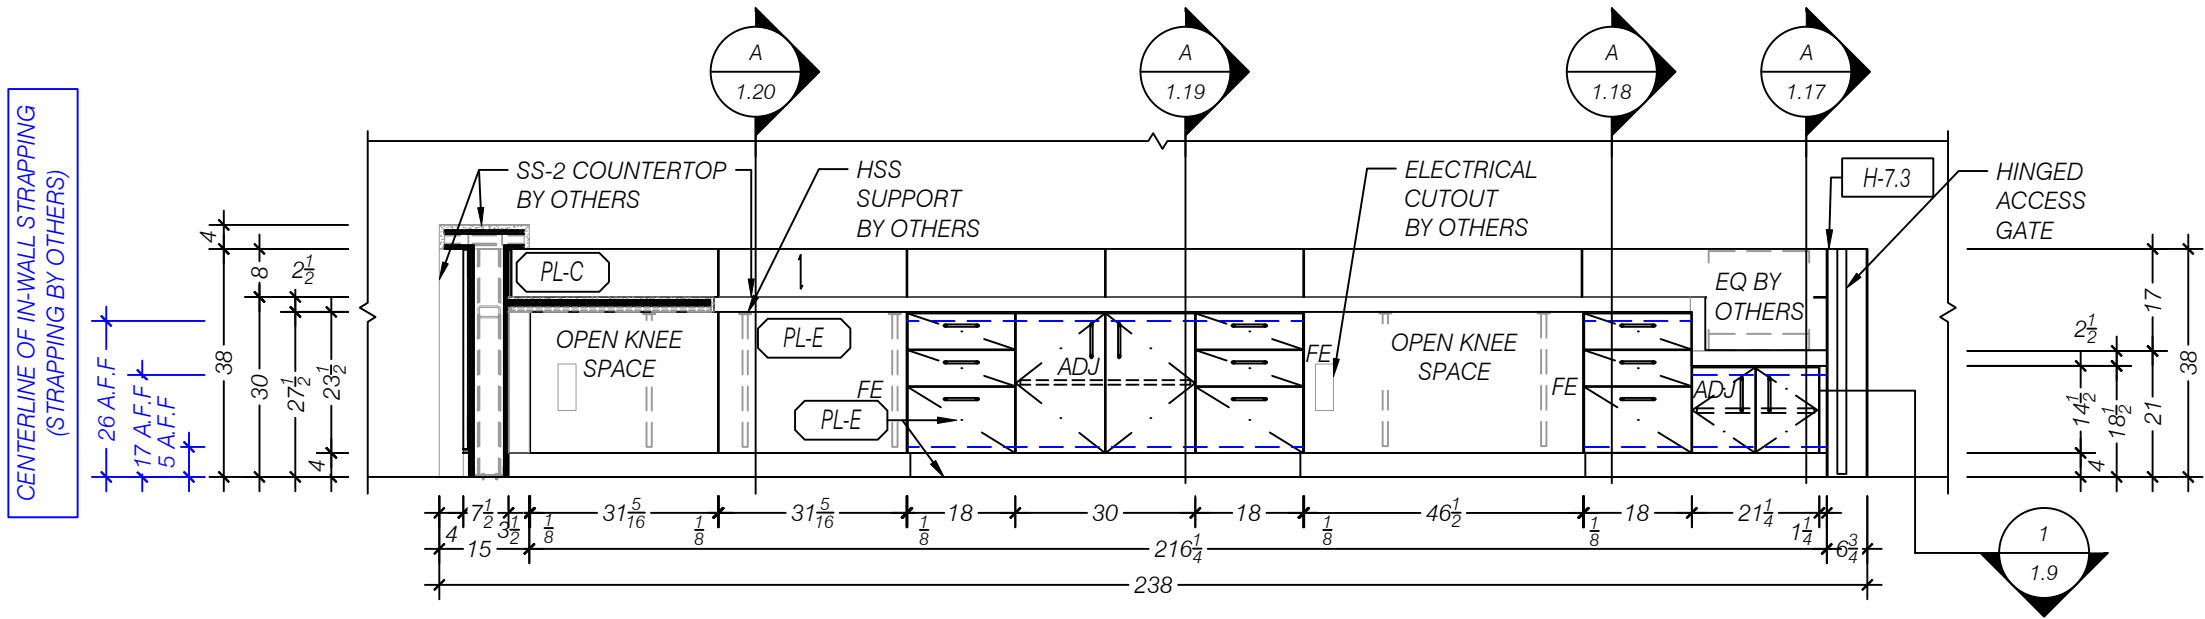


2 ELEVATION WEST- RECEPTION  
SCALE 1:24 (1/2"=1'-0")  
ARCH REF: 2/AE580

DGS SREOC COSTA

MESA


RECEPTION

| ISSUE        |                                       | BY        |
|--------------|---------------------------------------|-----------|
| DATE         | DESCRIPTION                           | Q-AS      |
| 05/05/2026   | REV-A FOR SUBMITTAL                   | -         |
| -            | -                                     | -         |
| -            | -                                     | -         |
| -            | -                                     | -         |
| -            | -                                     | -         |
| SITE ADDRESS |                                       |           |
| STREET       | 2301 South Shelley Circle BLDG. A & B |           |
| CITY         | Costa Mesa                            |           |
| STATE        | CA                                    | ZIP 92626 |
| JOB #:       | 26034                                 | REV: A    |
| MOD #:       | 1                                     | REL: N/A  |
| 1.11         |                                       |           |

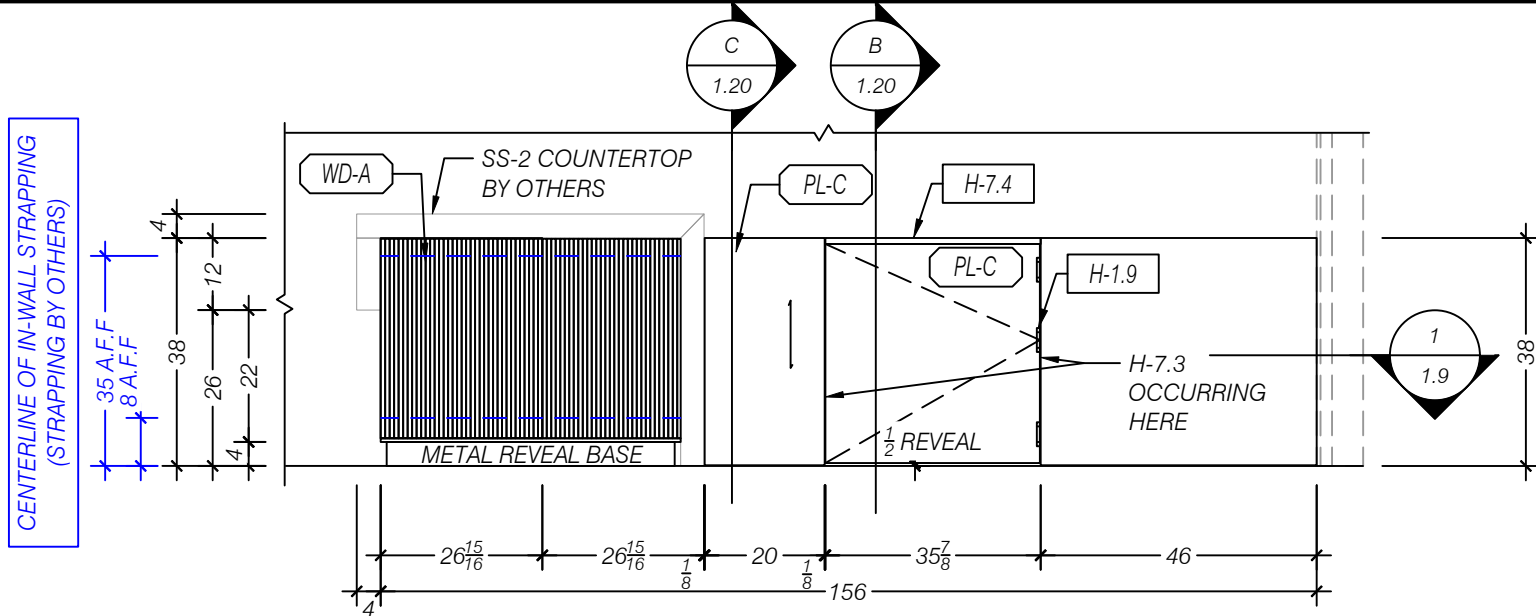


| MATERIALS     |                                                                                   |
|---------------|-----------------------------------------------------------------------------------|
| (MM-A)        | WHITE MELAMINE                                                                    |
| (PL-C)        | (PL-1, WB-2) WILSONART "HARVEST MAPLE", 7953-38, FINE VELVET TEXTURE              |
| (PL-E)        | (PL-3) WILSONART "WHITE", 1570-60, FINE VELVET TEXTURE 1570-38                    |
| (WD-A)        | (WD-1) SURFACING SOLUTIONS, MAPLE TAMBOUR HALF ROUND, PROFILE 383, 3/4"W x 5/16"H |
| QTY. HARDWARE |                                                                                   |
| H-1.2         | X SALICE 0mm CLIP-ON HINGE PLATE EURO SCREW, BARGR09/16                           |
| H-1.3         | X SALICE 110° FO SOFT-CLOSE, LOGICA SILENTIA, C7J6AE9                             |
| H-1.8         | X MC KINNEY DOUBLE ACTING SPRING HINGE, 1001,6",SATIN CHROME FINISH               |
| H-2.0         | X KNAPE & VOGT DRAWER SLIDES, KV8400, SIDE MOUNT, FULL EXT. 100lb LOAD RATING     |
| H-2.1         | X KNAPE & VOGT DRAWER SLIDES, KV8600, SIDE MOUNT, FULL EXT. 150lb LOAD RATING     |
| H-3.0         | X BERENSON WIRE PULL, BN6131-2SC-P, 96mm CTC, SATIN CHROME FINISH                 |
| H-4.0         | X HAFELE SHELF SUPPORT, 282.04.711, 5mm SHELF PIN, STEEL NICKEL-PLATED            |
| H-6.0         | X MOCKETT TG FLIP-TOP SERIES DESK GROMMET, 2"Ø, COLOR T.B.D.                      |
| H-7.1         | X ORANGE ALUMINUM Z-CLIP HD PANEL RAIL                                            |
| H-7.2         | X FRY REGLET MILLWORK REVEAL, 1" PANEL, 1/2" REVEAL, MWRB50P100, POWDER COATED    |
| H-7.3         | X EAGLE ALUMINUM 1/8" CORNER ACCENT, MILL FINISH                                  |
| H-7.4         | X McMASTER CARR ALUMINUM CHANNEL, 9001K664, 1-3/4"W x 1"H, MILL FINISH            |
| H-8.0         | X Keku CLIP, BLACK FINISH                                                         |

**1** ELEVATION NORTH - RECEPTION  
SCALE 1:24 (1/2"=1'-0")  
ARCH REF: 8/AE580

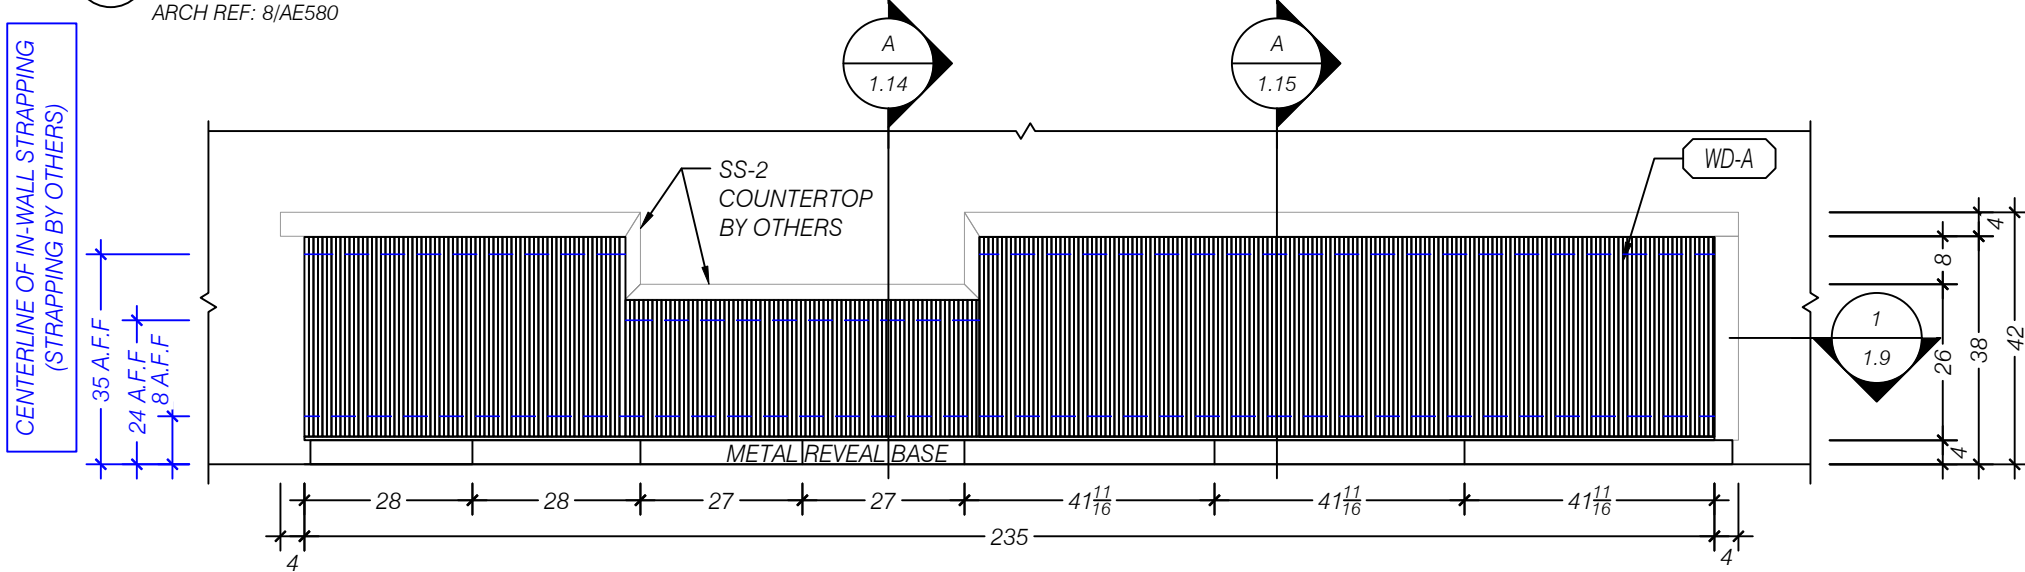


**2** ELEVATION EAST - RECEPTION  
SCALE 1:24 (1/2"=1'-0")  
ARCH REF: 7/AE580

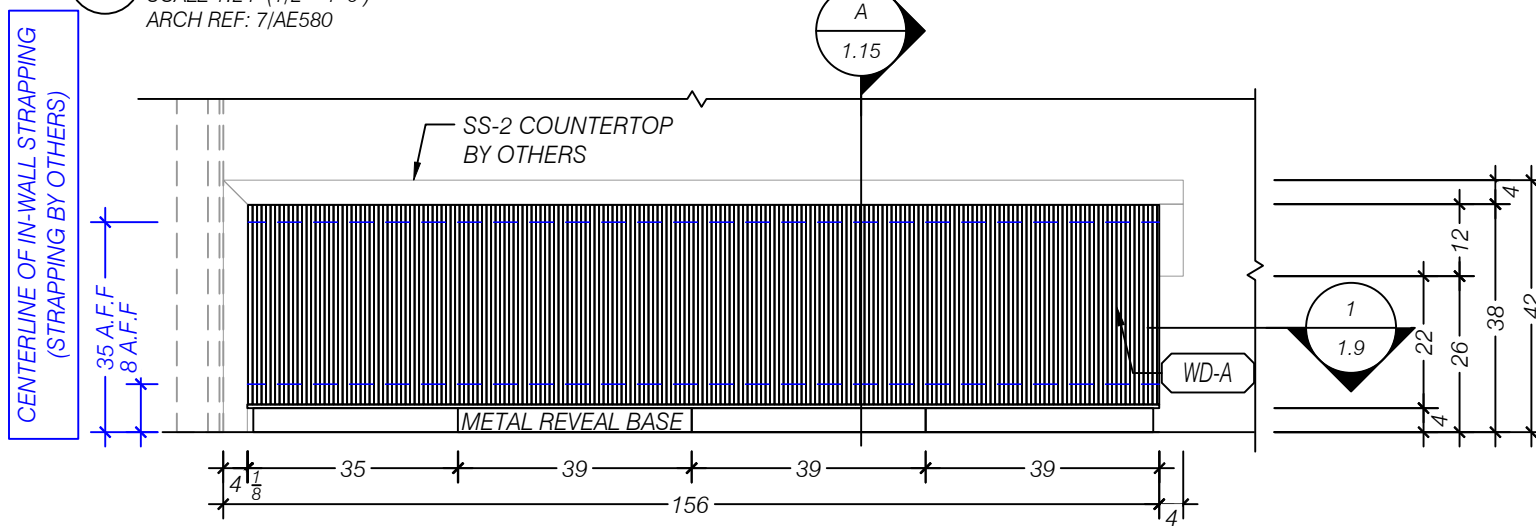

**3** ELEVATION SOUTH - RECEPTION  
SCALE 1:24 (1/2"=1'-0")  
ARCH REF: 6/AE580

**DGS SREOC COSTA**  
**MESA**  
**RECEPTION**

| ISSUE        |                                       | BY        |
|--------------|---------------------------------------|-----------|
| DATE         | DESCRIPTION                           |           |
| 05/05/2026   | REV-A FOR SUBMITTAL                   | Q-AS      |
| -            | -                                     | -         |
| -            | -                                     | -         |
| SITE ADDRESS |                                       |           |
| STREET       | 2301 South Shelley Circle BLDG. A & B |           |
| CITY         | Costa Mesa                            |           |
| STATE        | CA                                    | ZIP 92626 |
| JOB #:       | 26034                                 | REV: A    |
| MOD #:       | 1                                     | REL: N/A  |
| <b>1.12</b>  |                                       |           |

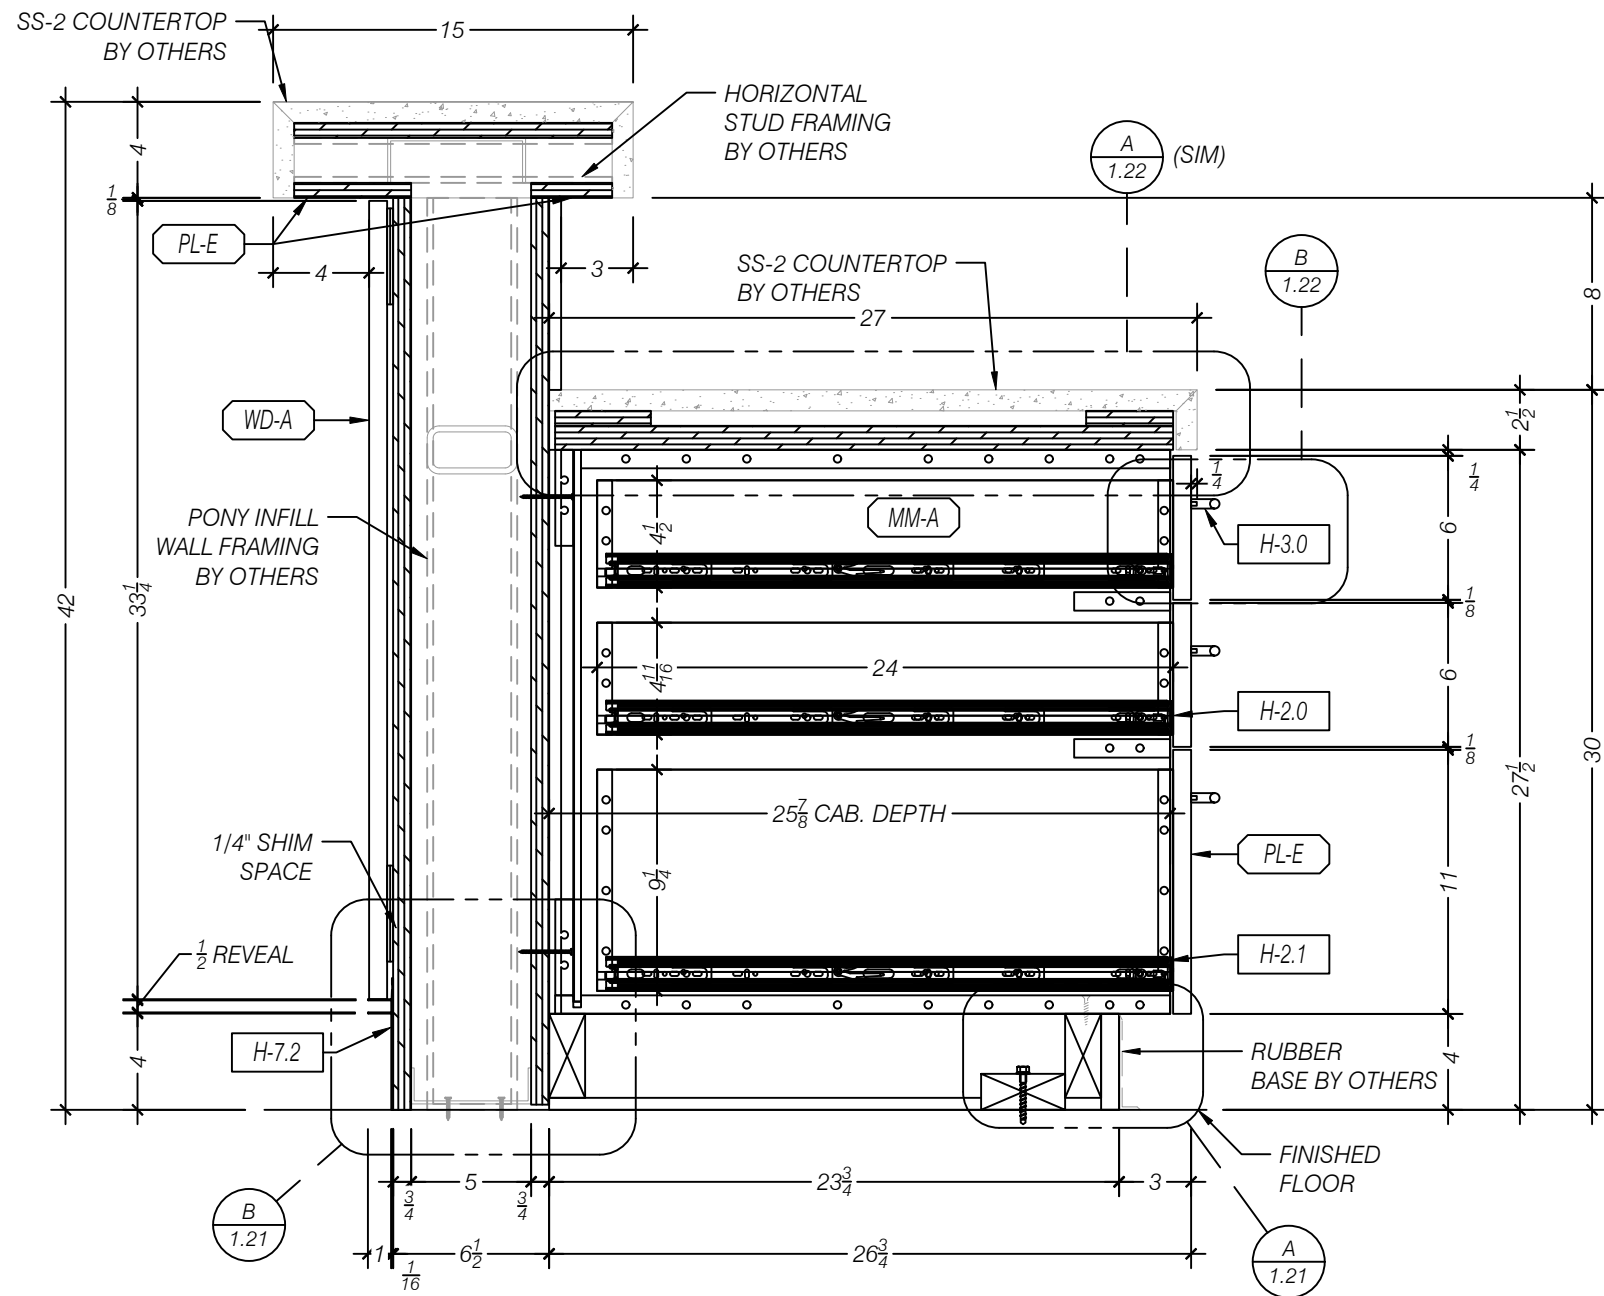


**A** SECTION - 3 DRAWER BASE CABINET w/ TRANSACTION COUNTER  
SCALE 1:8 (1 1/2"=1'-0")  
ARCH REF: 1/AE584

|        |      | MATERIALS                                                                         |
|--------|------|-----------------------------------------------------------------------------------|
| (MM-A) |      | WHITE MELAMINE                                                                    |
| (PL-C) |      | (PL-1, WB-2) WILSONART "HARVEST MAPLE", 7953-38, FINE VELVET TEXTURE              |
| (PL-E) |      | (PL-3) WILSONART "WHITE", 1570-60, FINE VELVET TEXTURE 1570-38                    |
| (WD-A) |      | (WD-1) SURFACING SOLUTIONS, MAPLE TAMBOUR HALF ROUND, PROFILE 383, 3/4"W x 5/16"H |
|        | QTY. | HARDWARE                                                                          |
| H-1.2  | X    | SALICE 0mm CLIP-ON HINGE PLATE EURO SCREW, BARGR09/16                             |
| H-1.3  | X    | SALICE 110° FO SOFT-CLOSE, LOGICA SILENTIA, C7J6AE9                               |
| H-1.8  | X    | MC KINNEY DOUBLE ACTING SPRING HINGE, 1001,6",SATIN CHROME FINISH                 |
| H-2.0  | X    | KNAPE & VOGT DRAWER SLIDES, KV8400, SIDE MOUNT, FULL EXT. 100lb LOAD RATING       |
| H-2.1  | X    | KNAPE & VOGT DRAWER SLIDES, KV8600, SIDE MOUNT, FULL EXT. 150lb LOAD RATING       |
| H-3.0  | X    | BERENSON WIRE PULL, BN6131-2SC-P, 96mm CTC, SATIN CHROME FINISH                   |
| H-4.0  | X    | HAFELE SHELF SUPPORT, 282.04.711, 5mm SHELF PIN, STEEL NICKEL-PLATED              |
| H-6.0  | X    | MOCKETT TG FLIP-TOP SERIES DESK GROMMET, 2"Ø, COLOR T.B.D.                        |
| H-7.1  | X    | ORANGE ALUMINUM Z-CLIP HD PANEL RAIL                                              |
| H-7.2  | X    | FRY REGLET MILLWORK REVEAL, 1" PANEL, 1/2" REVEAL, MWRB50P100, POWDER COATED      |
| H-7.3  | X    | EAGLE ALUMINUM 1/8" CORNER ACCENT, MILL FINISH                                    |
| H-7.4  | X    | McMASTER CARR ALUMINUM CHANNEL, 9001K664, 1-3/4"W x 1"H, MILL FINISH              |
| H-8.0  | X    | KEKU CLIP, BLACK FINISH                                                           |

**DGS SREOC COSTA**  
**MESA**  
**RECEPTION**

| ISSUE      |                     | BY   |
|------------|---------------------|------|
| DATE       | DESCRIPTION         |      |
| 05/05/2026 | REV-A FOR SUBMITTAL | Q-AS |
| -          | -                   | -    |
| -          | -                   | -    |
| -          | -                   | -    |
| -          | -                   | -    |

| SITE ADDRESS |                                       |      |       |
|--------------|---------------------------------------|------|-------|
| STREET       | 2301 South Shelley Circle BLDG. A & B |      |       |
| CITY         | Costa Mesa                            |      |       |
| STATE        | CA                                    | ZIP  | 92626 |
| JOB #:       | 26034                                 | REV: | A     |
| MOD #:       | 1                                     | REL: | N/A   |

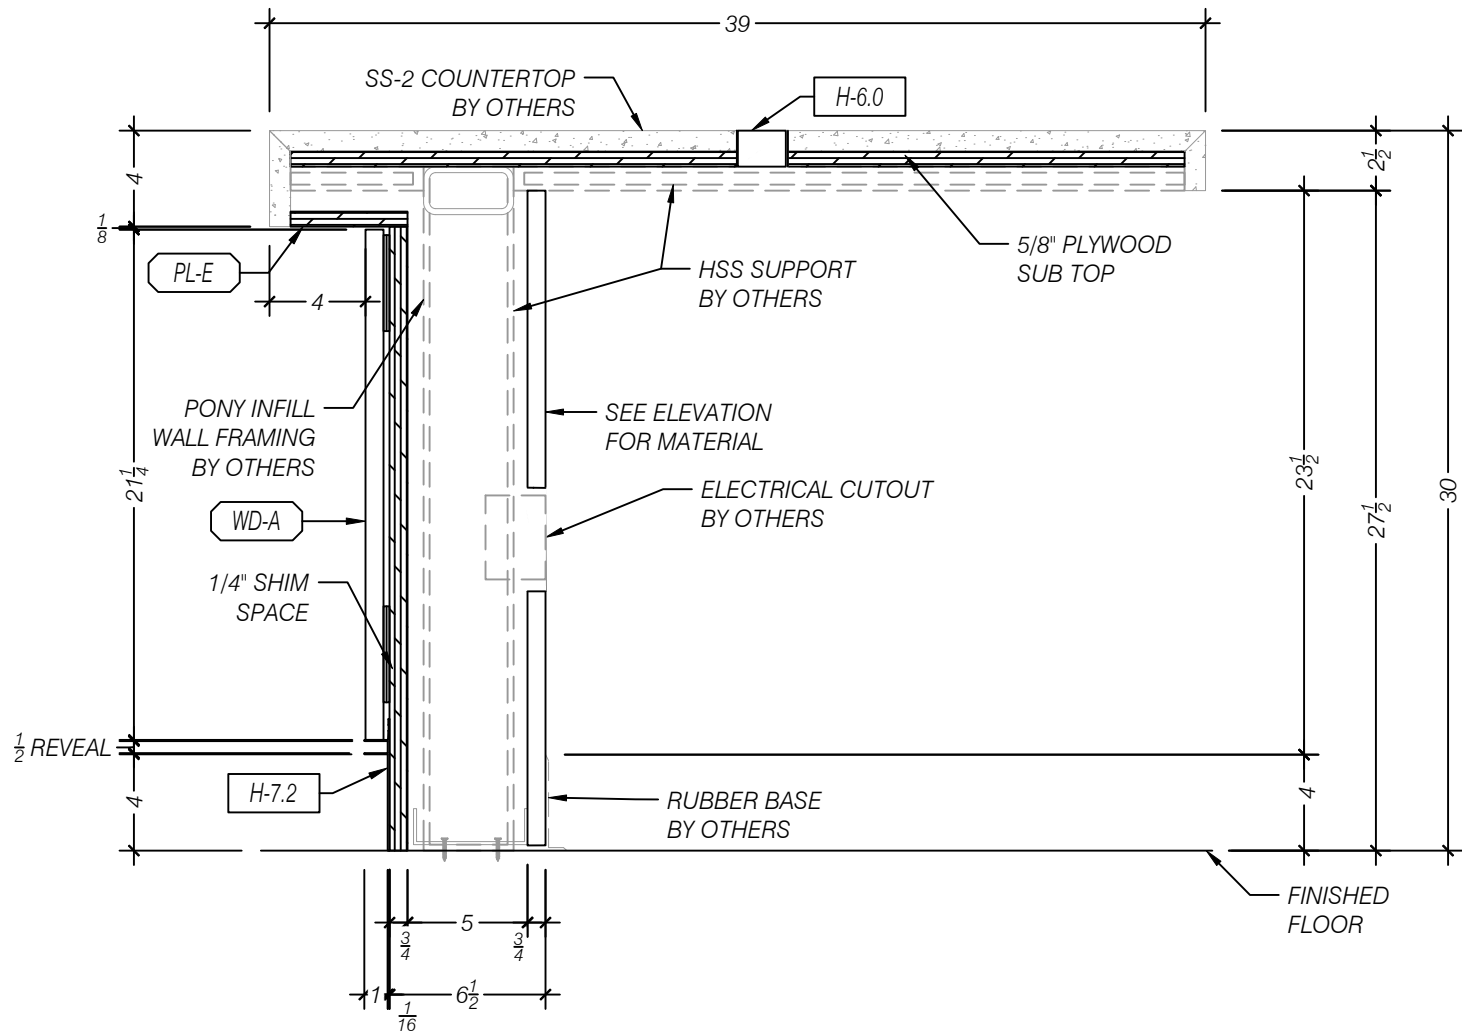

**A** SECTION - COUNTERTOP w/ TRANSACTION COUNTER  
SCALE 1:8 (1 1/2"=1'-0")  
ARCH REF: 2/AE584


|        |      | MATERIALS                                                                         |
|--------|------|-----------------------------------------------------------------------------------|
| (MM-A) |      | WHITE MELAMINE                                                                    |
| (PL-C) |      | (PL-1, WB-2) WILSONART "HARVEST MAPLE", 7953-38, FINE VELVET TEXTURE              |
| (PL-E) |      | (PL-3) WILSONART "WHITE", 1570-60, FINE VELVET TEXTURE 1570-38                    |
| (WD-A) |      | (WD-1) SURFACING SOLUTIONS, MAPLE TAMBOUR HALF ROUND, PROFILE 383, 3/4"W x 5/16"H |
|        | QTY. | HARDWARE                                                                          |
| H-1.2  | X    | SALICE 0mm CLIP-ON HINGE PLATE EURO SCREW, BARGR09/16                             |
| H-1.3  | X    | SALICE 110° FO SOFT-CLOSE, LOGICA SILENTIA, C7J6AE9                               |
| H-1.8  | X    | MC KINNEY DOUBLE ACTING SPRING HINGE, 1001,6",SATIN CHROME FINISH                 |
| H-2.0  | X    | KNAPE & VOGT DRAWER SLIDES, KV8400, SIDE MOUNT, FULL EXT. 100lb LOAD RATING       |
| H-2.1  | X    | KNAPE & VOGT DRAWER SLIDES, KV8600, SIDE MOUNT, FULL EXT. 150lb LOAD RATING       |
| H-3.0  | X    | BERENSON WIRE PULL, BN6131-2SC-P, 96mm CTC, SATIN CHROME FINISH                   |
| H-4.0  | X    | HAFELE SHELF SUPPORT, 282.04.711, 5mm SHELF PIN, STEEL NICKEL-PLATED              |
| H-6.0  | X    | MOCKETT TG FLIP-TOP SERIES DESK GROMMET, 2"Ø, COLOR T.B.D.                        |
| H-7.1  | X    | ORANGE ALUMINUM Z-CLIP HD PANEL RAIL                                              |
| H-7.2  | X    | FRY REGLET MILLWORK REVEAL, 1" PANEL, 1/2" REVEAL, MWRB50P100, POWDER COATED      |
| H-7.3  | X    | EAGLE ALUMINUM 1/8" CORNER ACCENT, MILL FINISH                                    |
| H-7.4  | X    | McMASTER CARR ALUMINUM CHANNEL, 9001K664, 1-3/4"W x 1"H, MILL FINISH              |
| H-8.0  | X    | KEKU CLIP, BLACK FINISH                                                           |

DGS SREOC COSTA

MESA

RECEPTION

| ISSUE        |                                       |      | BY    |
|--------------|---------------------------------------|------|-------|
| DATE         | DESCRIPTION                           |      | Q-AS  |
| 05/05/2026   | REV-A FOR SUBMITTAL                   | -    | -     |
| -            | -                                     | -    | -     |
| -            | -                                     | -    | -     |
| -            | -                                     | -    | -     |
| -            | -                                     | -    | -     |
| SITE ADDRESS |                                       |      |       |
| STREET       | 2301 South Shelley Circle BLDG. A & B |      |       |
| CITY         | Costa Mesa                            |      |       |
| STATE        | CA                                    | ZIP  | 92626 |
| JOB #:       | 26034                                 | REV: | A     |
| MOD #:       | 1                                     | REL: | N/A   |
| 1.14         |                                       |      |       |

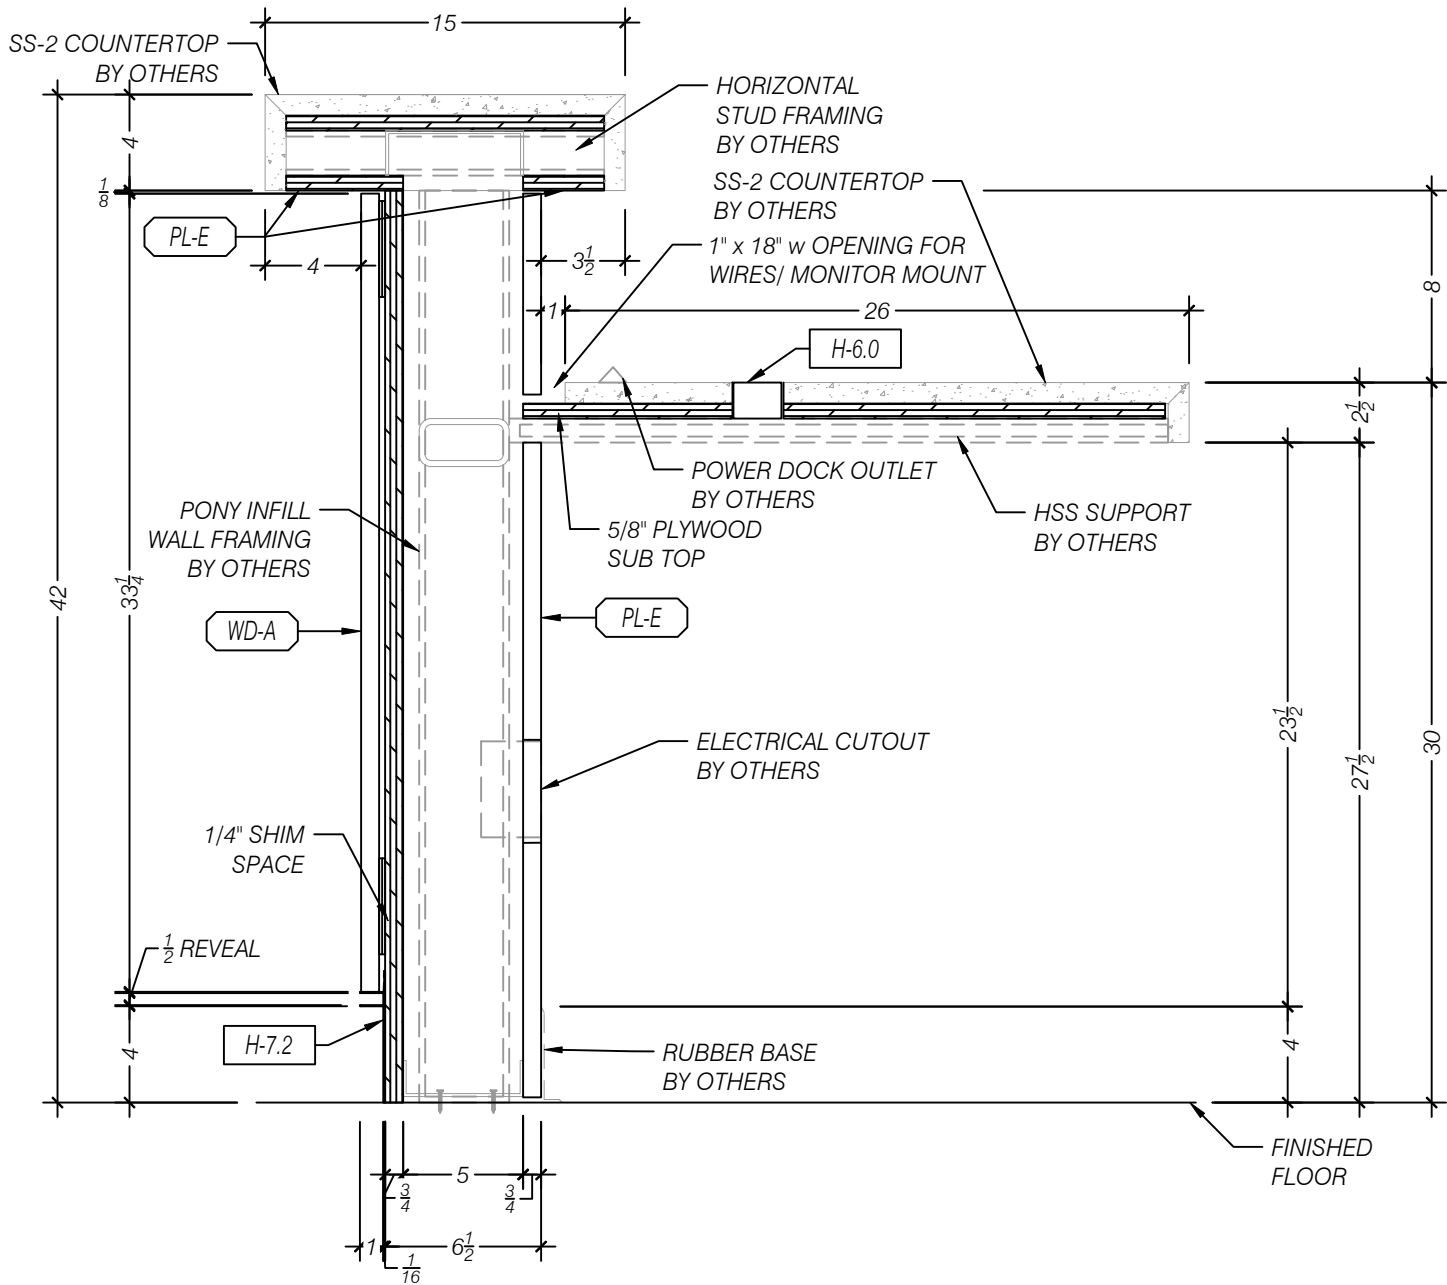

**A** SECTION - COUNTERTOP w/ TRANSACTION COUNTER  
SCALE 1:8 (1 1/2"=1'-0")  
ARCH REF: 3/AE584

| MATERIALS     |   |                                                                                   |
|---------------|---|-----------------------------------------------------------------------------------|
| (MM-A)        | X | WHITE MELAMINE                                                                    |
| (PL-C)        | X | (PL-1, WB-2) WILSONART "HARVEST MAPLE", 7953-38, FINE VELVET TEXTURE              |
| (PL-E)        | X | (PL-3) WILSONART "WHITE", 1570-60, FINE VELVET TEXTURE 1570-38                    |
| (WD-A)        | X | (WD-1) SURFACING SOLUTIONS, MAPLE TAMBOUR HALF ROUND, PROFILE 383, 3/4"W x 5/16"H |
| QTY. HARDWARE |   |                                                                                   |
| H-1.2         | X | SALICE 0mm CLIP-ON HINGE PLATE EURO SCREW, BARGR09/16                             |
| H-1.3         | X | SALICE 110° FO SOFT-CLOSE, LOGICA SILENTIA, C7J6AE9                               |
| H-1.8         | X | MC KINNEY DOUBLE ACTING SPRING HINGE, 1001,6",SATIN CHROME FINISH                 |
| H-2.0         | X | KNAPE & VOGT DRAWER SLIDES, KV8400, SIDE MOUNT, FULL EXT. 100lb LOAD RATING       |
| H-2.1         | X | KNAPE & VOGT DRAWER SLIDES, KV8600, SIDE MOUNT, FULL EXT. 150lb LOAD RATING       |
| H-3.0         | X | BERENSON WIRE PULL, BN6131-2SC-P, 96mm CTC, SATIN CHROME FINISH                   |
| H-4.0         | X | HAFELE SHELF SUPPORT, 282.04.711, 5mm SHELF PIN, STEEL NICKEL-PLATED              |
| H-6.0         | X | MOCKETT TG FLIP-TOP SERIES DESK GROMMET, 2"Ø, COLOR T.B.D.                        |
| H-7.1         | X | ORANGE ALUMINUM Z-CLIP HD PANEL RAIL                                              |
| H-7.2         | X | FRY REGLET MILLWORK REVEAL, 1" PANEL, 1/2" REVEAL, MWRB50P100, POWDER COATED      |
| H-7.3         | X | EAGLE ALUMINUM 1/8" CORNER ACCENT, MILL FINISH                                    |
| H-7.4         | X | McMASTER CARR ALUMINUM CHANNEL, 9001K664, 1-3/4"W x 1"H, MILL FINISH              |
| H-8.0         | X | KEKU CLIP, BLACK FINISH                                                           |




**CRESTMARK**  
MILLWORK

5640 WEST END ROAD  
ARCATA, CA 95521  
PH (707) 822-4034 FAX (707) 822-5478  
WWW.CRESTMARKMILLWORK.COM

**DGS SREOC COSTA**  
**MESA**  
**RECEPTION**

| ISSUE        |                                       |      |       |
|--------------|---------------------------------------|------|-------|
| DATE         | DESCRIPTION                           | BY   |       |
| 05/05/2026   | REV-A FOR SUBMITTAL                   | Q-AS |       |
|              |                                       |      |       |
|              |                                       |      |       |
|              |                                       |      |       |
|              |                                       |      |       |
| SITE ADDRESS |                                       |      |       |
| STREET       | 2301 South Shelley Circle BLDG. A & B |      |       |
| CITY         | Costa Mesa                            |      |       |
| STATE        | CA                                    | ZIP  | 92626 |
| JOB #:       | 26034                                 | REV: | A     |
| MOD #:       | 1                                     | REL: | N/A   |
| 1.15         |                                       |      |       |

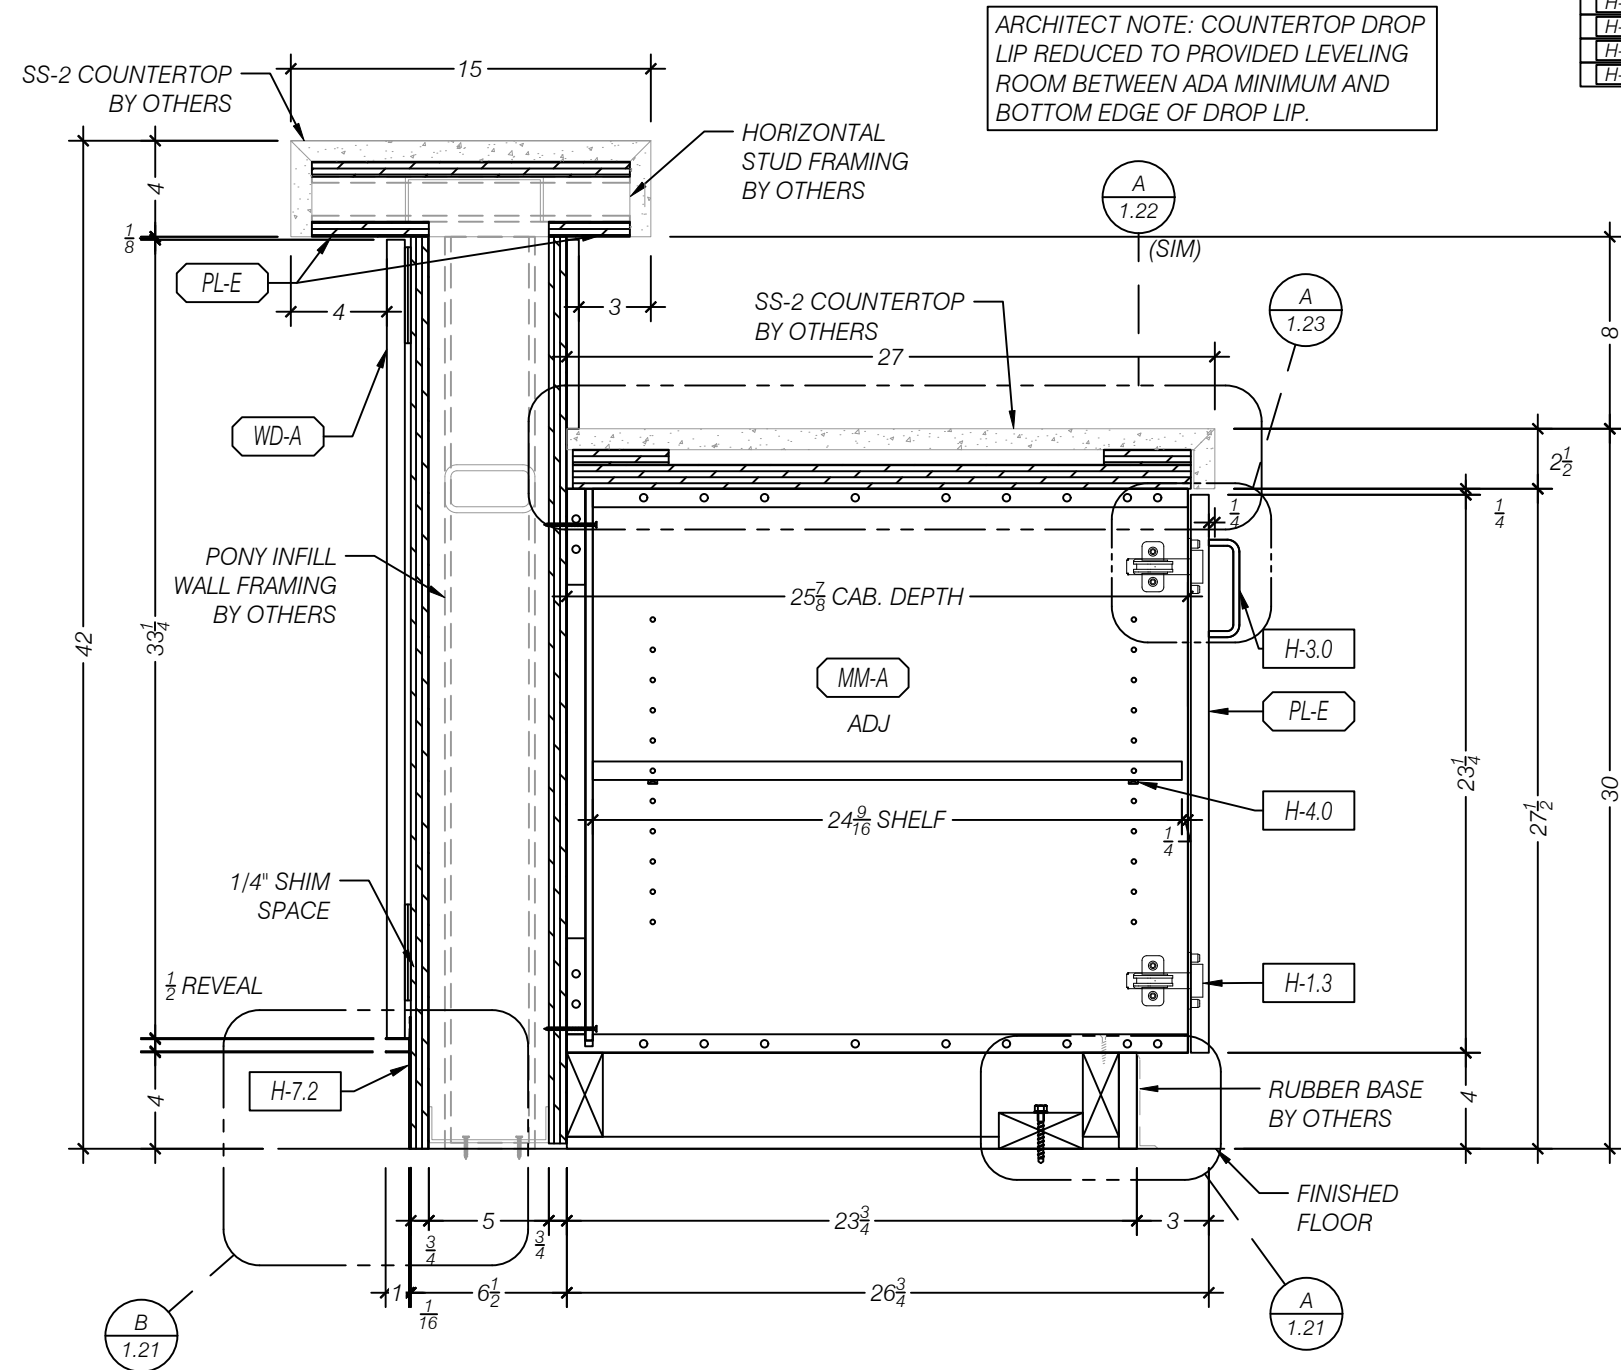

**A** SECTION - BASE CABINET w/ TRANSACTION COUNTER  
SCALE 1:8 (1 1/2"=1'-0")  
ARCH REF: 4/AE584


| MATERIALS     |                                                                                   |
|---------------|-----------------------------------------------------------------------------------|
| (MM-A)        | WHITE MELAMINE                                                                    |
| (PL-C)        | (PL-1, WB-2) WILSONART "HARVEST MAPLE", 7953-38, FINE VELVET TEXTURE              |
| (PL-E)        | (PL-3) WILSONART "WHITE", 1570-60, FINE VELVET TEXTURE 1570-38                    |
| (WD-A)        | (WD-1) SURFACING SOLUTIONS, MAPLE TAMBOUR HALF ROUND, PROFILE 383, 3/4"W x 5/16"H |
| QTY. HARDWARE |                                                                                   |
| H-1.2         | X SALICE 0mm CLIP-ON HINGE PLATE EURO SCREW, BARGR09/16                           |
| H-1.3         | X SALICE 110° FO SOFT-CLOSE, LOGICA SILENTIA, C7J6AE9                             |
| H-1.8         | X MC KINNEY DOUBLE ACTING SPRING HINGE, 1001,6",SATIN CHROME FINISH               |
| H-2.0         | X KNAPE & VOGT DRAWER SLIDES, KV8400, SIDE MOUNT, FULL EXT. 100lb LOAD RATING     |
| H-2.1         | X KNAPE & VOGT DRAWER SLIDES, KV8600, SIDE MOUNT, FULL EXT. 150lb LOAD RATING     |
| H-3.0         | X BERENSON WIRE PULL, BN6131-2SC-P, 96mm CTC, SATIN CHROME FINISH                 |
| H-4.0         | X HAFELE SHELF SUPPORT, 282.04.711, 5mm SHELF PIN, STEEL NICKEL-PLATED            |
| H-6.0         | X MOCKETT TG FLIP-TOP SERIES DESK GROMMET, 2"Ø, COLOR T.B.D.                      |
| H-7.1         | X ORANGE ALUMINUM Z-CLIP HD PANEL RAIL                                            |
| H-7.2         | X FRY REGLET MILLWORK REVEAL, 1" PANEL, 1/2" REVEAL, MWRB50P100, POWDER COATED    |
| H-7.3         | X EAGLE ALUMINUM 1/8" CORNER ACCENT, MILL FINISH                                  |
| H-7.4         | X McMASTER CARR ALUMINUM CHANNEL, 9001K664, 1-3/4"W x 1"H, MILL FINISH            |
| H-8.0         | X KEKU CLIP, BLACK FINISH                                                         |

**DGS SREOC COSTA**  
**MESA**  
**RECEPTION**

| ISSUE      |                     | BY   |
|------------|---------------------|------|
| DATE       | DESCRIPTION         | Q-AS |
| 05/05/2026 | REV-A FOR SUBMITTAL | -    |
| -          | -                   | -    |
| -          | -                   | -    |
| -          | -                   | -    |
| -          | -                   | -    |

| SITE ADDRESS |                                       |      |       |
|--------------|---------------------------------------|------|-------|
| STREET       | 2301 South Shelley Circle BLDG. A & B |      |       |
| CITY         | Costa Mesa                            |      |       |
| STATE        | CA                                    | ZIP  | 92626 |
| JOB #:       | 26034                                 | REV: | A     |
| MOD #:       | 1                                     | REL: | N/A   |

|        |   |                                                                                   |
|--------|---|-----------------------------------------------------------------------------------|
|        |   | MATERIALS                                                                         |
| (MM-A) |   | WHITE MELAMINE                                                                    |
| (PL-C) |   | (PL-1, WB-2) WILSONART "HARVEST MAPLE", 7953-38, FINE VELVET TEXTURE              |
| (PL-E) |   | (PL-3) WILSONART "WHITE", 1570-60, FINE VELVET TEXTURE 1570-38                    |
| (WD-A) |   | (WD-1) SURFACING SOLUTIONS, MAPLE TAMBOUR HALF ROUND, PROFILE 383, 3/4"W x 5/16"H |
|        |   | QTY.    HARDWARE                                                                  |
| H-1.2  | X | SALICE 0mm CLIP-ON HINGE PLATE EURO SCREW, BARGR09/16                             |
| H-1.3  | X | SALICE 110° FO SOFT-CLOSE, LOGICA SILENTIA, C7J6AE9                               |
| H-1.8  | X | MC KINNEY DOUBLE ACTING SPRING HINGE, 1001,6", SATIN CHROME FINISH                |
| H-2.0  | X | KNAPE & VOGT DRAWER SLIDES, KV8400, SIDE MOUNT, FULL EXT. 100lb LOAD RATING       |
| H-2.1  | X | KNAPE & VOGT DRAWER SLIDES, KV8600, SIDE MOUNT, FULL EXT. 150lb LOAD RATING       |
| H-3.0  | X | BERENSON WIRE PULL, BN6131-2SC-P, 96mm CTC, SATIN CHROME FINISH                   |
| H-4.0  | X | HAFELE SHELF SUPPORT, 282.04.711, 5mm SHELF PIN, STEEL NICKEL-PLATED              |
| H-6.0  | X | MOCKETT TG FLIP-TOP SERIES DESK GROMMET, 2"Ø, COLOR T.B.D.                        |
| H-7.1  | X | ORANGE ALUMINUM Z-CLIP HD PANEL RAIL                                              |
| H-7.2  | X | FRY REGLET MILLWORK REVEAL, 1" PANEL, 1/2" REVEAL, MWRB50P100, POWDER COATED      |
| H-7.3  | X | EAGLE ALUMINUM 1/8" CORNER ACCENT, MILL FINISH                                    |
| H-7.4  | X | McMASTER CARR ALUMINUM CHANNEL, 9001K664, 1-3/4"W x 1"H, MILL FINISH              |
| H-8.0  | X | KEKU CLIP, BLACK FINISH                                                           |

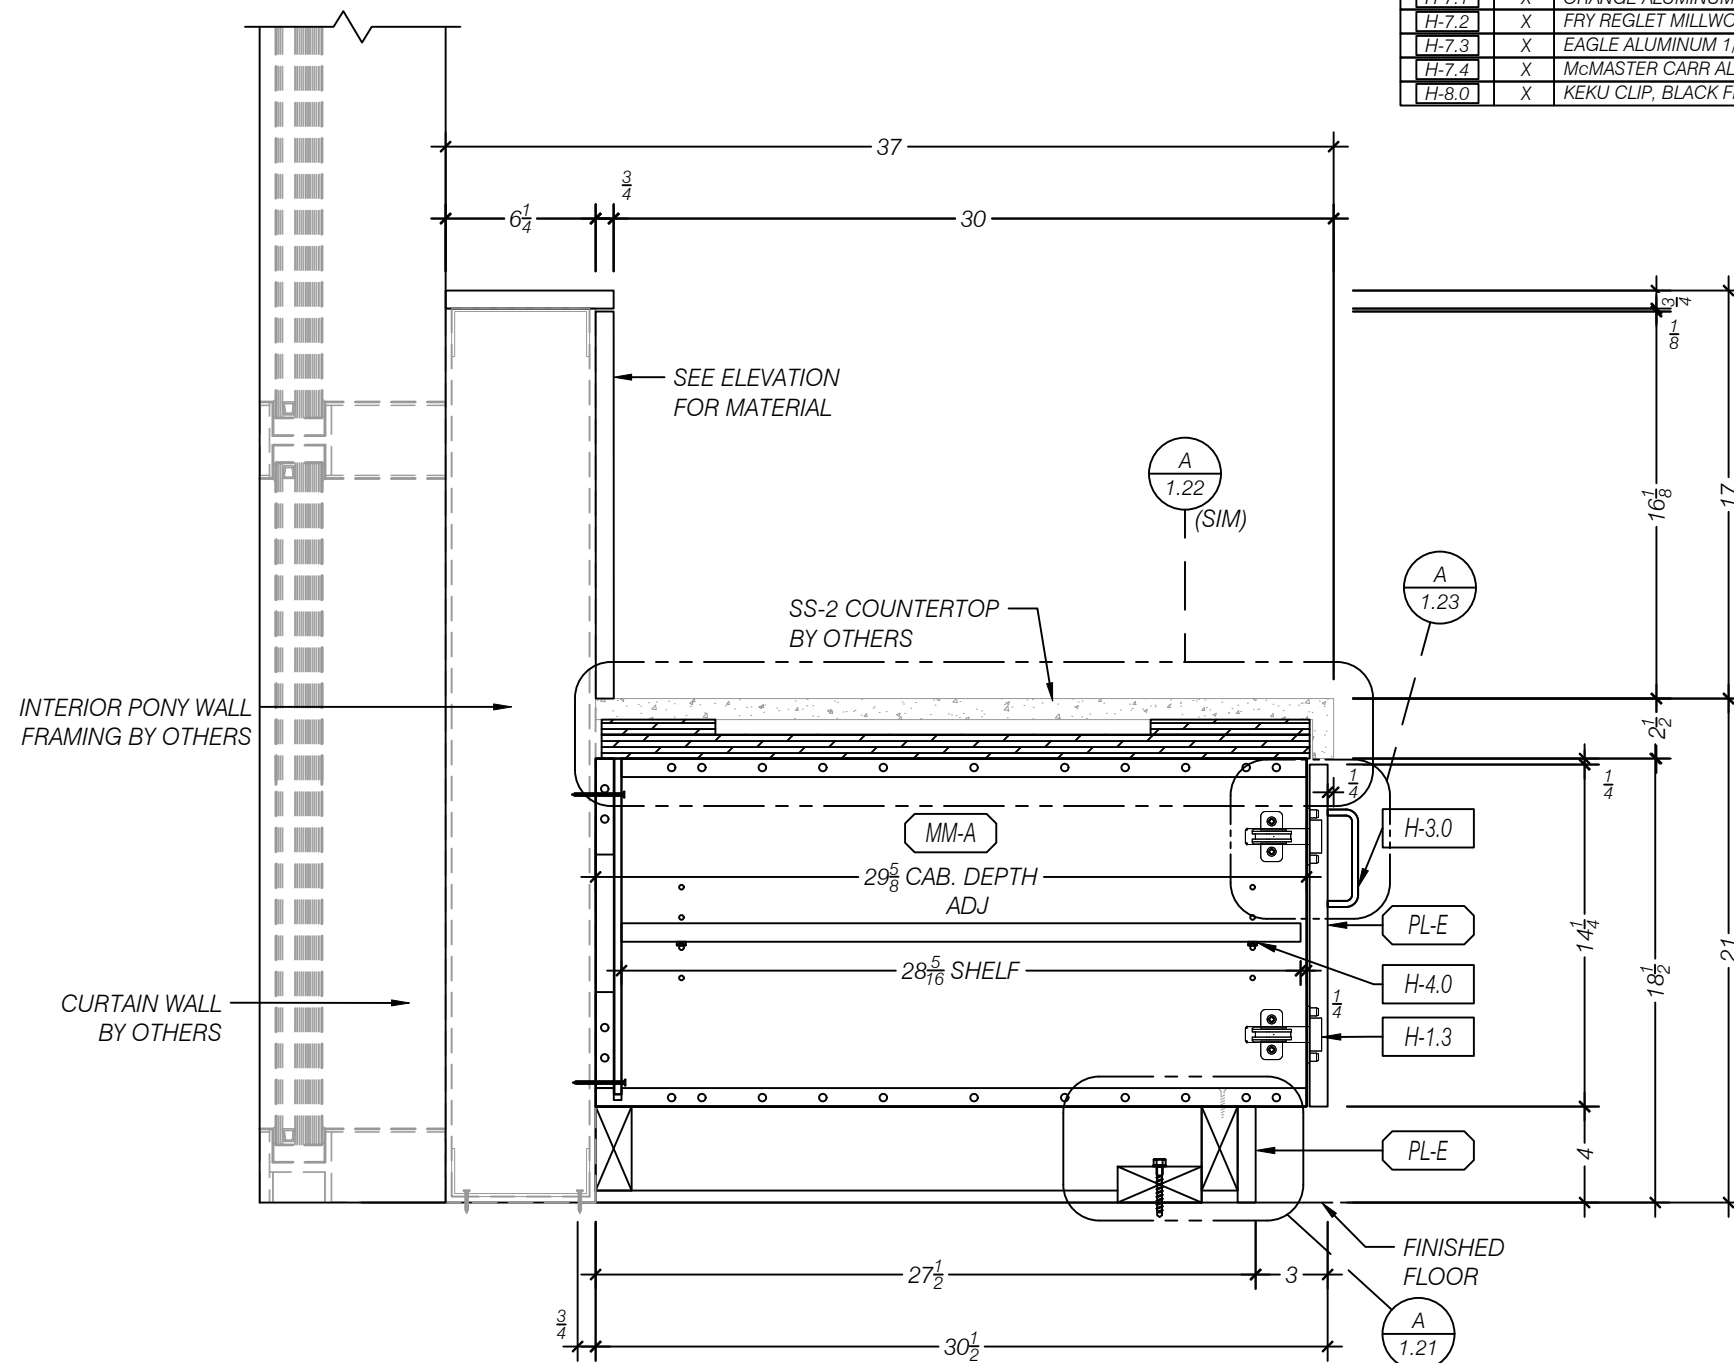

**A** SECTION - LOW COUNTER BASE CABINET w/ TRANSACTION COUNTER  
SCALE 1:8 (1 1/2" = 1'-0")  
ARCH REF: 5/AE584


**DGS SREOC COSTA  
MESA  
RECEPTION**

| ISSUE      |                     |      |
|------------|---------------------|------|
| DATE       | DESCRIPTION         | BY   |
| 05/05/2026 | REV-A FOR SUBMITTAL | Q-AS |
| -          | -                   | -    |
| -          | -                   | -    |
**SITE ADDRESS**

|              |                                                     |            |       |
|--------------|-----------------------------------------------------|------------|-------|
| <b>TREET</b> | 2301 South Shelley<br>Circle <i>BLDG. A &amp; B</i> |            |       |
| <b>CITY</b>  | Costa Mesa                                          |            |       |
| <b>STATE</b> | CA                                                  | <b>ZIP</b> | 92626 |

|                     |                 |
|---------------------|-----------------|
| <b>JOB #:</b> 26034 | <b>REV:</b> A   |
| <b>MOD #:</b> 1     | <b>REL:</b> N/A |

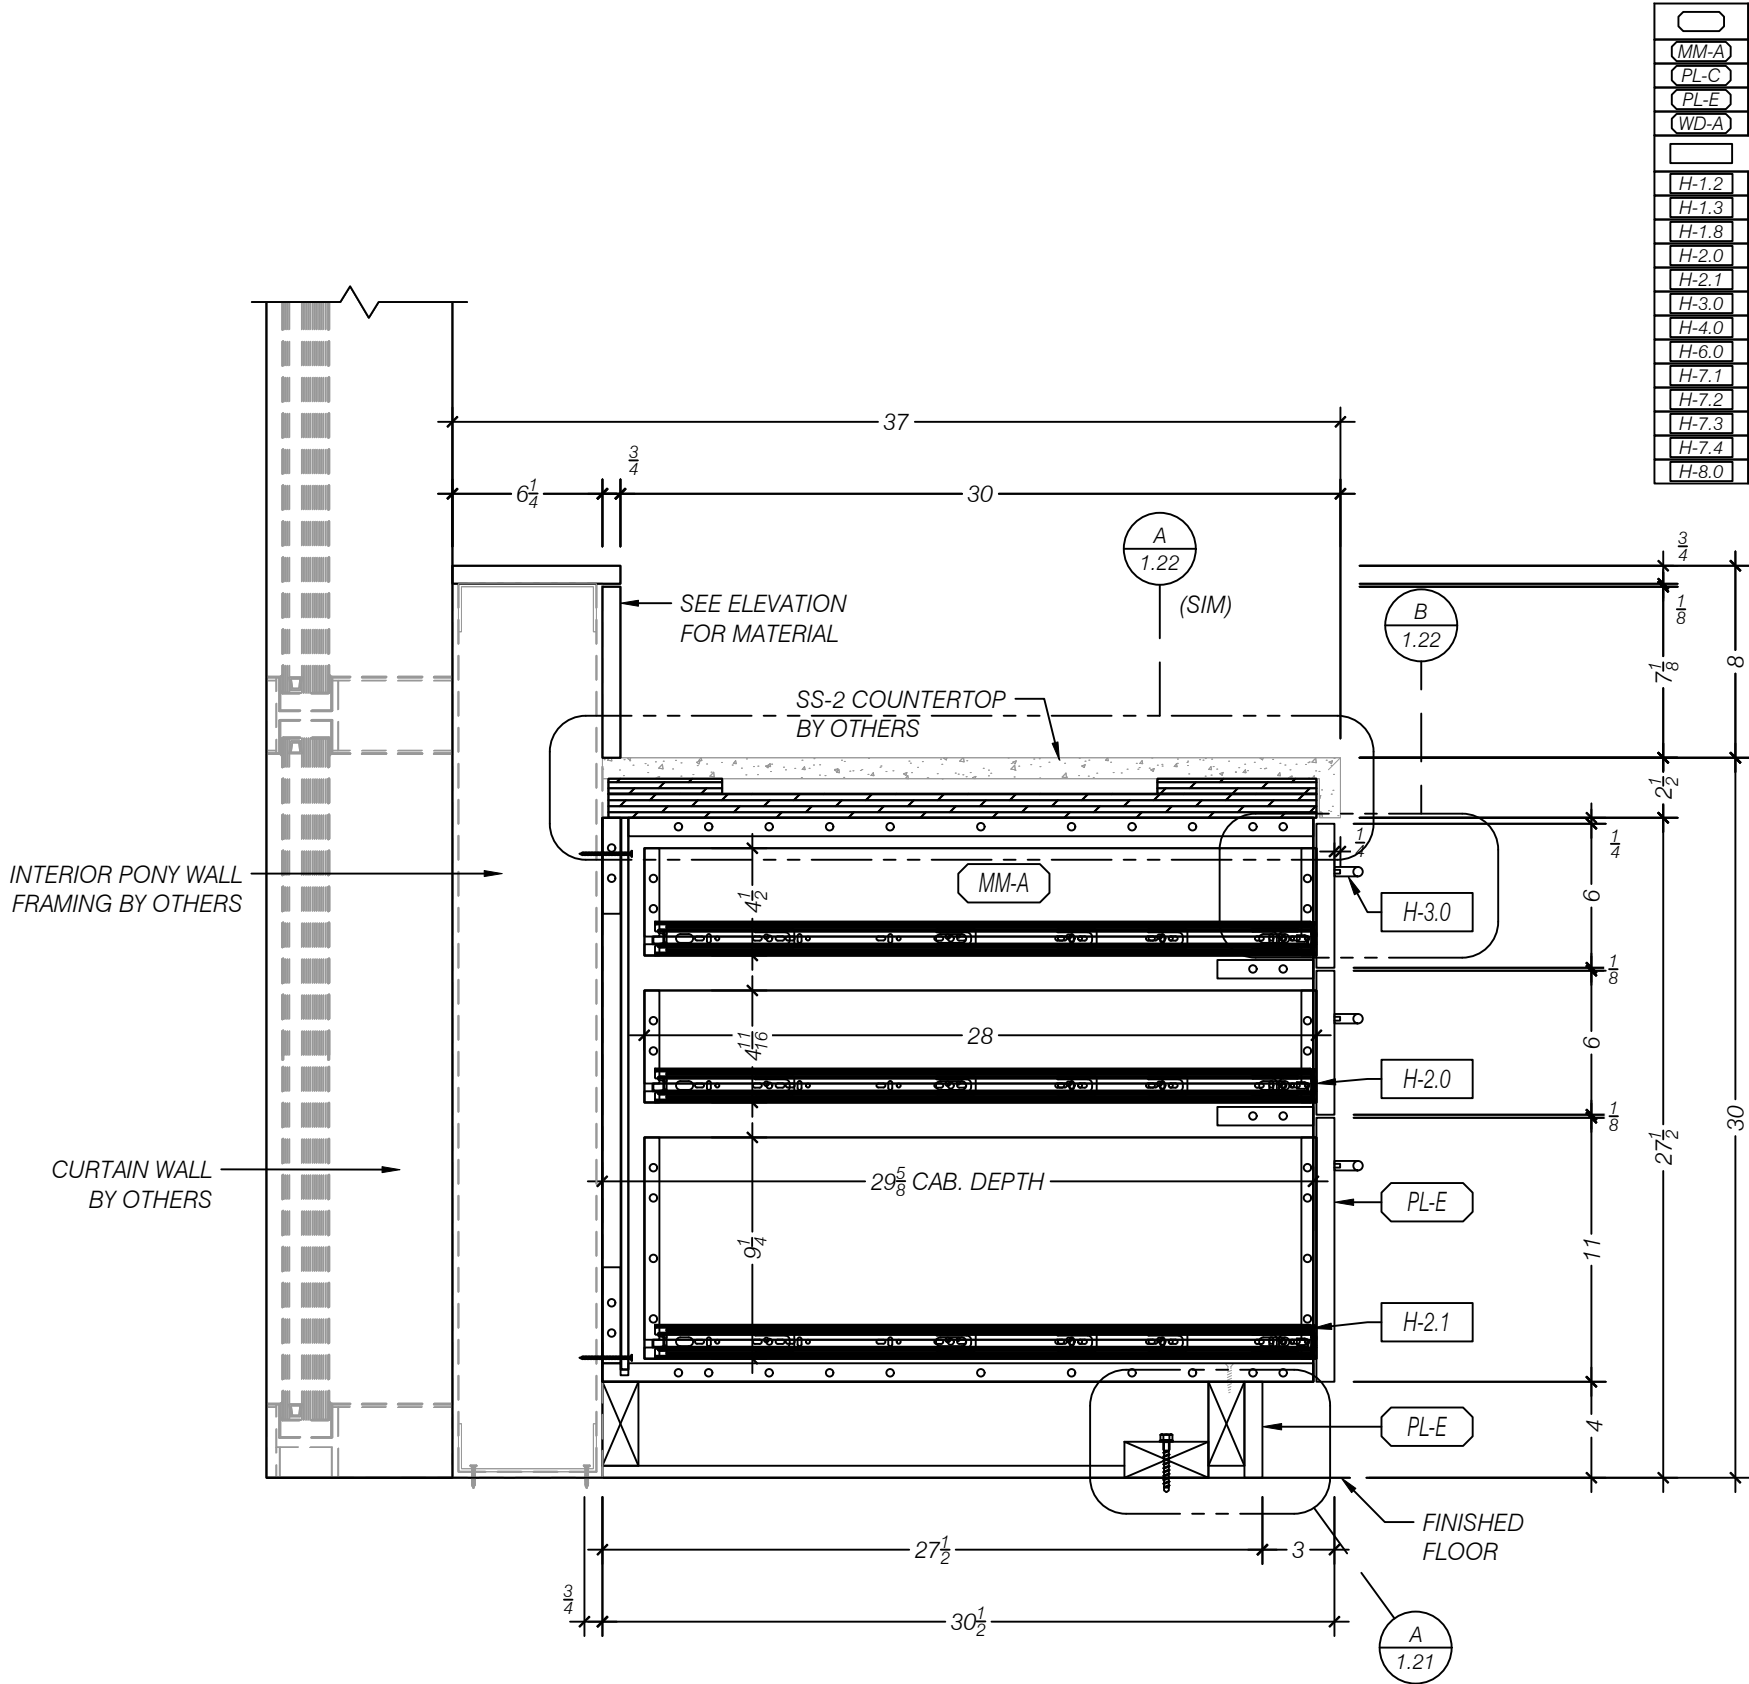

| MATERIALS     |   |                                                                                   |
|---------------|---|-----------------------------------------------------------------------------------|
| (MM-A)        | X | WHITE MELAMINE                                                                    |
| (PL-C)        | X | (PL-1, WB-2) WILSONART "HARVEST MAPLE", 7953-38, FINE VELVET TEXTURE              |
| (PL-E)        | X | (PL-3) WILSONART "WHITE", 1570-60, FINE VELVET TEXTURE 1570-38                    |
| (WD-A)        | X | (WD-1) SURFACING SOLUTIONS, MAPLE TAMBOUR HALF ROUND, PROFILE 383, 3/4"W x 5/16"H |
| QTY. HARDWARE |   |                                                                                   |
| H-1.2         | X | SALICE 0mm CLIP-ON HINGE PLATE EURO SCREW, BARGR09/16                             |
| H-1.3         | X | SALICE 110° FO SOFT-CLOSE, LOGICA SILENTIA, C7J6AE9                               |
| H-1.8         | X | MC KINNEY DOUBLE ACTING SPRING HINGE, 1001,6",SATIN CHROME FINISH                 |
| H-2.0         | X | KNAPE & VOGT DRAWER SLIDES, KV8400, SIDE MOUNT, FULL EXT. 100lb LOAD RATING       |
| H-2.1         | X | KNAPE & VOGT DRAWER SLIDES, KV8600, SIDE MOUNT, FULL EXT. 150lb LOAD RATING       |
| H-3.0         | X | BERENSON WIRE PULL, BN6131-2SC-P, 96mm CTC, SATIN CHROME FINISH                   |
| H-4.0         | X | HAFELE SHELF SUPPORT, 282.04.711, 5mm SHELF PIN, STEEL NICKEL-PLATED              |
| H-6.0         | X | MOCKETT TG FLIP-TOP SERIES DESK GROMMET, 2"Ø, COLOR T.B.D.                        |
| H-7.1         | X | ORANGE ALUMINUM Z-CLIP HD PANEL RAIL                                              |
| H-7.2         | X | FRY REGLET MILLWORK REVEAL, 1" PANEL, 1/2" REVEAL, MWRB50P100, POWDER COATED      |
| H-7.3         | X | EAGLE ALUMINUM 1/8" CORNER ACCENT, MILL FINISH                                    |
| H-7.4         | X | McMASTER CARR ALUMINUM CHANNEL, 9001K664, 1-3/4"W x 1"H, MILL FINISH              |
| H-8.0         | X | KEKU CLIP, BLACK FINISH                                                           |


**A** SECTION - 3 DRAWER BASE CABINET w/ TRANSACTION COUNTER  
SCALE 1:8 (1 1/2"=1'-0")  
ARCH REF: 6/AE584

DGS SREOC COSTA

MESA

RECEPTION

| ISSUE        |                                       |      |       |
|--------------|---------------------------------------|------|-------|
| DATE         | DESCRIPTION                           | BY   |       |
| 05/05/2026   | REV-A FOR SUBMITTAL                   | Q-AS |       |
|              |                                       |      |       |
|              |                                       |      |       |
|              |                                       |      |       |
|              |                                       |      |       |
| SITE ADDRESS |                                       |      |       |
| STREET       | 2301 South Shelley Circle BLDG. A & B |      |       |
| CITY         | Costa Mesa                            |      |       |
| STATE        | CA                                    | ZIP  | 92626 |
| JOB #:       | 26034                                 | REV: | A     |
| MOD #:       | 1                                     | REL: | N/A   |
| 1.18         |                                       |      |       |

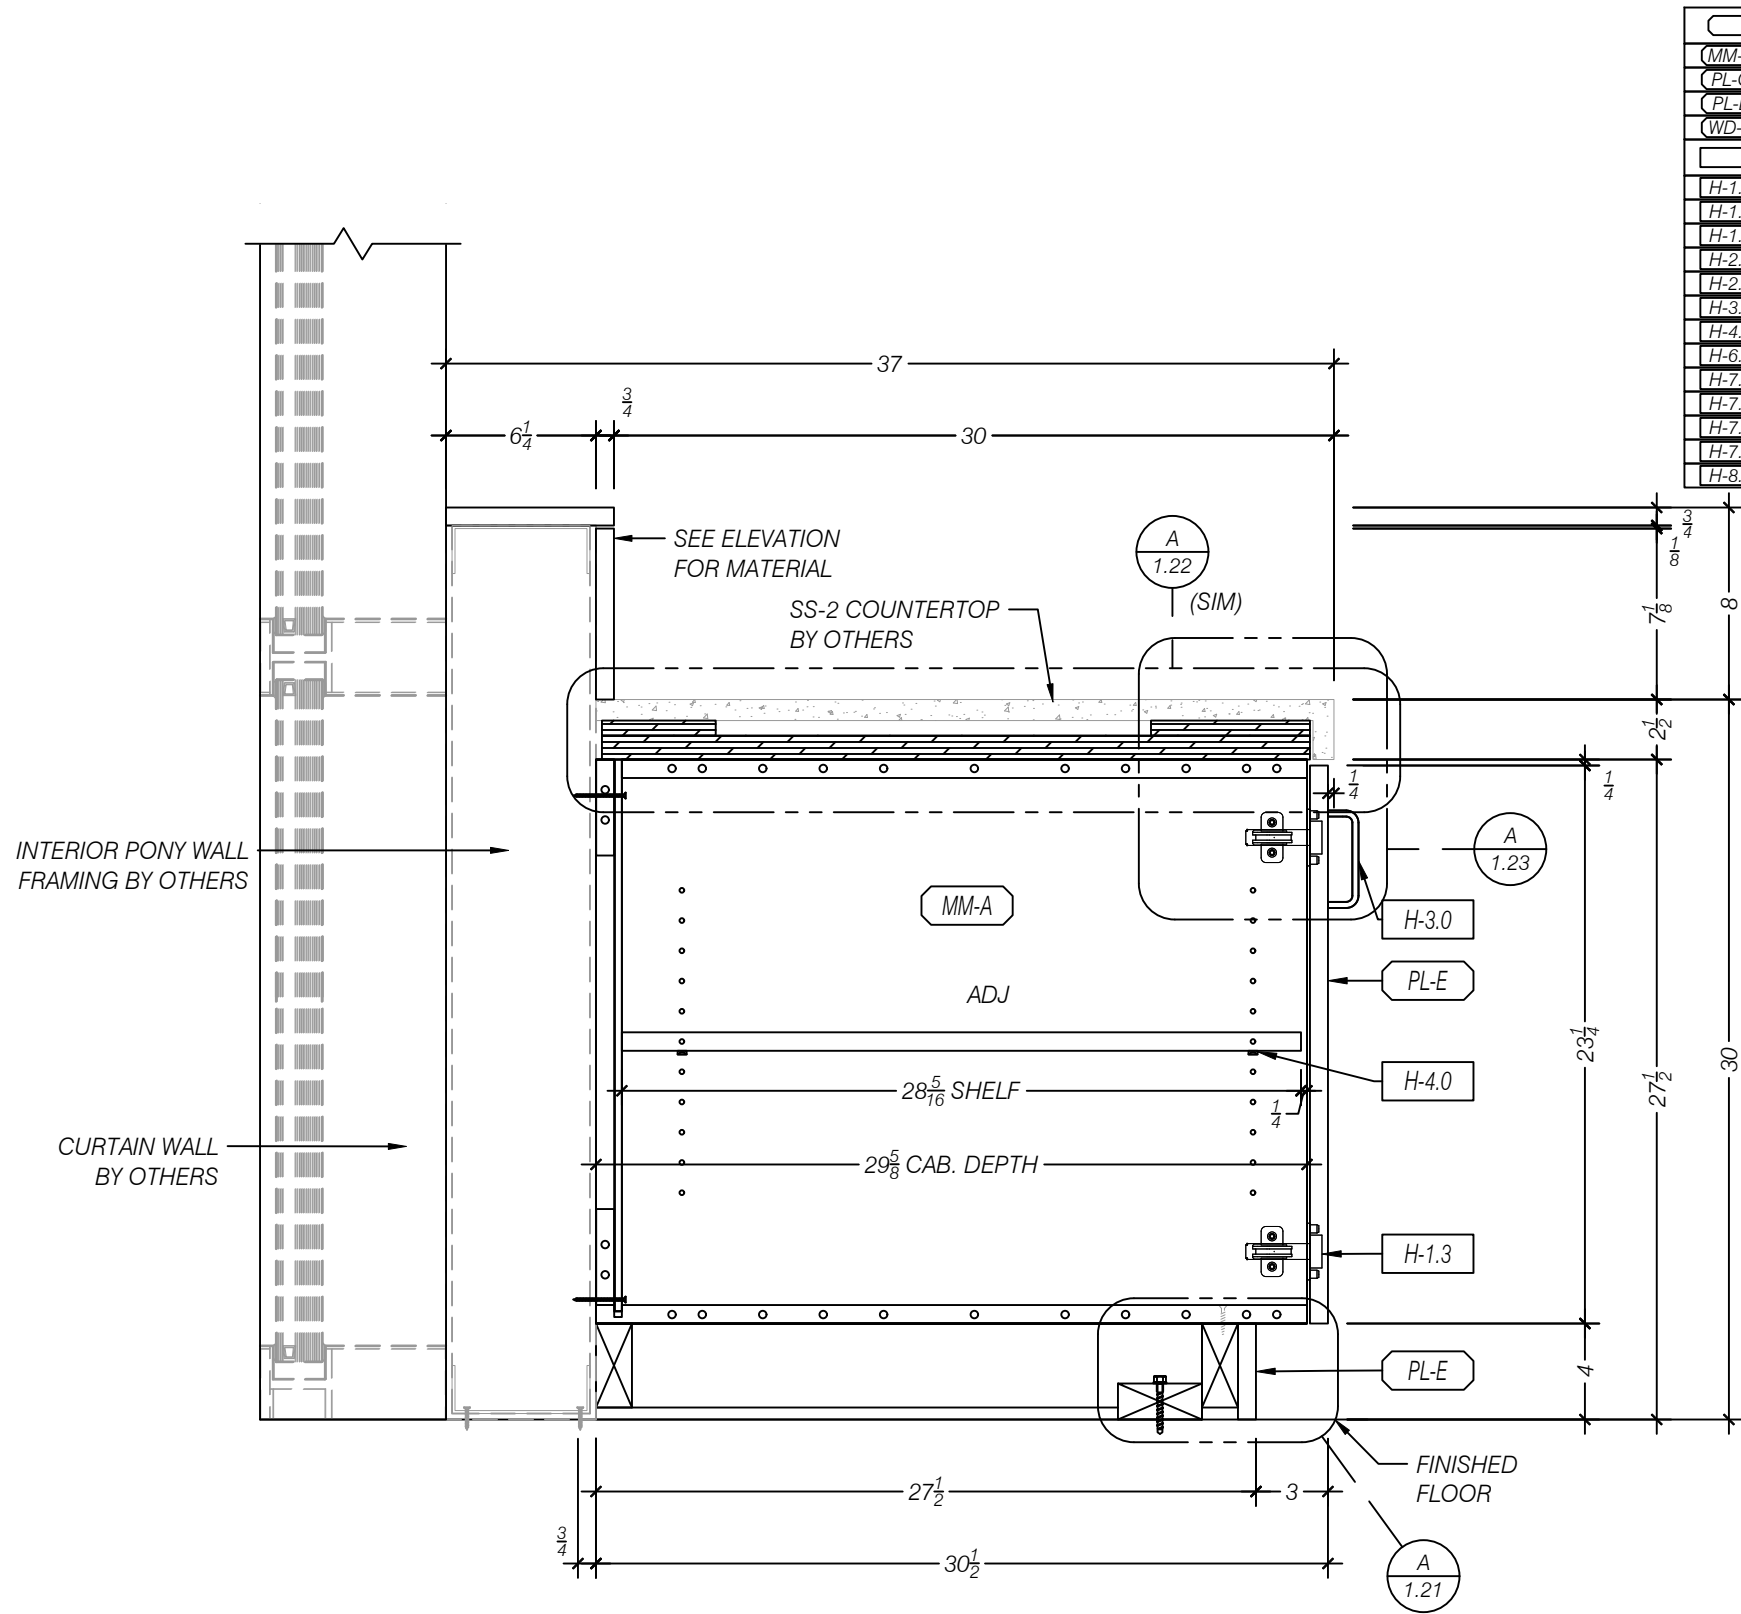


|        |      | MATERIALS                                                                         |
|--------|------|-----------------------------------------------------------------------------------|
| (MM-A) |      | WHITE MELAMINE                                                                    |
| (PL-C) |      | (PL-1, WB-2) WILSONART "HARVEST MAPLE", 7953-38, FINE VELVET TEXTURE              |
| (PL-E) |      | (PL-3) WILSONART "WHITE", 1570-60, FINE VELVET TEXTURE 1570-38                    |
| (WD-A) |      | (WD-1) SURFACING SOLUTIONS, MAPLE TAMBOUR HALF ROUND, PROFILE 383, 3/4"W x 5/16"H |
|        | QTY. | HARDWARE                                                                          |
| H-1.2  | X    | SALICE 0mm CLIP-ON HINGE PLATE EURO SCREW, BARGR09/16                             |
| H-1.3  | X    | SALICE 110° FO SOFT-CLOSE, LOGICA SILENTIA, C7J6AE9                               |
| H-1.8  | X    | MC KINNEY DOUBLE ACTING SPRING HINGE, 1001,6",SATIN CHROME FINISH                 |
| H-2.0  | X    | KNAPE & VOGT DRAWER SLIDES, KV8400, SIDE MOUNT, FULL EXT. 100lb LOAD RATING       |
| H-2.1  | X    | KNAPE & VOGT DRAWER SLIDES, KV8600, SIDE MOUNT, FULL EXT. 150lb LOAD RATING       |
| H-3.0  | X    | BERENSON WIRE PULL, BN6131-2SC-P, 96mm CTC, SATIN CHROME FINISH                   |
| H-4.0  | X    | HAFELE SHELF SUPPORT, 282.04.711, 5mm SHELF PIN, STEEL NICKEL-PLATED              |
| H-6.0  | X    | MOCKETT TG FLIP-TOP SERIES DESK GROMMET, 2"Ø, COLOR T.B.D.                        |
| H-7.1  | X    | ORANGE ALUMINUM Z-CLIP HD PANEL RAIL                                              |
| H-7.2  | X    | FRY REGLET MILLWORK REVEAL, 1" PANEL, 1/2" REVEAL, MWRB50P100, POWDER COATED      |
| H-7.3  | X    | EAGLE ALUMINUM 1/8" CORNER ACCENT, MILL FINISH                                    |
| H-7.4  | X    | McMASTER CARR ALUMINUM CHANNEL, 9001K664, 1-3/4"W x 1"H, MILL FINISH              |
| H-8.0  | X    | KEKU CLIP, BLACK FINISH                                                           |

**A** SECTION - BASE CABINET w/ DOOR  
SCALE 1:8 (1 1/2"=1'-0")  
ARCH REF: 7/AE584


**DGS SREOC COSTA**  
**MESA**  
**RECEPTION**

| ISSUE      |                     | BY   |
|------------|---------------------|------|
| DATE       | DESCRIPTION         |      |
| 05/05/2026 | REV-A FOR SUBMITTAL | Q-AS |
| -          | -                   | -    |
| -          | -                   | -    |
| -          | -                   | -    |
| -          | -                   | -    |


| SITE ADDRESS |                                       |      |       |
|--------------|---------------------------------------|------|-------|
| STREET       | 2301 South Shelley Circle BLDG. A & B |      |       |
| CITY         | Costa Mesa                            |      |       |
| STATE        | CA                                    | ZIP  | 92626 |
| JOB #:       | 26034                                 | REV: | A     |
| MOD #:       | 1                                     | REL: | N/A   |

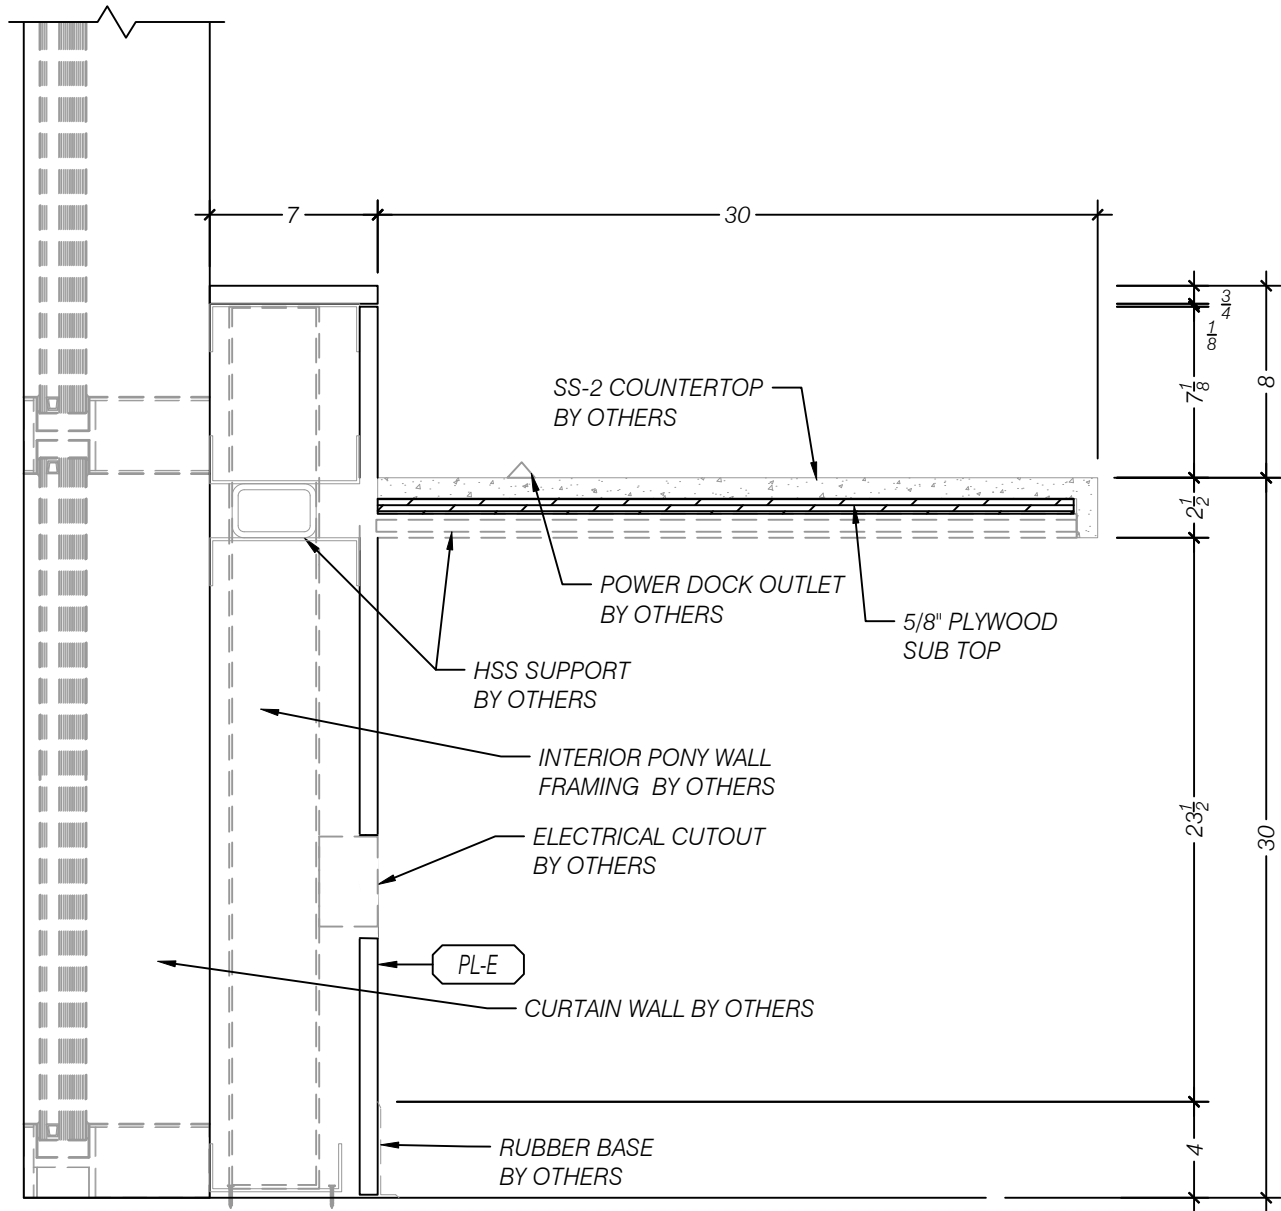

**A** SECTION - OPEN KNEE SPACE COUNTER w/ TRANSACTION COUNTER  
SCALE 1:8 (1 1/2" = 1'-0")  
ARCH REF: 8/AE584

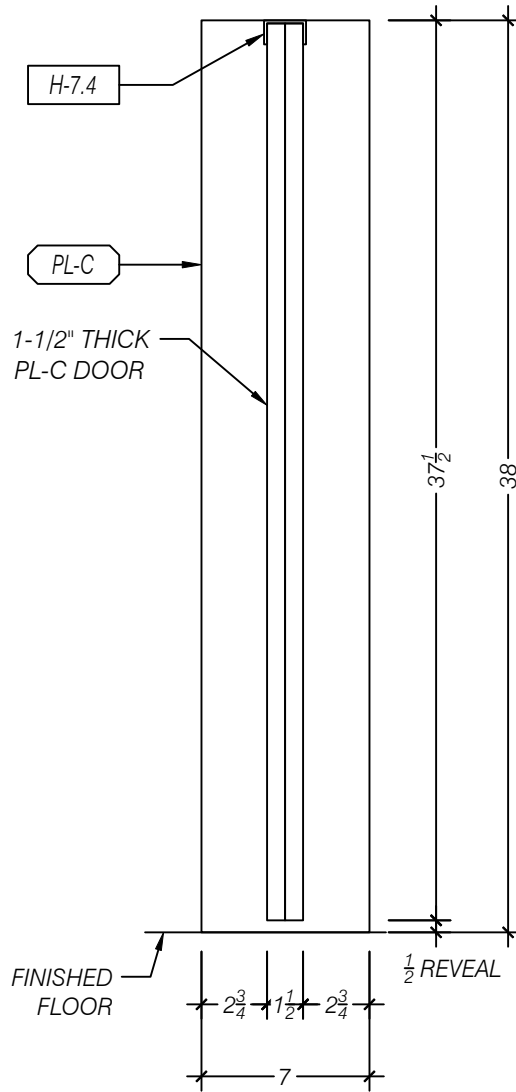

**B** SECTION - U CHANNEL @ TOP OF GATE  
SCALE 1:8 (1 1/2" = 1'-0")  
ARCH REF: NA

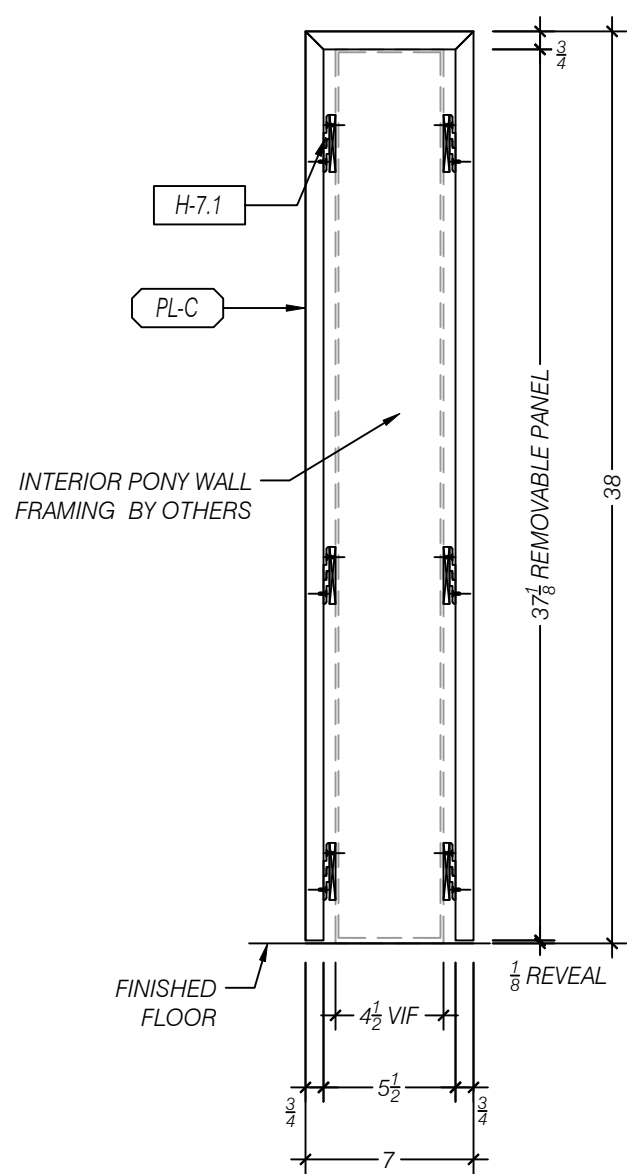

**C** SECTION - PANEL PARTITION  
SCALE 1:8 (1 1/2" = 1'-0")  
ARCH REF: NA


| MATERIALS     |   |                                                                                   |
|---------------|---|-----------------------------------------------------------------------------------|
| (MM-A)        | X | WHITE MELAMINE                                                                    |
| (PL-C)        | X | (PL-1, WB-2) WILSONART "HARVEST MAPLE", 7953-38, FINE VELVET TEXTURE              |
| (PL-E)        | X | (PL-3) WILSONART "WHITE", 1570-60, FINE VELVET TEXTURE 1570-38                    |
| (WD-A)        | X | (WD-1) SURFACING SOLUTIONS, MAPLE TAMBOUR HALF ROUND, PROFILE 383, 3/4"W x 5/16"H |
| QTY. HARDWARE |   |                                                                                   |
| H-1.2         | X | SALICE 0mm CLIP-ON HINGE PLATE EURO SCREW, BARGR09/16                             |
| H-1.3         | X | SALICE 110° FO SOFT-CLOSE, LOGICA SILENTIA, C7J6AE9                               |
| H-1.8         | X | MC KINNEY DOUBLE ACTING SPRING HINGE, 1001, 6", SATIN CHROME FINISH               |
| H-2.0         | X | KNAPE & VOGT DRAWER SLIDES, KV8400, SIDE MOUNT, FULL EXT. 100lb LOAD RATING       |
| H-2.1         | X | KNAPE & VOGT DRAWER SLIDES, KV8600, SIDE MOUNT, FULL EXT. 150lb LOAD RATING       |
| H-3.0         | X | BERENSON WIRE PULL, BN6131-2SC-P, 96mm CTC, SATIN CHROME FINISH                   |
| H-4.0         | X | HAFELE SHELF SUPPORT, 282.04.711, 5mm SHELF PIN, STEEL NICKEL-PLATED              |
| H-6.0         | X | MOCKETT TG FLIP-TOP SERIES DESK GROMMET, 2"Ø, COLOR T.B.D.                        |
| H-7.1         | X | ORANGE ALUMINUM Z-CLIP HD PANEL RAIL                                              |
| H-7.2         | X | FRY REGLET MILLWORK REVEAL, 1" PANEL, 1/2" REVEAL, MWRB50P100, POWDER COATED      |
| H-7.3         | X | EAGLE ALUMINUM 1/8" CORNER ACCENT, MILL FINISH                                    |
| H-7.4         | X | McMASTER CARR ALUMINUM CHANNEL, 9001K664, 1-3/4"W x 1"H, MILL FINISH              |
| H-8.0         | X | KEKU CLIP, BLACK FINISH                                                           |

**DGS SREOC COSTA**  
**MESA**  
**RECEPTION**

| ISSUE      |                     | BY   |
|------------|---------------------|------|
| DATE       | DESCRIPTION         |      |
| 05/05/2026 | REV-A FOR SUBMITTAL | Q-AS |
|            |                     | -    |
|            |                     | -    |
| SITE ADDRESS |                                       |      |       |
|--------------|---------------------------------------|------|-------|
| STREET       | 2301 South Shelley Circle BLDG. A & B |      |       |
| CITY         | Costa Mesa                            |      |       |
| STATE        | CA                                    | ZIP  | 92626 |
| JOB #:       | 26034                                 | REV: | A     |
| MOD #:       | 1                                     | REL: | N/A   |

TYPICAL TOE KICK DETAILS SET TO INDUSTRY STANDARDS BY DEFAULT (U.O.N.)  
IF TOE IS SET TO SUB FLOOR, GC TO SPECIFY LOCATION OF LEVEL / CONTROL MARK  
TO BE USED, AND INSTALLER TO ADD FINISHED FLOOR THICKNESS  
TO FINISH OUT TOE AT SPECIFIED HEIGHT

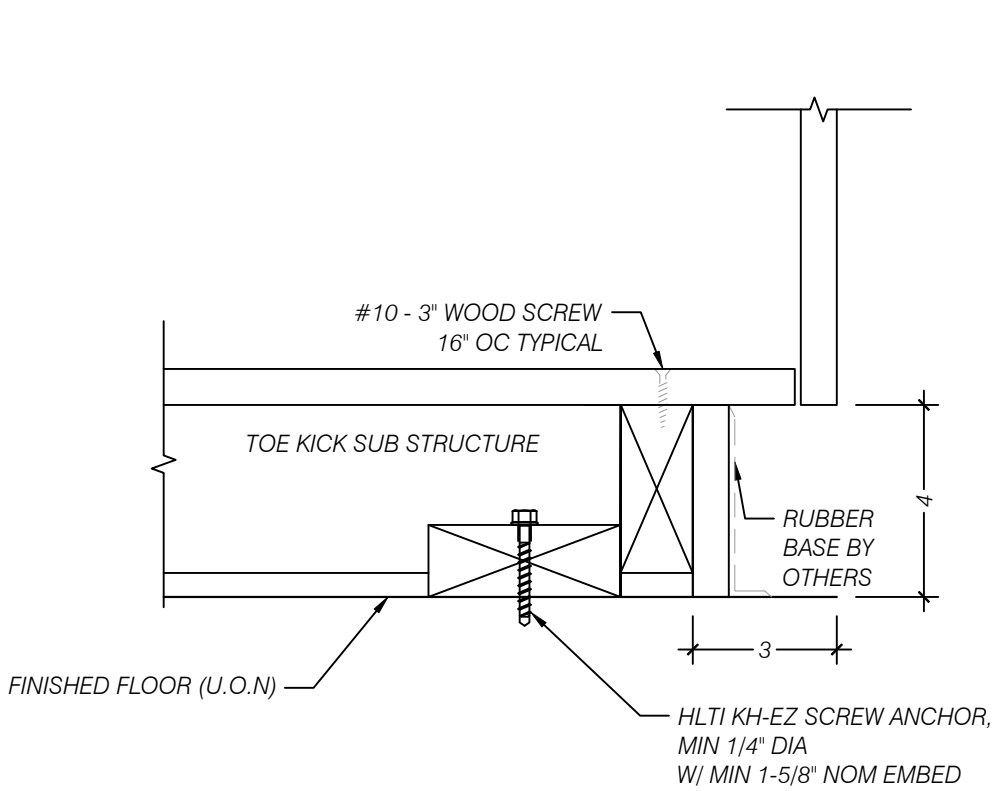

**A** ENLARGED DETAIL - TOE KICK FACE  
SCALE 1:4 (3"=1'-0")  
ARCH REF: NA

|        |      | MATERIALS                                                                         |
|--------|------|-----------------------------------------------------------------------------------|
| (MM-A) |      | WHITE MELAMINE                                                                    |
| (PL-C) |      | (PL-1, WB-2) WILSONART "HARVEST MAPLE", 7953-38, FINE VELVET TEXTURE              |
| (PL-E) |      | (PL-3) WILSONART "WHITE", 1570-60, FINE VELVET TEXTURE 1570-38                    |
| (WD-A) |      | (WD-1) SURFACING SOLUTIONS, MAPLE TAMBOUR HALF ROUND, PROFILE 383, 3/4"W x 5/16"H |
|        | QTY. | HARDWARE                                                                          |
| H-1.2  | X    | SALICE 0mm CLIP-ON HINGE PLATE EURO SCREW, BARGR09/16                             |
| H-1.3  | X    | SALICE 110° FO SOFT-CLOSE, LOGICA SILENTIA, C7J6AE9                               |
| H-1.8  | X    | MC KINNEY DOUBLE ACTING SPRING HINGE, 1001,6",SATIN CHROME FINISH                 |
| H-2.0  | X    | KNAPE & VOGT DRAWER SLIDES, KV8400, SIDE MOUNT, FULL EXT. 100lb LOAD RATING       |
| H-2.1  | X    | KNAPE & VOGT DRAWER SLIDES, KV8600, SIDE MOUNT, FULL EXT. 150lb LOAD RATING       |
| H-3.0  | X    | BERENSON WIRE PULL, BN6131-2SC-P, 96mm CTC, SATIN CHROME FINISH                   |
| H-4.0  | X    | HAFELE SHELF SUPPORT, 282.04.711, 5mm SHELF PIN, STEEL NICKEL-PLATED              |
| H-6.0  | X    | MOCKETT TG FLIP-TOP SERIES DESK GROMMET, 2"Ø, COLOR T.B.D.                        |
| H-7.1  | X    | ORANGE ALUMINUM Z-CLIP HD PANEL RAIL                                              |
| H-7.2  | X    | FRY REGLET MILLWORK REVEAL, 1" PANEL, 1/2" REVEAL, MWRB50P100, POWDER COATED      |
| H-7.3  | X    | EAGLE ALUMINUM 1/8" CORNER ACCENT, MILL FINISH                                    |
| H-7.4  | X    | McMASTER CARR ALUMINUM CHANNEL, 9001K664, 1-3/4"W x 1"H, MILL FINISH              |
| H-8.0  | X    | KEKU CLIP, BLACK FINISH                                                           |

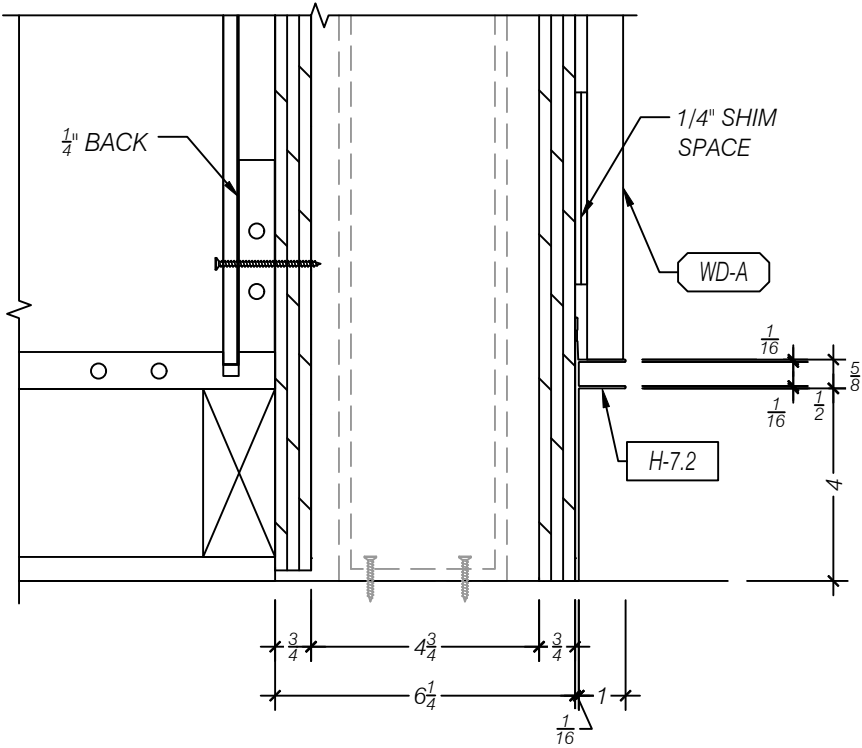


**B** ENLARGED DETAIL - TYPICAL BASE CABINET ATTACHMENT @ PONY WALL  
SCALE 1:4 (3"=1'-0")  
ARCH REF: NA

**CRESTMARK**  
MILLWORK

5640 WEST END ROAD  
ARCATA, CA 95521  
PH (707) 822-4034 FAX (707) 822-5478  
WWW.CRESTMARKMILLWORK.COM


DGS SREOC COSTA  
MESA  
RECEPTION

| ISSUE        |                                       | BY        |
|--------------|---------------------------------------|-----------|
| DATE         | DESCRIPTION                           |           |
| 05/05/2026   | REV-A FOR SUBMITTAL                   | Q-AS      |
| -            | -                                     | -         |
| -            | -                                     | -         |
| SITE ADDRESS |                                       |           |
| STREET       | 2301 South Shelley Circle BLDG. A & B |           |
| CITY         | Costa Mesa                            |           |
| STATE        | CA                                    | ZIP 92626 |
| JOB #:       | 26034                                 | REV: A    |
| MOD #:       | 1                                     | REL: N/A  |
| 1.21         |                                       |           |

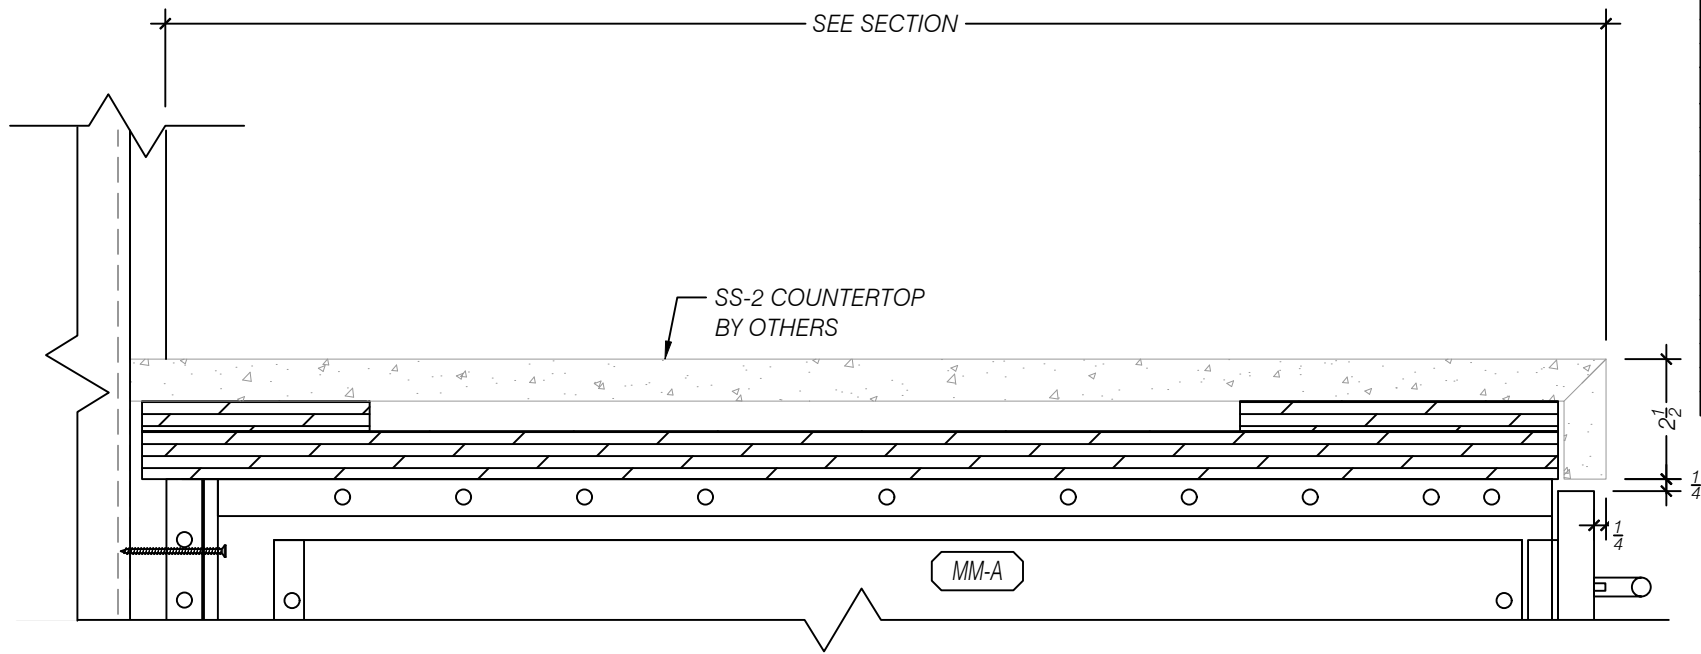

**A** ENLARGED DETAIL - COUNTERTOP DETAIL  
SCALE 1:4 (3"=1'-0")  
ARCH REF: NA

|        |      | MATERIALS                                                                         |
|--------|------|-----------------------------------------------------------------------------------|
| (MM-A) |      | WHITE MELAMINE                                                                    |
| (PL-C) |      | (PL-1, WB-2) WILSONART "HARVEST MAPLE", 7953-38, FINE VELVET TEXTURE              |
| (PL-E) |      | (PL-3) WILSONART "WHITE", 1570-60, FINE VELVET TEXTURE 1570-38                    |
| (WD-A) |      | (WD-1) SURFACING SOLUTIONS, MAPLE TAMBOUR HALF ROUND, PROFILE 383, 3/4"W x 5/16"H |
|        | QTY. | HARDWARE                                                                          |
| H-1.2  | X    | SALICE 0mm CLIP-ON HINGE PLATE EURO SCREW, BARGR09/16                             |
| H-1.3  | X    | SALICE 110° FO SOFT-CLOSE, LOGICA SILENTIA, C7J6AE9                               |
| H-1.8  | X    | MC KINNEY DOUBLE ACTING SPRING HINGE, 1001,6",SATIN CHROME FINISH                 |
| H-2.0  | X    | KNAPE & VOGT DRAWER SLIDES, KV8400, SIDE MOUNT, FULL EXT. 100lb LOAD RATING       |
| H-2.1  | X    | KNAPE & VOGT DRAWER SLIDES, KV8600, SIDE MOUNT, FULL EXT. 150lb LOAD RATING       |
| H-3.0  | X    | BERENSON WIRE PULL, BN6131-2SC-P, 96mm CTC, SATIN CHROME FINISH                   |
| H-4.0  | X    | HAFELE SHELF SUPPORT, 282.04.711, 5mm SHELF PIN, STEEL NICKEL-PLATED              |
| H-6.0  | X    | MOCKETT TG FLIP-TOP SERIES DESK GROMMET, 2"Ø, COLOR T.B.D.                        |
| H-7.1  | X    | ORANGE ALUMINUM Z-CLIP HD PANEL RAIL                                              |
| H-7.2  | X    | FRY REGLET MILLWORK REVEAL, 1" PANEL, 1/2" REVEAL, MWRB50P100, POWDER COATED      |
| H-7.3  | X    | EAGLE ALUMINUM 1/8" CORNER ACCENT, MILL FINISH                                    |
| H-7.4  | X    | McMASTER CARR ALUMINUM CHANNEL, 9001K664, 1-3/4"W x 1"H, MILL FINISH              |
| H-8.0  | X    | KEKU CLIP, BLACK FINISH                                                           |

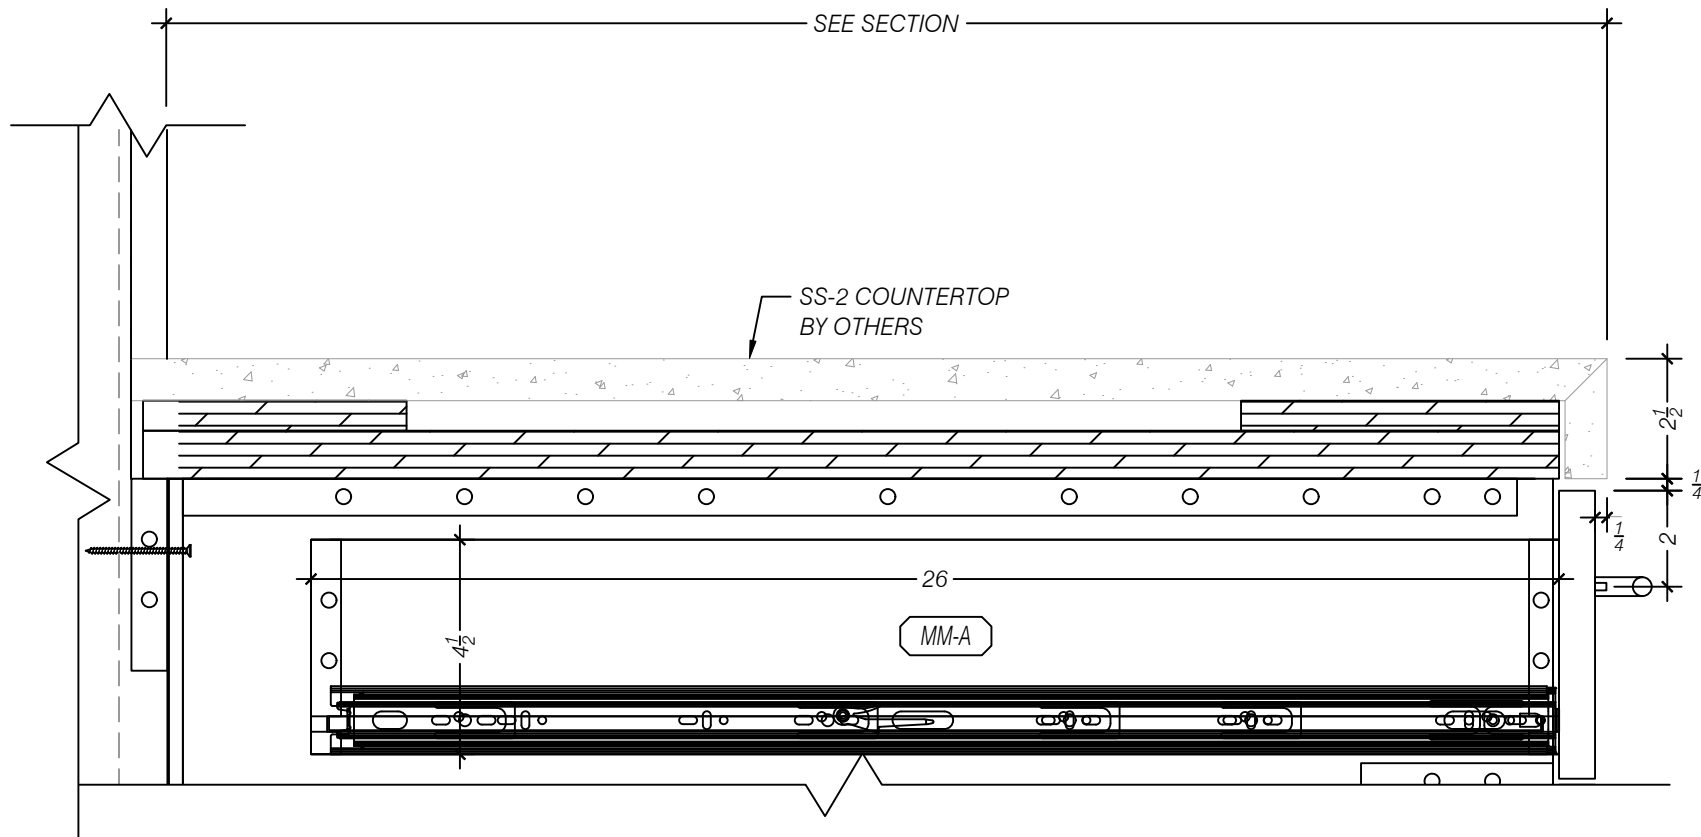


**B** ENLARGED DETAIL - DRAWER PULL LOCATION  
SCALE 1:4 (3"=1'-0")  
ARCH REF: NA



5640 WEST END ROAD  
ARCATA, CA 95521  
PH (707) 822-4034 FAX (707) 822-5478  
WWW.CRESTMARKMILLWORK.COM


**DGS SREOC COSTA**  
**MESA**  
**RECEPTION**

| ISSUE        |                                       | BY        |
|--------------|---------------------------------------|-----------|
| DATE         | DESCRIPTION                           |           |
| 05/05/2026   | REV-A FOR SUBMITTAL                   | Q-AS      |
| -            | -                                     | -         |
| -            | -                                     | -         |
| SITE ADDRESS |                                       |           |
| STREET       | 2301 South Shelley Circle BLDG. A & B |           |
| CITY         | Costa Mesa                            |           |
| STATE        | CA                                    | ZIP 92626 |
| JOB #:       | 26034                                 | REV: A    |
| MOD #:       | 1                                     | REL: N/A  |
| 1.22         |                                       |           |

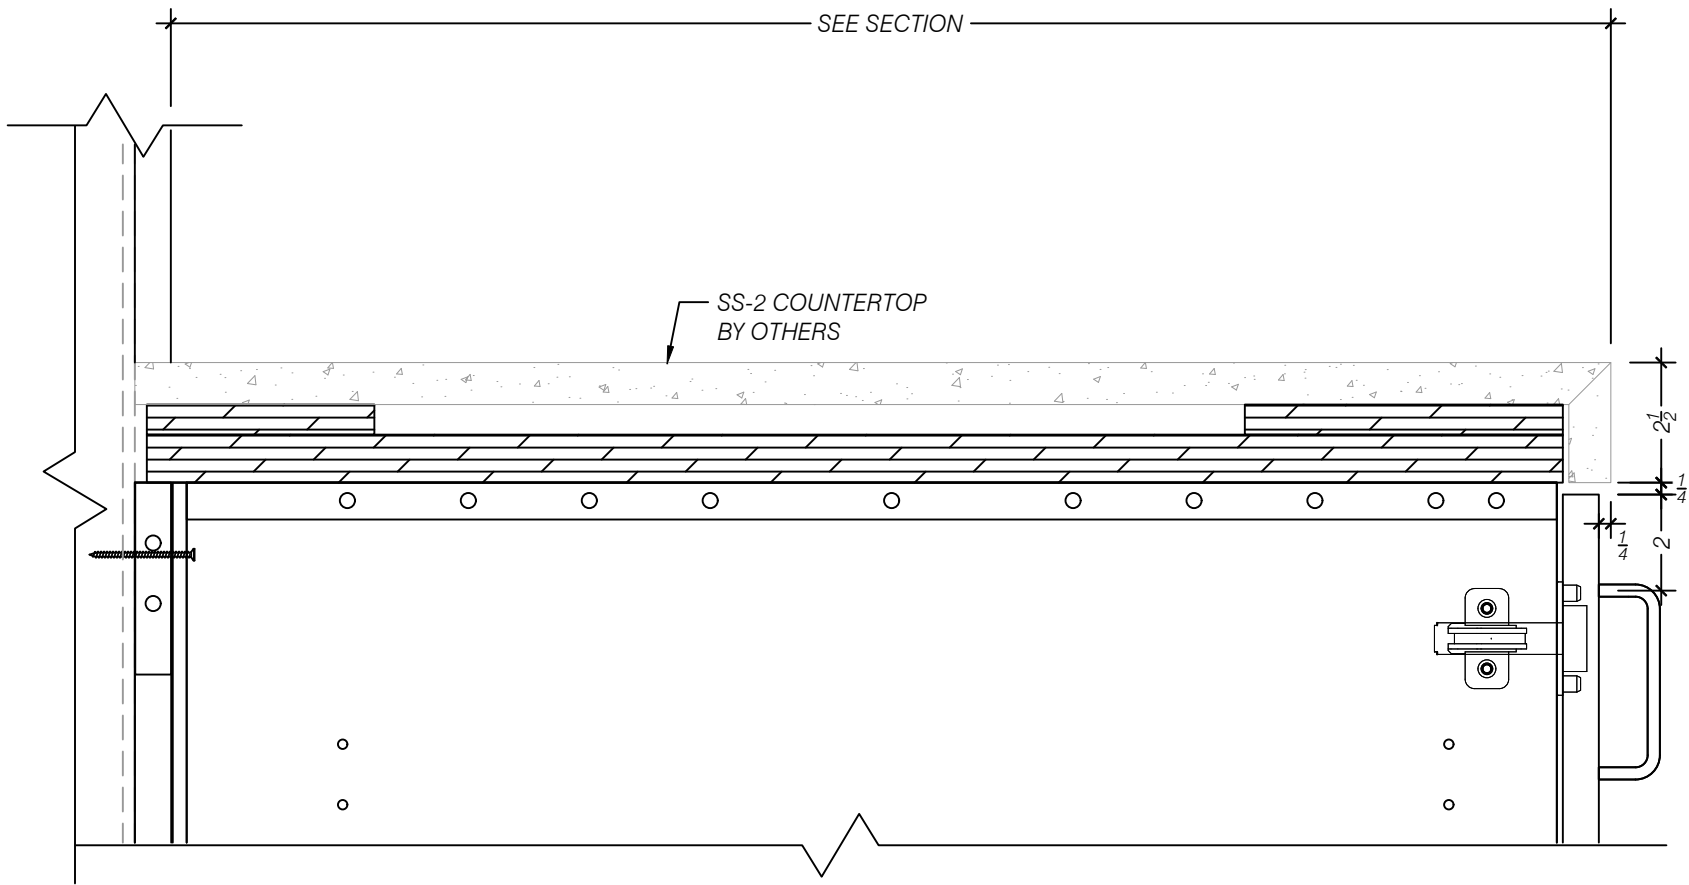

**A** ENLARGED DETAIL - DOOR PULL LOCATION  
SCALE 1:4 (3"=1'-0")  
ARCH REF: NA


|        |      | MATERIALS                                                                         |
|--------|------|-----------------------------------------------------------------------------------|
| (MM-A) |      | WHITE MELAMINE                                                                    |
| (PL-C) |      | (PL-1, WB-2) WILSONART "HARVEST MAPLE", 7953-38, FINE VELVET TEXTURE              |
| (PL-E) |      | (PL-3) WILSONART "WHITE", 1570-60, FINE VELVET TEXTURE 1570-38                    |
| (WD-A) |      | (WD-1) SURFACING SOLUTIONS, MAPLE TAMBOUR HALF ROUND, PROFILE 383, 3/4"W x 5/16"H |
|        | QTY. | HARDWARE                                                                          |
| H-1.2  | X    | SALICE 0mm CLIP-ON HINGE PLATE EURO SCREW, BARGR09/16                             |
| H-1.3  | X    | SALICE 110° FO SOFT-CLOSE, LOGICA SILENTIA, C7J6AE9                               |
| H-1.8  | X    | MC KINNEY DOUBLE ACTING SPRING HINGE, 1001,6",SATIN CHROME FINISH                 |
| H-2.0  | X    | KNAPE & VOGT DRAWER SLIDES, KV8400, SIDE MOUNT, FULL EXT. 100lb LOAD RATING       |
| H-2.1  | X    | KNAPE & VOGT DRAWER SLIDES, KV8600, SIDE MOUNT, FULL EXT. 150lb LOAD RATING       |
| H-3.0  | X    | BERENSON WIRE PULL, BN6131-2SC-P, 96mm CTC, SATIN CHROME FINISH                   |
| H-4.0  | X    | HAFELE SHELF SUPPORT, 282.04.711, 5mm SHELF PIN, STEEL NICKEL-PLATED              |
| H-6.0  | X    | MOCKETT TG FLIP-TOP SERIES DESK GROMMET, 2"Ø, COLOR T.B.D.                        |
| H-7.1  | X    | ORANGE ALUMINUM Z-CLIP HD PANEL RAIL                                              |
| H-7.2  | X    | FRY REGLET MILLWORK REVEAL, 1" PANEL, 1/2" REVEAL, MWRB50P100, POWDER COATED      |
| H-7.3  | X    | EAGLE ALUMINUM 1/8" CORNER ACCENT, MILL FINISH                                    |
| H-7.4  | X    | McMASTER CARR ALUMINUM CHANNEL, 9001K664, 1-3/4"W x 1"H, MILL FINISH              |
| H-8.0  | X    | KEKU CLIP, BLACK FINISH                                                           |

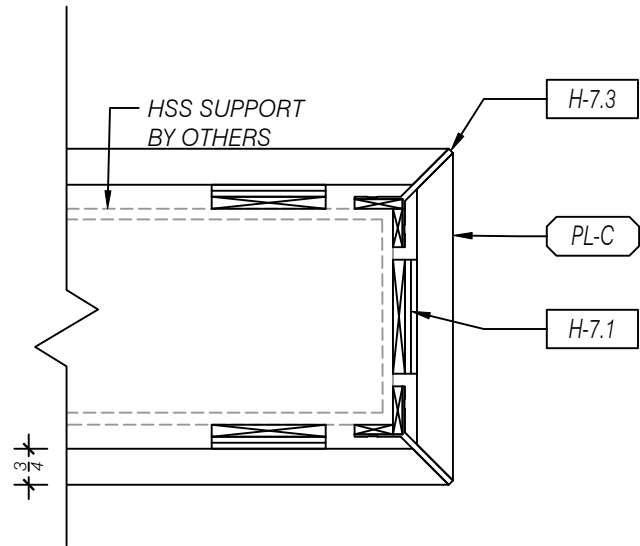

**B** ENLARGED DETAIL - PANEL TO PANEL CONNECTION  
SCALE 1:4 (3"=1'-0")  
ARCH REF: NA

**DGS SREOC COSTA**  
**MESA**  
**RECEPTION**


| ISSUE        |                                       |      |       |  |
|--------------|---------------------------------------|------|-------|--|
| DATE         | DESCRIPTION                           | BY   |       |  |
| 05/05/2026   | REV-A FOR SUBMITTAL                   | Q-AS |       |  |
| -            | -                                     | -    |       |  |
| -            | -                                     | -    |       |  |
| SITE ADDRESS |                                       |      |       |  |
| STREET       | 2301 South Shelley Circle BLDG. A & B |      |       |  |
| CITY         | Costa Mesa                            |      |       |  |
| STATE        | CA                                    | ZIP  | 92626 |  |
| JOB #:       | 26034                                 | REV: | A     |  |
| MOD #:       | 1                                     | REL: | N/A   |  |
| 1.23         |                                       |      |       |  |

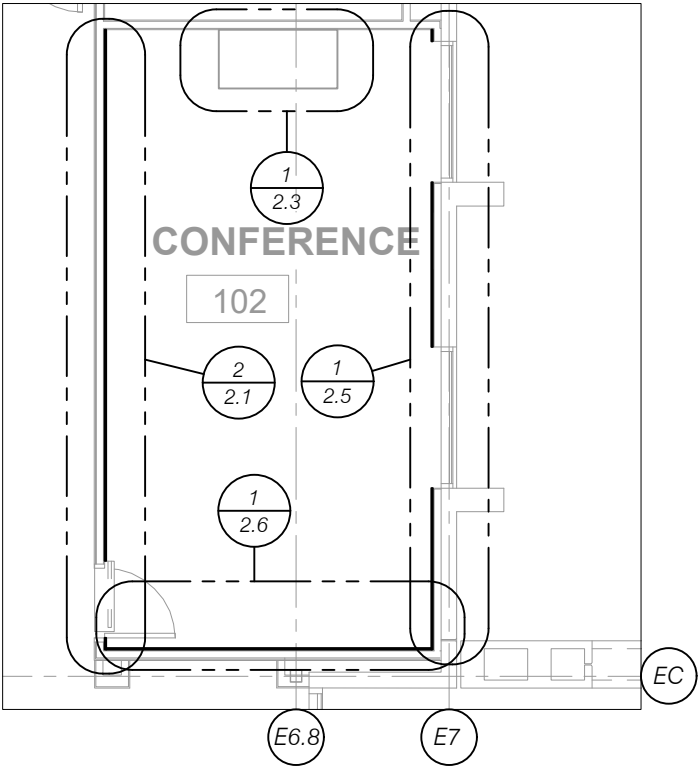

**1** KEY PLAN  
SCALE: NTS  
ARCH REF: 1/AE101.1

| NOTES |   |
|-------|---|
| 1     | ALL DIMENSIONS TO BE FIELD VERIFIED                                                                                          |
| 2     | GENERAL CONTRACTOR TO COORDINATE ALL FRAMING REQUIREMENTS WITH CMI                                                           |
| 3     | GENERAL CONTRACTOR TO COORDINATE ALL WALL TYPES, THICKNESSES AND ROUGH OPENINGS                                              |
| 4     | GENERAL CONTRACTOR & ELECTRICAL CONTRACTOR TO COORDINATE ALL ELECTRICAL BOX LOCATIONS & REQUIREMENTS WITH MILLWORK DRAWINGS  |
| 5     | GENERAL CONTRACTOR & ELECTRICAL CONTRACTOR TO COORDINATE ALL LIGHT FIXTURE FEED & SWITCHING LOCATIONS WITH MILLWORK DRAWINGS |
| 6     | GENERAL CONTRACTOR & PLUMBING CONTRACTOR TO COORDINATE ALL PLUMBING FIXTURES & INSTALLATION REQUIREMENTS                     |

|        |   |
|--------|---|
|        | MATERIALS                                                                                             |
| (PG-C) | (CR-1) FINGER JOINT PINE, DELIVERED PRIME (PREPPING, PAINTING, FILLING OF ATTACHMENT HOLES BY OTHERS) |

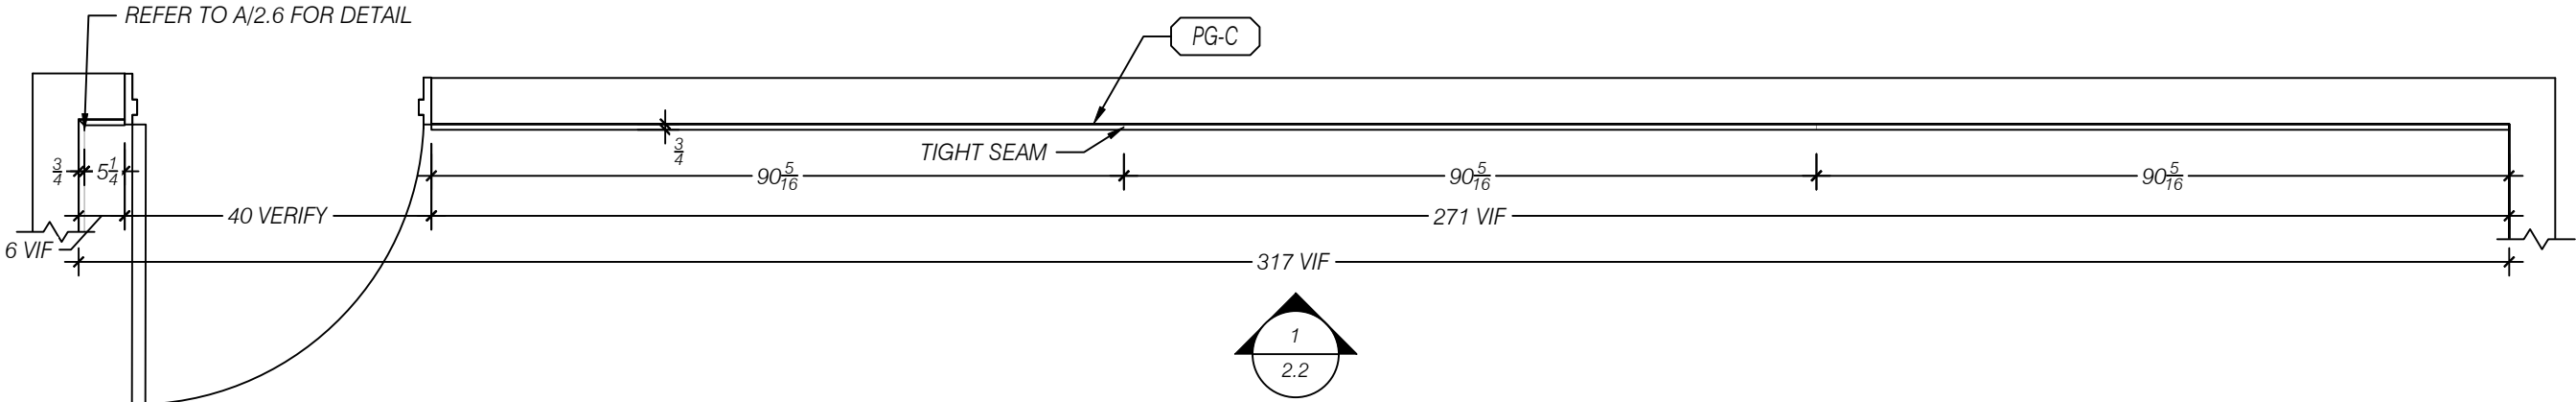

**2** PLAN - CONFERENCE 102  
SCALE 1:24 (1/2"=1'-0")  
ARCH REF: 1/AE406



**CRESTMARK**  
MILLWORK


5640 WEST END ROAD  
ARCATA, CA 95521  
PH (707) 822-4034 FAX (707) 822-5478  
WWW.CRESTMARKMILLWORK.COM

DGS SREOC COSTA  
MESA  
CONFERENCE 102

| ISSUE        |                                       | BY        |
|--------------|---------------------------------------|-----------|
| DATE         | DESCRIPTION                           |           |
| 05/05/2026   | REV-A FOR SUBMITTAL                   | Q-AS      |
| -            | -                                     | -         |
| -            | -                                     | -         |
| SITE ADDRESS |                                       |           |
| STREET       | 2301 South Shelley Circle Bldg. A & B |           |
| CITY         | Costa Mesa                            |           |
| STATE        | CA                                    | ZIP 92626 |
| JOB #:       | 26034                                 | REV: A    |
| MOD #:       | 2                                     | REL: N/A  |
| 2.1          |                                       |           |

CENTERLINE OF IN-WALL STRAPPING  
(STRAPPING BY OTHERS)

30 A.F.F

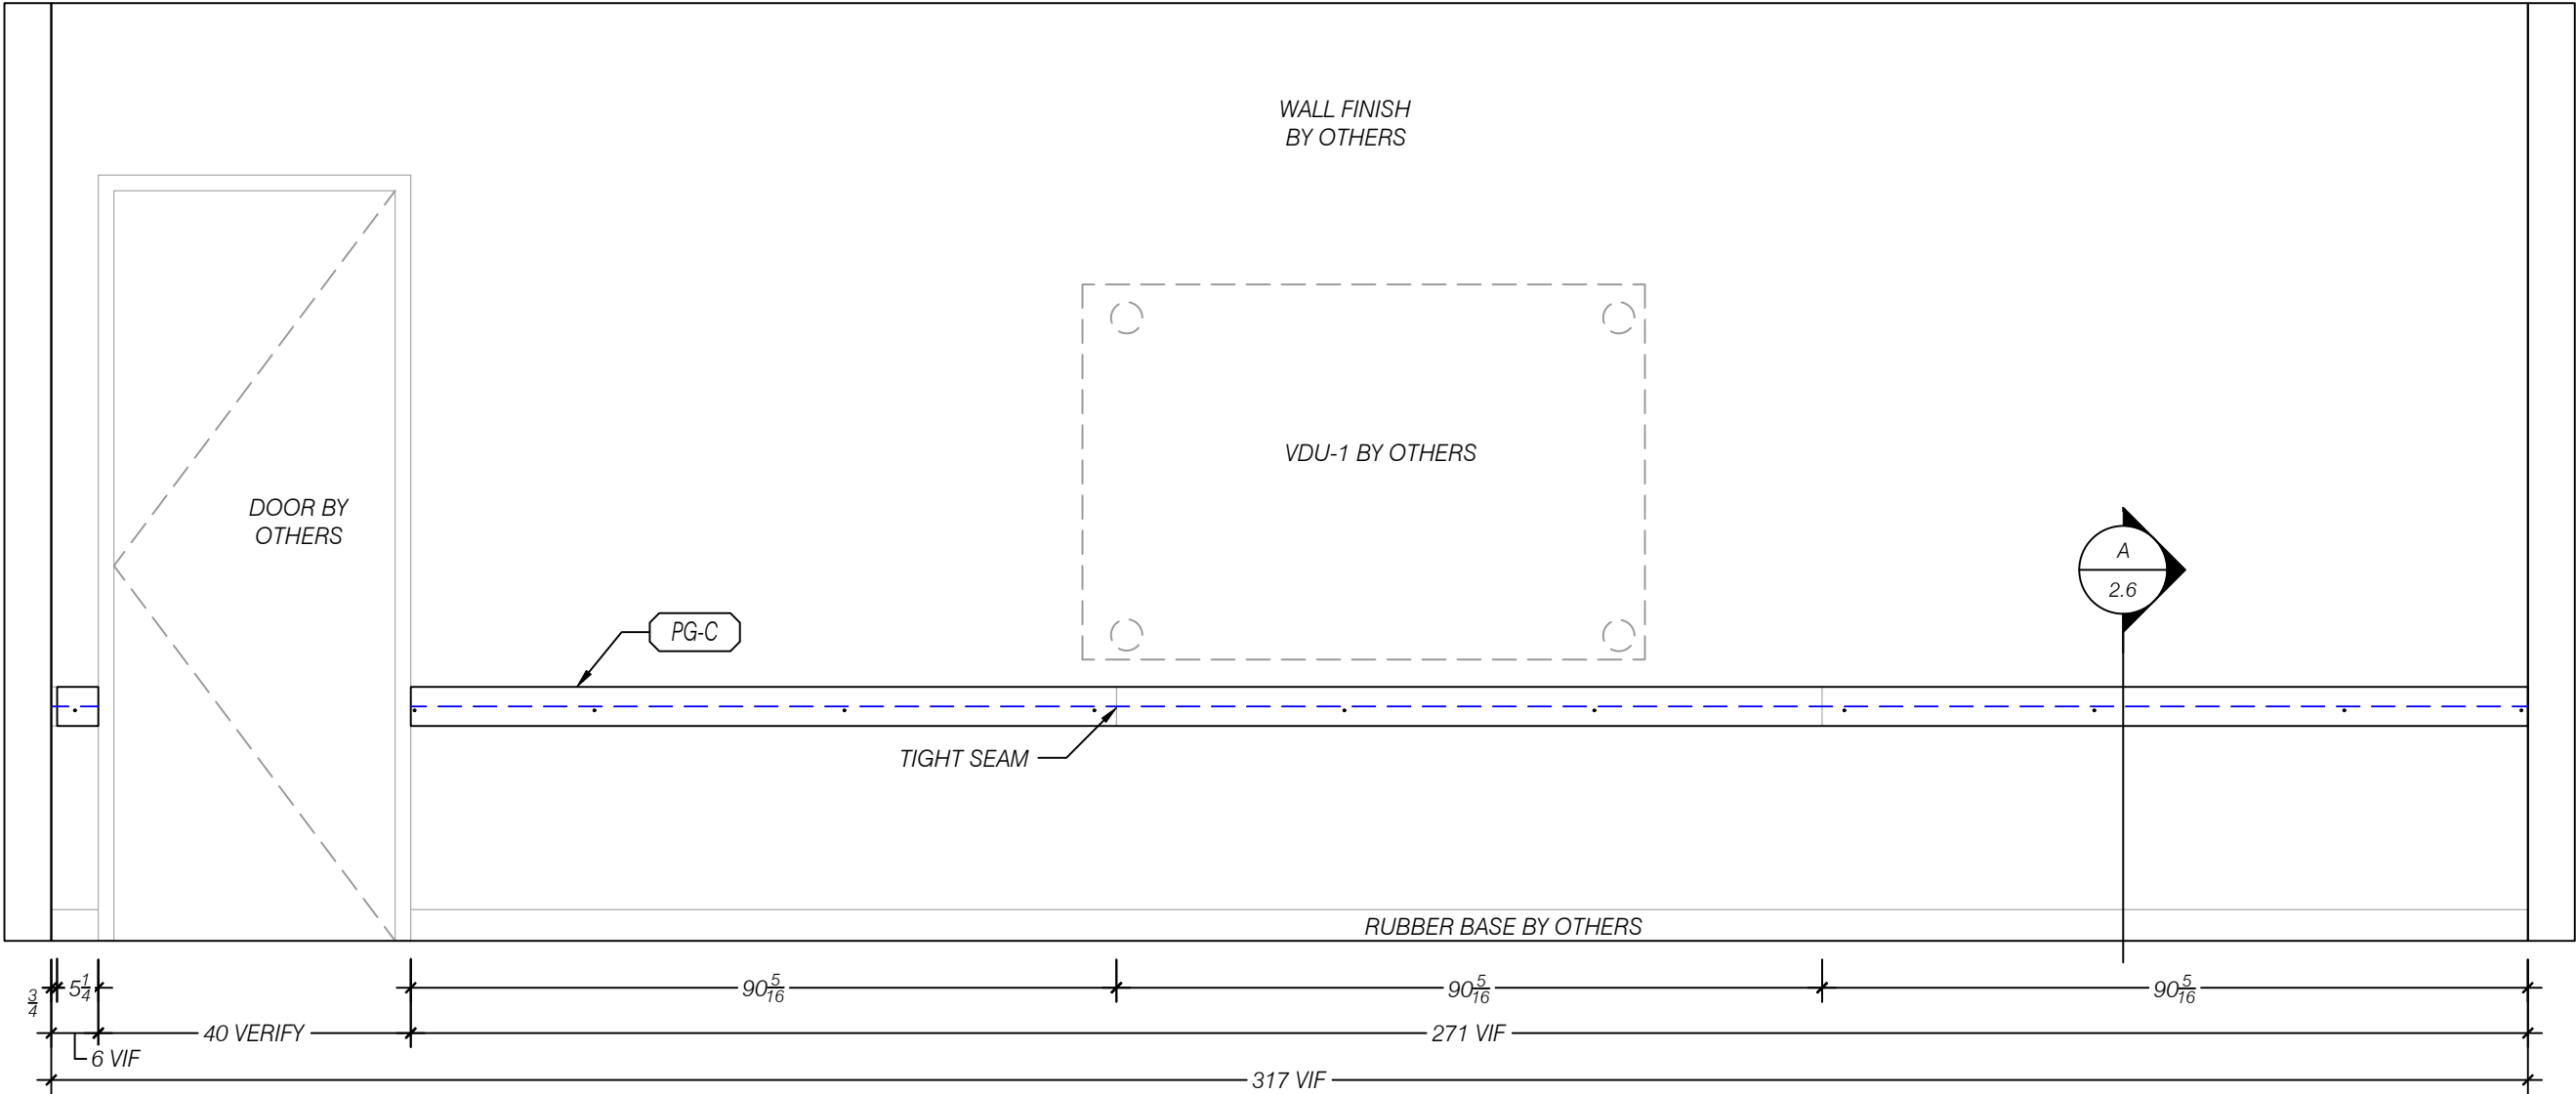

**1** ELEVATION WEST - CONFERENCE 102  
SCALE 1:24 (1/2"=1'-0")  
ARCH REF: 9/AE406



|        |   |
|--------|---|
|        | MATERIALS                                                                                             |
| (PG-C) | (CR-1) FINGER JOINT PINE, DELIVERED PRIME (PREPPING, PAINTING, FILLING OF ATTACHMENT HOLES BY OTHERS) |



5640 WEST END ROAD  
ARCATA, CA 95521  
PH (707) 822-4034 FAX (707) 822-5478  
WWW.CRESTMARKMILLWORK.COM

**DGS SREOC COSTA  
MESA  
CONFERENCE 102**

| ISSUE        |                                       | BY        |
|--------------|---------------------------------------|-----------|
| DATE         | DESCRIPTION                           |           |
| 05/05/2026   | REV-A FOR SUBMITTAL                   | Q-AS      |
| -            | -                                     | -         |
| -            | -                                     | -         |
| SITE ADDRESS |                                       |           |
| STREET       | 2301 South Shelley Circle Bldg. A & B |           |
| CITY         | Costa Mesa                            |           |
| STATE        | CA                                    | ZIP 92626 |
| JOB #:       | 26034                                 | REV: A    |
| MOD #:       | 2                                     | REL: N/A  |
| 2.2          |                                       |           |

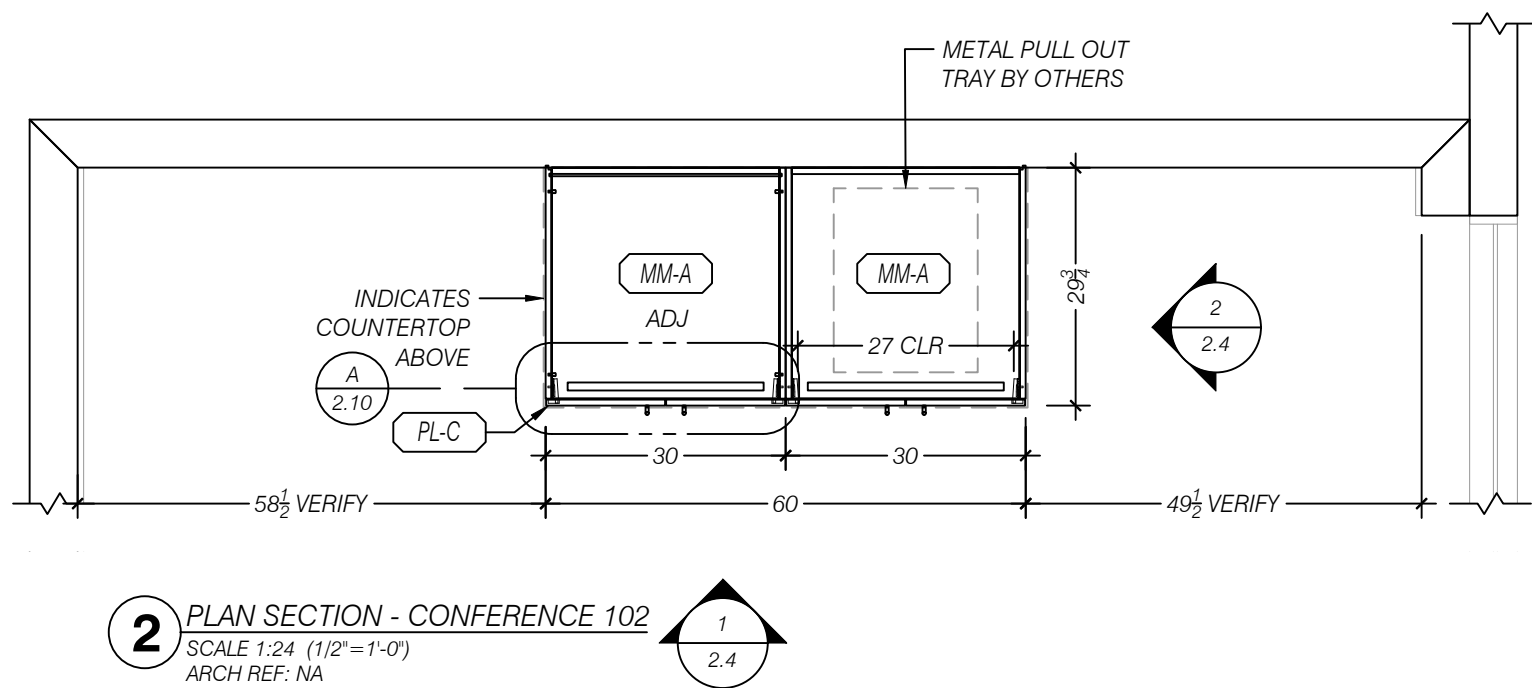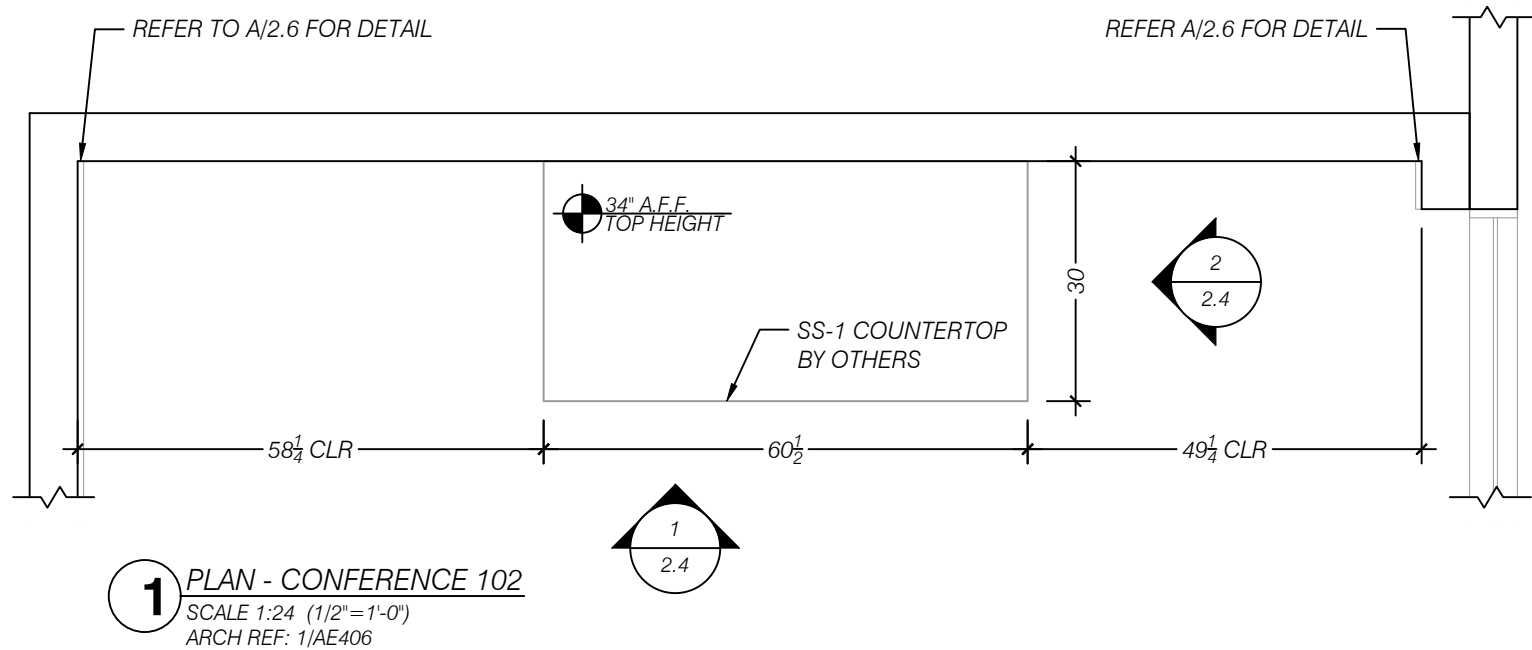

|       |      | MATERIALS                                                                           |
|-------|------|-------------------------------------------------------------------------------------|
| MM-A  |      | WHITE MELAMINE                                                                      |
| PL-C  |      | (PL-1, WB-2) WILSONART "HARVEST MAPLE", 7953-38, FINE VELVET TEXTURE                |
|       | QTY. | HARDWARE                                                                            |
| H-1.2 | X    | SALICE 0mm CLIP-ON HINGE PLATE EURO SCREW, BARGR09/16                               |
| H-1.3 | X    | SALICE 110° FO SOFT-CLOSE, LOGICA SILENTIA, C7J6AE9                                 |
| H-3.0 | X    | BERENSON WIRE PULL, BN6131-2SC-P, 96mm CTC, SATIN CHROME FINISH                     |
| H-4.0 | X    | HAFELE SHELF SUPPORT, 282.04.711, 5mm SHELF PIN, STEEL NICKEL-PLATED                |
| H-9.5 | X    | MOCKETT, GT-METAL AIR VENT GRILLE, 17"W x 4"H OPENING, MATTE BLACK FINISH W/ MESH/3 |




5640 WEST END ROAD  
ARCATA, CA 95521  
PH (707) 822-4034 FAX (707) 822-5478  
WWW.CRESTMARKMILLWORK.COM

**DGS SREOC COSTA**  
**MESA**  
**CONFERENCE 102**

| ISSUE        |                                       |      |       |  |
|--------------|---------------------------------------|------|-------|--|
| DATE         | DESCRIPTION                           | BY   |       |  |
| 05/05/2026   | REV-A FOR SUBMITTAL                   | Q-AS |       |  |
|              |                                       |      |       |  |
|              |                                       |      |       |  |
|              |                                       |      |       |  |
|              |                                       |      |       |  |
| SITE ADDRESS |                                       |      |       |  |
| STREET       | 2301 South Shelley Circle Bldg. A & B |      |       |  |
| CITY         | Costa Mesa                            |      |       |  |
| STATE        | CA                                    | ZIP  | 92626 |  |
| JOB #:       | 26034                                 | REV: | A     |  |
| MOD #:       | 2                                     | REL: | N/A   |  |
| 2.3          |                                       |      |       |  |


CENTERLINE OF IN-WALL STRAPPING  
(STRAPPING BY OTHERS)

31 A.F.F.  
5 A.F.F.

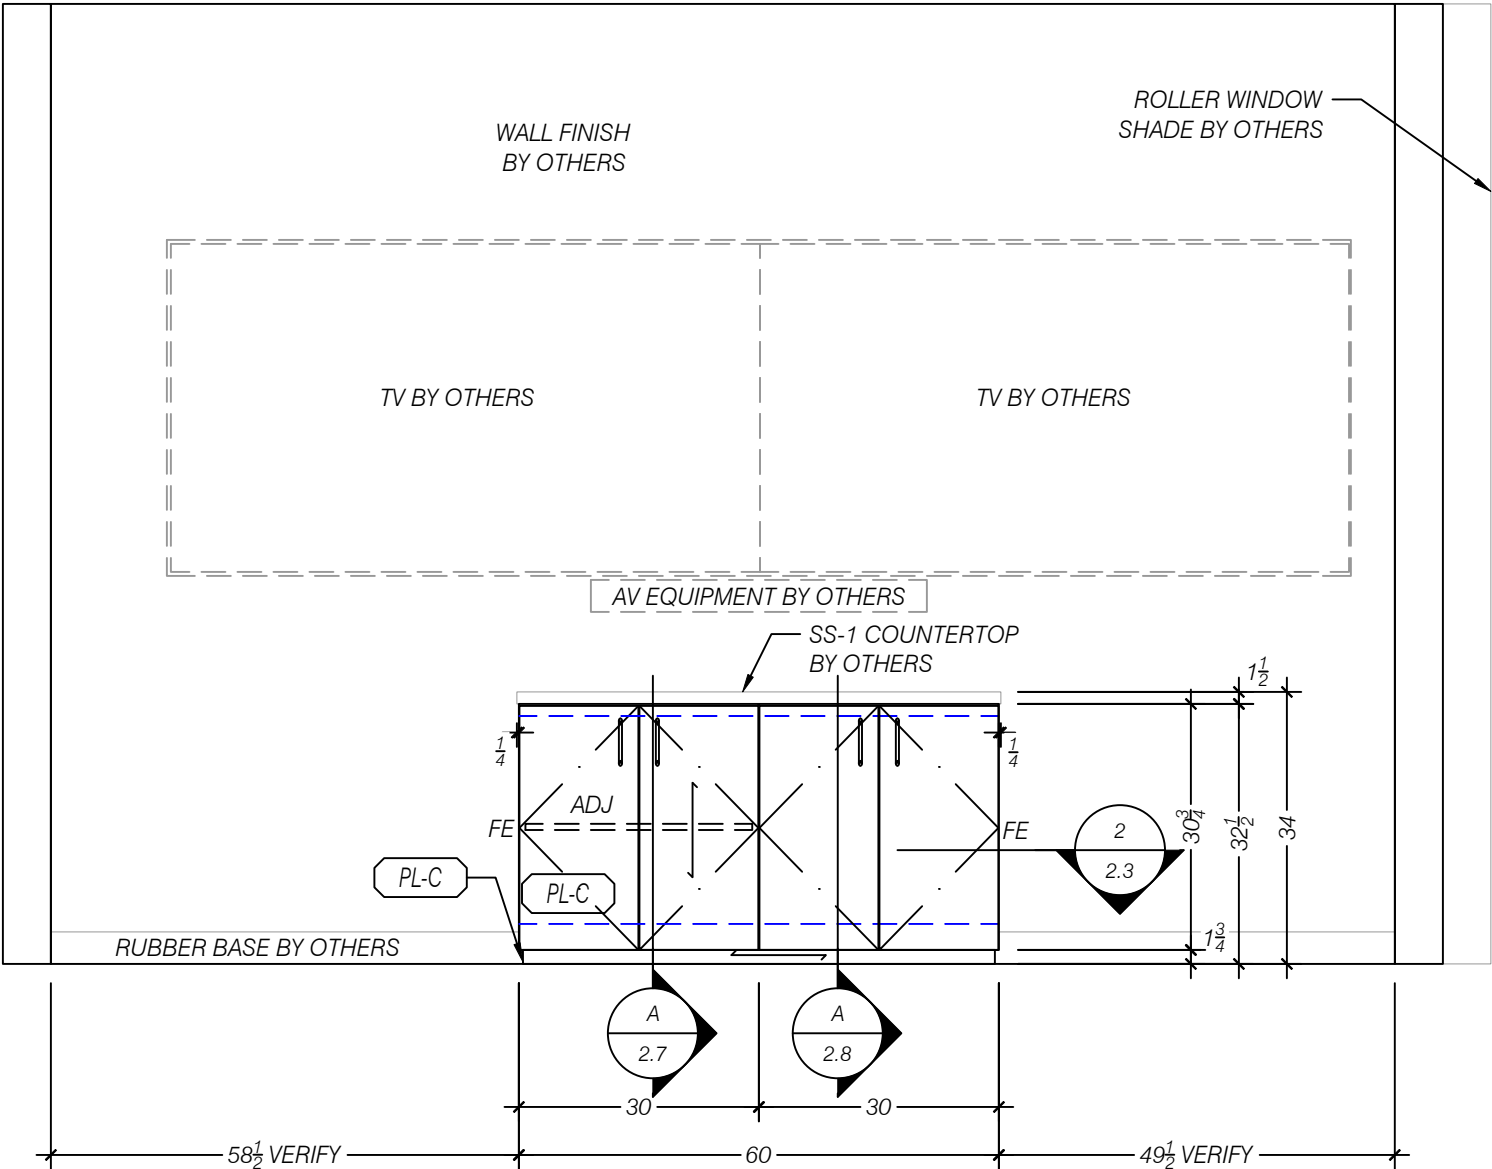

**1** ELEVATION NORTH - CONFERENCE 102  
SCALE 1:24 (1/2" = 1'-0")  
ARCH REF: 6/AE406

|        |      | MATERIALS                                                                           |
|--------|------|-------------------------------------------------------------------------------------|
| (MM-A) |      | WHITE MELAMINE                                                                      |
| (PL-C) |      | (PL-1, WB-2) WILSONART "HARVEST MAPLE", 7953-38, FINE VELVET TEXTURE                |
|        | QTY. | HARDWARE                                                                            |
| H-1.2  | X    | SALICE 0mm CLIP-ON HINGE PLATE EURO SCREW, BARGR09/16                               |
| H-1.3  | X    | SALICE 110° FO SOFT-CLOSE, LOGICA SILENTIA, C7J6AE9                                 |
| H-3.0  | X    | BERENSON WIRE PULL, BN6131-2SC-P, 96mm CTC, SATIN CHROME FINISH                     |
| H-4.0  | X    | HAFELE SHELF SUPPORT, 282.04.711, 5mm SHELF PIN, STEEL NICKEL-PLATED                |
| H-9.5  | X    | MOCKETT, GT-METAL AIR VENT GRILLE, 17"W x 4"H OPENING, MATTE BLACK FINISH W/ MESH/3 |

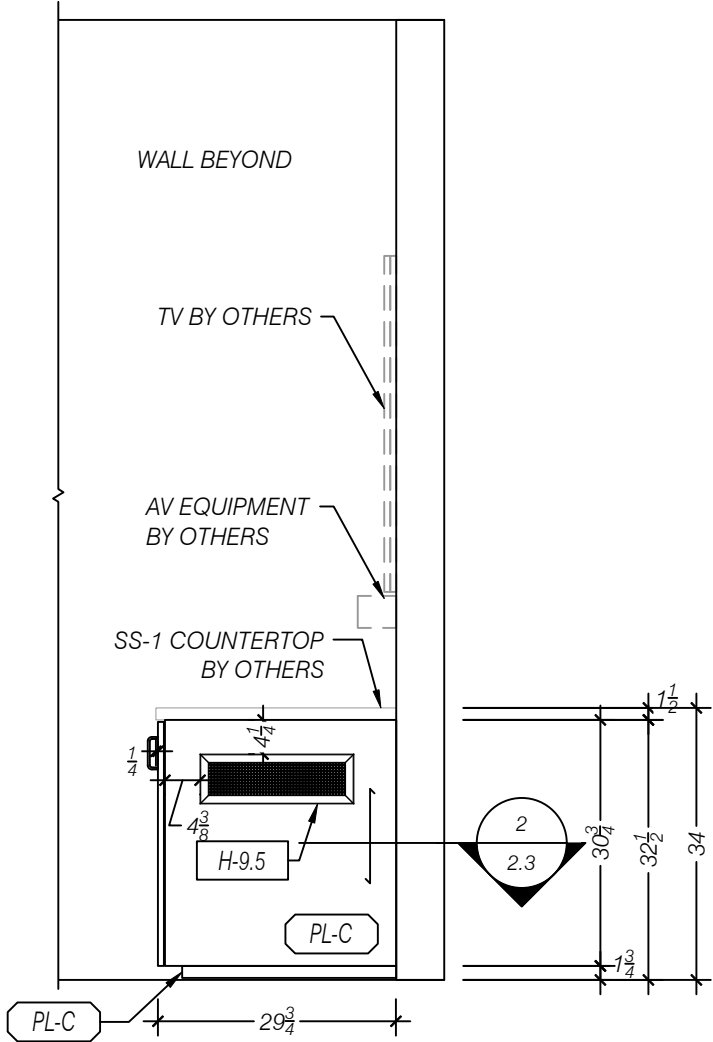

**2** ELEVATION WEST - CONFERENCE 102  
SCALE 1:24 (1/2" = 1'-0")  
ARCH REF: NA


**DGS SREOC COSTA  
MESA  
CONFERENCE 102**

| ISSUE        |                                       | BY        |
|--------------|---------------------------------------|-----------|
| DATE         | DESCRIPTION                           | Q-AS      |
| 05/05/2026   | REV-A FOR SUBMITTAL                   | -         |
| -            | -                                     | -         |
| -            | -                                     | -         |
| -            | -                                     | -         |
| -            | -                                     | -         |
| SITE ADDRESS |                                       |           |
| STREET       | 2301 South Shelley Circle Bldg. A & B |           |
| CITY         | Costa Mesa                            |           |
| STATE        | CA                                    | ZIP 92626 |
| JOB #:       | 26034                                 | REV: A    |
| MOD #:       | 2                                     | REL: N/A  |




**2.4**



5640 WEST END ROAD  
ARCATA, CA 95521  
PH (707) 822-4034 FAX (707) 822-5478  
WWW.CRESTMARKMILLWORK.COM

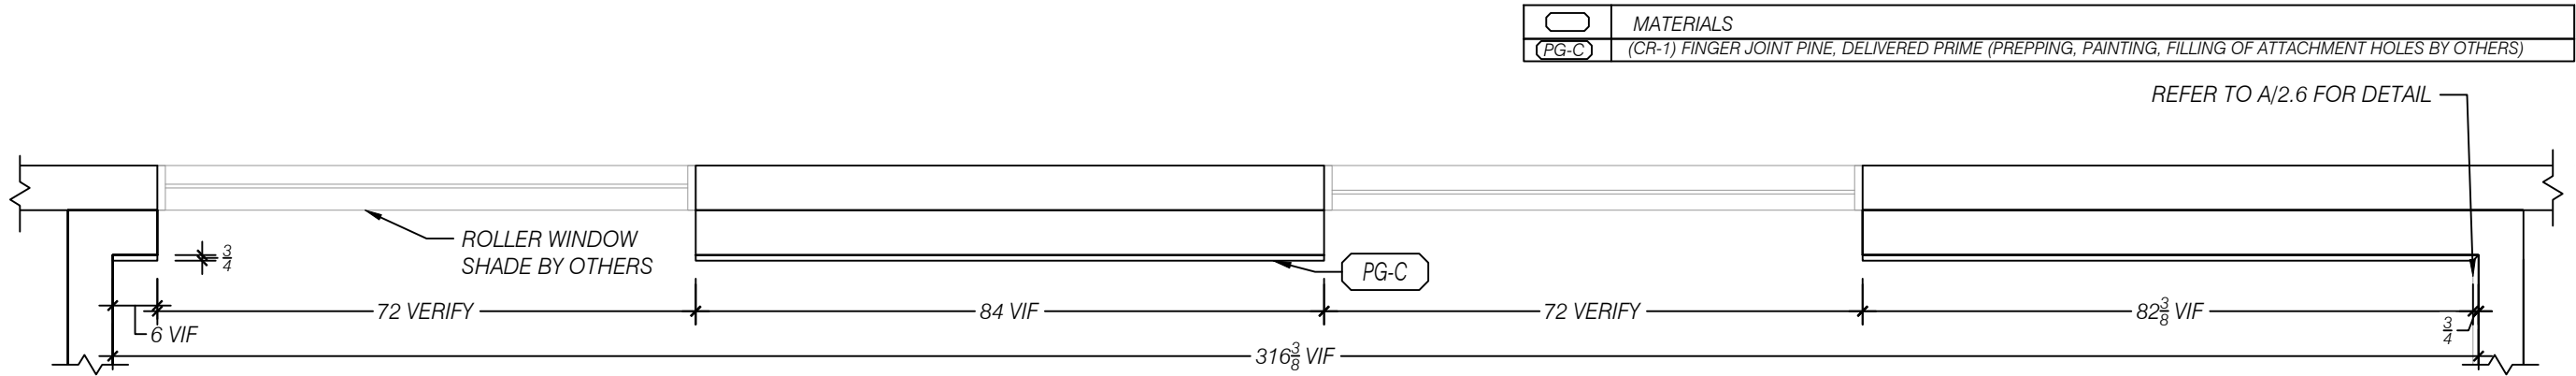

**1** PLAN - CONFERENCE 102  
SCALE 1:24 (1/2"=1'-0")  
ARCH REF: 1/AE406

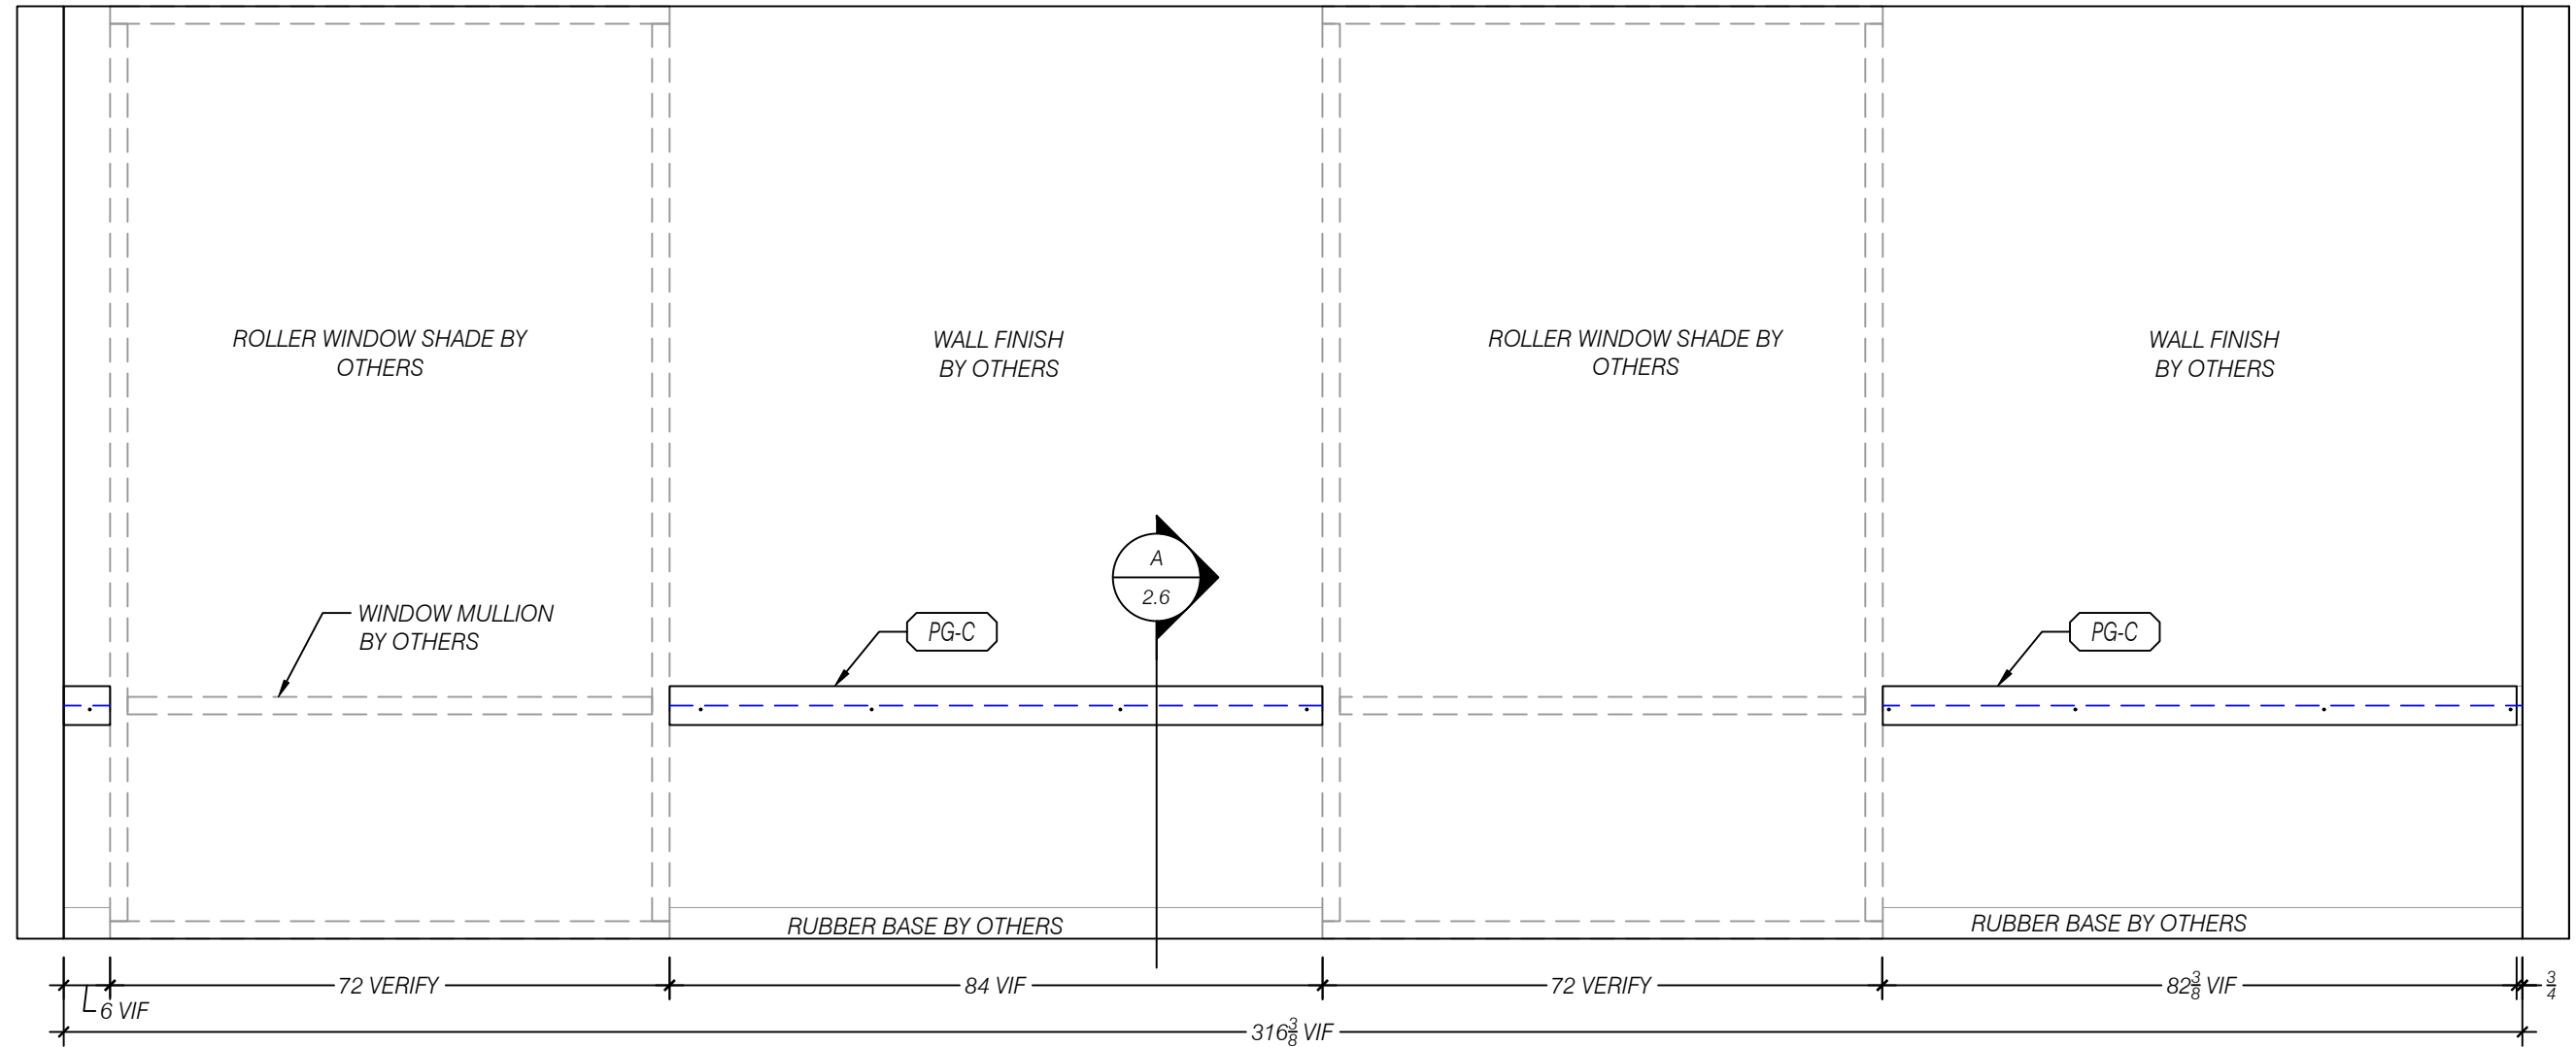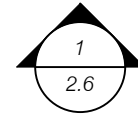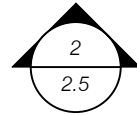

**2** ELEVATION EAST - CONFERENCE 102  
SCALE 1:24 (1/2"=1'-0")  
ARCH REF: 7/AE406




5640 WEST END ROAD  
ARCATA, CA 95521  
PH (707) 822-4034 FAX (707) 822-5478  
WWW.CRESTMARKMILLWORK.COM



**DGS SREOC COSTA  
MESA  
CONFERENCE 102**

| ISSUE        |                                       | BY        |
|--------------|---------------------------------------|-----------|
| DATE         | DESCRIPTION                           | Q-AS      |
| 05/05/2026   | REV-A FOR SUBMITTAL                   | -         |
| -            | -                                     | -         |
| -            | -                                     | -         |
| -            | -                                     | -         |
| -            | -                                     | -         |
| SITE ADDRESS |                                       |           |
| STREET       | 2301 South Shelley Circle Bldg. A & B |           |
| CITY         | Costa Mesa                            |           |
| STATE        | CA                                    | ZIP 92626 |
| JOB #:       | 26034                                 | REV: A    |
| MOD #:       | 2                                     | REL: N/A  |
| 2.5          |                                       |           |


|                                                                                     |   |
|-------------------------------------------------------------------------------------|---|
|  | MATERIALS                                                                                             |
|  | (CR-1) FINGER JOINT PINE, DELIVERED PRIME (PREPPING, PAINTING, FILLING OF ATTACHMENT HOLES BY OTHERS) |

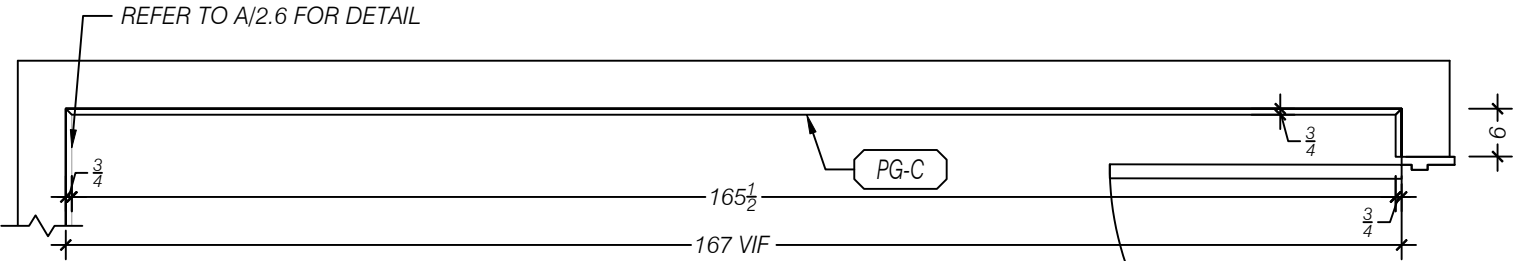

**1** PLAN - CONFERENCE 102  
SCALE 1:24 (1/2"=1'-0")  
ARCH REF: 1/AE406

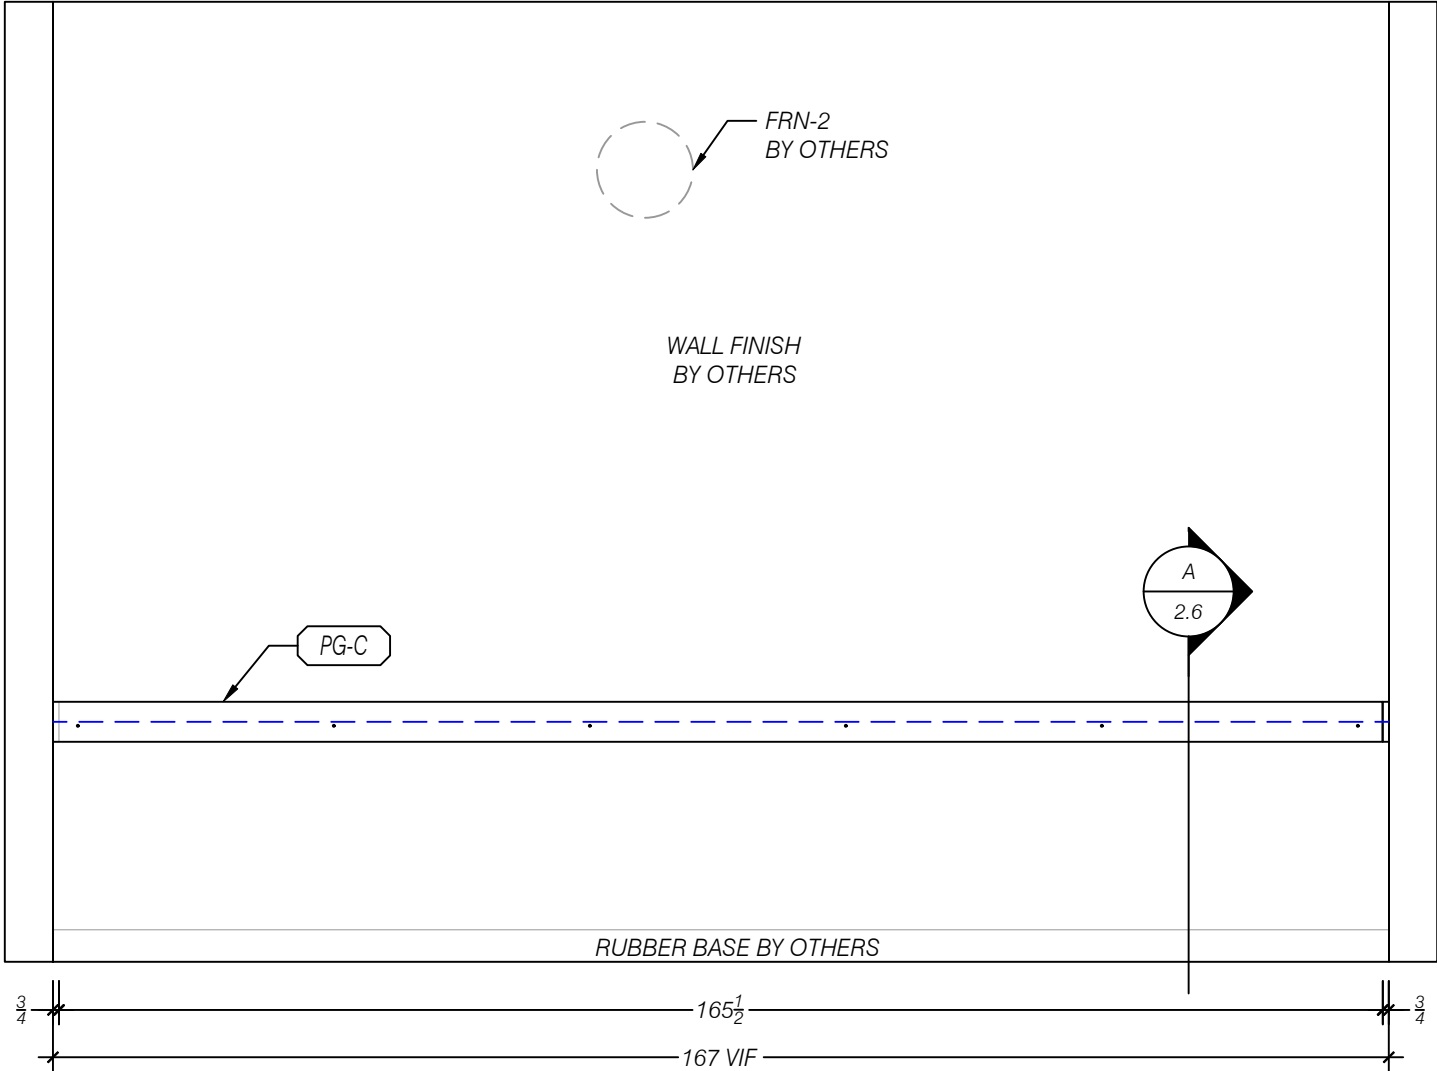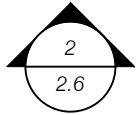

**2** ELEVATION SOUTH - CONFERENCE 102  
SCALE 1:24 (1/2"=1'-0")  
ARCH REF: 8/AE406

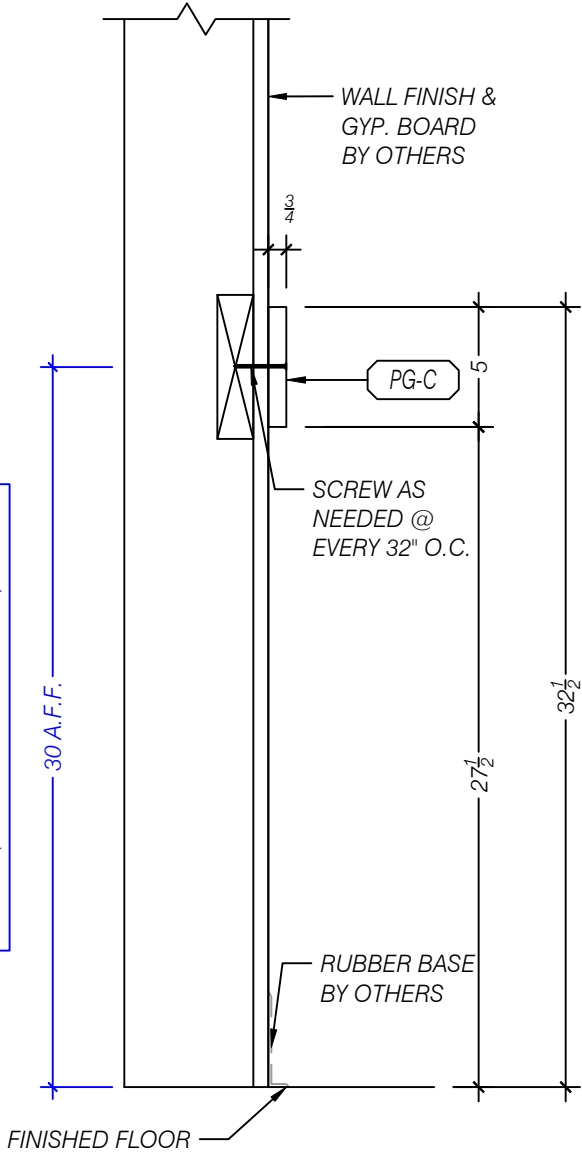


**A** SECTION - CHAIR RAIL  
SCALE 1:8 (1 1/2"=1'-0")  
ARCH REF: 3/AE585



5640 WEST END ROAD  
ARCATA, CA 95521  
PH (707) 822-4034 FAX (707) 822-5478  
WWW.CRESTMARKMILLWORK.COM

**DGS SREOC COSTA  
MESA  
CONFERENCE 102**

| ISSUE        |                                       | BY        |
|--------------|---------------------------------------|-----------|
| DATE         | DESCRIPTION                           |           |
| 05/05/2026   | REV-A FOR SUBMITTAL                   | Q-AS      |
| -            | -                                     | -         |
| -            | -                                     | -         |
| SITE ADDRESS |                                       |           |
| STREET       | 2301 South Shelley Circle Bldg. A & B |           |
| CITY         | Costa Mesa                            |           |
| STATE        | CA                                    | ZIP 92626 |
| JOB #:       | 26034                                 | REV: A    |
| MOD #:       | 2                                     | REL: N/A  |
| 2.6          |                                       |           |

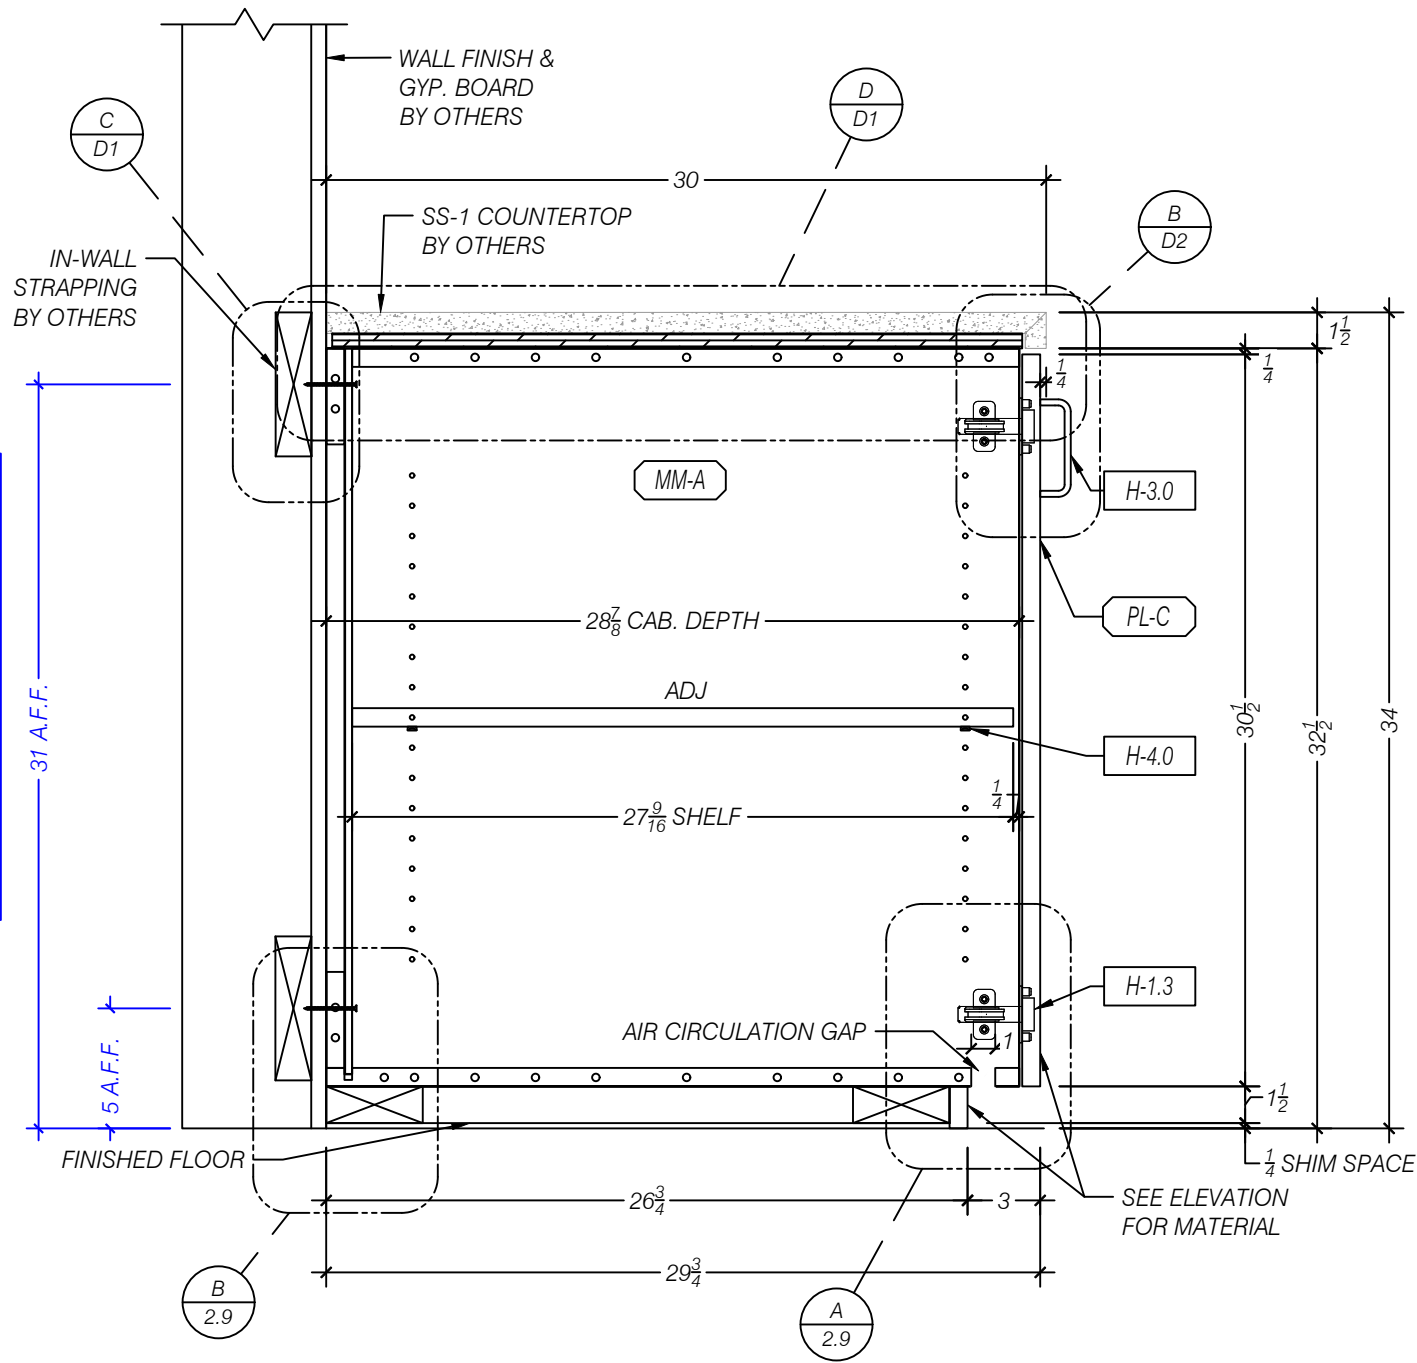

**A** SECTION - BASE CABINET  
SCALE 1:8 (1 1/2" = 1'-0")  
ARCH REF: 15/AE581

|             |                                                                      |                                                                                     |
|-------------|----------------------------------------------------------------------|-------------------------------------------------------------------------------------|
| <div></div> | MATERIALS                                                            |                                                                                     |
| (MM-A)      | WHITE MELAMINE                                                       |                                                                                     |
| (PL-C)      | (PL-1, WB-2) WILSONART "HARVEST MAPLE", 7953-38, FINE VELVET TEXTURE |                                                                                     |
| <div></div> | QTY. HARDWARE                                                        |                                                                                     |
| H-1.2       | X                                                                    | SALICE 0mm CLIP-ON HINGE PLATE EURO SCREW, BARGR09/16                               |
| H-1.3       | X                                                                    | SALICE 110° FO SOFT-CLOSE, LOGICA SILENTIA, C7J6AE9                                 |
| H-3.0       | X                                                                    | BERENSON WIRE PULL, BN6131-2SC-P, 96mm CTC, SATIN CHROME FINISH                     |
| H-4.0       | X                                                                    | HAFELE SHELF SUPPORT, 282.04.711, 5mm SHELF PIN, STEEL NICKEL-PLATED                |
| H-9.5       | X                                                                    | MOCKETT, GT-METAL AIR VENT GRILLE, 17"W x 4"H OPENING, MATTE BLACK FINISH W/ MESH/3 |




5640 WEST END ROAD  
ARCATA, CA 95521  
PH (707) 822-4034 FAX (707) 822-5478  
WWW.CRESTMARKMILLWORK.COM

**DGS SREOC COSTA  
MESA  
CONFERENCE 102**

| ISSUE      |                     | BY   |
|------------|---------------------|------|
| DATE       | DESCRIPTION         |      |
| 05/05/2026 | REV-A FOR SUBMITTAL | Q-AS |
| -          | -                   | -    |
| -          | -                   | -    |
| -          | -                   | -    |
| -          | -                   | -    |

| SITE ADDRESS |                                       |      |       |
|--------------|---------------------------------------|------|-------|
| STREET       | 2301 South Shelley Circle Bldg. A & B |      |       |
| CITY         | Costa Mesa                            |      |       |
| STATE        | CA                                    | ZIP  | 92626 |
| JOB #:       | 26034                                 | REV: | A     |
| MOD #:       | 2                                     | REL: | N/A   |

|        |      | MATERIALS                                                                           |
|--------|------|-------------------------------------------------------------------------------------|
| (MM-A) |      | WHITE MELAMINE                                                                      |
| (PL-C) |      | (PL-1, WB-2) WILSONART "HARVEST MAPLE", 7953-38, FINE VELVET TEXTURE                |
|        | QTY. | HARDWARE                                                                            |
| H-1.2  | X    | SALICE 0mm CLIP-ON HINGE PLATE EURO SCREW, BARGR09/16                               |
| H-1.3  | X    | SALICE 110° FO SOFT-CLOSE, LOGICA SILENTIA, C7J6AE9                                 |
| H-3.0  | X    | BERENSON WIRE PULL, BN6131-2SC-P, 96mm CTC, SATIN CHROME FINISH                     |
| H-4.0  | X    | HAFELE SHELF SUPPORT, 282.04.711, 5mm SHELF PIN, STEEL NICKEL-PLATED                |
| H-9.5  | X    | MOCKETT, GT-METAL AIR VENT GRILLE, 17"W x 4"H OPENING, MATTE BLACK FINISH W/ MESH/3 |

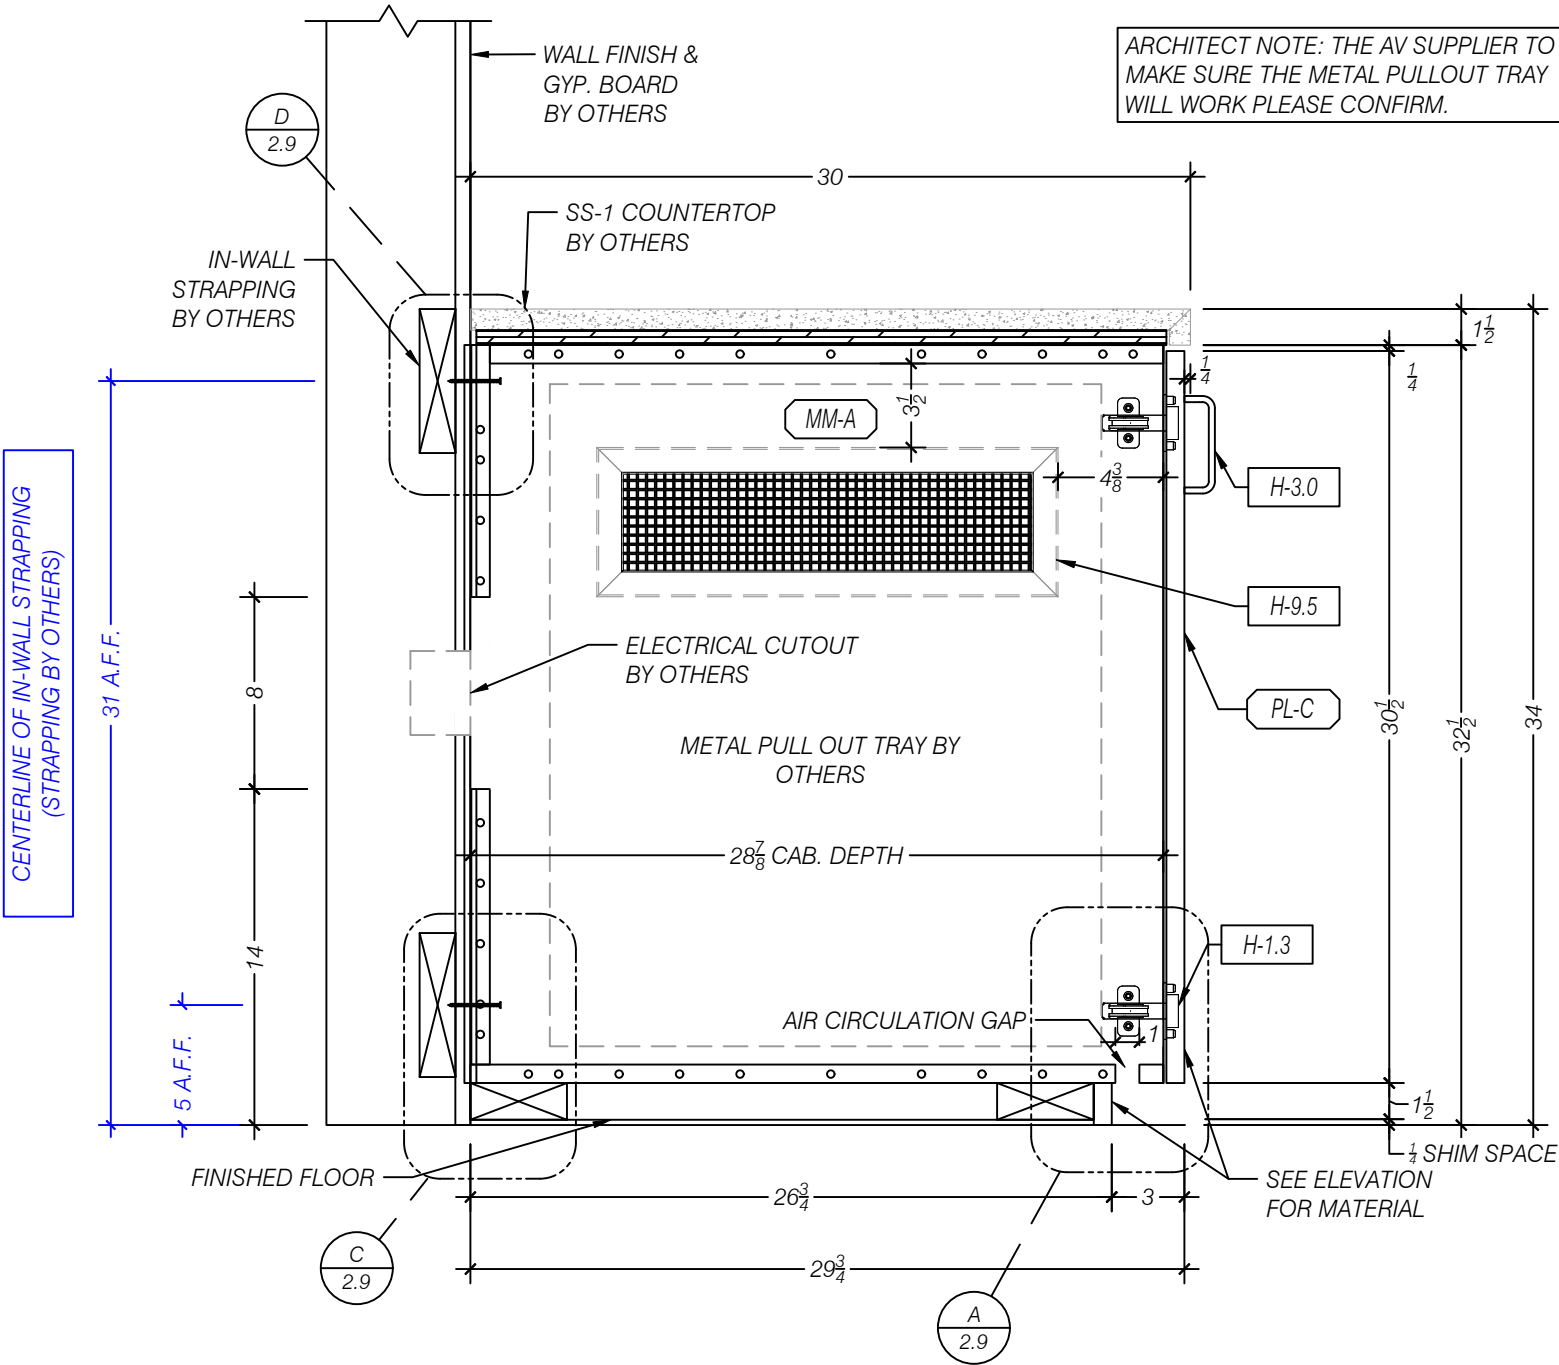

ARCHITECT NOTE: THE AV SUPPLIER TO MAKE SURE THE METAL PULLOUT TRAY WILL WORK PLEASE CONFIRM.

**A** SECTION - BASE CABINET  
SCALE 1:8 (1 1/2"=1'-0")  
ARCH REF: 10/AE581




5640 WEST END ROAD  
ARCATA, CA 95521  
PH (707) 822-4034 FAX (707) 822-5478  
WWW.CRESTMARKMILLWORK.COM

# DGS SREOC COSTA MESA CONFERENCE 102

| ISSUE      |                     | BY   |
|------------|---------------------|------|
| DATE       | DESCRIPTION         |      |
| 05/05/2026 | REV-A FOR SUBMITTAL | Q-AS |
| -          | -                   | -    |
| -          | -                   | -    |
| -          | -                   | -    |
| -          | -                   | -    |


| SITE ADDRESS |                                       |      |       |
|--------------|---------------------------------------|------|-------|
| STREET       | 2301 South Shelley Circle Bldg. A & B |      |       |
| CITY         | Costa Mesa                            |      |       |
| STATE        | CA                                    | ZIP  | 92626 |
| JOB #:       | 26034                                 | REV: | A     |
| MOD #:       | 2                                     | REL: | N/A   |

TYPICAL TOE KICK DETAILS SET TO INDUSTRY STANDARDS BY DEFAULT (U.O.N.)  
IF TOE IS SET TO SUB FLOOR, GC TO SPECIFY LOCATION OF LEVEL / CONTROL MARK  
TO BE USED, AND INSTALLER TO ADD FINISHED FLOOR THICKNESS  
TO FINISH OUT TOE AT SPECIFIED HEIGHT

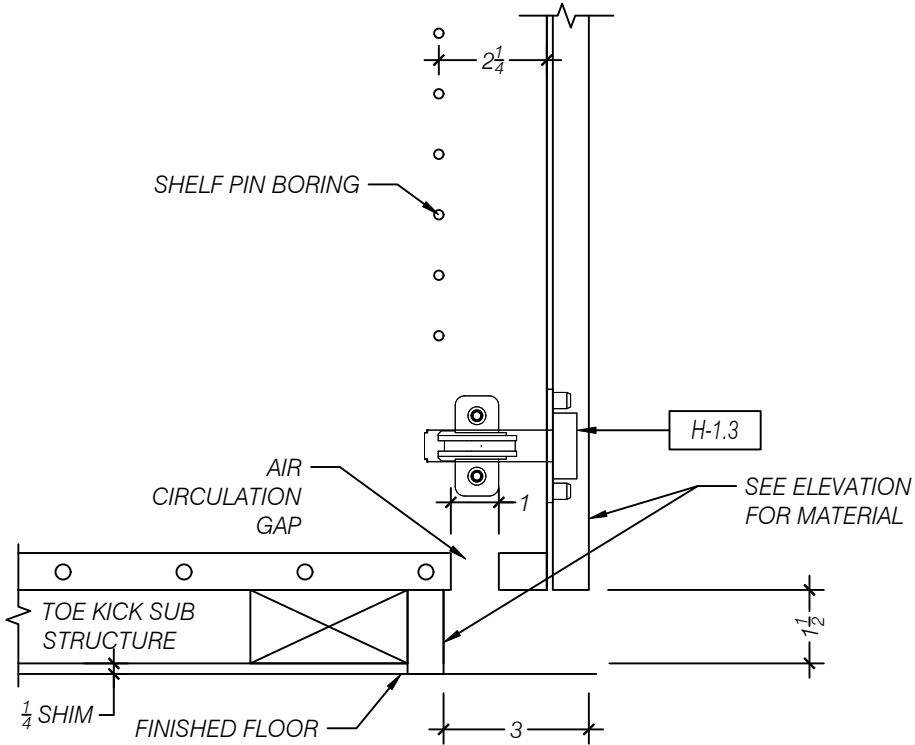


**A** ENLARGED DETAIL - TOE KICK FACE  
SCALE 1:4 (3"=1'-0")  
ARCH REF: 11/AE584

ALL IN-WALL BLOCKING AND SUPPORT BRACKET PROVIDED BY GC/OTHERS (U.O.N.)  
CRESTMARK TO PROVIDE BLOCKING/SUPPORT BRACKET HEIGHTS ONLY  
CRESTMARK IS NOT RESPONSIBLE FOR INCORRECT BLOCKING HEIGHTS SET BY GC  
OR CHANGES MADE BY ARCHITECT AFTER BLOCKING IS SET

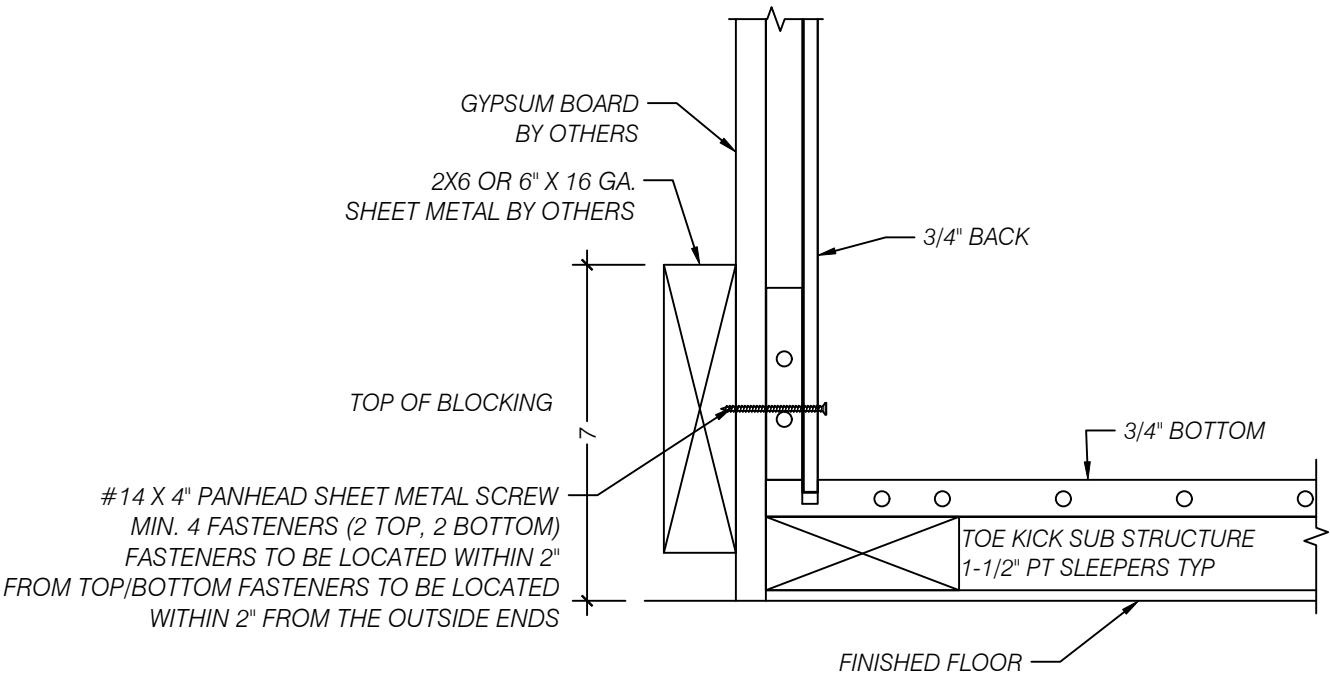


**C** ENLARGED DETAIL - THICK BACK CABINET ATTACHEMENT @ WALL  
SCALE 1:4 (3"=1'-0")  
ARCH REF: NA

ALL IN-WALL BLOCKING AND SUPPORT BRACKET PROVIDED BY GC/OTHERS (U.O.N.)  
CRESTMARK TO PROVIDE BLOCKING/SUPPORT BRACKET HEIGHTS ONLY  
CRESTMARK IS NOT RESPONSIBLE FOR INCORRECT BLOCKING HEIGHTS SET BY GC  
OR CHANGES MADE BY ARCHITECT AFTER BLOCKING IS SET

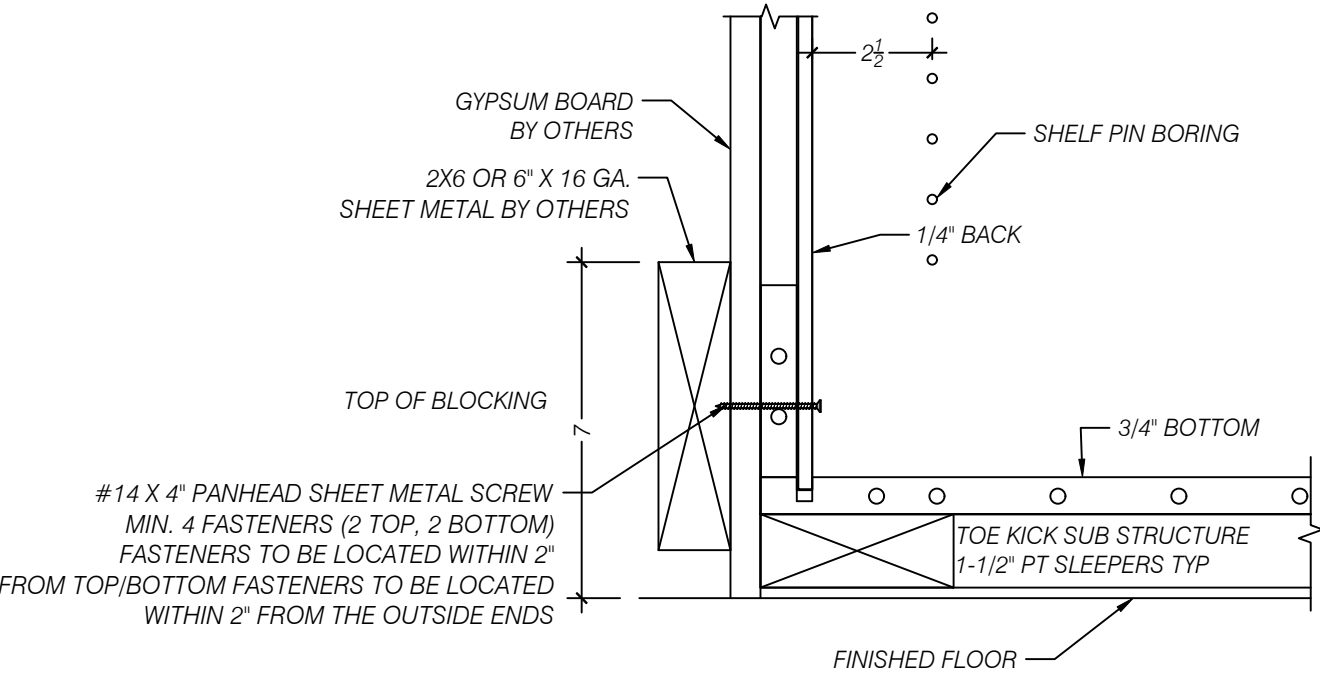

**B** ENLARGED DETAIL - BASE CABINET ATTACHEMENT @ WALL  
SCALE 1:4 (3"=1'-0")  
ARCH REF: NA

SHIMMING/SURFACE BLOCKING IS THE RESPONSIBILITY OF THE INSTALLER  
SURFACE BLOCKING/WALL CLEATS/Z-CLIPS WILL BE PROVIDED BY CRESTMARK (U.O.N.)  
CRESTMARK IS NOT RESPONSIBLE FOR GAPS DUE TO IRREGULAR WALL SURFACES  
IN THE EVENT OF EXTREME GAPS, A SURFACE MOUNT FLAT MOLDING WILL BE USED (U.O.N.)

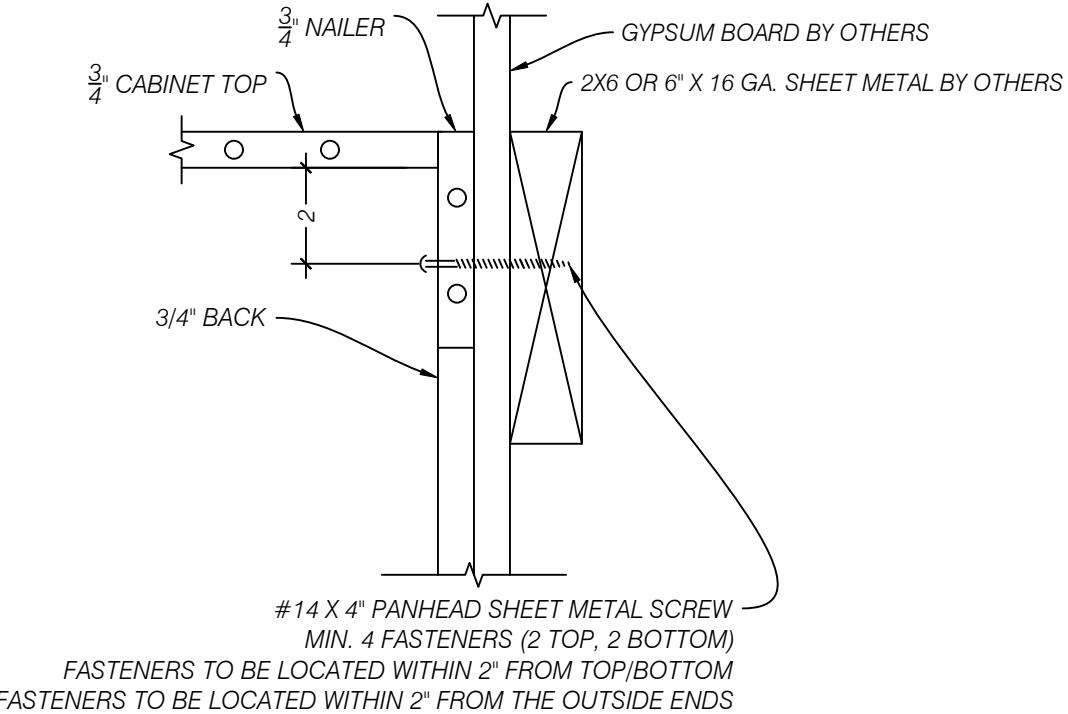


**D** ENLARGED DETAIL - THICK BACK CABINET ATTACHEMENT @ WALL  
SCALE 1:4 (3"=1'-0")  
ARCH REF: NA

**DGS SREOC COSTA**  
**MESA**  
**CONFERENCE 102**

| ISSUE | DESCRIPTION         | DATE       | BY   |  |  |  |  |
|-------|---------------------|------------|------|--|--|--|--|
|       |                     |            | Q-AS |  |  |  |  |
|       | REV-A FOR SUBMITTAL | 05/05/2026 |      |  |  |  |  |
|       |                     |            |      |  |  |  |  |
|       |                     |            |      |  |  |  |  |
|       |                     |            |      |  |  |  |  |
|       |                     |            |      |  |  |  |  |


| SITE ADDRESS |                                       |      |       |
|--------------|---------------------------------------|------|-------|
| STREET       | 2301 South Shelley Circle Bldg. A & B |      |       |
| CITY         | Costa Mesa                            |      |       |
| STATE        | CA                                    | ZIP  | 92626 |
| JOB #:       | 26034                                 | REV: | A     |
| MOD #:       | 2                                     | REL: | N/A   |

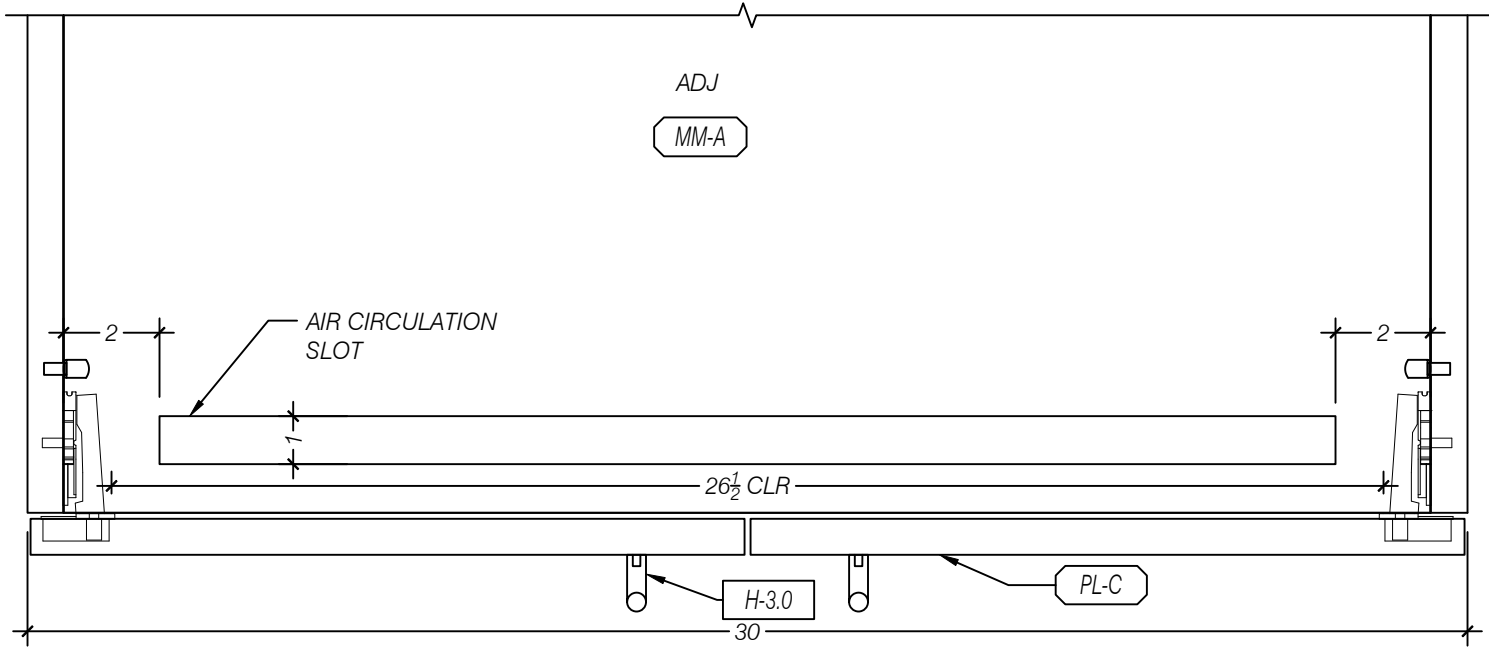

**A** ENLARGED DETAIL - AIR VENTILATION DETAIL  
SCALE 1:4 (3"=1'-0")  
ARCH REF: NA

DGS SREOC COSTA  
MESA  
CONFERENCE 102

| ISSUE        |                                       |      |       |     |
|--------------|---------------------------------------|------|-------|-----|
| DATE         | DESCRIPTION                           | BY   |       |     |
| 05/05/2026   | REV-A FOR SUBMITTAL                   | Q-AS |       |     |
| -            | -                                     | -    |       |     |
| -            | -                                     | -    |       |     |
| SITE ADDRESS |                                       |      |       |     |
| STREET       | 2301 South Shelley Circle Bldg. A & B |      |       |     |
| CITY         | Costa Mesa                            |      |       |     |
| STATE        | CA                                    | ZIP  | 92626 |     |
| JOB #:       | 26034                                 |      | REV:  | A   |
| MOD #:       | 2                                     |      | REL:  | N/A |
| 2.10         |                                       |      |       |     |

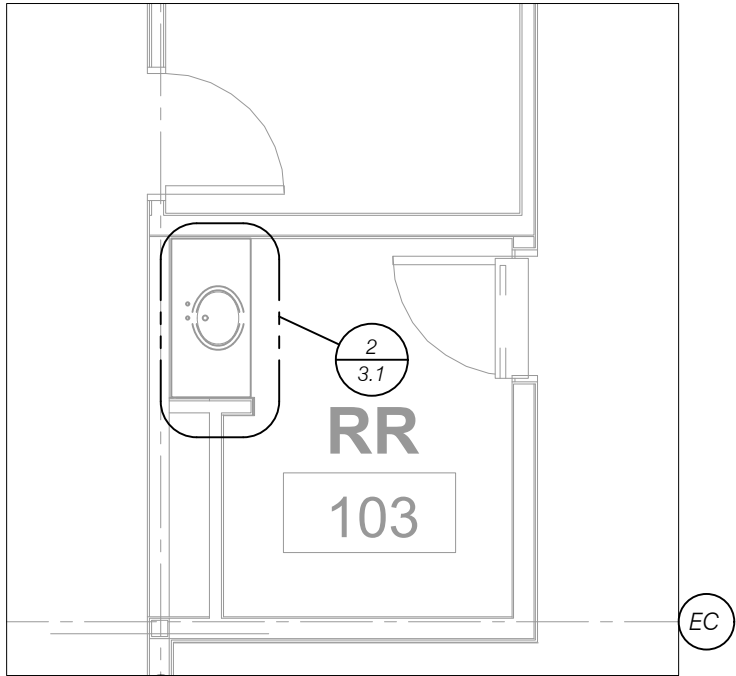


**1** KEY PLAN  
SCALE: NTS  
ARCH REF: 1/AE101.1


| NOTES |   |
|-------|---|
| 1     | ALL DIMENSIONS TO BE FIELD VERIFIED                                                                                          |
| 2     | GENERAL CONTRACTOR TO COORDINATE ALL FRAMING REQUIREMENTS WITH CMI                                                           |
| 3     | GENERAL CONTRACTOR TO COORDINATE ALL WALL TYPES, THICKNESSES AND ROUGH OPENINGS                                              |
| 4     | GENERAL CONTRACTOR & ELECTRICAL CONTRACTOR TO COORDINATE ALL ELECTRICAL BOX LOCATIONS & REQUIREMENTS WITH MILLWORK DRAWINGS  |
| 5     | GENERAL CONTRACTOR & ELECTRICAL CONTRACTOR TO COORDINATE ALL LIGHT FIXTURE FEED & SWITCHING LOCATIONS WITH MILLWORK DRAWINGS |
| 6     | GENERAL CONTRACTOR & PLUMBING CONTRACTOR TO COORDINATE ALL PLUMBING FIXTURES & INSTALLATION REQUIREMENTS                     |

| MATERIALS |                                                                      |
|-----------|----------------------------------------------------------------------|
| MM-A      | WHITE MELAMINE                                                       |
| PL-C      | (PL-1, WB-2) WILSONART "HARVEST MAPLE", 7953-38, FINE VELVET TEXTURE |
| HARDWARE  |                                                                      |
| H-1.2     | X SALICE 0mm CLIP-ON HINGE PLATE EURO SCREW, BARGR09/16              |
| H-1.3     | X SALICE 110° FO SOFT-CLOSE, LOGICA SILENTIA, C7J6AE9                |
| H-4.1.1   | X BRACKET, A&M CFLAT 21 (2.0)                                        |
| H-9.1     | X GRAINGER - GRAB CATCH - 4PE50, STEEL                               |


| PLUMBING SCHEDULE (BY OTHERS) |                   |                    |                 |                |
|-------------------------------|-------------------|--------------------|-----------------|----------------|
| ARCH. TAG                     | MAKE              | MODEL              | FINISH          | COMMENTS       |
| L-2                           | AMERICAN STANDARD | 9482               | WHITE           | SINK           |
| L-2                           | CHICAGO           | EQ - A11C - 11ABCP | POLISHED CHROME | FAUCET         |
| TA-5                          | SLOAN             | EAF - 200          | POLISHED CHROME | SOAP DISPENSER |

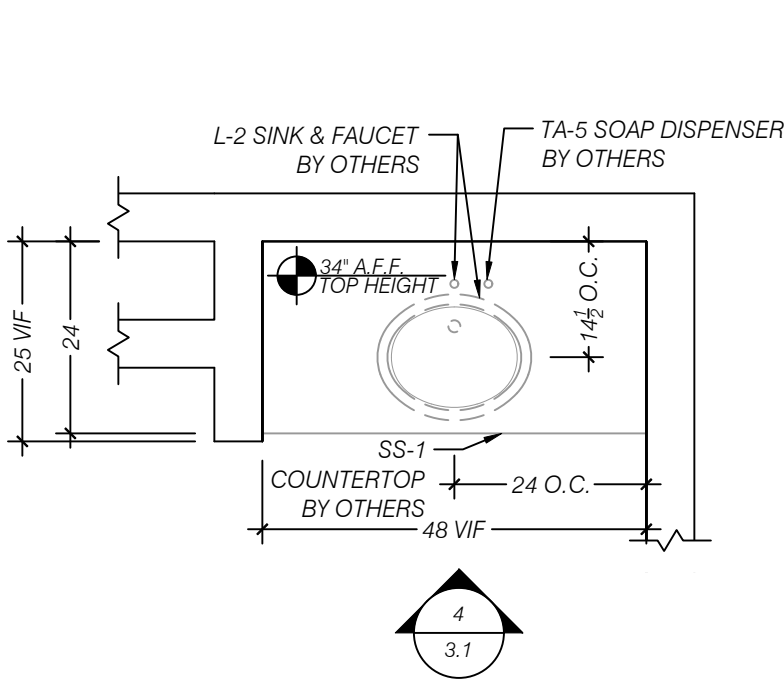

**2** PLAN - ALL GENDER 103  
SCALE 1:24 (1/2"=1'-0")  
ARCH REF: 4/AE402

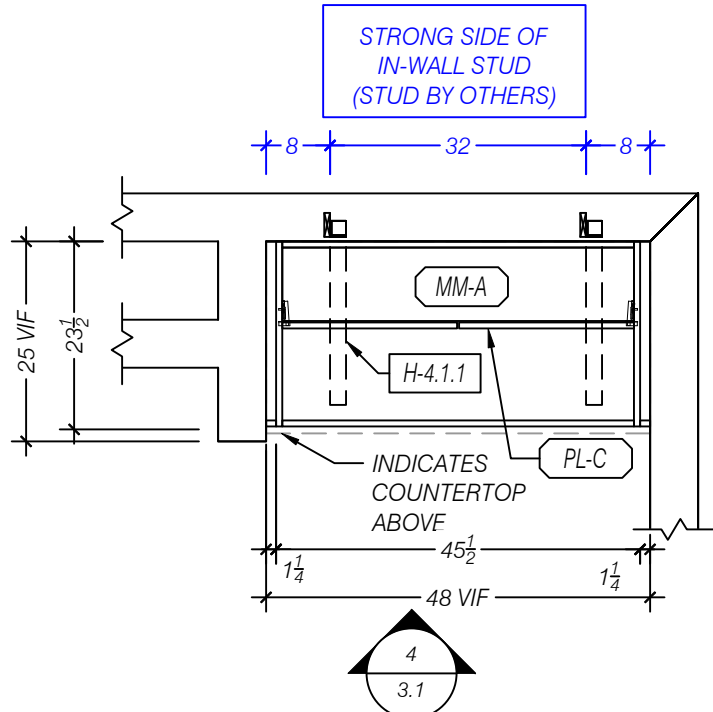

**3** PLAN SECTION - ALL GENDER 103  
SCALE 1:24 (1/2"=1'-0")  
ARCH REF: NA

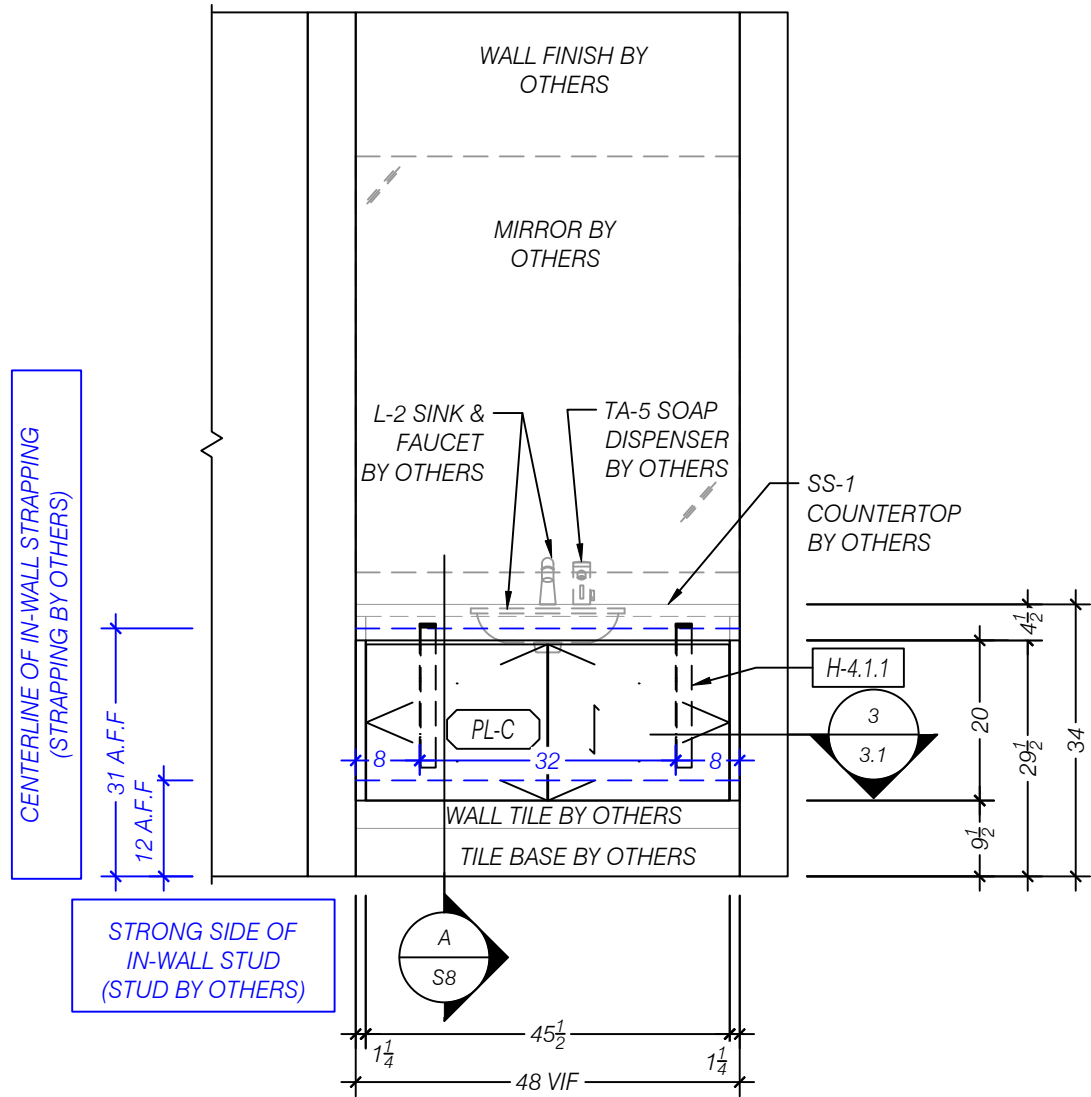

**4** ELEVATION WEST - ALL GENDER 103  
SCALE 1:24 (1/2"=1'-0")  
ARCH REF: 4/AE403




**DGS SREOC COSTA**  
**MESA**  
**ALL GENDER 103**

| ISSUE      |                     | BY   |
|------------|---------------------|------|
| DATE       | DESCRIPTION         | Q-AS |
| 05/05/2026 | REV-A FOR SUBMITTAL | -    |
| -          | -                   | -    |
| -          | -                   | -    |
| -          | -                   | -    |
| -          | -                   | -    |

| SITE ADDRESS |                                       |      |       |
|--------------|---------------------------------------|------|-------|
| STREET       | 2301 South Shelley Circle Bldg. A & B |      |       |
| CITY         | Costa Mesa                            |      |       |
| STATE        | CA                                    | ZIP  | 92626 |
| JOB #:       | 26034                                 | REV: | A     |
| MOD #:       | 3                                     | REL: | N/A   |




|                                                                                     |                                                                           |
|-------------------------------------------------------------------------------------|---------------------------------------------------------------------------|
|  | MATERIALS                                                                 |
| (MM-A)                                                                              | WHITE MELAMINE                                                            |
| (PL-C)                                                                              | (PL-1, WB-2) WILSONART "HARVEST MAPLE", 7953-38, FINE VELVET TEXTURE      |
|  | QTY. <b>HARDWARE</b>                                                      |
| H-1.2                                                                               | X    SAUCE 0mm CLIP-ON HINGE PLATE EURO SCREW, BARGR09/16                 |
| H-1.3                                                                               | X    SALICE 110° FO SOFT-CLOSE, LOGICA SILENTIA, C7J6AE9                  |
| H-3.0                                                                               | X    BERENSON WIRE PULL, BN6131-2SC-P, 96mm CTC, SATIN CHROME FINISH      |
| H-4.0                                                                               | X    HAFELE SHELF SUPPORT, 282.04.711, 5mm SHELF PIN, STEEL NICKEL-PLATED |
| H-5.5                                                                               | X    KITLOCK ELECTRONIC LOCKER LOCK, KL1100 RFID, BLACK FINISH            |

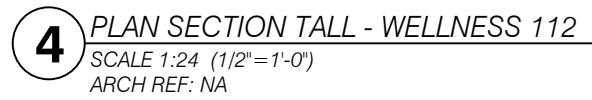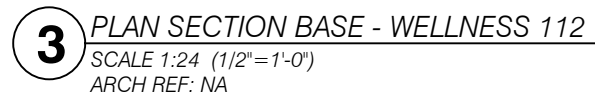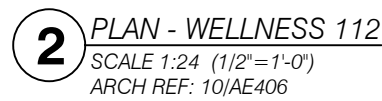

**DGS SREOC COSTA  
MESA  
WELLNESS 112**

| ISSUE               |                                       |       |       |     |
|---------------------|---------------------------------------|-------|-------|-----|
| DATE                | DESCRIPTION                           | BY    |       |     |
| 05/05/2026          | REV-A FOR SUBMITTAL                   | Q-AS  |       |     |
|                     |                                       |       |       |     |
|                     |                                       |       |       |     |
|                     |                                       |       |       |     |
|                     |                                       |       |       |     |
| <b>SITE ADDRESS</b> |                                       |       |       |     |
| STREET              | 2301 South Shelley Circle Bldg. A & B |       |       |     |
| CITY                | Costa Mesa                            |       |       |     |
| STATE               | CA                                    | ZIP   | 92626 |     |
| JOB #:              |                                       | 26034 | REV:  | A   |
| MOD #:              |                                       | 4     | REL:  | N/A |
| <b>4.1</b>          |                                       |       |       |     |

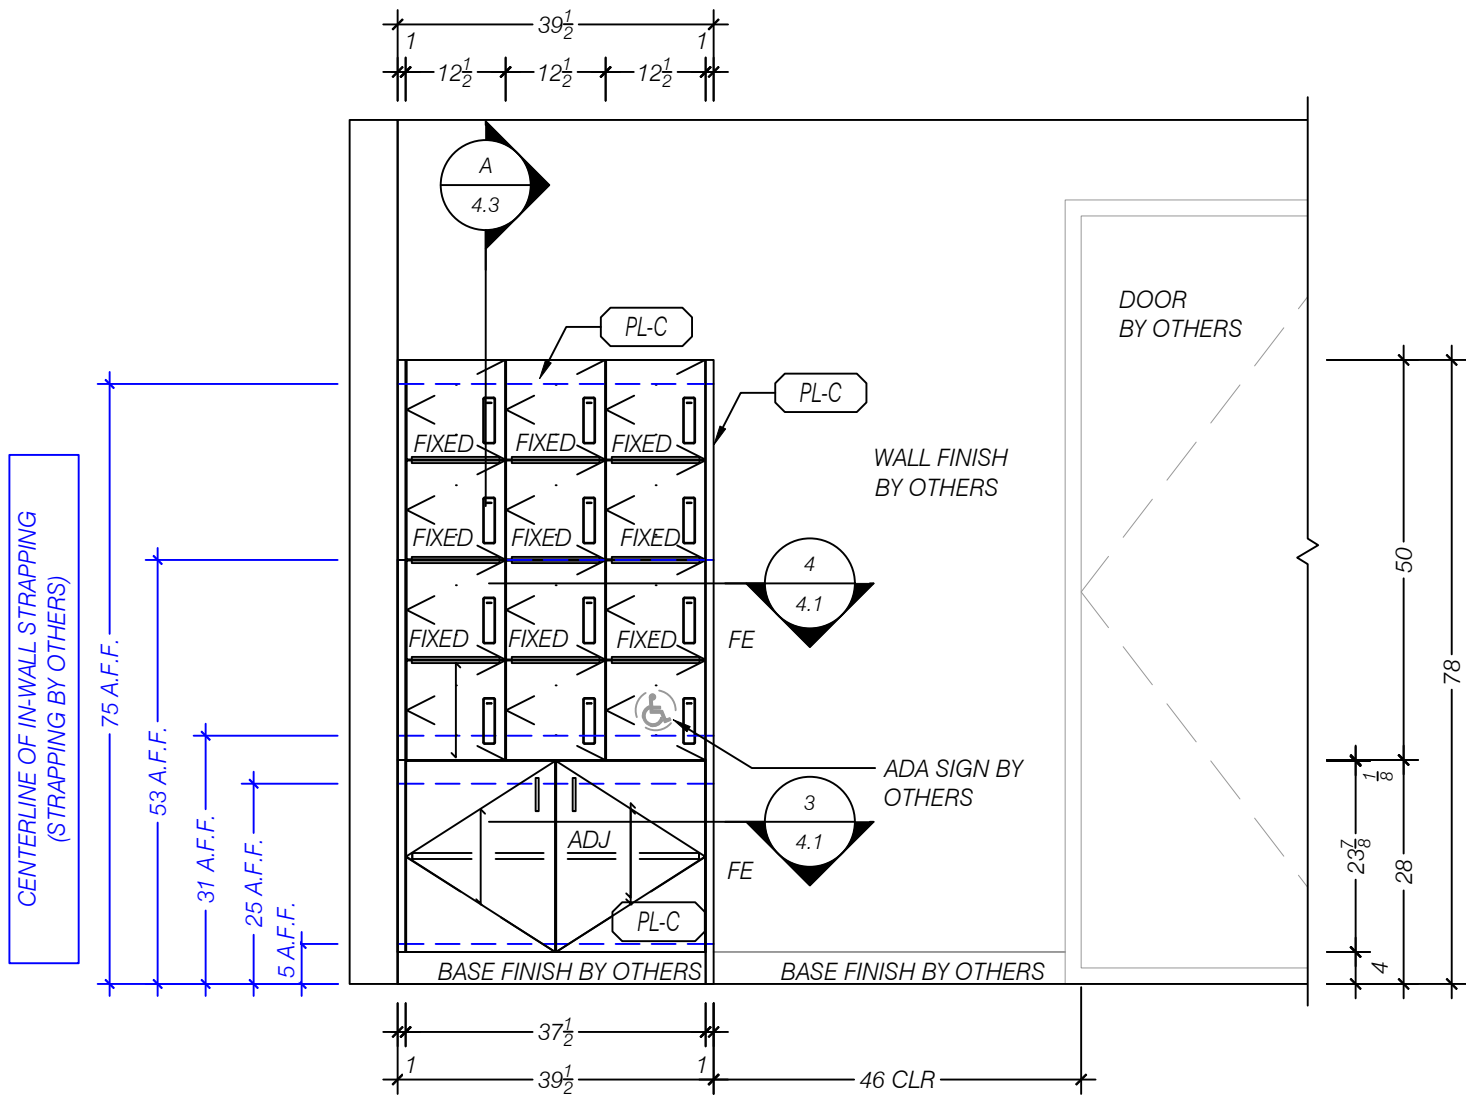

**1** ELEVATION NORTH - WELLNESS 112  
SCALE 1:24 (1/2" = 1'-0")  
ARCH REF: 11/AE406

|        |      | MATERIALS                                                            |
|--------|------|----------------------------------------------------------------------|
| (MM-A) |      | WHITE MELAMINE                                                       |
| (PL-C) |      | (PL-1, WB-2) WILSONART "HARVEST MAPLE", 7953-38, FINE VELVET TEXTURE |
|        | QTY. | HARDWARE                                                             |
| H-1.2  | X    | SALICE 0mm CLIP-ON HINGE PLATE EURO SCREW, BARGR09/16                |
| H-1.3  | X    | SALICE 110° FO SOFT-CLOSE, LOGICA SILENTIA, C7J6AE9                  |
| H-3.0  | X    | BERENSON WIRE PULL, BN6131-2SC-P, 96mm CTC, SATIN CHROME FINISH      |
| H-4.0  | X    | HAFELE SHELF SUPPORT, 282.04.711, 5mm SHELF PIN, STEEL NICKEL-PLATED |
| H-5.5  | X    | KITLOCK ELECTRONIC LOCKER LOCK, KL1100 RFID, BLACK FINISH            |



**DGS SREOC COSTA**  
**MESA**  
**WELLNESS 112**

| ISSUE        |                                       | BY        |
|--------------|---------------------------------------|-----------|
| DATE         | DESCRIPTION                           | Q-AS      |
| 05/05/2026   | REV-A FOR SUBMITTAL                   | -         |
| -            | -                                     | -         |
| -            | -                                     | -         |
| -            | -                                     | -         |
| -            | -                                     | -         |
| SITE ADDRESS |                                       |           |
| STREET       | 2301 South Shelley Circle Bldg. A & B |           |
| CITY         | Costa Mesa                            |           |
| STATE        | CA                                    | ZIP 92626 |
| JOB #:       | 26034                                 | REV: A    |
| MOD #:       | 4                                     | REL: N/A  |

**4.2**

|        |      | MATERIALS                                                            |
|--------|------|----------------------------------------------------------------------|
| (MM-A) |      | WHITE MELAMINE                                                       |
| (PL-C) |      | (PL-1, WB-2) WILSONART "HARVEST MAPLE", 7953-38, FINE VELVET TEXTURE |
|        | QTY. | HARDWARE                                                             |
| H-1.2  | X    | SALICE 0mm CLIP-ON HINGE PLATE EURO SCREW, BARGR09/16                |
| H-1.3  | X    | SALICE 110° FO SOFT-CLOSE, LOGICA SILENTIA, C7J6AE9                  |
| H-3.0  | X    | BERENSON WIRE PULL, BN6131-2SC-P, 96mm CTC, SATIN CHROME FINISH      |
| H-4.0  | X    | HAFELE SHELF SUPPORT, 282.04.711, 5mm SHELF PIN, STEEL NICKEL-PLATED |
| H-5.5  | X    | KITLOCK ELECTRONIC LOCKER LOCK, KL1100 RFID, BLACK FINISH            |



5640 WEST END ROAD  
ARCATA, CA 95521  
PH (707) 822-4034 FAX (707) 822-5478  
WWW.CRESTMILLWORK.COM


DGS SREOC COSTA  
MESA  
WELLNESS 112

| ISSUE | DESCRIPTION         | BY   |
|-------|---------------------|------|
|       | REV-A FOR SUBMITTAL | Q-AS |
| DATE  | 05/05/2026          |      |
|       |                     |      |
|       |                     |      |
|       |                     |      |



| SITE ADDRESS |                                       |      |       |
|--------------|---------------------------------------|------|-------|
| STREET       | 2301 South Shelley Circle Bldg. A & B |      |       |
| CITY         | Costa Mesa                            |      |       |
| STATE        | CA                                    | ZIP  | 92626 |
| JOB #:       | 26034                                 | REV: | A     |
| MOD #:       | 4                                     | REL: | N/A   |

4.3

© CRESTMILLWORK, INC.

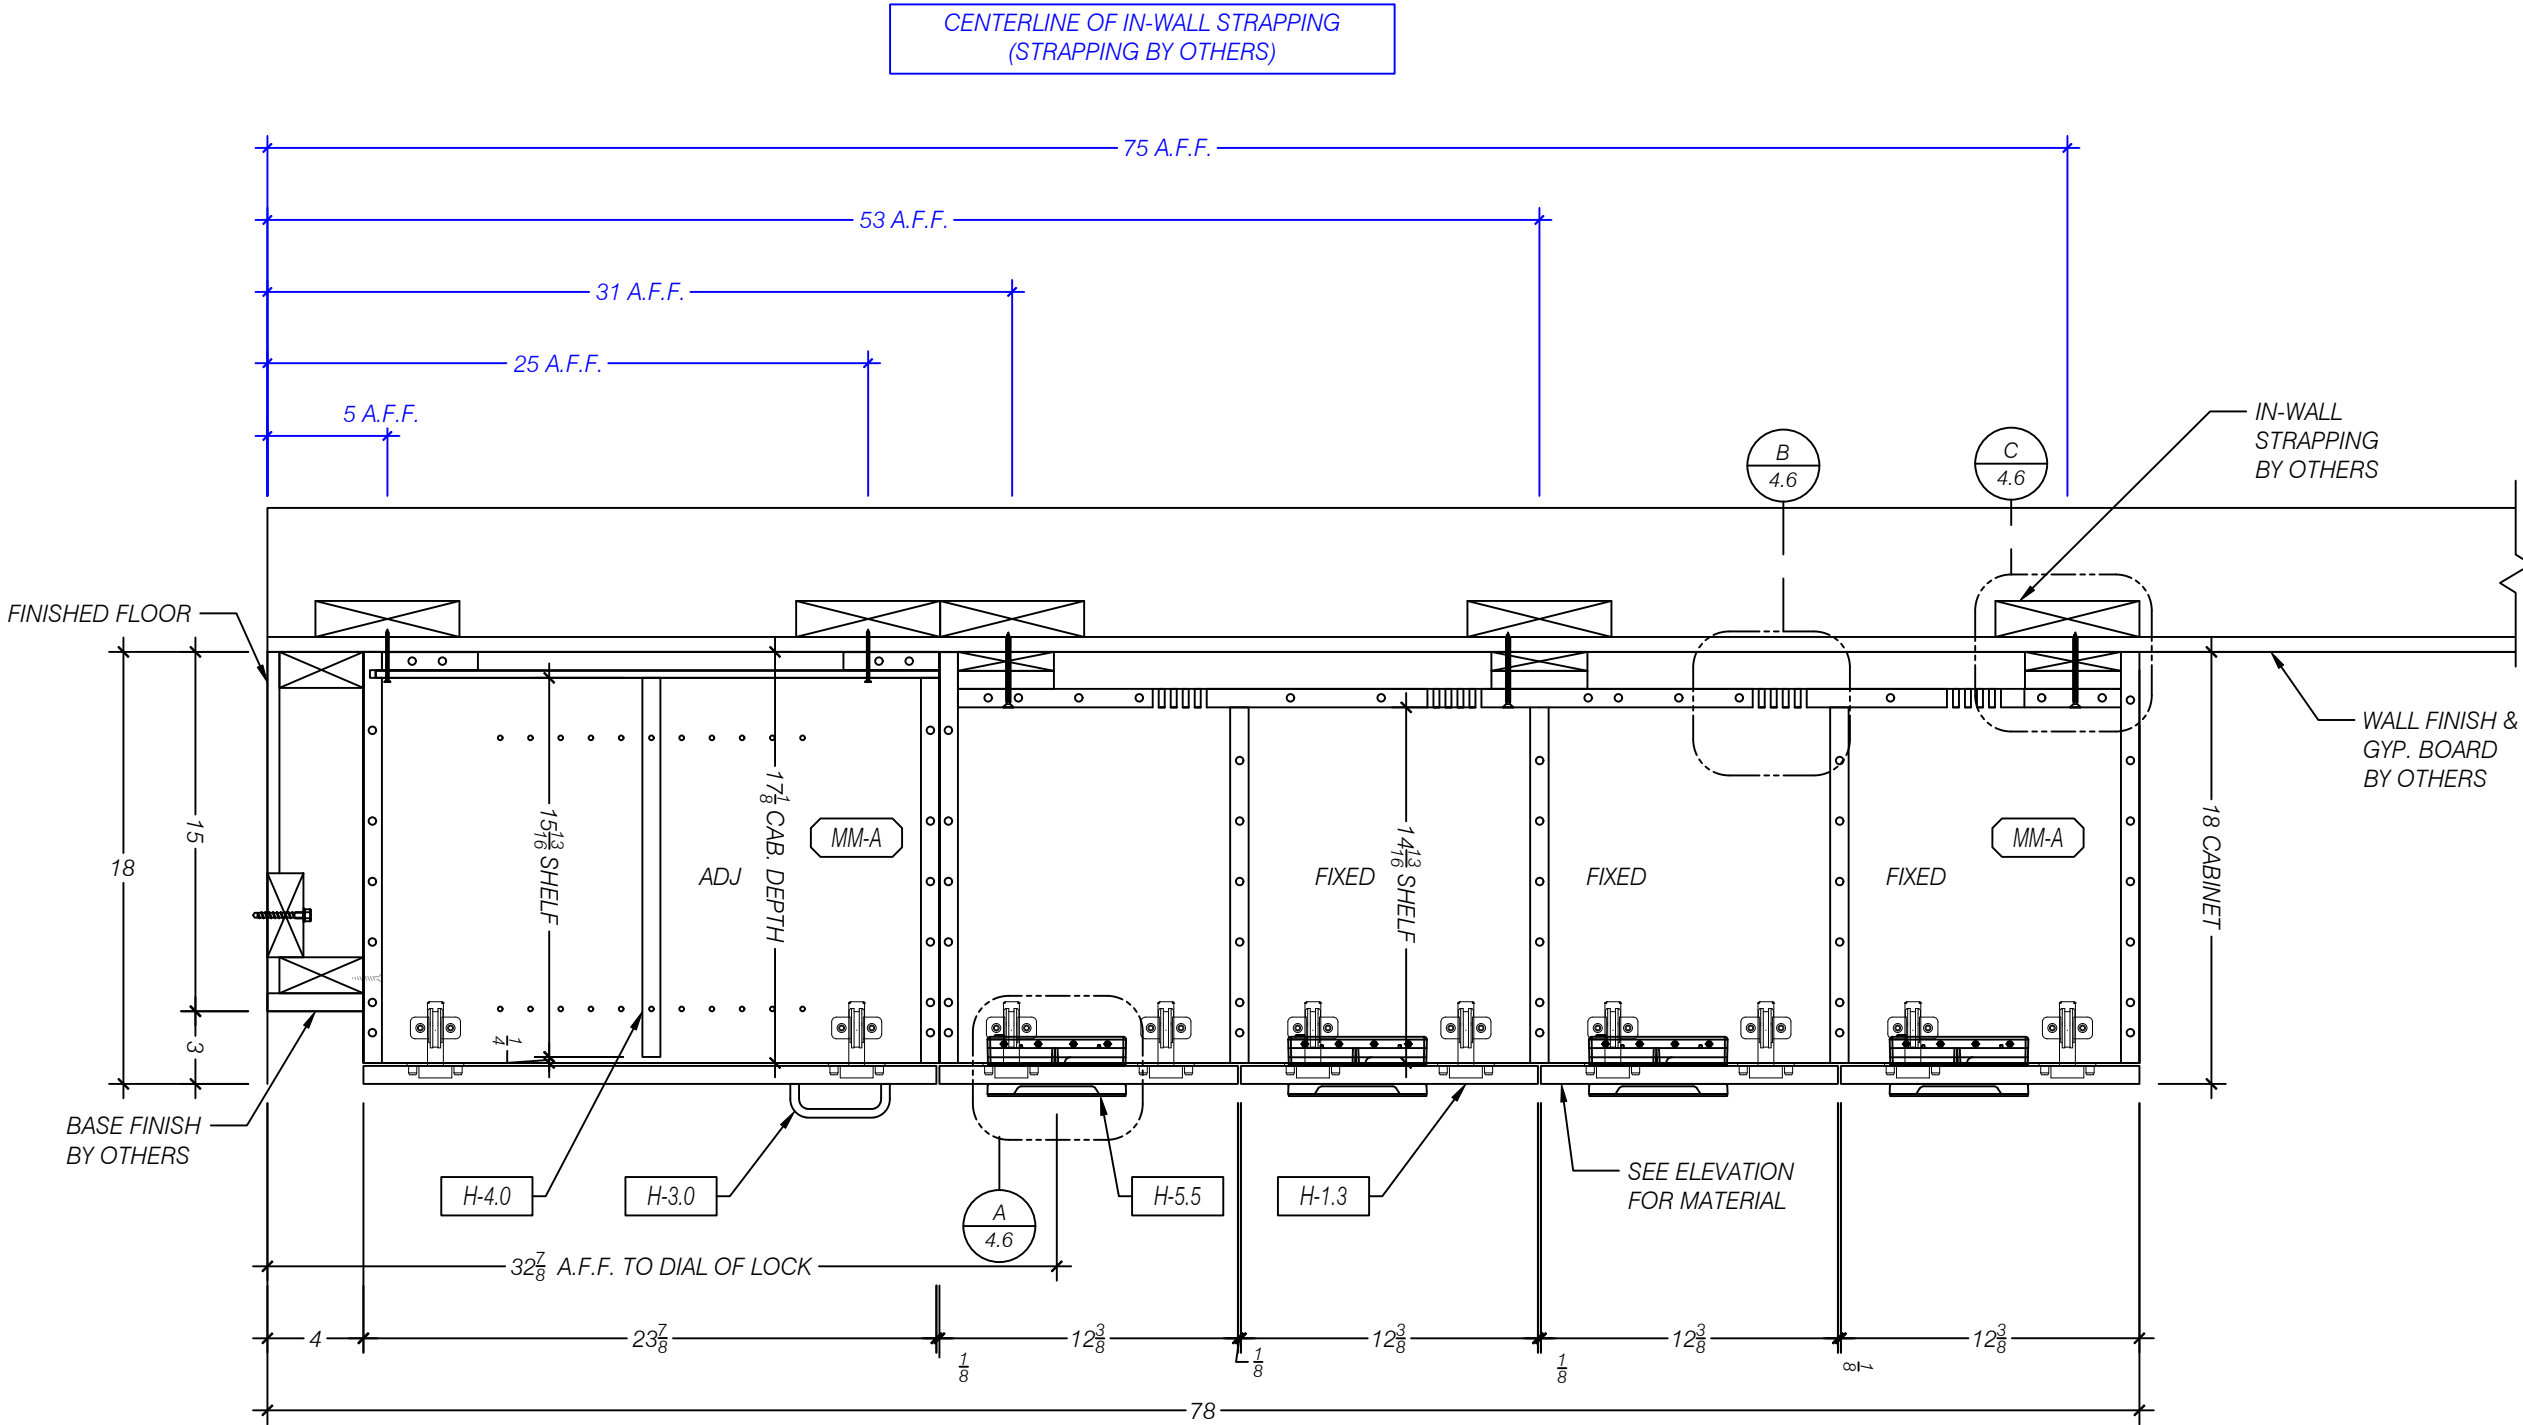


**A** SECTION - TALL CABINET  
SCALE 1:8 (1 1/2"=1'-0")  
ARCH REF: 22/AE582

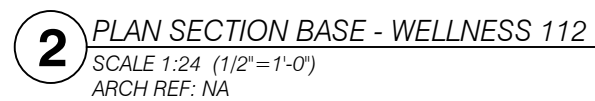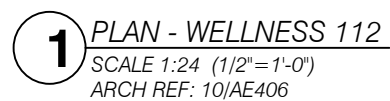


| PLUMBING SCHEDULE (BY OTHERS) |         |                  |                 |                |
|-------------------------------|---------|------------------|-----------------|----------------|
| ARCH. TAG                     | MAKE    | MODEL            | FINISH          | COMMENTS       |
| HS-1                          | ELKAY   | D11515           | POLISHED CHROME | SINK           |
| HS-1                          | CHICAGO | #2302-GN8AE3ABCP | POLISHED CHROME | FAUCET         |
| TA-5                          | SLOAN   | EAF - 200        | POLISHED CHROME | SOAP DISPENSER |

| ISSUE        |                                       |       |          |
|--------------|---------------------------------------|-------|----------|
| DATE         | DESCRIPTION                           | BY    |          |
| 05/05/2026   | REV-A FOR SUBMITTAL                   | Q-AS  |          |
|              |                                       |       |          |
|              |                                       |       |          |
| SITE ADDRESS |                                       |       |          |
| STREET       | 2301 South Shelley Circle Bldg. A & B |       |          |
| CITY         | Costa Mesa                            |       |          |
| STATE        | CA                                    | ZIP   | 92626    |
| JOB #:       |                                       | 26034 | REV: A   |
| MOD #:       |                                       | 4     | REL: N/A |
| 4.4          |                                       |       |          |



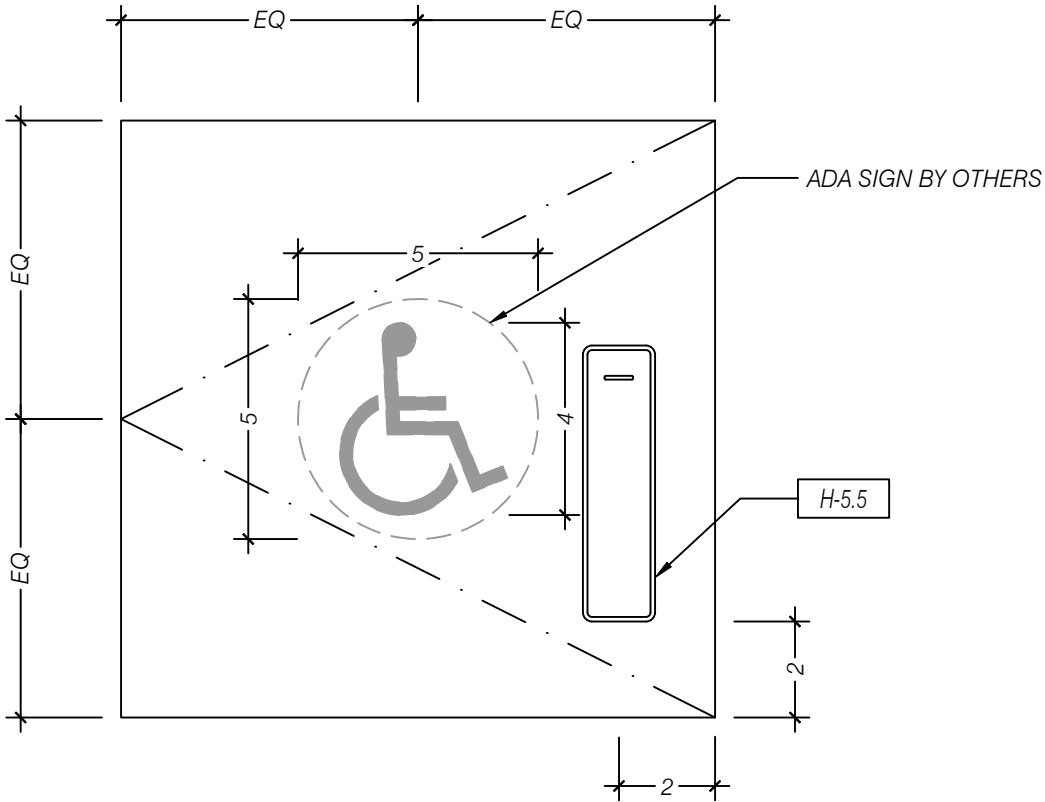


**A** ENLARGED DETAIL - LOCK LOCATION  
SCALE 1:4 (3"=1'-0")  
ARCH REF: NA

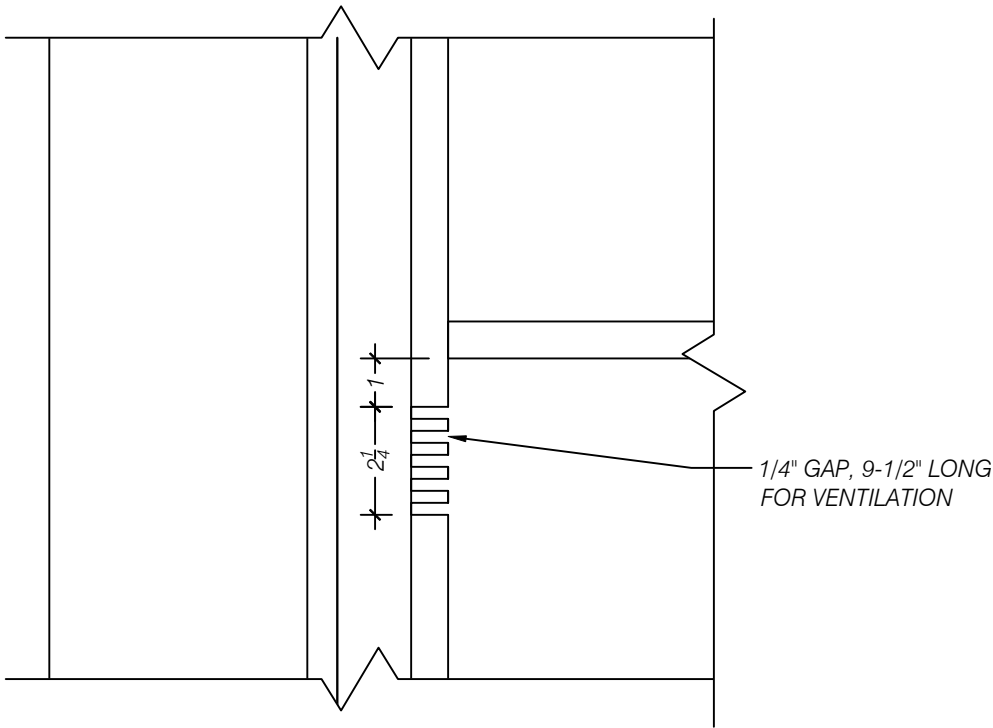

**B** ENLARGED DETAIL - LOCKER VENTILATION  
SCALE 1:4 (3"=1'-0")  
ARCH REF: NA

|         |      | MATERIALS                                                            |
|---------|------|----------------------------------------------------------------------|
| (MM-A)  |      | WHITE MELAMINE                                                       |
| (PL-C)  |      | (PL-1, WB-2) WILSONART "HARVEST MAPLE", 7953-38, FINE VELVET TEXTURE |
|         | QTY. | HARDWARE                                                             |
| H-1.2   | X    | SALICE 0mm CLIP-ON HINGE PLATE EURO SCREW, BARGR09/16                |
| H-1.3   | X    | SALICE 110° FO SOFT-CLOSE, LOGICA SILENTIA, C7J6AE9                  |
| H-4.1.1 | X    | BRACKET, A&M CFLAT 21 (2.0)                                          |
| H-9.1   | X    | GRAINGER - GRAB CATCH - 4PE50, STEEL                                 |

SHIMMING/SURFACE BLOCKING IS THE RESPONSIBILITY OF THE INSTALLER  
SURFACE BLOCKING/WALL CLEATS/Z-CLIPS WILL BE PROVIDED BY CRESTMARK (U.O.N.)  
CRESTMARK IS NOT RESPONSIBLE FOR GAPS DUE TO IRREGULAR WALL SURFACES  
IN THE EVENT OF EXTREME GAPS, A SURFACE MOUNT FLAT MOLDING WILL BE USED (U.O.N.)

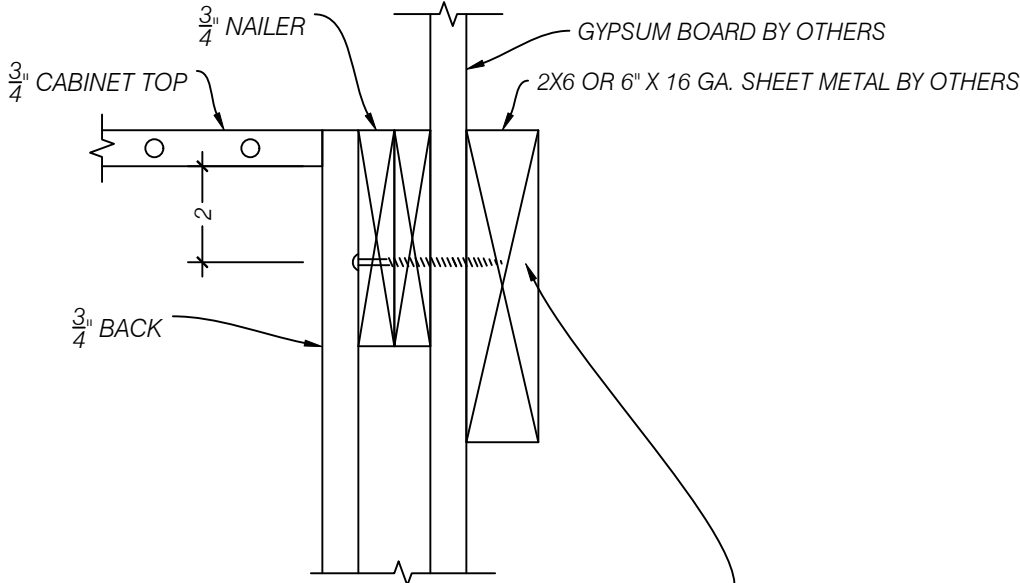

#14 X 4" PANHEAD SHEET METAL SCREW  
MIN. 4 FASTENERS (2 TOP, 2 BOTTOM)  
FASTENERS TO BE LOCATED WITHIN 2" FROM TOP/BOTTOM  
FASTENERS TO BE LOCATED WITHIN 2" FROM THE OUTSIDE ENDS


**C** ENLARGED DETAIL - LOCKER CABINET ATTACHMENT @ WALL  
SCALE 1:4 (3"=1'-0")  
ARCH REF: NA

DGS SREOC COSTA

MESA

WELLNESS 112


| ISSUE        |                                       | BY   |       |   |   |   |   |
|--------------|---------------------------------------|------|-------|---|---|---|---|
| DATE         | DESCRIPTION                           | Q-AS |       |   |   |   |   |
| 05/05/2026   | REV-A FOR SUBMITTAL                   | -    | -     | - | - | - | - |
|              |                                       |      |       |   |   |   |   |
|              |                                       |      |       |   |   |   |   |
|              |                                       |      |       |   |   |   |   |
|              |                                       |      |       |   |   |   |   |
| SITE ADDRESS |                                       |      |       |   |   |   |   |
| STREET       | 2301 South Shelley Circle Bldg. A & B |      |       |   |   |   |   |
| CITY         | Costa Mesa                            |      |       |   |   |   |   |
| STATE        | CA                                    | ZIP  | 92626 |   |   |   |   |
| JOB #:       | 26034                                 | REV: | A     |   |   |   |   |
| MOD #:       | 4                                     | REL: | N/A   |   |   |   |   |

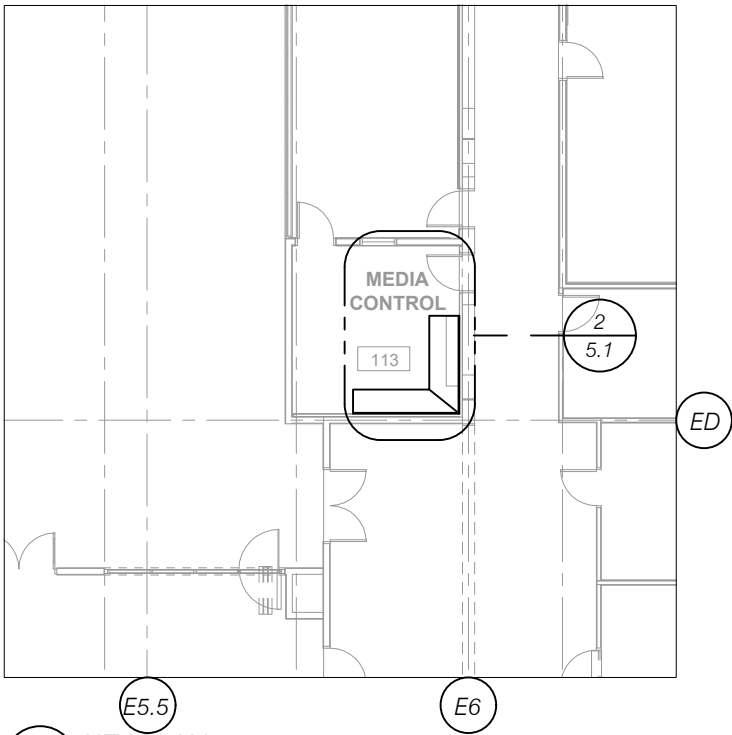


**1** KEY PLAN  
SCALE : NTS  
ARCH REF: 1/AE101.1

| NOTES |   |
|-------|---|
| 1     | ALL DIMENSIONS TO BE FIELD VERIFIED                                                                                          |
| 2     | GENERAL CONTRACTOR TO COORDINATE ALL FRAMING REQUIREMENTS WITH CMI                                                           |
| 3     | GENERAL CONTRACTOR TO COORDINATE ALL WALL TYPES, THICKNESSES AND ROUGH OPENINGS                                              |
| 4     | GENERAL CONTRACTOR & ELECTRICAL CONTRACTOR TO COORDINATE ALL ELECTRICAL BOX LOCATIONS & REQUIREMENTS WITH MILLWORK DRAWINGS  |
| 5     | GENERAL CONTRACTOR & ELECTRICAL CONTRACTOR TO COORDINATE ALL LIGHT FIXTURE FEED & SWITCHING LOCATIONS WITH MILLWORK DRAWINGS |
| 6     | GENERAL CONTRACTOR & PLUMBING CONTRACTOR TO COORDINATE ALL PLUMBING FIXTURES & INSTALLATION REQUIREMENTS                     |

|         |   | MATERIALS                                                                   |
|---------|---|-----------------------------------------------------------------------------|
| MM-A    |   | WHITE MELAMINE                                                              |
| PL-A    |   | WHITE CAB LINER                                                             |
| PL-D    |   | (PL-2) PIONITE "FOLKSTONE GRAY", SG241-SD, TEXTURED/SUEDE FINISH            |
| PL-E    |   | (PL-3) WILSONART "WHITE", 1570-60, FINE VELVET TEXTURE 1570-38              |
| PL-F    |   | (PL-4) WILSONART "CARBON MESH", 4880-38, FINE VELVET TEXTURE                |
| QTY.    |   | HARDWARE                                                                    |
| H-1.2   | X | SALICE 0mm CLIP-ON HINGE PLATE EURO SCREW, BARGR09/16                       |
| H-1.3   | X | SALICE 110° FO SOFT-CLOSE, LOGICA SILENTIA, C7J6AE9                         |
| H-2.0   | X | KNAPE & VOGT DRAWER SLIDES, KV8400, SIDE MOUNT, FULL EXT. 100lb LOAD RATING |
| H-2.1   | X | KNAPE & VOGT DRAWER SLIDES, KV8600, SIDE MOUNT, FULL EXT. 150lb LOAD RATING |
| H-3.0   | X | BERENSON WIRE PULL, BN6131-2SC-P, 96mm CTC, SATIN CHROME FINISH             |
| H-4.0   | X | HAFELE SHELF SUPPORT, 282.04.711, 5mm SHELF PIN, STEEL NICKEL-PLATED        |
| H-4.1.1 | X | BRACKET, A&M CFLAT 21 (2.0)                                                 |
| H-4.1.2 | X | BRACKET, A&M CFLAT 24 (2.0)                                                 |
| H-7.0   | X | 1/8" x 1-1/4" x 1-1/4" ALUMINUM L-ANGLE, MILL FINISH                        |

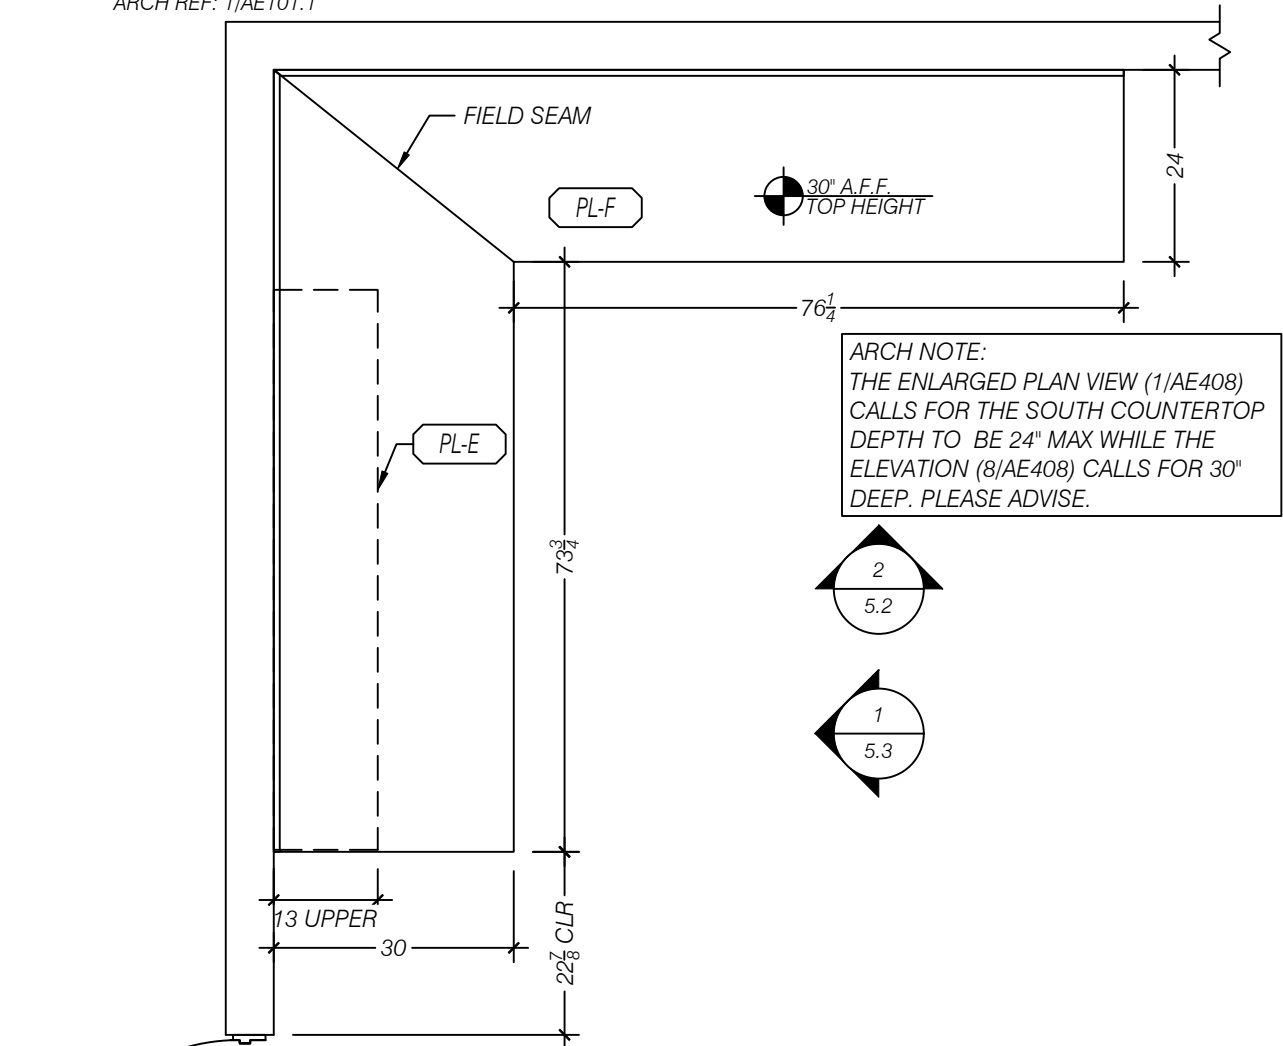

**2** PLAN - MEDIA CONTROL 113  
SCALE 1:24 (1/2"=1'-0")  
ARCH REF: 1/AE408

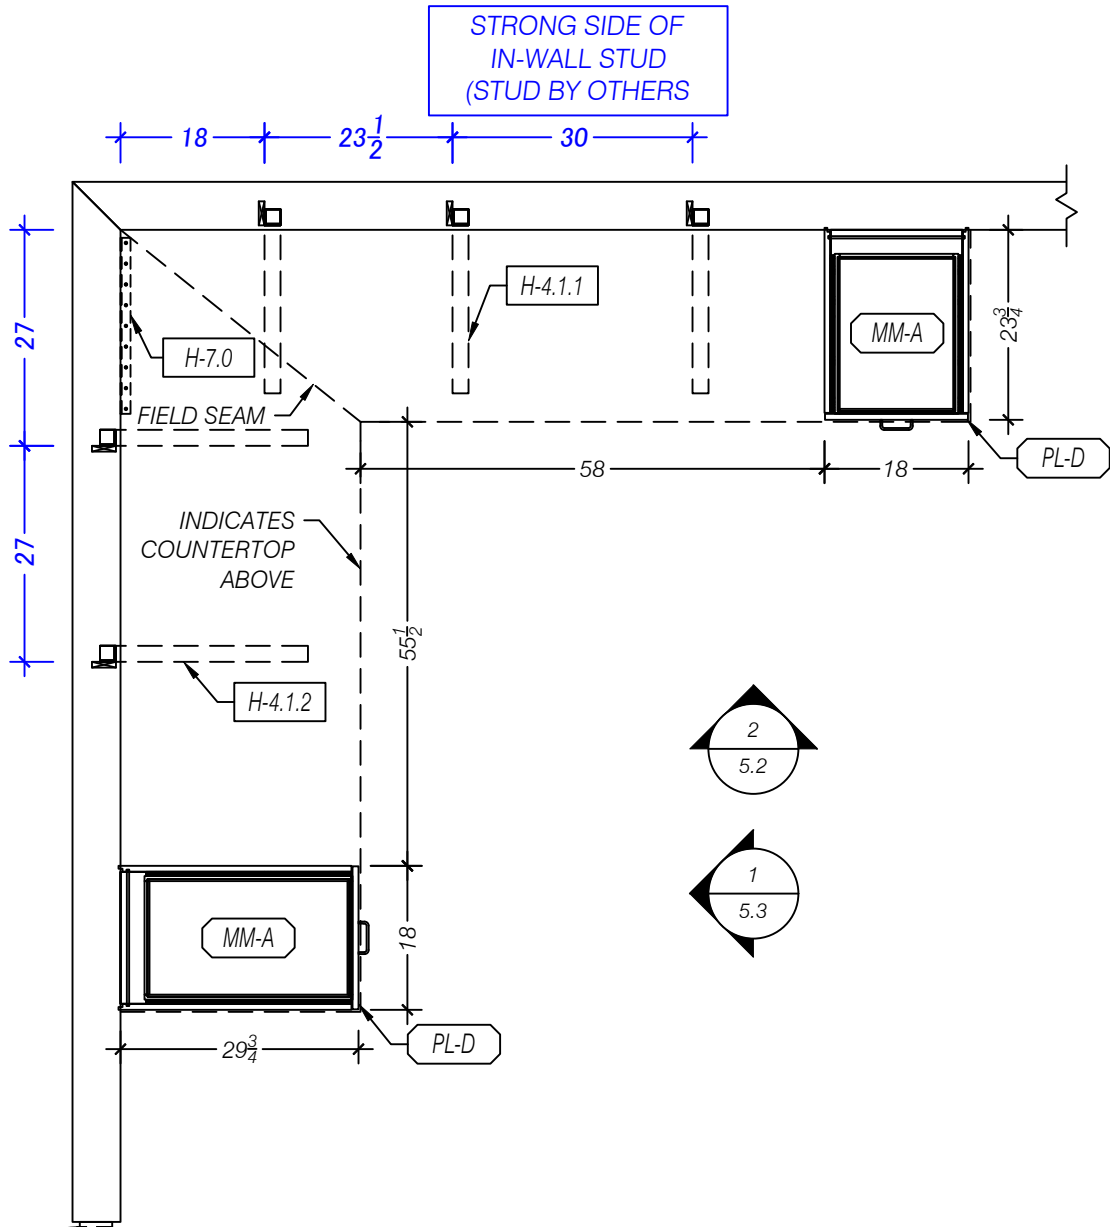


**3** PLAN SECTION BASE - MEDIA CONTROL 113  
SCALE 1:24 (1/2"=1'-0")  
ARCH REF: NA

**DGS SREOC COSTA**  
**MESA**  
**MEDIA CONTROL 113**


| ISSUE | DESCRIPTION        | DATE       | BY   |   |   |   |   |
|-------|--------------------|------------|------|---|---|---|---|
|       |                    |            | Q-AS |   |   |   |   |
|       | REVA FOR SUBMITTAL | 05/05/2026 | -    | - | - | - | - |
|       |                    |            | -    | - | - | - | - |
|       |                    |            | -    | - | - | - | - |
|       |                    |            | -    | - | - | - | - |
|       |                    |            | -    | - | - | - | - |

| SITE ADDRESS |                                       |      |       |
|--------------|---------------------------------------|------|-------|
| STREET       | 2301 South Shelley Circle Bldg. A & B |      |       |
| CITY         | Costa Mesa                            |      |       |
| STATE        | CA                                    | ZIP  | 92626 |
| JOB #:       | 26034                                 | REV: | A     |
| MOD #:       | 5                                     | REL: | N/A   |

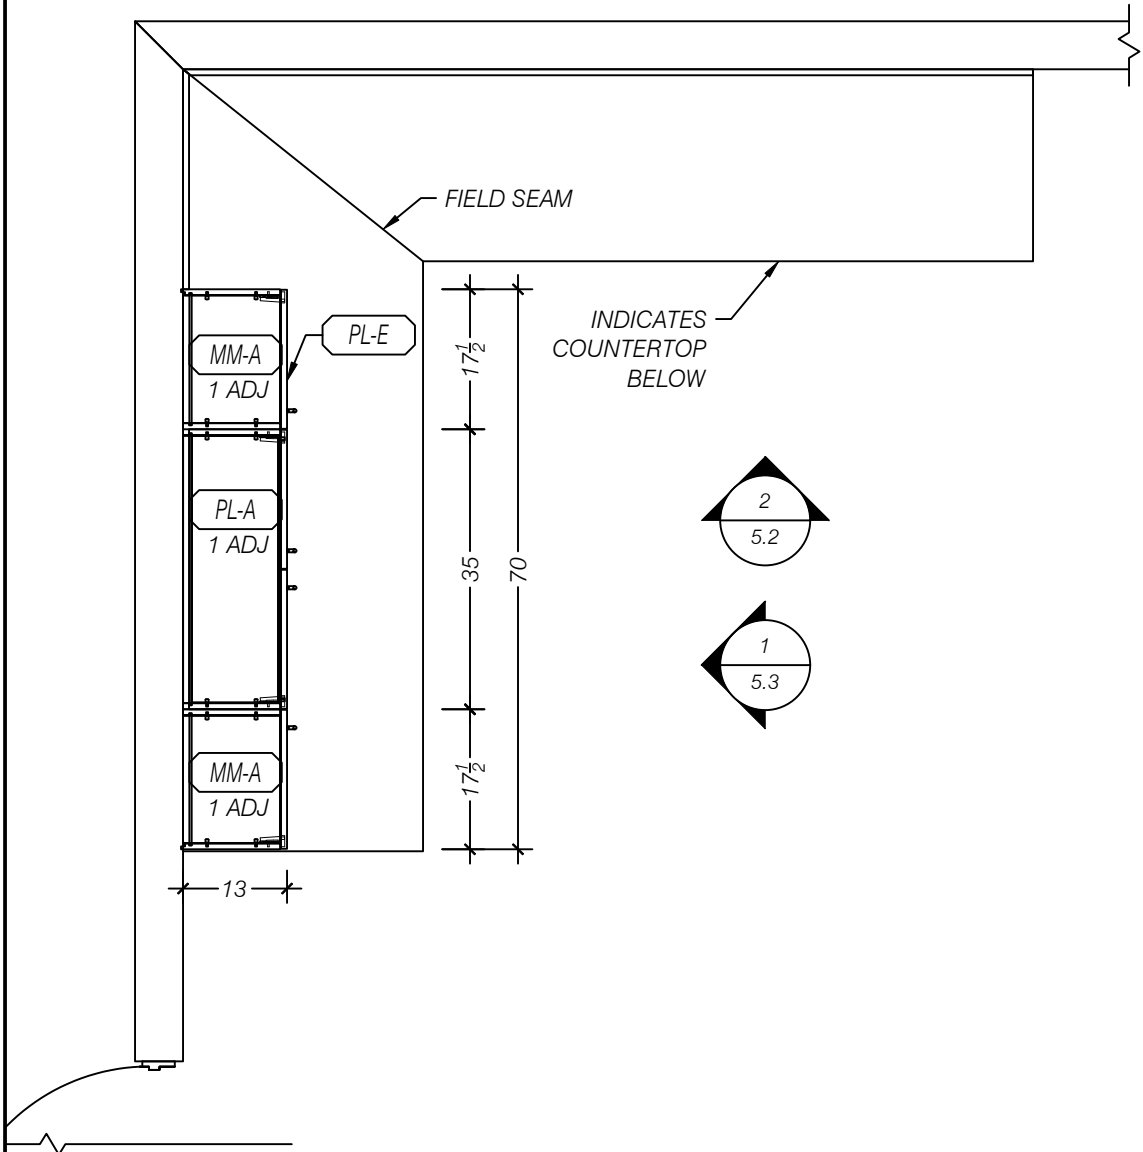

**1** PLAN SECTION WALL - MEDIA CONTROL 113  
SCALE 1:24 (1/2"=1'-0")  
ARCH REF: NA

|  |      | MATERIALS                                                                   |
|--|------|-----------------------------------------------------------------------------|
|  |      | WHITE MELAMINE                                                              |
|  |      | WHITE CAB LINER                                                             |
|  |      | (PL-2) PIONITE "FOLKSTONE GRAY", SG241-SD, TEXTURED/SUEDE FINISH            |
|  |      | (PL-3) WILSONART "WHITE", 1570-60, FINE VELVET TEXTURE 1570-38              |
|  |      | (PL-4) WILSONART "CARBON MESH", 4880-38, FINE VELVET TEXTURE                |
|  | QTY. | HARDWARE                                                                    |
|  | X    | SALICE 0mm CLIP-ON HINGE PLATE EURO SCREW, BARGR09/16                       |
|  | X    | SALICE 110° FO SOFT-CLOSE, LOGICA SILENTIA, C7J6AE9                         |
|  | X    | KNAPE & VOGT DRAWER SLIDES, KV8400, SIDE MOUNT, FULL EXT. 100lb LOAD RATING |
|  | X    | KNAPE & VOGT DRAWER SLIDES, KV8600, SIDE MOUNT, FULL EXT. 150lb LOAD RATING |
|  | X    | BERENSON WIRE PULL, BN6131-2SC-P, 96mm CTC, SATIN CHROME FINISH             |
|  | X    | HAFELE SHELF SUPPORT, 282.04.711, 5mm SHELF PIN, STEEL NICKEL-PLATED        |
|  | X    | BRACKET, A&M CFLAT 21 (2.0)                                                 |
|  | X    | BRACKET, A&M CFLAT 24 (2.0)                                                 |
|  | X    | 1/8" x 1-1/4" x 1-1/4" ALUMINUM L-ANGLE, MILL FINISH                        |

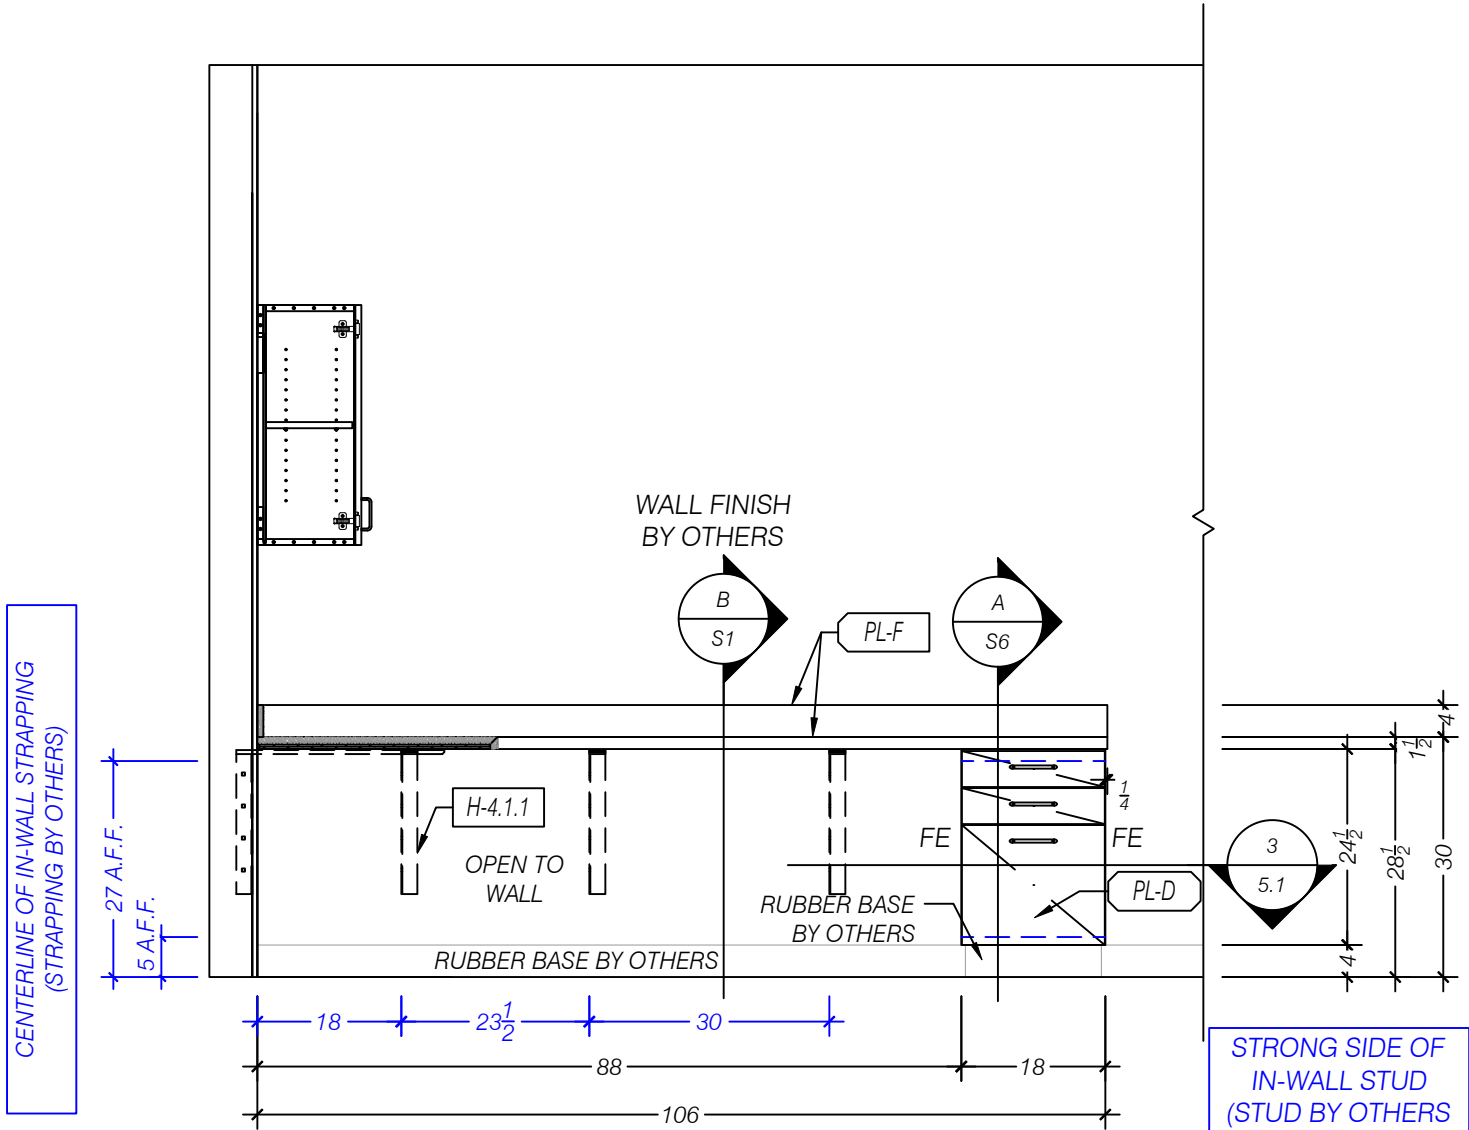

**2** ELEVATION SOUTH - MEDIA CONTROL 113  
SCALE 1:24 (1/2"=1'-0")  
ARCH REF: 8/AE408

5640 WEST END ROAD  
ARCATA, CA 95521  
PH (707) 822-4034 FAX (707) 822-5478  
WWW.CRESTMILLWORK.COM

DGS SREOC COSTA


MESA

MEDIA CONTROL 113

| ISSUE              | DESCRIPTION | BY   |
|--------------------|-------------|------|
| DATE               | 05/05/2026  | Q-AS |
| REVA FOR SUBMITTAL | -           | -    |
| -                  | -           | -    |
| -                  | -           | -    |
| -                  | -           | -    |
| -                  | -           | -    |

| SITE ADDRESS |                                       |      |       |
|--------------|---------------------------------------|------|-------|
| STREET       | 2301 South Shelley Circle Bldg. A & B |      |       |
| CITY         | Costa Mesa                            |      |       |
| STATE        | CA                                    | ZIP  | 92626 |
| JOB #:       | 26034                                 | REV: | A     |
| MOD #:       | 5                                     | REL: | N/A   |

CENTERLINE OF IN-WALL STRAPPING  
(STRAPPING BY OTHERS)

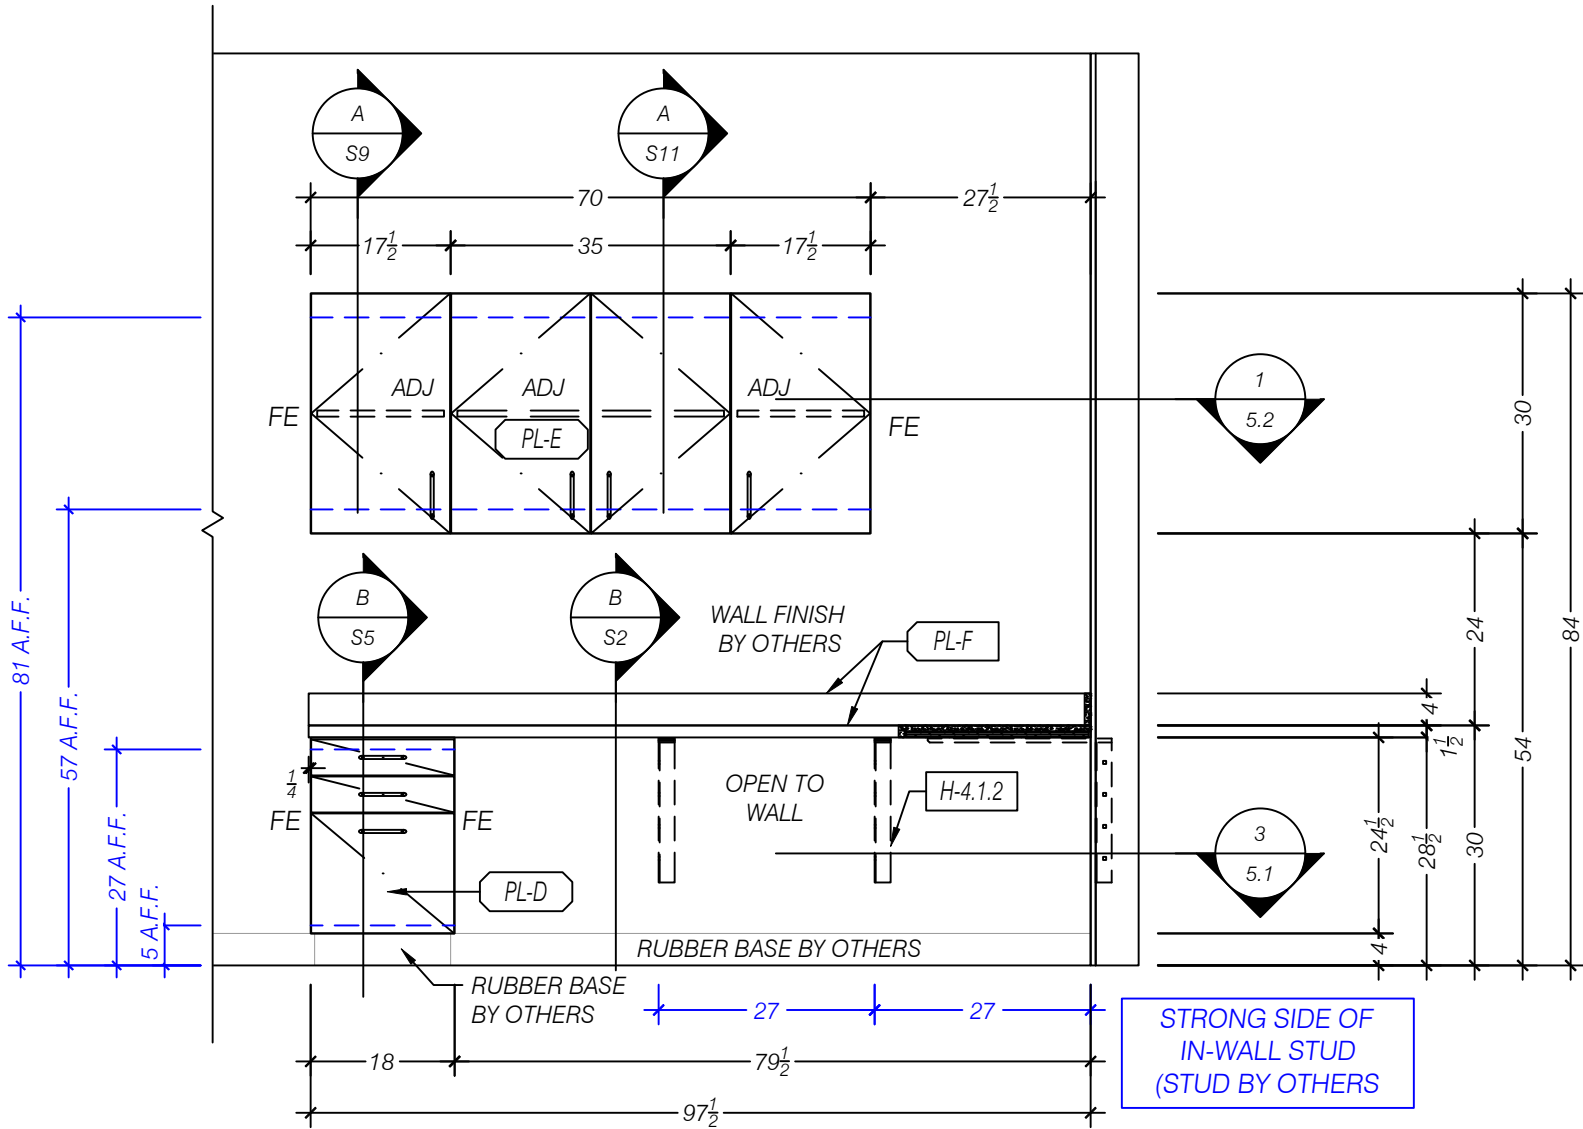

**1** ELEVATION EAST- MEDIA CONTROL 113  
SCALE 1:24 (1/2"=1'-0")  
ARCH REF: 7/AE408

|         |      | MATERIALS                                                                   |
|---------|------|-----------------------------------------------------------------------------|
| (MM-A)  |      | WHITE MELAMINE                                                              |
| (PL-A)  |      | WHITE CAB LINER                                                             |
| (PL-D)  |      | (PL-2) PIONITE "FOLKSTONE GRAY", SG241-SD, TEXTURED/SUEDE FINISH            |
| (PL-E)  |      | (PL-3) WILSONART "WHITE", 1570-60, FINE VELVET TEXTURE 1570-38              |
| (PL-F)  |      | (PL-4) WILSONART "CARBON MESH", 4880-38, FINE VELVET TEXTURE                |
|         | QTY. | HARDWARE                                                                    |
| H-1.2   | X    | SALICE 0mm CLIP-ON HINGE PLATE EURO SCREW, BARGR09/16                       |
| H-1.3   | X    | SALICE 110° FO SOFT-CLOSE, LOGICA SILENTIA, C7J6AE9                         |
| H-2.0   | X    | KNAPE & VOGT DRAWER SLIDES, KV8400, SIDE MOUNT, FULL EXT. 100lb LOAD RATING |
| H-2.1   | X    | KNAPE & VOGT DRAWER SLIDES, KV8600, SIDE MOUNT, FULL EXT. 150lb LOAD RATING |
| H-3.0   | X    | BERENSON WIRE PULL, BN6131-2SC-P, 96mm CTC, SATIN CHROME FINISH             |
| H-4.0   | X    | HAFELE SHELF SUPPORT, 282.04.711, 5mm SHELF PIN, STEEL NICKEL-PLATED        |
| H-4.1.1 | X    | BRACKET, A&M CFLAT 21 (2.0)                                                 |
| H-4.1.2 | X    | BRACKET, A&M CFLAT 24 (2.0)                                                 |
| H-7.0   | X    | 1/8" x 1-1/4" x 1-1/4" ALUMINUM L-ANGLE, MILL FINISH                        |




**DGS SREOC COSTA**  
**MESA**  
**MEDIA CONTROL 113**

| ISSUE | DESCRIPTION         | BY   |
|-------|---------------------|------|
| DATE  | 05/05/2026          | Q-AS |
|       | REV-A FOR SUBMITTAL | -    |
|       |                     | -    |
|       |                     | -    |
|       |                     | -    |
|       |                     | -    |

| SITE ADDRESS |                                       |      |       |
|--------------|---------------------------------------|------|-------|
| STREET       | 2301 South Shelley Circle Bldg. A & B |      |       |
| CITY         | Costa Mesa                            |      |       |
| STATE        | CA                                    | ZIP  | 92626 |
| JOB #:       | 26034                                 | REV: | A     |
| MOD #:       | 5                                     | REL: | N/A   |

**5.3**

© CRESTMILLWORK, INC.

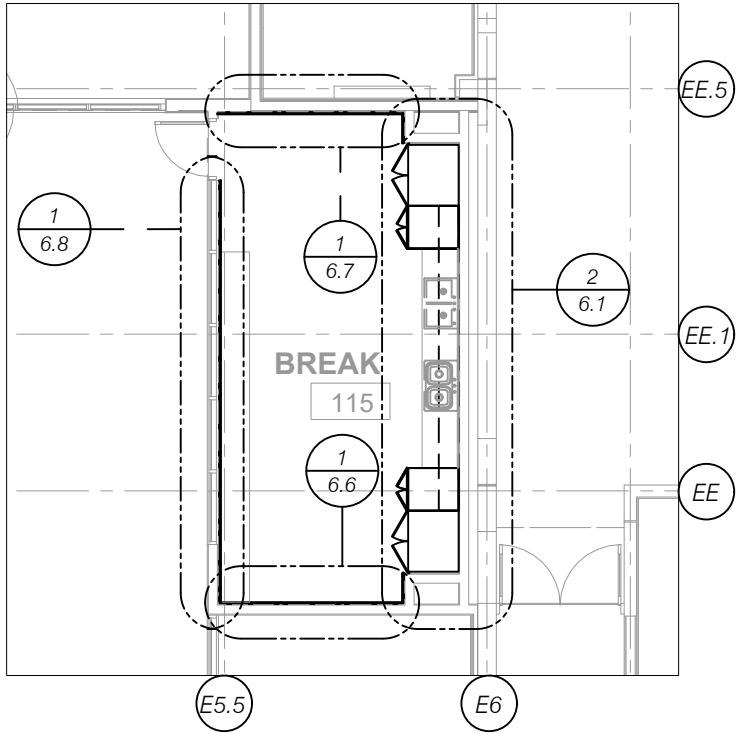


**1** KEY PLAN  
SCALE: NTS  
ARCH REF: 1/AE101.1

| NOTES |   |
|-------|---|
| 1     | ALL DIMENSIONS TO BE FIELD VERIFIED                                                                                          |
| 2     | GENERAL CONTRACTOR TO COORDINATE ALL FRAMING REQUIREMENTS WITH CMI                                                           |
| 3     | GENERAL CONTRACTOR TO COORDINATE ALL WALL TYPES, THICKNESSES AND ROUGH OPENINGS                                              |
| 4     | GENERAL CONTRACTOR & ELECTRICAL CONTRACTOR TO COORDINATE ALL ELECTRICAL BOX LOCATIONS & REQUIREMENTS WITH MILLWORK DRAWINGS  |
| 5     | GENERAL CONTRACTOR & ELECTRICAL CONTRACTOR TO COORDINATE ALL LIGHT FIXTURE FEED & SWITCHING LOCATIONS WITH MILLWORK DRAWINGS |
| 6     | GENERAL CONTRACTOR & PLUMBING CONTRACTOR TO COORDINATE ALL PLUMBING FIXTURES & INSTALLATION REQUIREMENTS                     |

|         | MATERIALS                                                                                         |
|---------|---------------------------------------------------------------------------------------------------|
| (MM-A)  | WHITE MELAMINE                                                                                    |
| (PL-C)  | (PL-1, WB-2) WILSONART "HARVEST MAPLE", 7953-38, FINE VELVET TEXTURE                              |
| (PG-A)  | (CR-1) SOLID POPLAR, DELIVERED PRIMED (PREPPING, PAINTING, FILLING OF ATTACHMENT HOLES BY OTHERS) |
|         | QTY.    HARDWARE                                                                                  |
| (H-1.2) | X    SALICE 0mm CLIP-ON HINGE PLATE EURO SCREW, BARGR09/16                                        |
| (H-1.3) | X    SALICE 110° FO SOFT-CLOSE, LOGICA SILENTIA, C7J6AE9                                          |
| (H-2.0) | X    KNAPE & VOGT DRAWER SLIDES, KV8400, SIDE MOUNT, FULL EXT. 100lb LOAD RATING                  |
| (H-2.1) | X    KNAPE & VOGT DRAWER SLIDES, KV8600, SIDE MOUNT, FULL EXT. 150lb LOAD RATING                  |
| (H-4.0) | X    HAFELE SHELF SUPPORT, 282.04.711, 5mm SHELF PIN, STEEL NICKEL-PLATED                         |
| (H-9.1) | X    GRAINGER - GRAB CATCH - 4PE50, STEEL                                                         |

| PLUMBING SCHEDULE BY OTHERS |                         |                     |                 |                |
|-----------------------------|-------------------------|---------------------|-----------------|----------------|
| ARCH. TAG                   | MAKE                    | MODEL               | FINISH          | COMMENTS       |
| KS-1                        | KOHLER                  | K-5267-4            | STAINLESS STEEL | SINK           |
| KS-2                        | KOHLER                  | K-3996-4            | STAINLESS STEEL | SINK           |
| KS-1 & KS-2                 | CHICAGO FAUCETS TYPICAL | 895-317-GN8AE35ABCP | POLISHED CHROME | FAUCET         |
| TA-5                        | SLOAN                   | EAF - 200           | POLISHED CHROME | SOAP DISPENSER |

| EQUIPMENT SCHEDULE BY OTHERS |                  |              |           |                        |
|------------------------------|------------------|--------------|-----------|------------------------|
| ARCH. TAG                    | MAKE             | MODEL        | FINISH    | COMMENTS               |
| REF-1                        | FRIDGIDAIRE      | PRFG2383AF   | STAINLESS | REFRIGERATOR           |
| ICE-1                        | SUMMIT APPLIANCE | BIM44GCSSADA | STAINLESS | UNDERCOUNTER ICE MAKER |
| MW-1                         | FRIDGIDAIRE      | PMBS3080BF   | STAINLESS | MICROWAVE              |

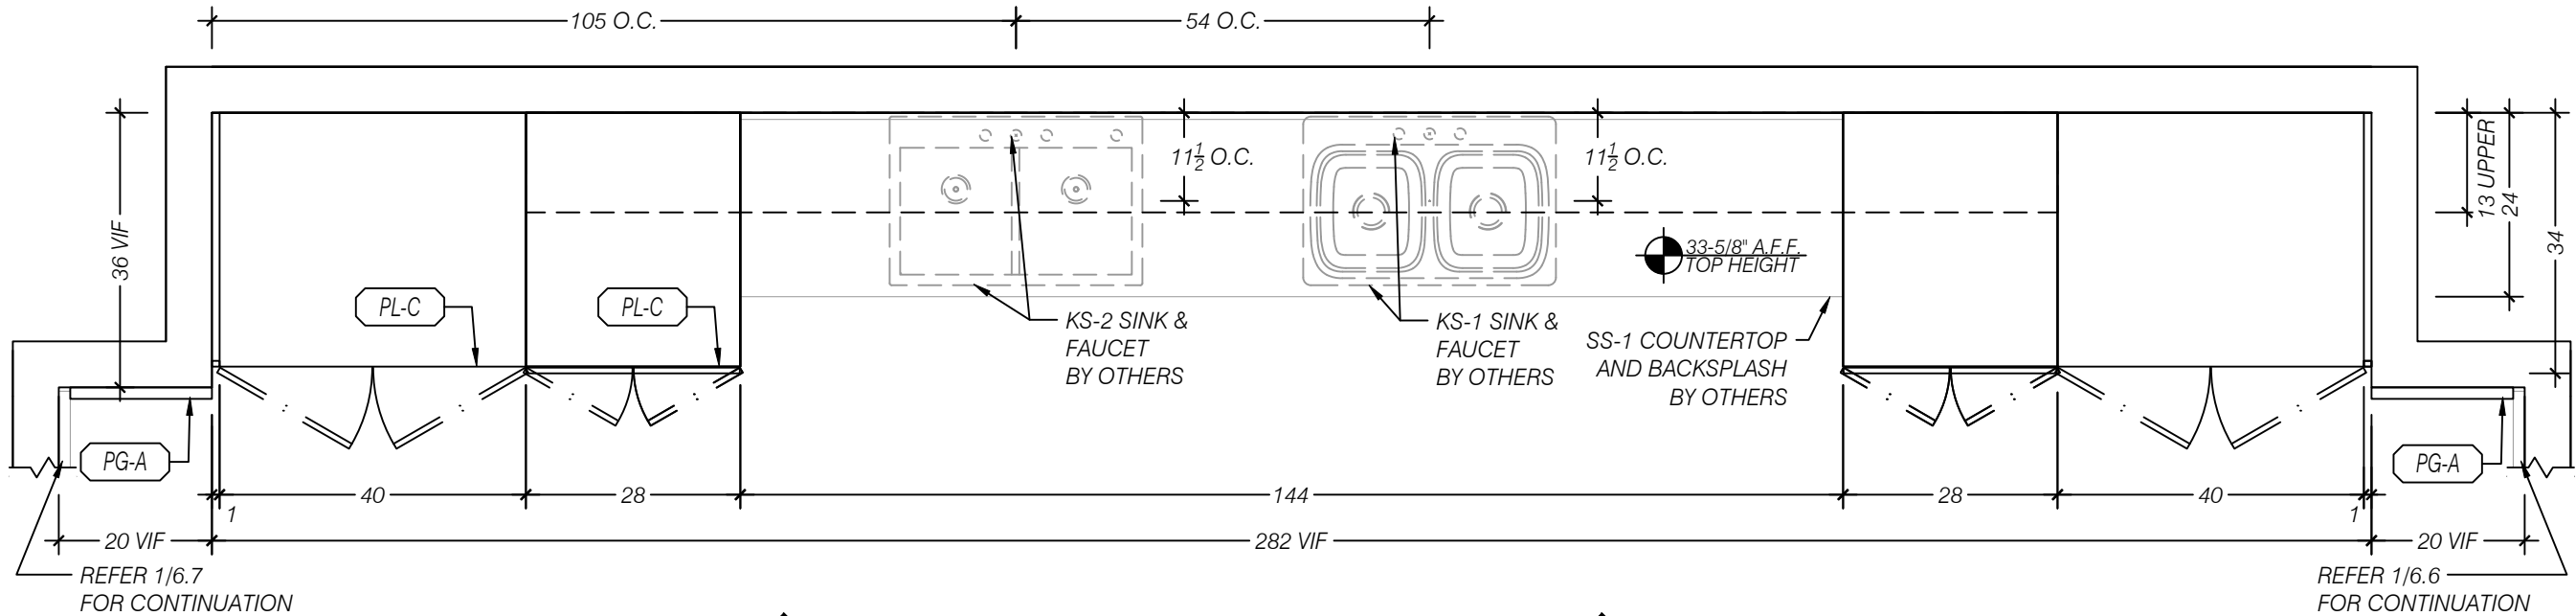

**2** PLAN - BREAK ROOM 115  
SCALE 1:24 (1/2"=1'-0")  
ARCH REF: 1/AE407

5640 WEST END ROAD  
ARCATA, CA 95521  
PH (707) 822-4034 FAX (707) 822-5478  
WWW.CRESTMILLWORK.COM

DGS SREOC COSTA

MESA

BREAK ROOM 115


| ISSUE               |  | BY   | DATE |
|---------------------|--|------|------|
| DESCRIPTION         |  | Q-AS |      |
| REV-A FOR SUBMITTAL |  | -    | -    |
|                     |  | -    | -    |
|                     |  | -    | -    |
|                     |  | -    | -    |
|                     |  | -    | -    |

| SITE ADDRESS |                                       |      |       |
|--------------|---------------------------------------|------|-------|
| STREET       | 2301 South Shelley Circle Bldg. A & B |      |       |
| CITY         | Costa Mesa                            |      |       |
| STATE        | CA                                    | ZIP  | 92626 |
| JOB #:       | 26034                                 | REV: | A     |
| MOD #:       | 6                                     | REL: | N/A   |


| PLUMBING SCHEDULE BY OTHERS |                            |                     |                 |                |
|-----------------------------|----------------------------|---------------------|-----------------|----------------|
| ARCH. TAG                   | MAKE                       | MODEL               | FINISH          | COMMENTS       |
| KS-1                        | KOHLER                     | K-5267-4            | STAINLESS STEEL | SINK           |
| KS-2                        | KOHLER                     | K-3996-4            | STAINLESS STEEL | SINK           |
| KS-1 & KS-2                 | CHICAGO FAUCETS<br>TYPICAL | 895-317-GN8AE35ABCP | POLISHED CHROME | FAUCET         |
| TA-5                        | SLOAN                      | EAJ - 200           | POLISHED CHROME | SOAP DISPENSER |

| MATERIALS     |                                                                                                   |
|---------------|---------------------------------------------------------------------------------------------------|
| MM-A          | WHITE MELAMINE                                                                                    |
| PL-C          | (PL-1, WB-2) WILSONART "HARVEST MAPLE", 7953-38, FINE VELVET TEXTURE                              |
| PG-A          | (CR-1) SOLID POPLAR, DELIVERED PRIMED (PREPPING, PAINTING, FILLING OF ATTACHMENT HOLES BY OTHERS) |
| QTY. HARDWARE |                                                                                                   |
| H-1.2         | X SALICE 0mm CLIP-ON HINGE PLATE EURO SCREW, BARGR09/16                                           |
| H-1.3         | X SALICE 110° FO SOFT-CLOSE, LOGICA SILENTIA, C7J6AE9                                             |
| H-2.0         | X KNAPE & VOGT DRAWER SLIDES, KV8400, SIDE MOUNT, FULL EXT. 100lb LOAD RATING                     |
| H-2.1         | X KNAPE & VOGT DRAWER SLIDES, KV8600, SIDE MOUNT, FULL EXT. 150lb LOAD RATING                     |
| H-4.0         | X HAFELE SHELF SUPPORT, 282.04.711, 5mm SHELF PIN, STEEL NICKEL-PLATED                            |
| H-9.1         | X GRAINGER - GRAB CATCH - 4PE50, STEEL                                                            |

| EQUIPMENT SCHEDULE BY OTHERS |                  |              |           |                        |
|------------------------------|------------------|--------------|-----------|------------------------|
| ARCH. TAG                    | MAKE             | MODEL        | FINISH    | COMMENTS               |
| REF-1                        | FRIDGIDAIRE      | PRFG2383AF   | STAINLESS | REFRIGERATOR           |
| ICE-1                        | SUMMIT APPLIANCE | BIM44GCSSADA | STAINLESS | UNDERCOUNTER ICE MAKER |
| MW-1                         | FRIDGIDAIRE      | PMBS3080BF   | STAINLESS | MICROWAVE              |

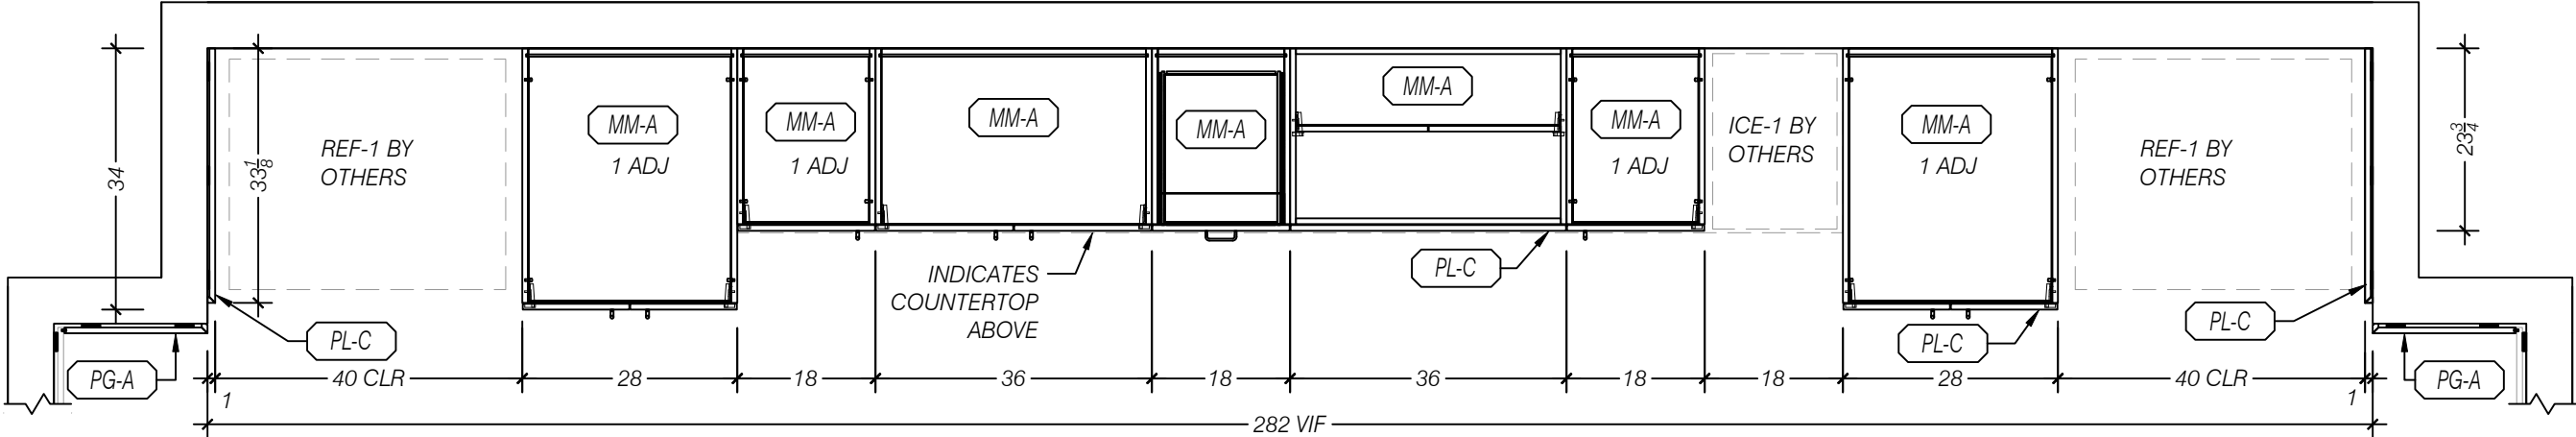

**1** PLAN SECTION BASE - BREAK ROOM 115  
SCALE 1:24 (1/2"=1'-0")  
ARCH REF: NA

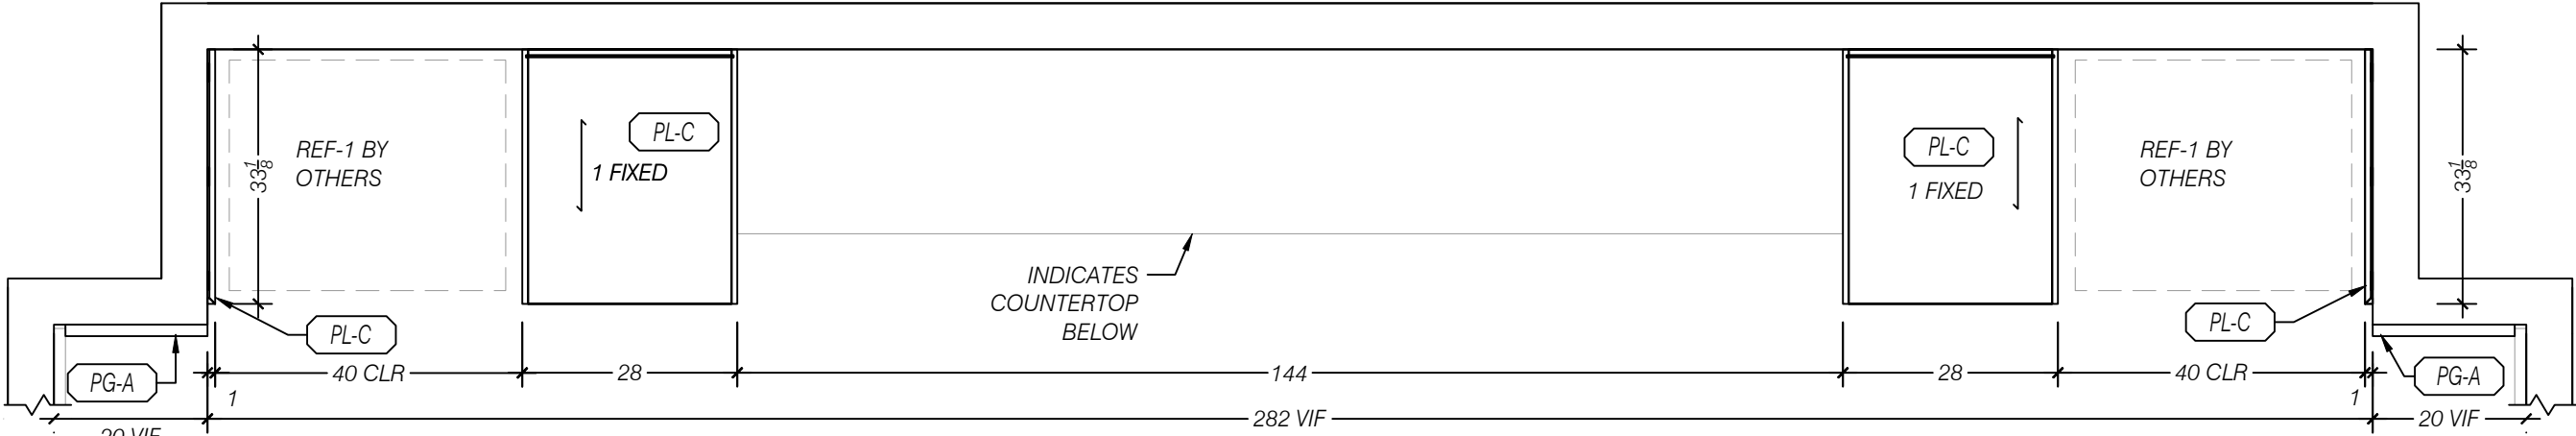

**2** PLAN SECTION TALL - BREAK ROOM 115  
SCALE 1:24 (1/2"=1'-0")  
ARCH REF: NA



CRESTMILLWORK

5640 WEST END ROAD  
ARCATA, CA 95521  
PH (707) 822-4034 FAX (707) 822-5478  
WWW.CRESTMILLWORK.COM

DGS SREOC COSTA

MESA

BREAK ROOM 115

| ISSUE        |  |                                       |       |          |
|--------------|--|---------------------------------------|-------|----------|
| DATE         |  | DESCRIPTION                           | BY    |          |
| 05/05/2026   |  | REV-A FOR SUBMITTAL                   | Q-AS  |          |
|              |  |                                       |       |          |
|              |  |                                       |       |          |
| SITE ADDRESS |  |                                       |       |          |
| STREET       |  | 2301 South Shelley Circle Bldg. A & B |       |          |
| CITY         |  | Costa Mesa                            |       |          |
| STATE        |  | CA                                    | ZIP   | 92626    |
| JOB #:       |  |                                       | 26034 | REV: A   |
| MOD #:       |  |                                       | 6     | REL: N/A |
| 6.2          |  |                                       |       |          |






| PLUMBING SCHEDULE BY OTHERS |                         |                     |                 |                |
|-----------------------------|-------------------------|---------------------|-----------------|----------------|
| ARCH. TAG                   | MAKE                    | MODEL               | FINISH          | COMMENTS       |
| KS-1                        | KOHLER                  | K-5267-4            | STAINLESS STEEL | SINK           |
| KS-2                        | KOHLER                  | K-3996-4            | STAINLESS STEEL | SINK           |
| KS-1 & KS-2                 | CHICAGO FAUCETS TYPICAL | 895-317-GN8AE35ABCP | POLISHED CHROME | FAUCET         |
| TA-5                        | SLOAN                   | EAJ - 200           | POLISHED CHROME | SOAP DISPENSER |

| MATERIALS |                                                                                                   |
|-----------|---------------------------------------------------------------------------------------------------|
| (MM-A)    | WHITE MELAMINE                                                                                    |
| (PL-C)    | (PL-1, WB-2) WILSONART "HARVEST MAPLE", 7953-38, FINE VELVET TEXTURE                              |
| (PG-A)    | (CR-1) SOLID POPLAR, DELIVERED PRIMED (PREPPING, PAINTING, FILLING OF ATTACHMENT HOLES BY OTHERS) |
| QTY.      | HARDWARE                                                                                          |
| H-1.2     | X SALICE 0mm CLIP-ON HINGE PLATE EURO SCREW, BARGR09/16                                           |
| H-1.3     | X SALICE 110° FO SOFT-CLOSE, LOGICA SILENTIA, C7J6AE9                                             |
| H-2.0     | X KNAPE & VOGT DRAWER SLIDES, KV8400, SIDE MOUNT, FULL EXT. 100lb LOAD RATING                     |
| H-2.1     | X KNAPE & VOGT DRAWER SLIDES, KV8600, SIDE MOUNT, FULL EXT. 150lb LOAD RATING                     |
| H-4.0     | X HAFELE SHELF SUPPORT, 282.04.711, 5mm SHELF PIN, STEEL NICKEL-PLATED                            |
| H-9.1     | X GRAINGER - GRAB CATCH - 4PE50, STEEL                                                            |

| EQUIPMENT SCHEDULE BY OTHERS |                  |              |           |                        |
|------------------------------|------------------|--------------|-----------|------------------------|
| ARCH. TAG                    | MAKE             | MODEL        | FINISH    | COMMENTS               |
| REF-1                        | FRIDGIDAIRE      | PRFG2383AF   | STAINLESS | REFRIGERATOR           |
| ICE-1                        | SUMMIT APPLIANCE | BIM44GCSSADA | STAINLESS | UNDERCOUNTER ICE MAKER |
| MW-1                         | FRIDGIDAIRE      | PMBS3080BF   | STAINLESS | MICROWAVE              |

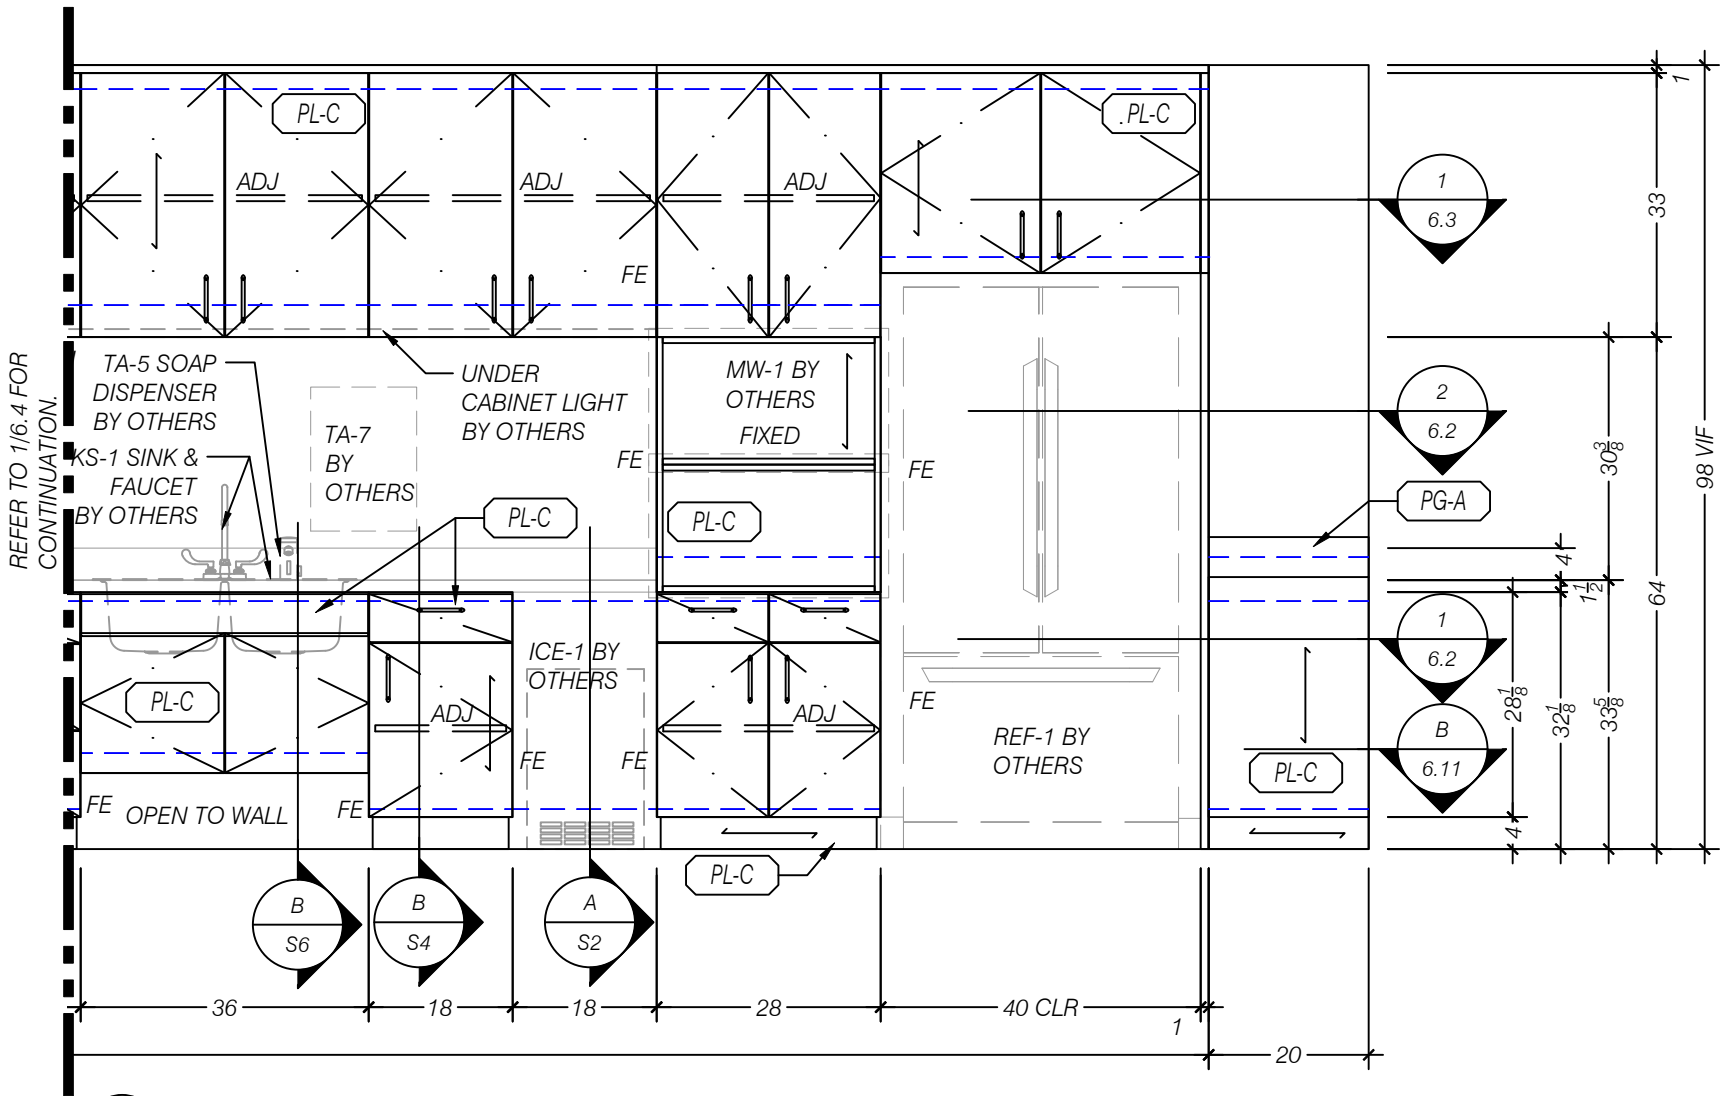

ARCHITECT NOTE:

- MW-1 CALLS FOR A BUILT IN MICROWAVE WHICH REQUIRES A TRIM KIT THAT'S 30"W x 18"H. THE MICROWAVE CABINET IS DRAWN AT 28"W x 30"H. PLEASE ADVISE WHICH CABINETS WE CAN CHANGE.
- DUE TO PRESENCE OF DROP-IN SINK (MODEL) WE HAVE REDUCED THE COUNTER HEIGHT TO 33-5/8" IN ORDER TO ACHIEVE THE POTENTIAL ADA COMPLIANCE & ALLOWING ENOUGH SPACE FOR APPLIANCE. PLEASE CONFIRM.
- THERE COULD BE A POTENTIAL CONFLICT BETWEEN SINK AND BACKSPLASH. PLEASE ADVISE.


**1** ELEVATION EAST - BREAK ROOM 115  
SCALE 1:24 (1/2"=1'-0")  
ARCH REF: 3/AE407

DGS SREOC COSTA  
MESA  
BREAK ROOM 115

| ISSUE      |                     | BY   |
|------------|---------------------|------|
| DATE       | DESCRIPTION         | Q-AS |
| 05/05/2026 | REV-A FOR SUBMITTAL | -    |
| -          | -                   | -    |
| -          | -                   | -    |
| -          | -                   | -    |
| -          | -                   | -    |

| SITE ADDRESS |                                       |      |       |
|--------------|---------------------------------------|------|-------|
| STREET       | 2301 South Shelley Circle Bldg. A & B |      |       |
| CITY         | Costa Mesa                            |      |       |
| STATE        | CA                                    | ZIP  | 92626 |
| JOB #:       | 26034                                 | REV: | A     |
| MOD #:       | 6                                     | REL: | N/A   |

Diagram showing the elevation view of a 122 VIF wall section. The wall is 122 VIF long, divided into three 40-unit segments. The top edge is labeled PL-C. The bottom edge has dimensions: 1/2, 1/4, 1/8, 1/8, 1/8, 1/8. A note on the left says "REFER 1/6.1 FOR CONTINUATION". A note on the right says "1/4".

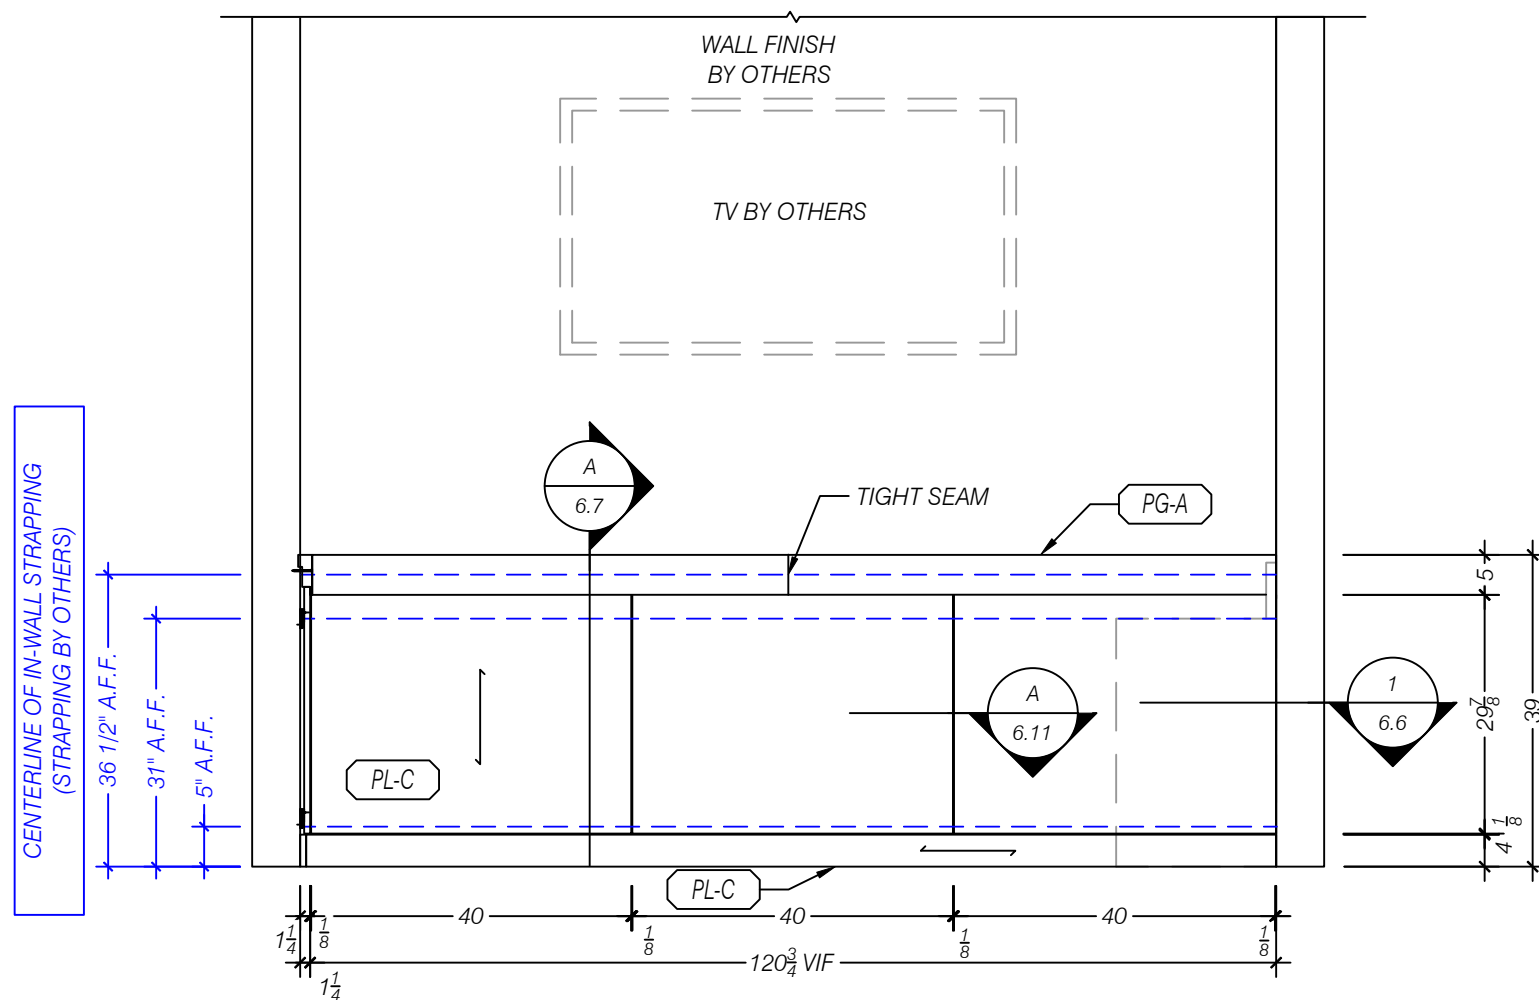


**2** ELEVATION SOUTH - BREAK ROOM 115  
SCALE 1:24 (1/2"=1'-0")  
ARCH REF: 4/AE407

3040 WEST END ROAD  
ARCATA, CA 95521  
PH (707) 822-4034 FAX (707) 822-5478  
WWW.CRESTMARKMILLWORK.COM

**DGS SREOC COSTA  
MESA  
BREAK ROOM 115**

| ISSUE      |                     |      |  |
|------------|---------------------|------|--|
| DATE       | DESCRIPTION         | BY   |  |
| 05/05/2026 | REV-A FOR SUBMITTAL | Q-AS |  |
|            |                     |      |  |
|            |                     |      |  |
|                     |                                       |             |       |
|---------------------|---------------------------------------|-------------|-------|
| <b>SITE ADDRESS</b> |                                       |             |       |
| <b>STREET</b>       | 2301 South Shelley Circle Bldg. A & B |             |       |
| <b>CITY</b>         | Costa Mesa                            |             |       |
| <b>STATE</b>        | CA                                    | <b>ZIP</b>  | 92626 |
| <b>JOB #:</b>       | 26034                                 | <b>REV:</b> | A     |
| <b>MOD #:</b>       | 6                                     | <b>REL:</b> | N/A   |
| <b>6.6</b>          |                                       |             |       |

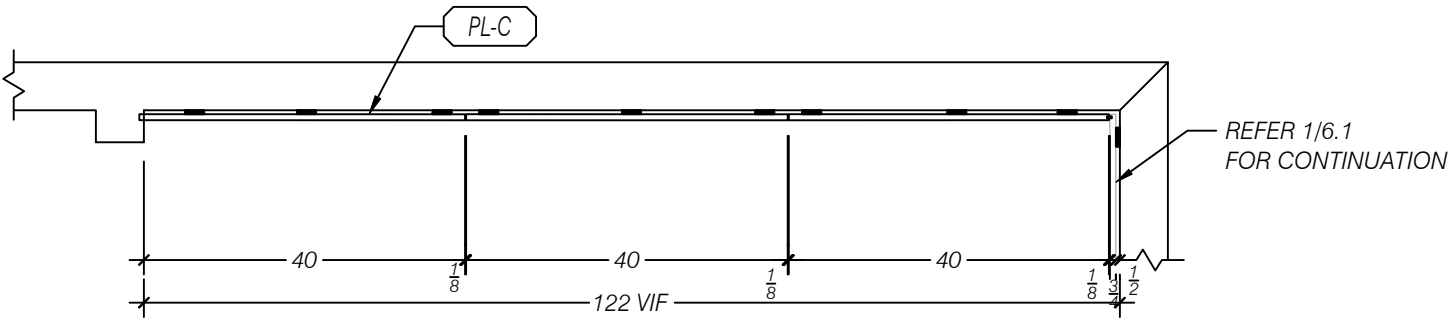

**1** PLAN SECTION - BREAK ROOM 115  
SCALE 1:24 (1/2"=1'-0")  
ARCH REF: 1/AE407

CENTERLINE OF IN-WALL STRAPPING  
(STRAPPING BY OTHERS)


36 1/2" A.F.F.  
31" A.F.F.  
5" A.F.F.

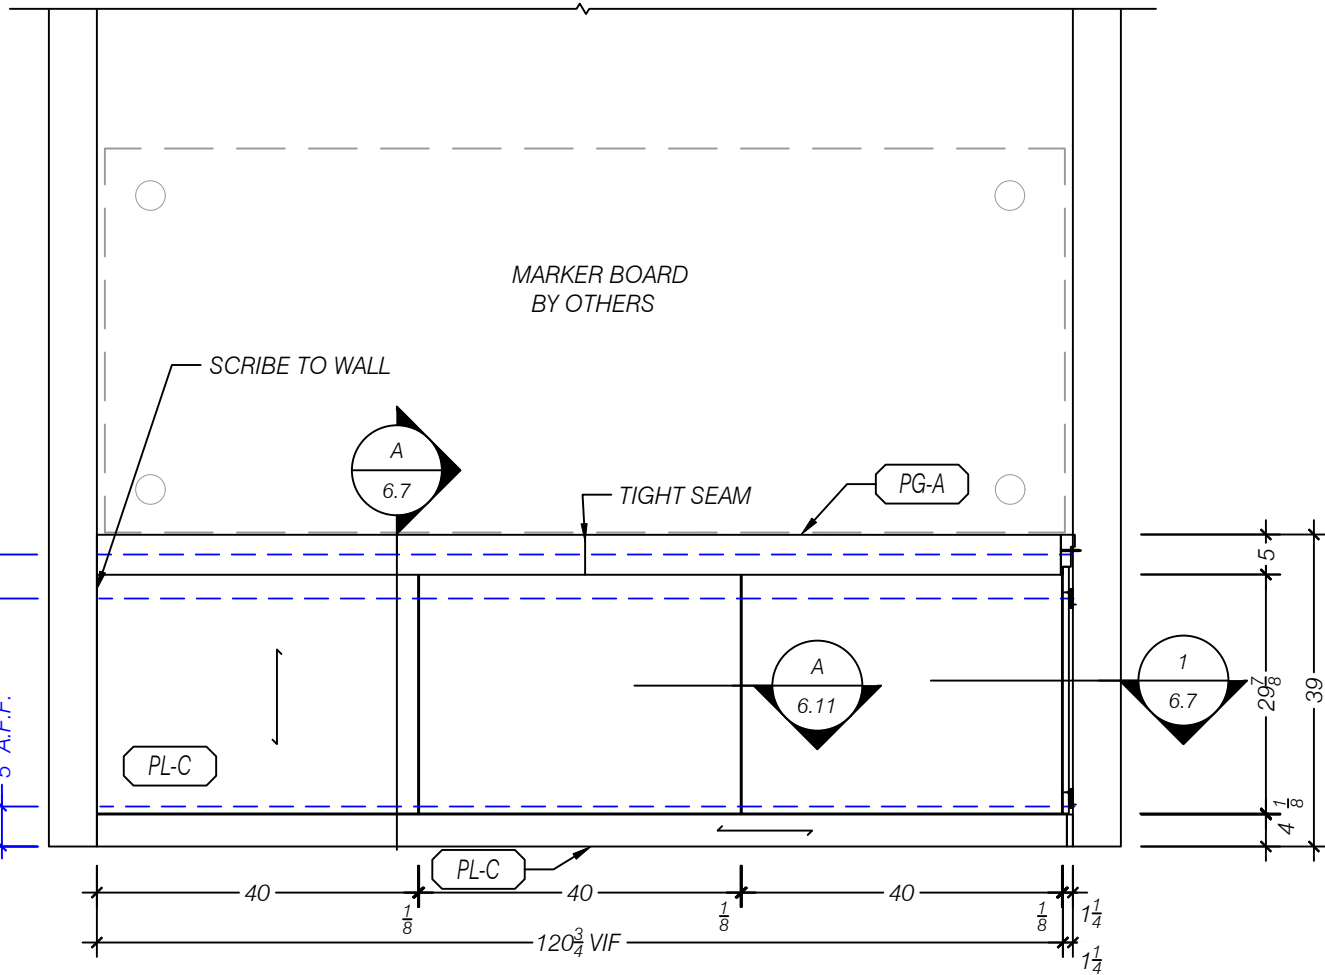

**2** ELEVATION NORTH - BREAK ROOM 115  
SCALE 1:24 (1/2"=1'-0")  
ARCH REF: 2/AE407

|         |      | MATERIALS                                                                                         |
|---------|------|---------------------------------------------------------------------------------------------------|
| (PG-A)  |      | (CR-1) SOLID POPLAR, DELIVERED PRIMED (PREPPING, PAINTING, FILLING OF ATTACHMENT HOLES BY OTHERS) |
| (PL-C)  |      | (PL-1, WB-2) WILSONART "HARVEST MAPLE", 7953-38, FINE VELVET TEXTURE                              |
|         | QTY. | HARDWARE                                                                                          |
| (H-7.1) | X    | ORANGE ALUMINUM Z-CLIP HD PANEL RAIL                                                              |

CENTERLINE OF IN-WALL STRAPPING  
(STRAPPING BY OTHERS)

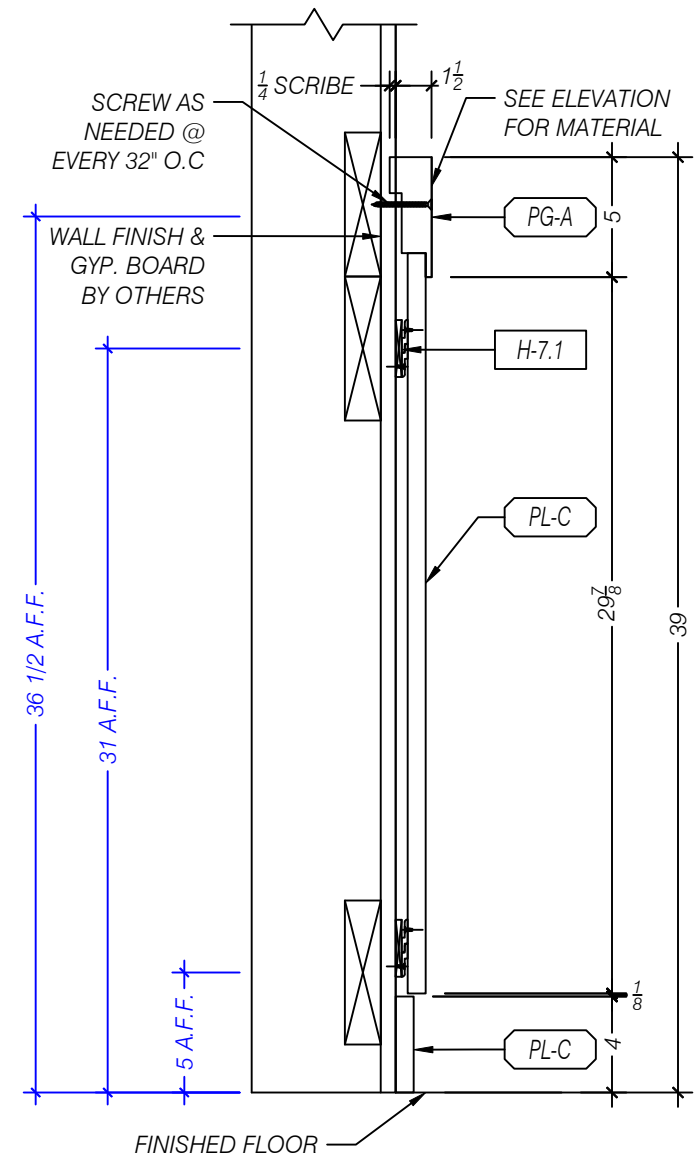

**A** SECTION - PANELLING  
SCALE 1:24 (1/2"=1'-0")  
ARCH REF: NA


# DGS SREOC COSTA MESA BREAK ROOM 115

| ISSUE | DATE       | DESCRIPTION         | BY   |
|-------|------------|---------------------|------|
|       | 05/05/2026 | REV-A FOR SUBMITTAL | Q-AS |
|       | -          | -                   | -    |
|       | -          | -                   | -    |
|       | -          | -                   | -    |
|       | -          | -                   | -    |



| SITE ADDRESS |                                       |      |       |
|--------------|---------------------------------------|------|-------|
| STREET       | 2301 South Shelley Circle Bldg. A & B |      |       |
| CITY         | Costa Mesa                            |      |       |
| STATE        | CA                                    | ZIP  | 92626 |
| JOB #:       | 26034                                 | REV: | A     |
| MOD #:       | 6                                     | REL: | N/A   |

**6.7**


|  |                                                                      |
|--|----------------------------------------------------------------------|
|  | MATERIALS                                                            |
|  | (PL-1, WB-2) WILSONART "HARVEST MAPLE", 7953-38, FINE VELVET TEXTURE |
|  | QTY. HARDWARE                                                        |
|  | X ORANGE ALUMINUM Z-CLIP HD PANEL RAIL                               |

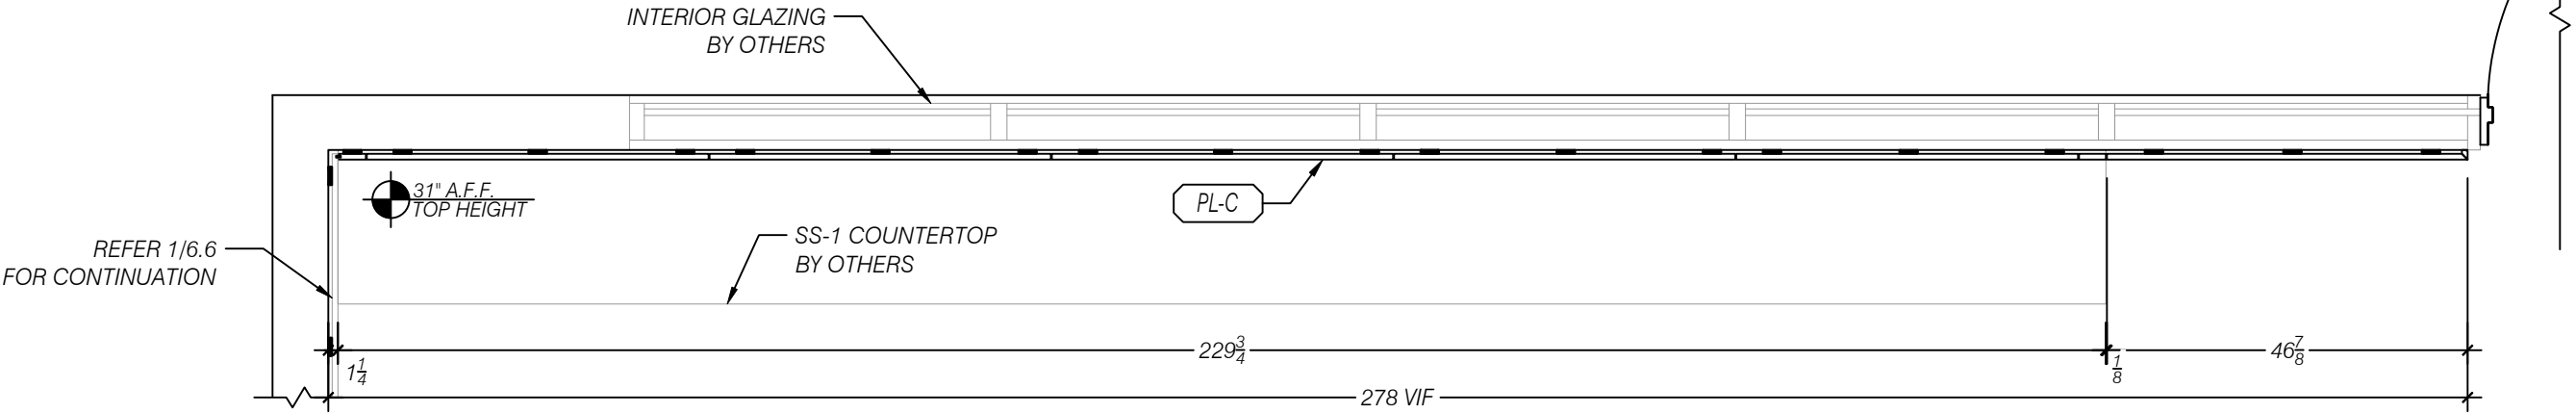

1 PLAN - BREAK ROOM 115  
SCALE 1:24 (1/2"=1'-0")  
ARCH REF: 5/AE407

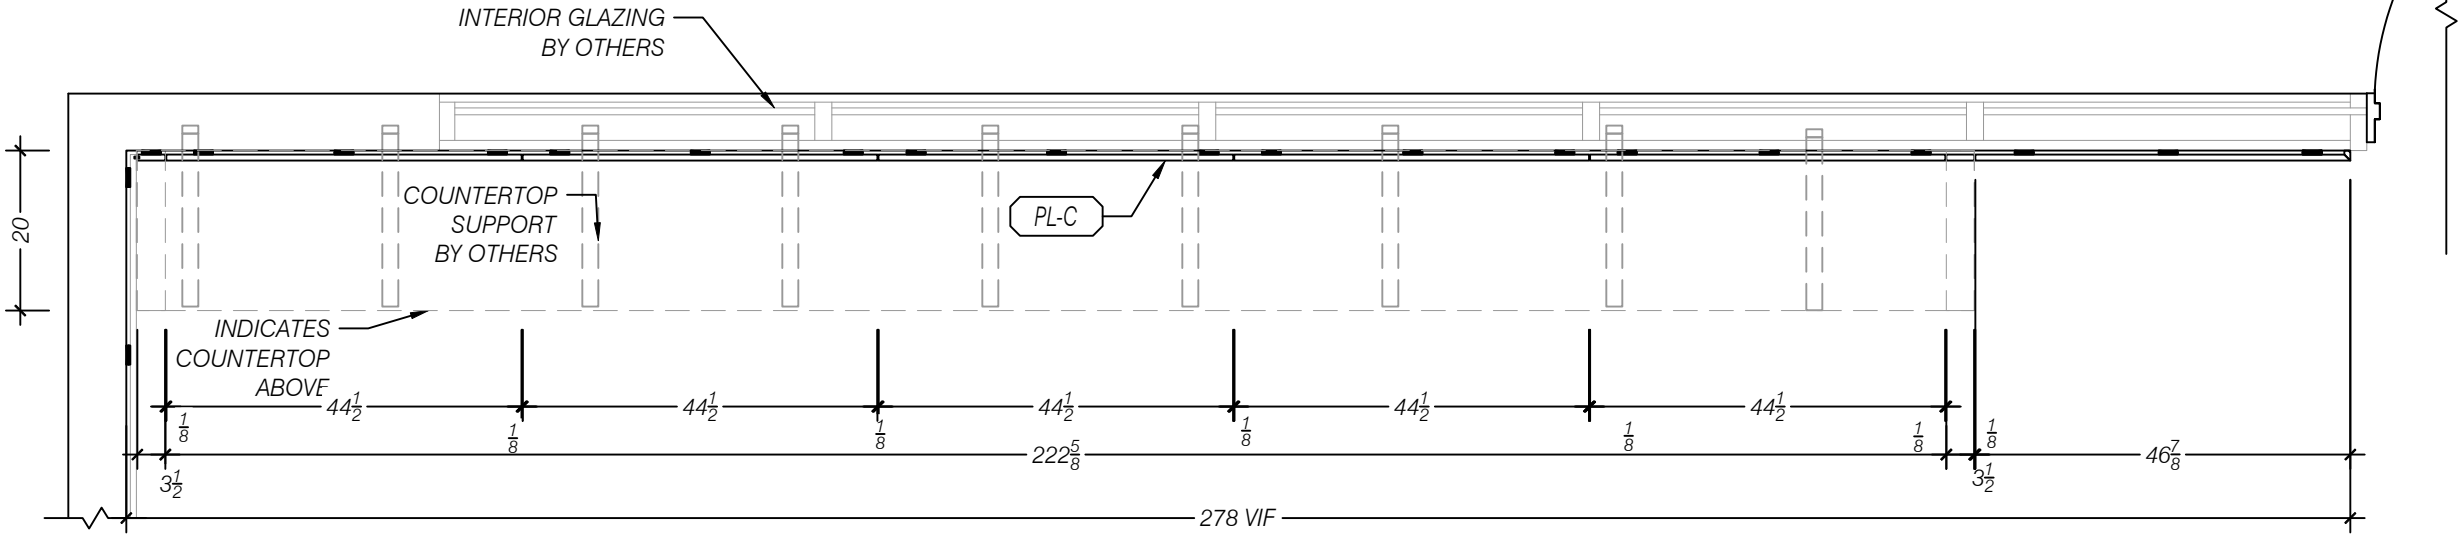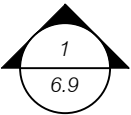

2 PLAN SECTION BASE - BREAK ROOM 115  
SCALE 1:24 (1/2"=1'-0")  
ARCH REF: NA

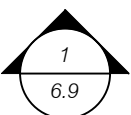

CRESTMILLWORK

5640 WEST END ROAD  
ARCATA, CA 95521  
PH (707) 822-4034 FAX (707) 822-5478  
WWW.CRESTMILLWORK.COM


DGS SREOC COSTA  
MESA  
BREAK ROOM 115

| ISSUE | DESCRIPTION        | DATE       | BY   |   |   |   |   |
|-------|--------------------|------------|------|---|---|---|---|
|       |                    |            | Q-AS |   |   |   |   |
|       | REVA FOR SUBMITTAL | 05/05/2026 | -    | - | - | - | - |
|       |                    |            | -    | - | - | - | - |
|       |                    |            | -    | - | - | - | - |
|       |                    |            | -    | - | - | - | - |

| SITE ADDRESS |                                       |      |       |
|--------------|---------------------------------------|------|-------|
| STREET       | 2301 South Shelley Circle Bldg. A & B |      |       |
| CITY         | Costa Mesa                            |      |       |
| STATE        | CA                                    | ZIP  | 92626 |
| JOB #:       | 26034                                 | REV: | A     |
| MOD #:       | 6                                     | REL: | N/A   |

CENTERLINE OF IN-WALL STRAPPING  
(STRAPPING BY OTHERS)

35 A.F.F.  
25 A.F.F.  
5 A.F.F.

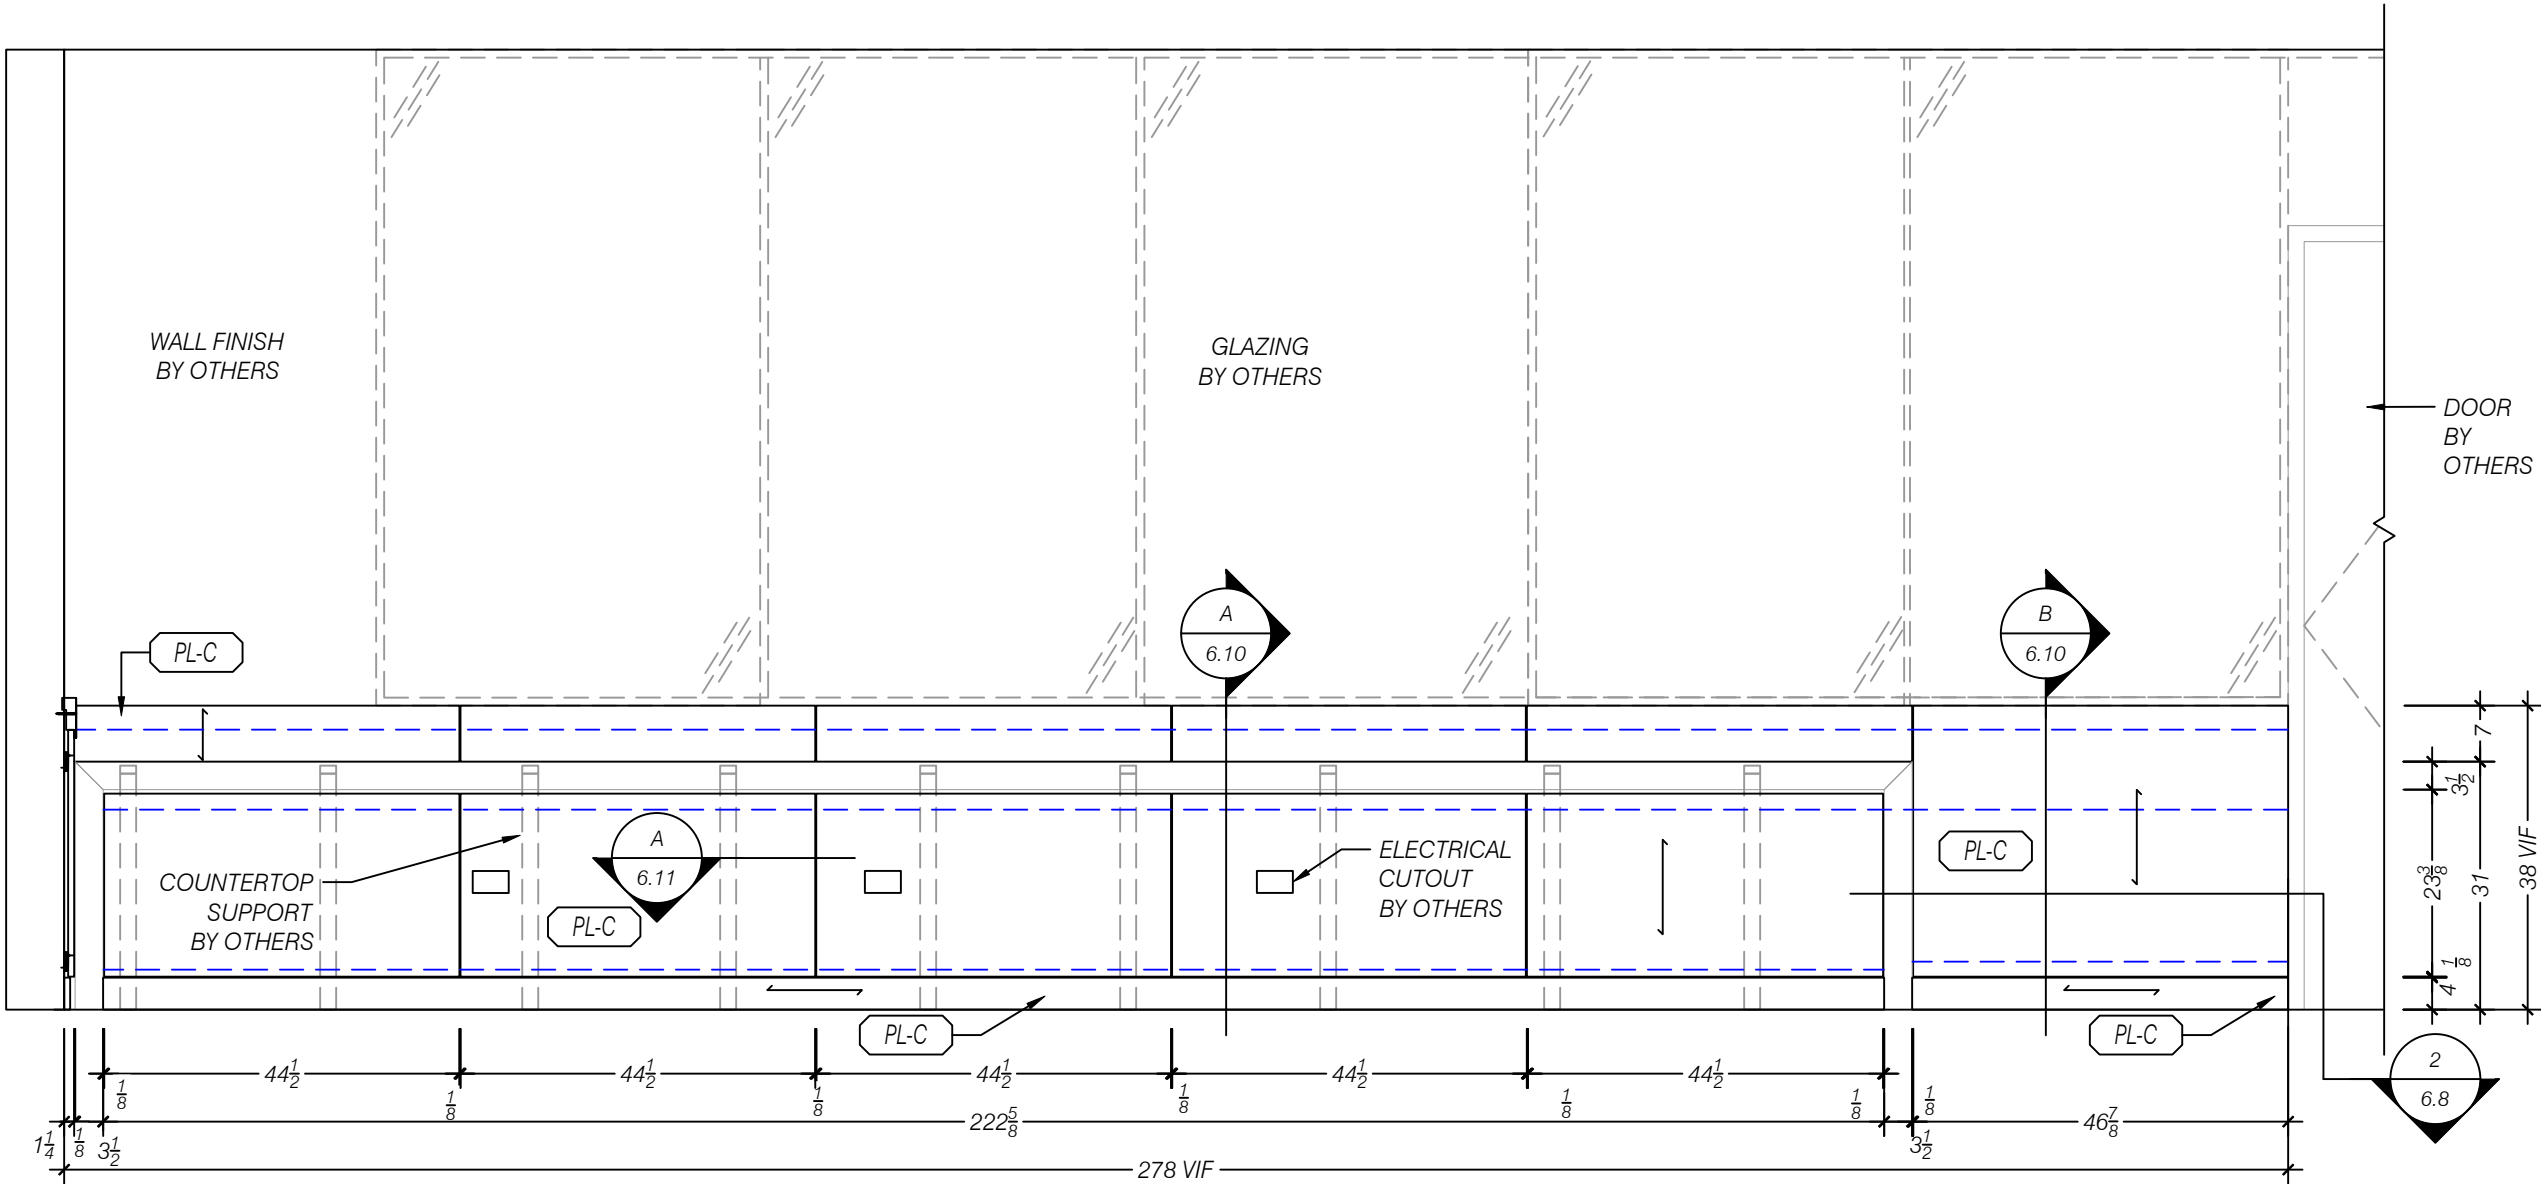

**1** ELEVATION WEST - BREAK ROOM 115  
SCALE 1:24 (1/2"=1'-0")  
ARCH REF: 5/AE407

|         | MATERIALS                                                            |
|---------|----------------------------------------------------------------------|
| (PL-C)  | (PL-1, WB-2) WILSONART "HARVEST MAPLE", 7953-38, FINE VELVET TEXTURE |
|         | QTY. HARDWARE                                                        |
| (H-7.1) | X ORANGE ALUMINUM Z-CLIP HD PANEL RAIL                               |




**DGS SREOC COSTA  
MESA  
BREAK ROOM 115**


| ISSUE | DATE       | DESCRIPTION         | BY   |
|-------|------------|---------------------|------|
|       | 05/05/2026 | REV-A FOR SUBMITTAL | Q-AS |
|       | -          | -                   | -    |
|       | -          | -                   | -    |
|       | -          | -                   | -    |
|       | -          | -                   | -    |

| SITE ADDRESS |                                       |      |       |
|--------------|---------------------------------------|------|-------|
| STREET       | 2301 South Shelley Circle Bldg. A & B |      |       |
| CITY         | Costa Mesa                            |      |       |
| STATE        | CA                                    | ZIP  | 92626 |
| JOB #:       | 26034                                 | REV: | A     |
| MOD #:       | 6                                     | REL: | N/A   |

**6.9**

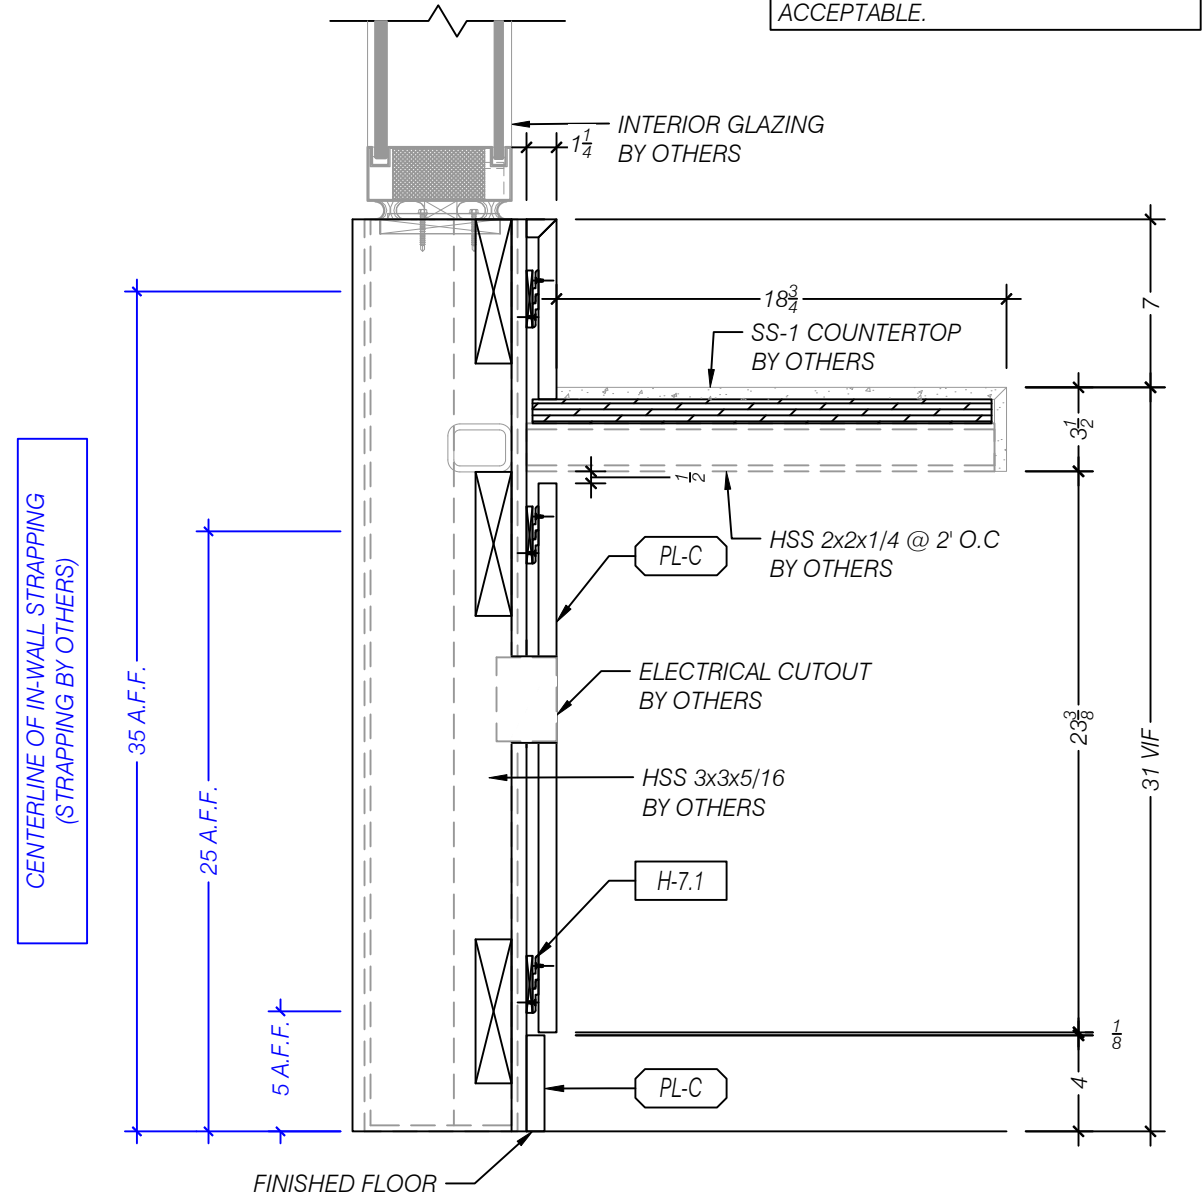

**A** SECTION - COUNTERTOP WITH PANELING  
SCALE 1:8 (1 1/2"=1'-0")  
ARCH REF: 5/AE583

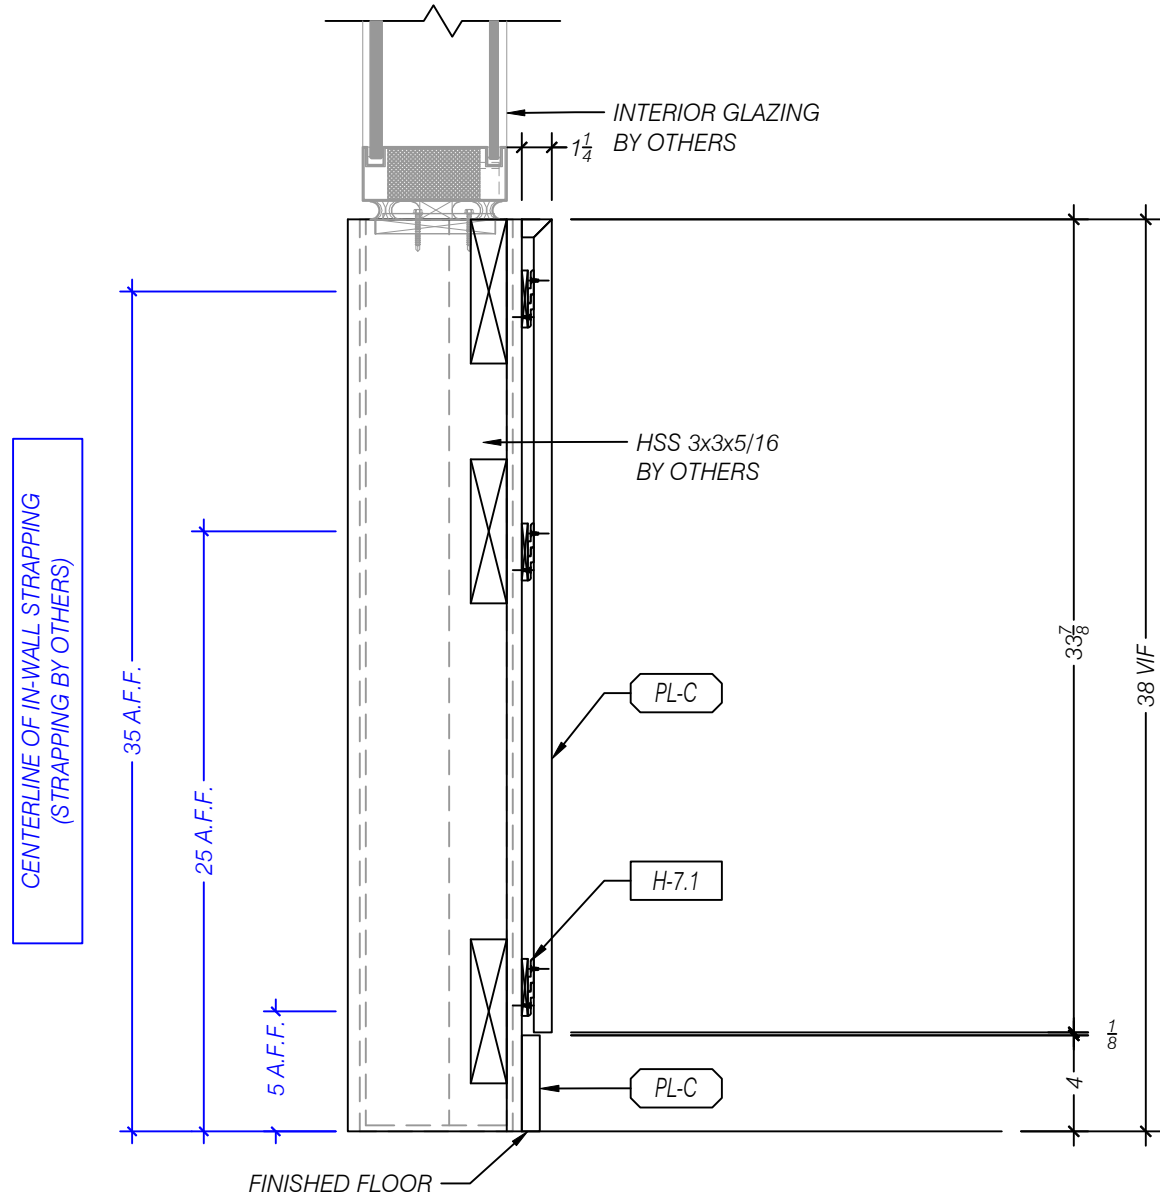


**B** SECTION - PANELING  
SCALE 1:8 (1 1/2"=1'-0")  
ARCH REF: NA

|         | MATERIALS                                                            |
|---------|----------------------------------------------------------------------|
| (PL-C)  | (PL-1, WB-2) WILSONART "HARVEST MAPLE", 7953-38, FINE VELVET TEXTURE |
|         | QTY. HARDWARE                                                        |
| (H-7.1) | X ORANGE ALUMINUM Z-CLIP HD PANEL RAIL                               |


**DGS SREOC COSTA  
MESA  
BREAK ROOM 115**

| ISSUE | DATE       | DESCRIPTION         | BY   |
|-------|------------|---------------------|------|
|       |            |                     |      |
|       | 05/05/2026 | REV-A FOR SUBMITTAL | Q-AS |
|       | -          | -                   | -    |
|       | -          | -                   | -    |
|       | -          | -                   | -    |
|       | -          | -                   | -    |

| SITE ADDRESS |                                       |      |       |
|--------------|---------------------------------------|------|-------|
| STREET       | 2301 South Shelley Circle Bldg. A & B |      |       |
| CITY         | Costa Mesa                            |      |       |
| STATE        | CA                                    | ZIP  | 92626 |
| JOB #:       | 26034                                 | REV: | A     |
| MOD #:       | 6                                     | REL: | N/A   |

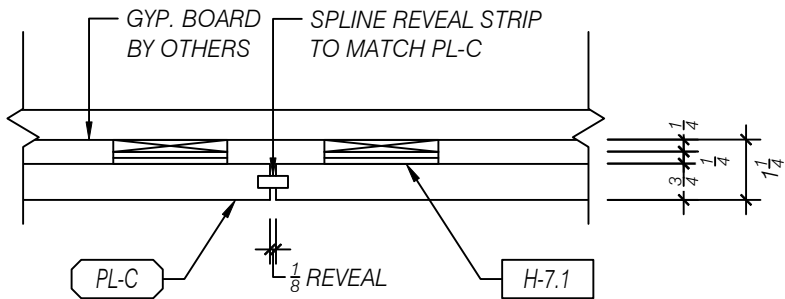

**A** ENLARGED DETAIL - PANEL TO PANEL REVEAL  
SCALE 1:4 (3"=1'-0")  
NA

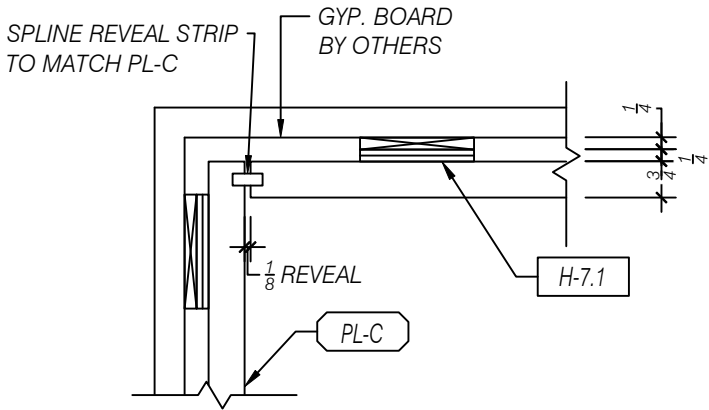


**B** ENLARGED DETAIL - PANEL TO PANEL REVEAL  
SCALE 1:4 (3"=1'-0")  
NA

|       |                                                                                                   |                                      |
|-------|---------------------------------------------------------------------------------------------------|--------------------------------------|
|       | MATERIALS                                                                                         |                                      |
| PG-A  | (CR-1) SOLID POPLAR, DELIVERED PRIMED (PREPPING, PAINTING, FILLING OF ATTACHMENT HOLES BY OTHERS) |                                      |
| PL-C  | (PL-1, WB-2) WILSONART "HARVEST MAPLE", 7953-38, FINE VELVET TEXTURE                              |                                      |
|       | QTY.                                                                                              | HARDWARE                             |
| H-7.1 | X                                                                                                 | ORANGE ALUMINUM Z-CLIP HD PANEL RAIL |

**DGS SREOC COSTA**  
**MESA**  
**BREAK ROOM 115**


| ISSUE        |                                       | BY        |
|--------------|---------------------------------------|-----------|
| DATE         | DESCRIPTION                           |           |
| 05/05/2026   | REV-A FOR SUBMITTAL                   | Q-AS      |
| -            | -                                     | -         |
| -            | -                                     | -         |
| SITE ADDRESS |                                       |           |
| STREET       | 2301 South Shelley Circle Bldg. A & B |           |
| CITY         | Costa Mesa                            |           |
| STATE        | CA                                    | ZIP 92626 |
| JOB #:       | 26034                                 | REV: A    |
| MOD #:       | 6                                     | REL: N/A  |

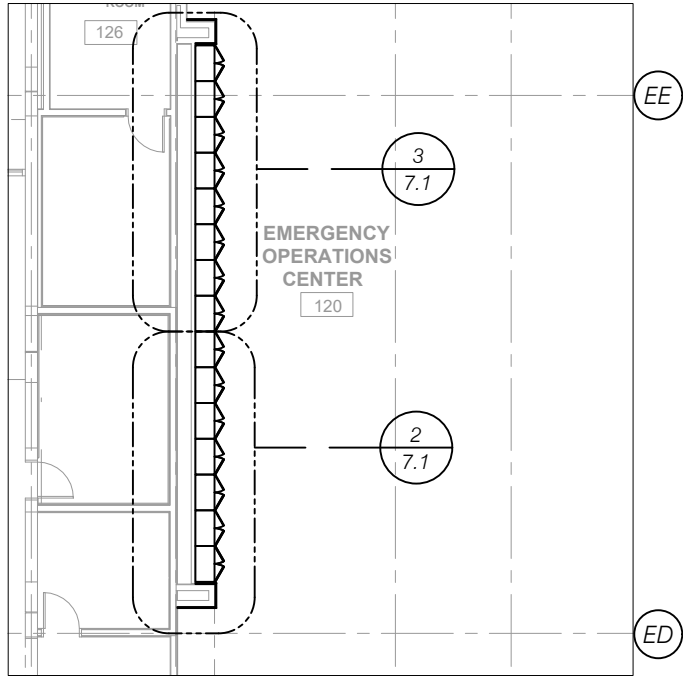

**1** KEY PLAN  
SCALE : NTS  
ARCH REF: 1/AE101.1


| NOTES |   |
|-------|---|
| 1     | ALL DIMENSIONS TO BE FIELD VERIFIED                                                                                          |
| 2     | GENERAL CONTRACTOR TO COORDINATE ALL FRAMING REQUIREMENTS WITH CMI                                                           |
| 3     | GENERAL CONTRACTOR TO COORDINATE ALL WALL TYPES, THICKNESSES AND ROUGH OPENINGS                                              |
| 4     | GENERAL CONTRACTOR & ELECTRICAL CONTRACTOR TO COORDINATE ALL ELECTRICAL BOX LOCATIONS & REQUIREMENTS WITH MILLWORK DRAWINGS  |
| 5     | GENERAL CONTRACTOR & ELECTRICAL CONTRACTOR TO COORDINATE ALL LIGHT FIXTURE FEED & SWITCHING LOCATIONS WITH MILLWORK DRAWINGS |
| 6     | GENERAL CONTRACTOR & PLUMBING CONTRACTOR TO COORDINATE ALL PLUMBING FIXTURES & INSTALLATION REQUIREMENTS                     |

| MATERIALS |          |                                                                      |
|-----------|----------|----------------------------------------------------------------------|
| (MM-A)    |          | WHITE MELAMINE                                                       |
| (PL-D)    |          | (PL-2) PIONITE "FOLKSTONE GRAY", SG241-SD, TEXTURED/SUEDE FINISH     |
| QTY.      | HARDWARE |                                                                      |
| H-1.2     | X        | SALICE 0mm CLIP-ON HINGE PLATE EURO SCREW, BARGR09/16                |
| H-1.3     | X        | SALICE 110° FO SOFT-CLOSE, LOGICA SILENTIA, C7J6AE9                  |
| H-3.0     | X        | BERENSON WIRE PULL, BN6131-2SC-P, 96mm CTC, SATIN CHROME FINISH      |
| H-4.0     | X        | HAFELE SHELF SUPPORT, 282.04.711, 5mm SHELF PIN, STEEL NICKEL-PLATED |
| H-7.1     | X        | ORANGE ALUMINUM Z-CLIP HD PANEL RAIL                                 |
| H-7.3     | X        | EAGLE ALUMINUM 1/8" CORNER ACCENT, MILL FINISH                       |

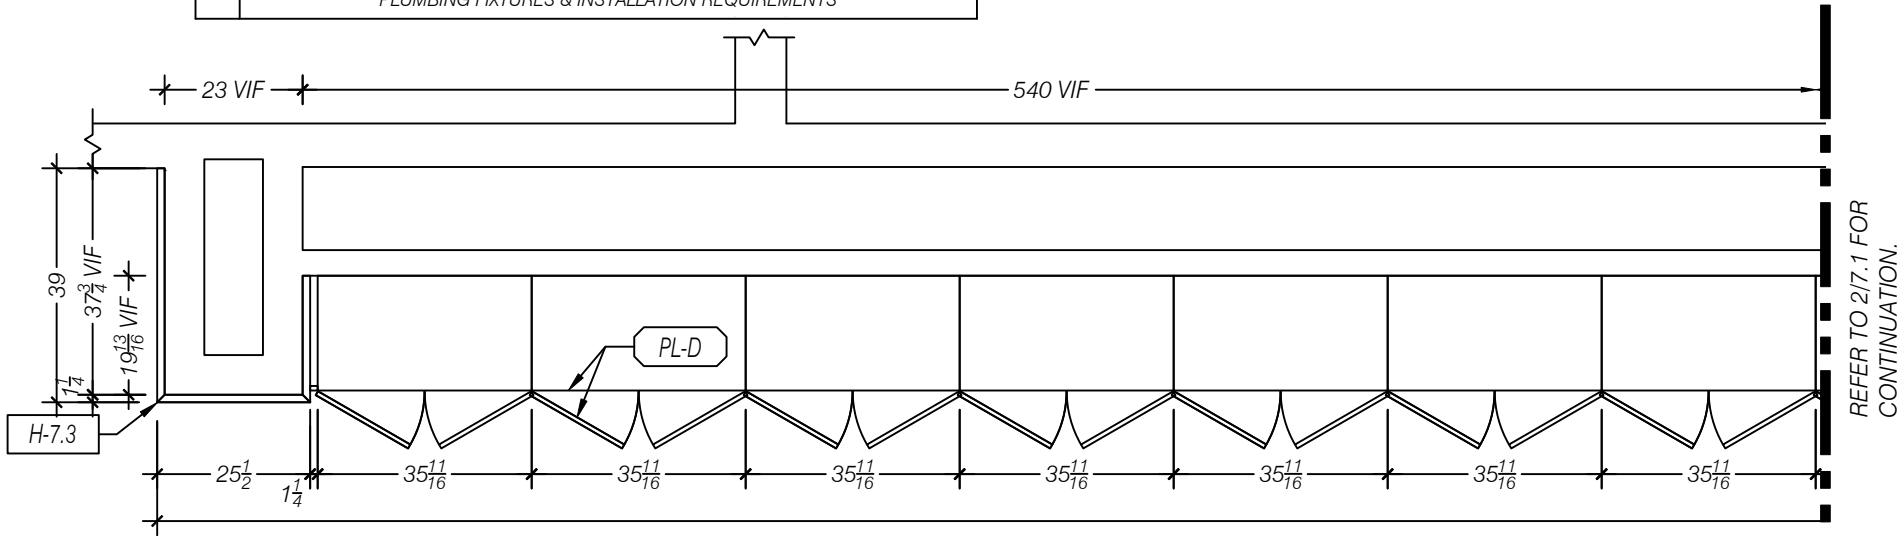

REFER TO 2/7.1 FOR CONTINUATION.

**2** PLAN - EMERGENCY OPERATIONS CENTER 120  
SCALE 1:32 (3/8"=1'-0")  
ARCH REF: 1/AE101

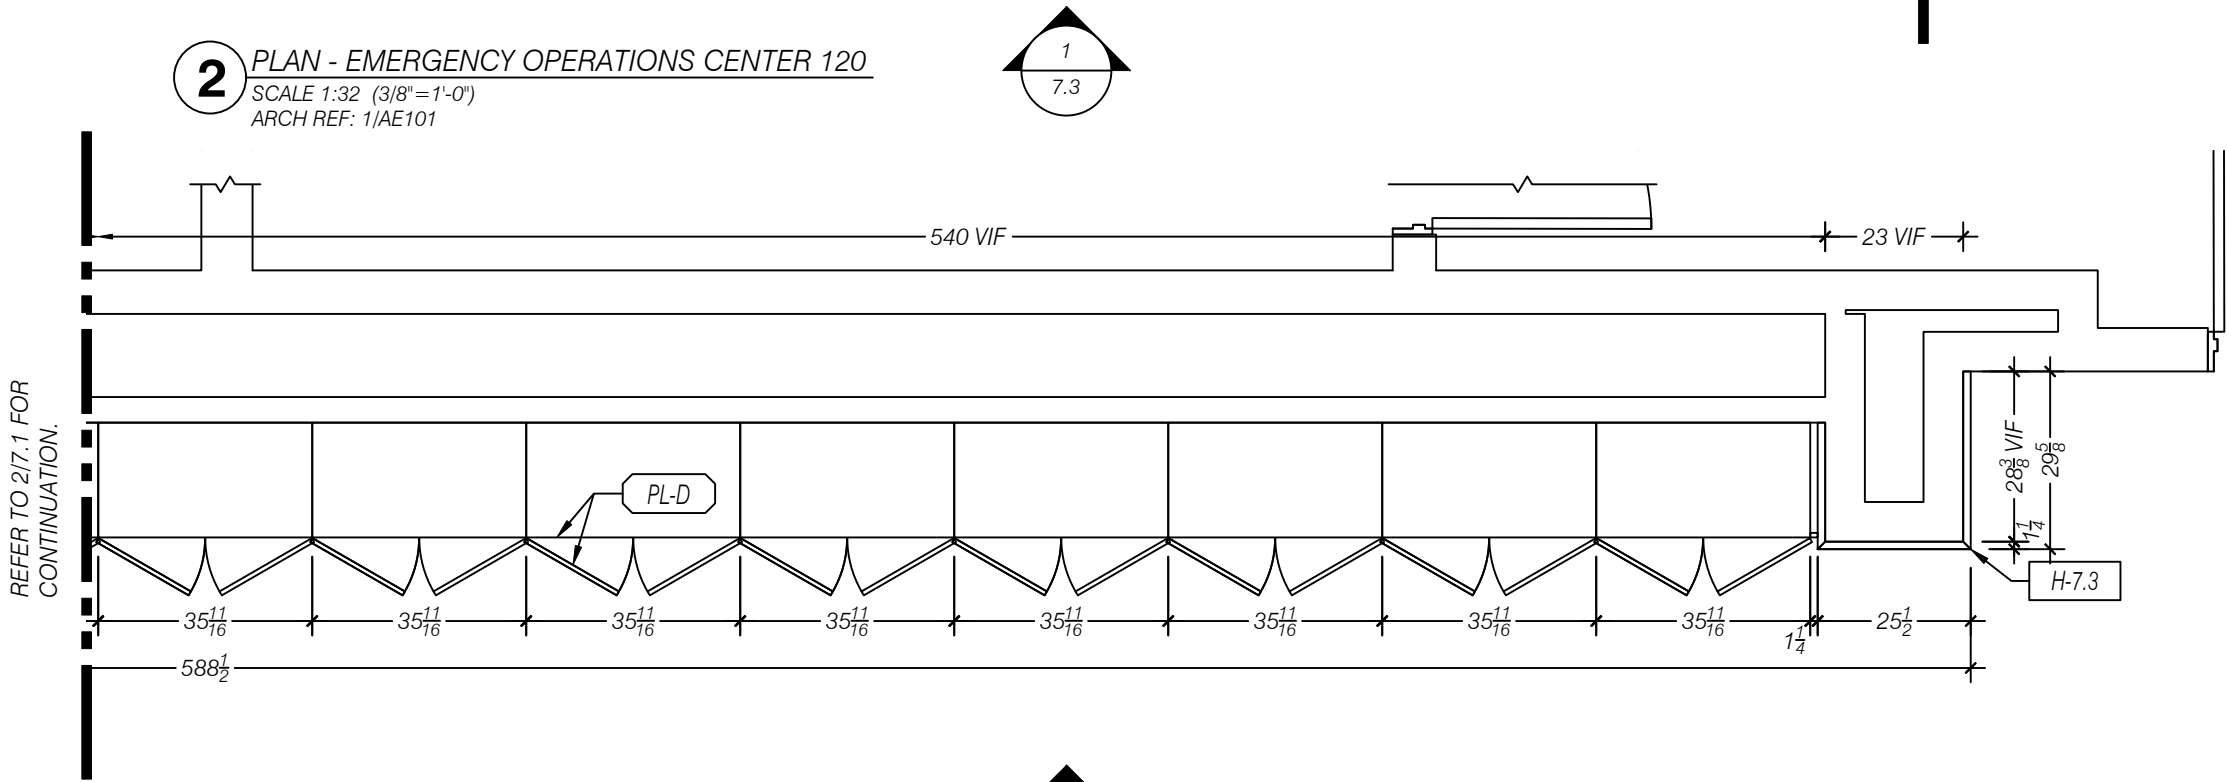

**3** PLAN - EMERGENCY OPERATIONS CENTER 120  
SCALE 1:32 (3/8"=1'-0")  
ARCH REF: 1/AE101


5640 WEST END ROAD  
ARCATA, CA 95521  
PH (707) 822-4034 FAX (707) 822-5478  
WWW.CRESTMILLWORK.COM

DGS SREOC COSTA  
MESA


EMERGENCY OPERATIONS CENTER 120

| ISSUE        |                                       | BY   |       |   |   |   |
|--------------|---------------------------------------|------|-------|---|---|---|
| DATE         | DESCRIPTION                           | Q-AS |       |   |   |   |
| 05/05/2026   | REV-A FOR SUBMITTAL                   |      | -     | - | - | - |
|              |                                       |      | -     | - | - | - |
|              |                                       |      | -     | - | - | - |
|              |                                       |      | -     | - | - | - |
|              |                                       |      | -     | - | - | - |
| SITE ADDRESS |                                       |      |       |   |   |   |
| STREET       | 2301 South Shelley Circle BLDG. A & B |      |       |   |   |   |
| CITY         | Costa Mesa                            |      |       |   |   |   |
| STATE        | CA                                    | ZIP  | 92626 |   |   |   |
| JOB #:       | 26034                                 | REV: | A     |   |   |   |
| MOD #:       | 7                                     | REL: | N/A   |   |   |   |
| 7.1          |                                       |      |       |   |   |   |

|  |        | MATERIALS                                                              |
|--|--------|------------------------------------------------------------------------|
|  | (MM-A) | WHITE MELAMINE                                                         |
|  | (PL-D) | (PL-2) PIONITE "FOLKSTONE GRAY", SG241-SD, TEXTURED/SUEDE FINISH       |
|  | QTY.   | HARDWARE                                                               |
|  | H-1.2  | X SALICE 0mm CLIP-ON HINGE PLATE EURO SCREW, BARGR09/16                |
|  | H-1.3  | X SALICE 110° FO SOFT-CLOSE, LOGICA SILENTIA, C7J6AE9                  |
|  | H-3.0  | X BERENSON WIRE PULL, BN6131-2SC-P, 96mm CTC, SATIN CHROME FINISH      |
|  | H-4.0  | X HAFELE SHELF SUPPORT, 282.04.711, 5mm SHELF PIN, STEEL NICKEL-PLATED |
|  | H-7.1  | X ORANGE ALUMINUM Z-CLIP HD PANEL RAIL                                 |
|  | H-7.3  | X EAGLE ALUMINUM 1/8" CORNER ACCENT, MILL FINISH                       |

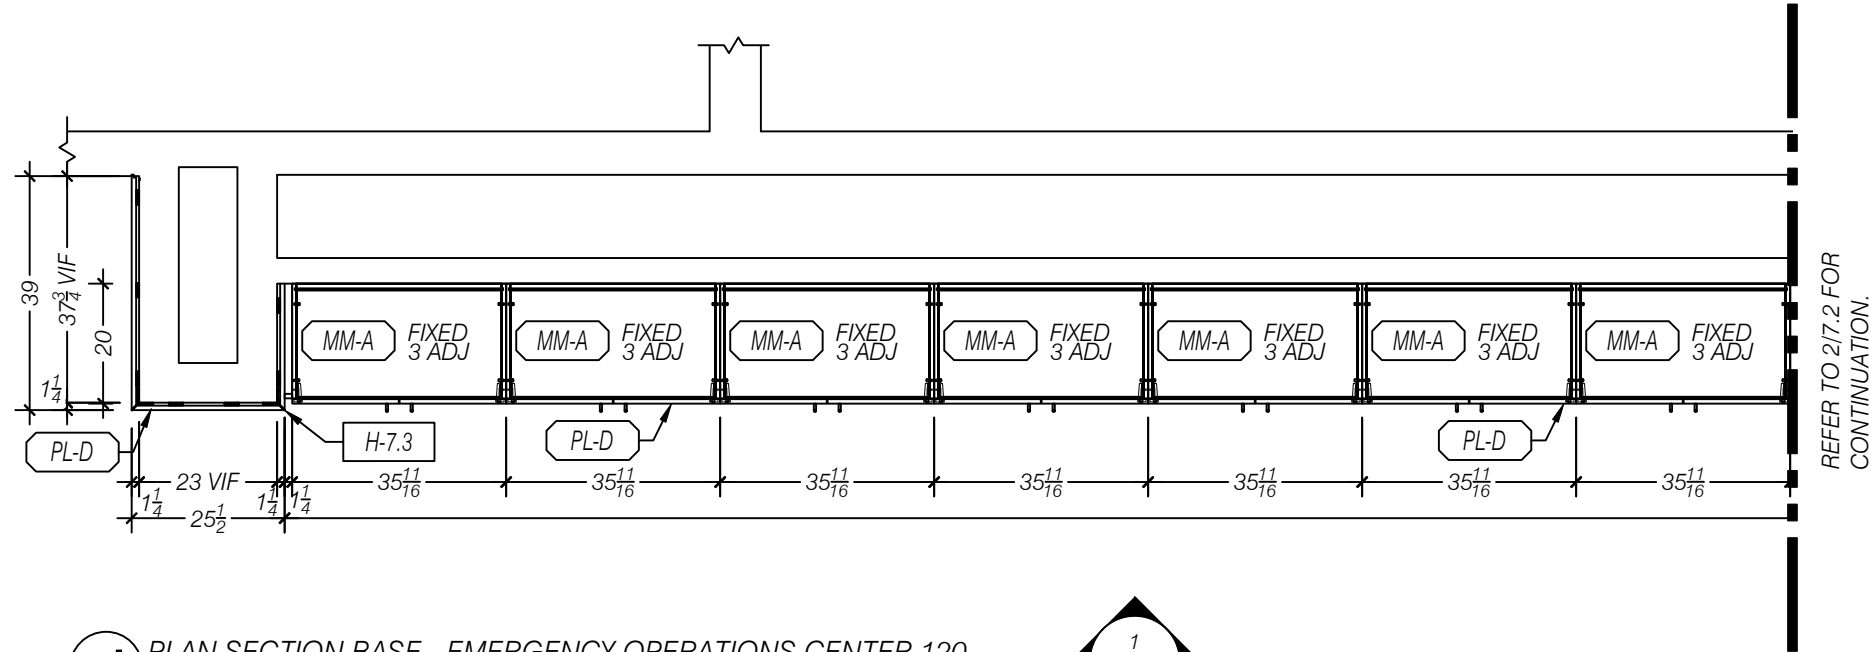

**1** PLAN SECTION BASE - EMERGENCY OPERATIONS CENTER 120  
 SCALE 1:32 (3/8"=1'-0")  
 ARCH REF: NA

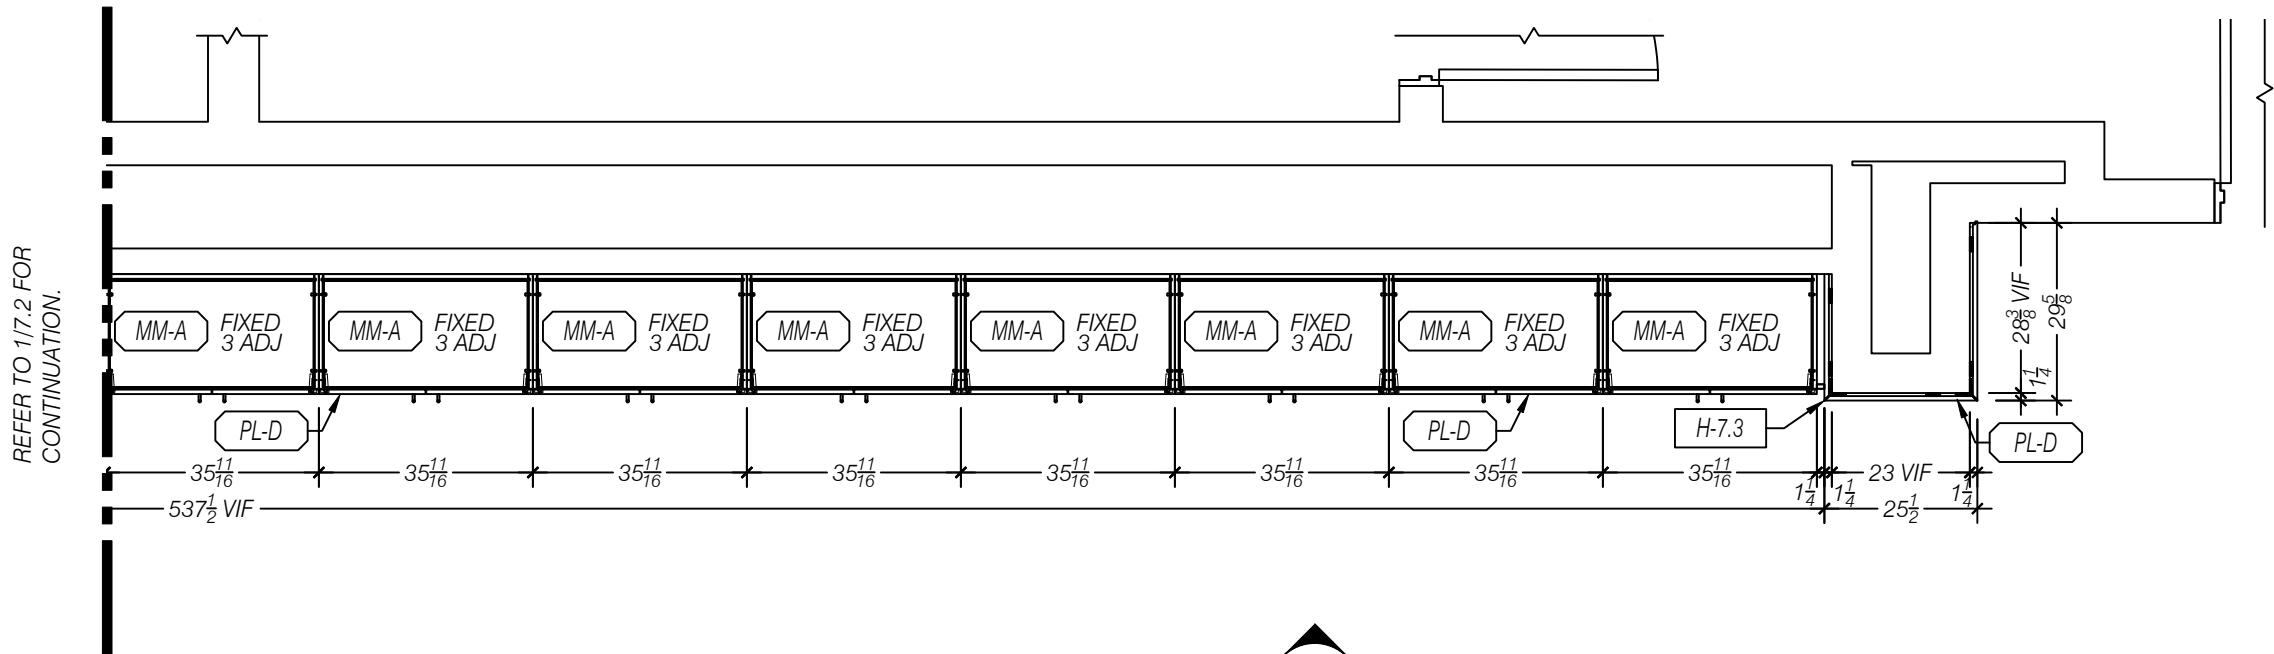

**2** PLAN SECTION BASE - EMERGENCY OPERATIONS CENTER 120  
 SCALE 1:32 (3/8"=1'-0")  
 ARCH REF: NA

5640 WEST END ROAD  
ARCATA, CA 95521  
PH (707) 822-4034 FAX (707) 822-5478  
WWW.CRESTMILLWORK.COM

DGS SREOC COSTA  
MESA


EMERGENCY OPERATIONS CENTER 120

| ISSUE        |                                          |     | BY    |      |     |   |
|--------------|------------------------------------------|-----|-------|------|-----|---|
| DATE         | DESCRIPTION                              |     |       | Q-AS |     |   |
| 05/05/2026   | REV-A FOR SUBMITTAL                      |     | -     | -    | -   | - |
|              |                                          |     | -     | -    | -   | - |
|              |                                          |     | -     | -    | -   | - |
|              |                                          |     | -     | -    | -   | - |
|              |                                          |     | -     | -    | -   | - |
| SITE ADDRESS |                                          |     |       |      |     |   |
| STREET       | 2301 South Shelley<br>Circle BLDG. A & B |     |       |      |     |   |
| CITY         | Costa Mesa                               |     |       |      |     |   |
| STATE        | CA                                       | ZIP | 92626 |      |     |   |
| JOB #:       | 26034                                    |     |       | REV: | A   |   |
| MOD #:       | 7                                        |     |       | REL: | N/A |   |
| 7.2          |                                          |     |       |      |     |   |

1 ELEVATION WEST - EMERGENCY OPERATIONS CENTER 120  
SCALE 1:32 (3/8"=1'-0")  
ARCH REF: 2/AE414

M:\Libraries\Foundation Library 25\Factory Database\26034 - DGS\Mod\_7\_Emergency\_Operations\_Center\_120.dwg 05/05/26 - 7:28pm

CENTERLINE OF IN-WALL  
STRAPPING  
(STRAPPING BY OTHERS)

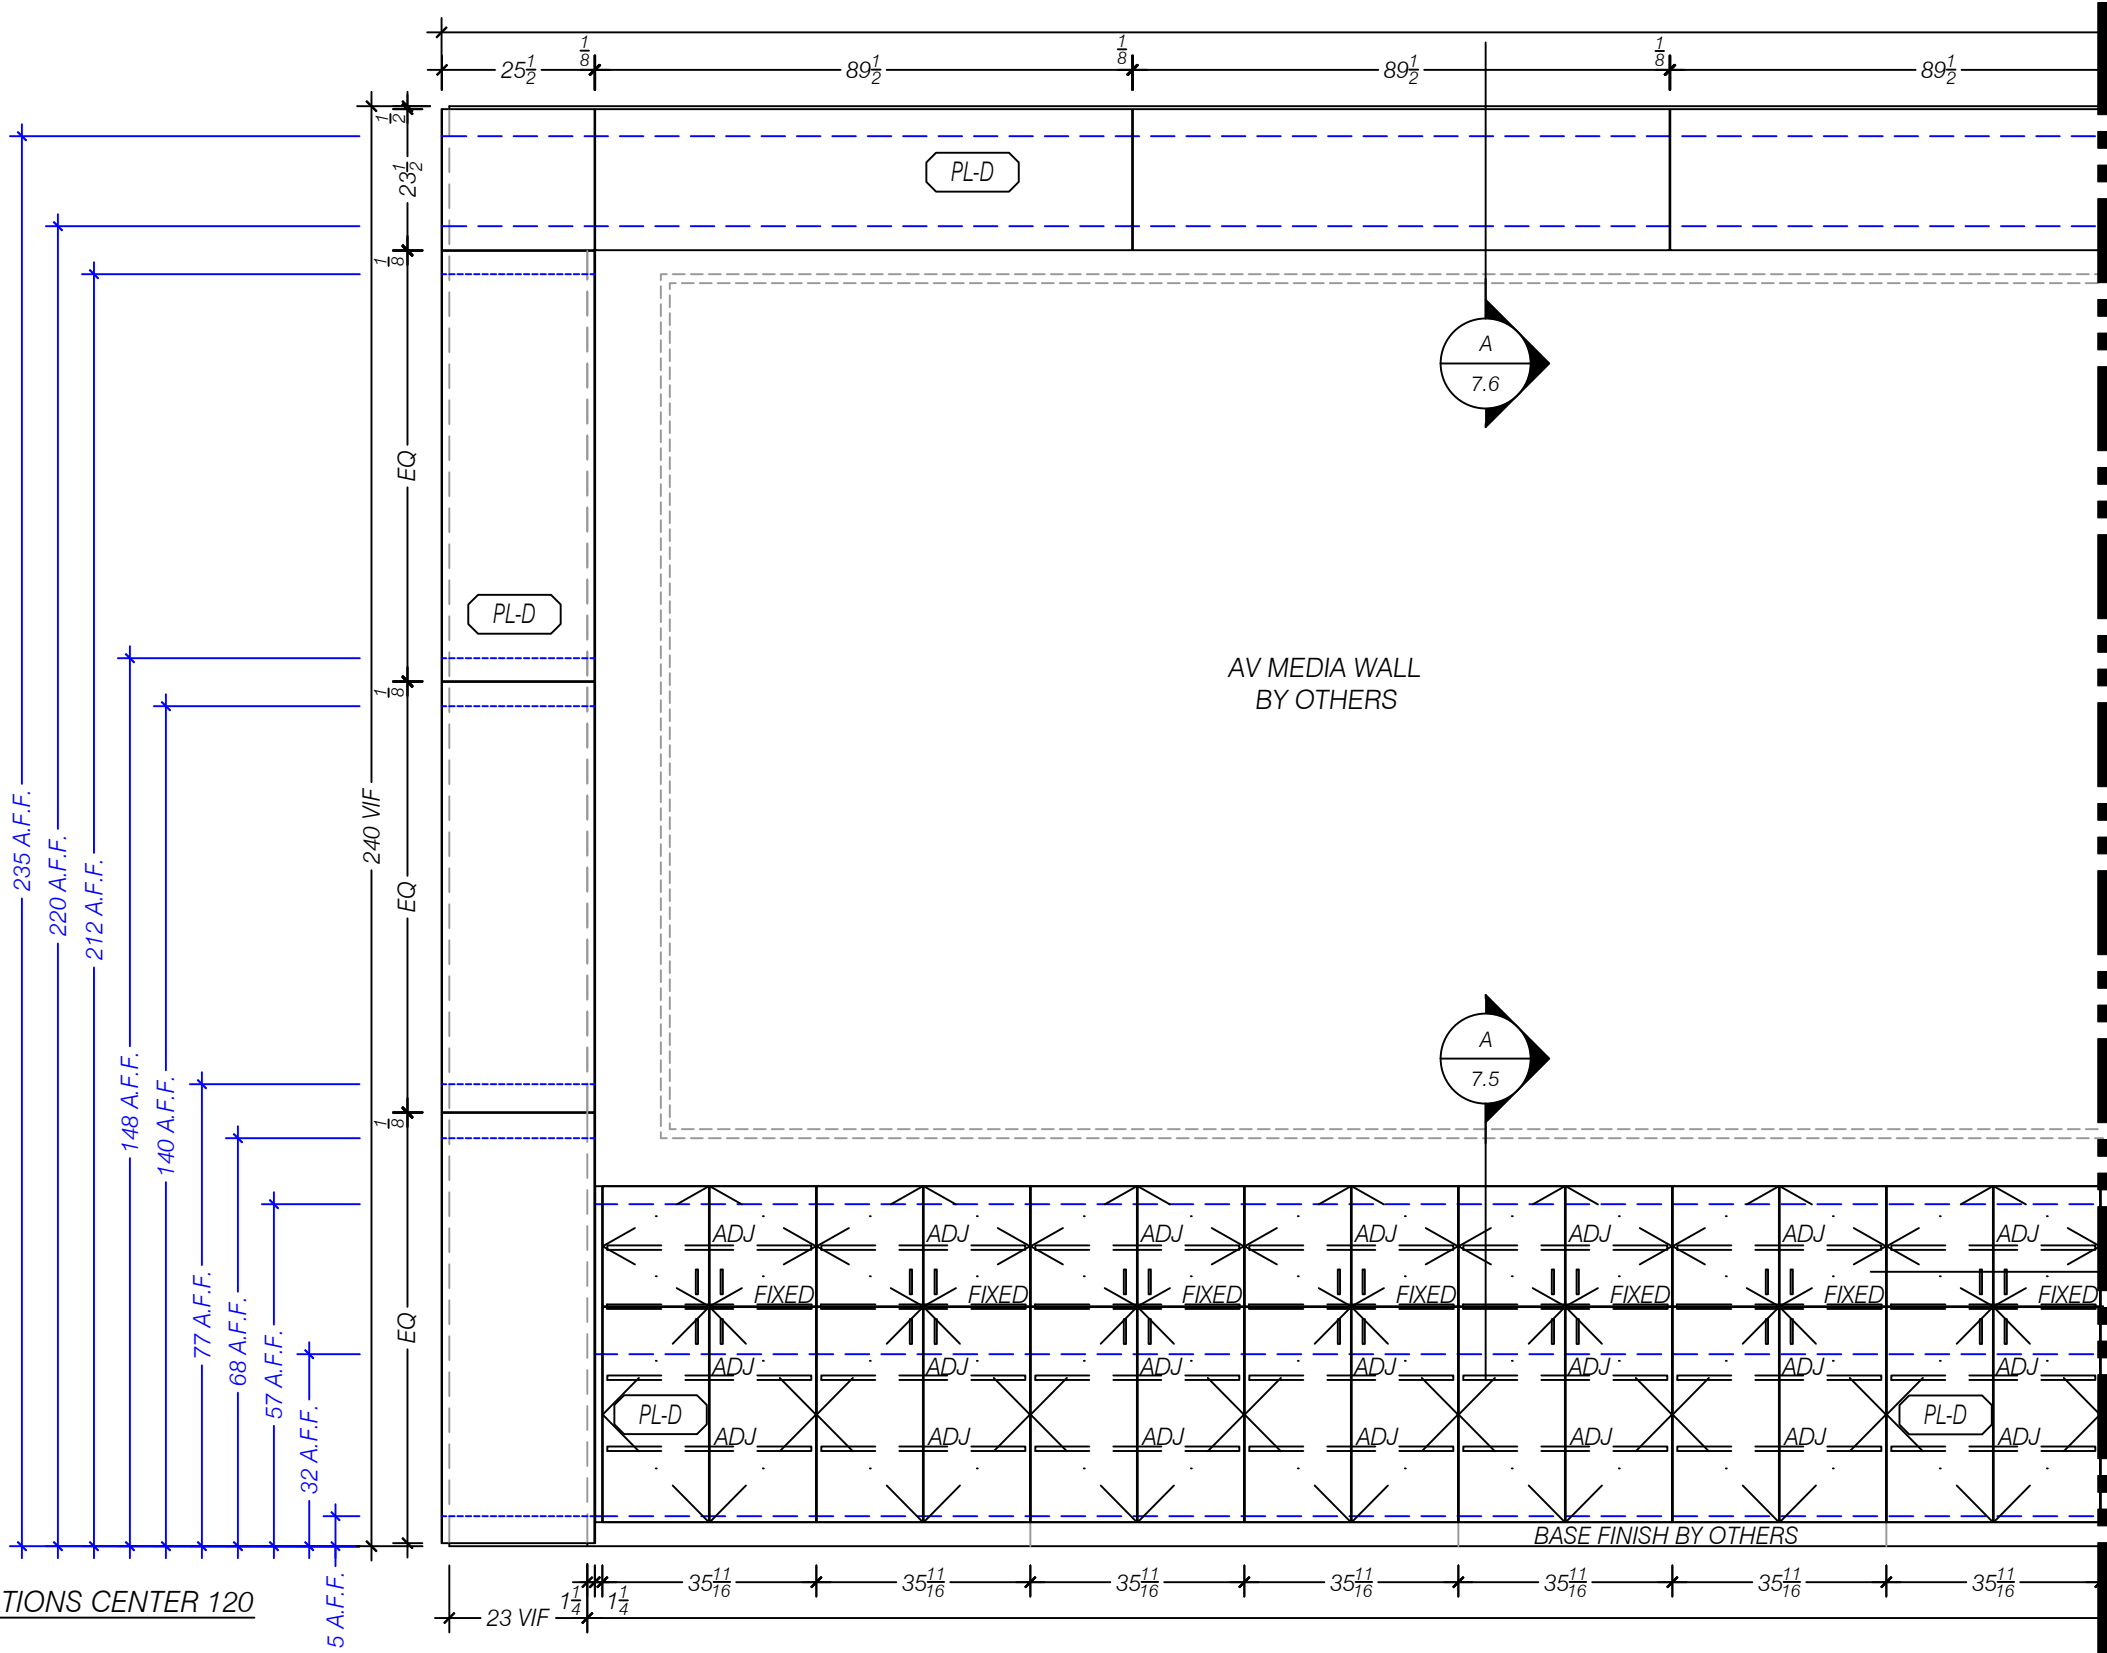

|        |      | MATERIALS                                                            |
|--------|------|----------------------------------------------------------------------|
| (MM-A) |      | WHITE MELAMINE                                                       |
| (PL-D) |      | (PL-2) PIONITE "FOLKSTONE GRAY", SG241-SD, TEXTURED/SUEDE FINISH     |
|        | QTY. | HARDWARE                                                             |
| H-1.2  | X    | SALICE 0mm CLIP-ON HINGE PLATE EURO SCREW, BARGR09/16                |
| H-1.3  | X    | SALICE 110° FO SOFT-CLOSE, LOGICA SILENTIA, C7J6AE9                  |
| H-3.0  | X    | BERENSON WIRE PULL, BN6131-2SC-P, 96mm CTC, SATIN CHROME FINISH      |
| H-4.0  | X    | HAFELE SHELF SUPPORT, 282.04.711, 5mm SHELF PIN, STEEL NICKEL-PLATED |
| H-7.1  | X    | ORANGE ALUMINUM Z-CLIP HD PANEL RAIL                                 |
| H-7.3  | X    | EAGLE ALUMINUM 1/8" CORNER ACCENT, MILL FINISH                       |



DGS SREOC COSTA  
MESA

EMERGENCY OPERATIONS CENTER 120

| ISSUE              | DESCRIPTION | BY   |
|--------------------|-------------|------|
| DATE               | 05/05/2026  | Q-AS |
| REVA FOR SUBMITTAL | -           | -    |
| -                  | -           | -    |
| -                  | -           | -    |
| -                  | -           | -    |
| -                  | -           | -    |

| SITE ADDRESS |                                       |      |       |
|--------------|---------------------------------------|------|-------|
| STREET       | 2301 South Shelley Circle BLDG. A & B |      |       |
| CITY         | Costa Mesa                            |      |       |
| STATE        | CA                                    | ZIP  | 92626 |
| JOB #:       | 26034                                 | REV: | A     |
| MOD #:       | 7                                     | REL: | N/A   |


7.3

© CRESTMILLWORK, INC.

CRESTMILLWORK

5640 WEST END ROAD  
ARCATA, CA 95521  
PH (707) 822-4034 FAX (707) 822-5478  
WWW.CRESTMILLWORK.COM

|                                                                                     |                                                                           |
|-------------------------------------------------------------------------------------|---------------------------------------------------------------------------|
|   | MATERIALS                                                                 |
| (MM-A)                                                                              | WHITE MELAMINE                                                            |
| (PL-D)                                                                              | (PL-2) PIONITE "FOLKSTONE GRAY", SG241-SD, TEXTURED/SUEDE FINISH          |
|  | QTY. <b>HARDWARE</b>                                                      |
| H-1.2                                                                               | X    SALICE 0mm CLIP-ON HINGE PLATE EURO SCREW, BARGR09/16                |
| H-1.3                                                                               | X    SALICE 110° FO SOFT-CLOSE, LOGICA SILENTIA, C7J6AE9                  |
| H-3.0                                                                               | X    BERENSON WIRE PULL, BN6131-2SC-P, 96mm CTC, SATIN CHROME FINISH      |
| H-4.0                                                                               | X    HAFELE SHELF SUPPORT, 282.04.711, 5mm SHELF PIN, STEEL NICKEL-PLATED |
| H-7.1                                                                               | X    ORANGE ALUMINUM Z-CLIP HD PANEL RAIL                                 |
| H-7.3                                                                               | X    EAGLE ALUMINUM 1/8" CORNER ACCENT, MILL FINISH                       |

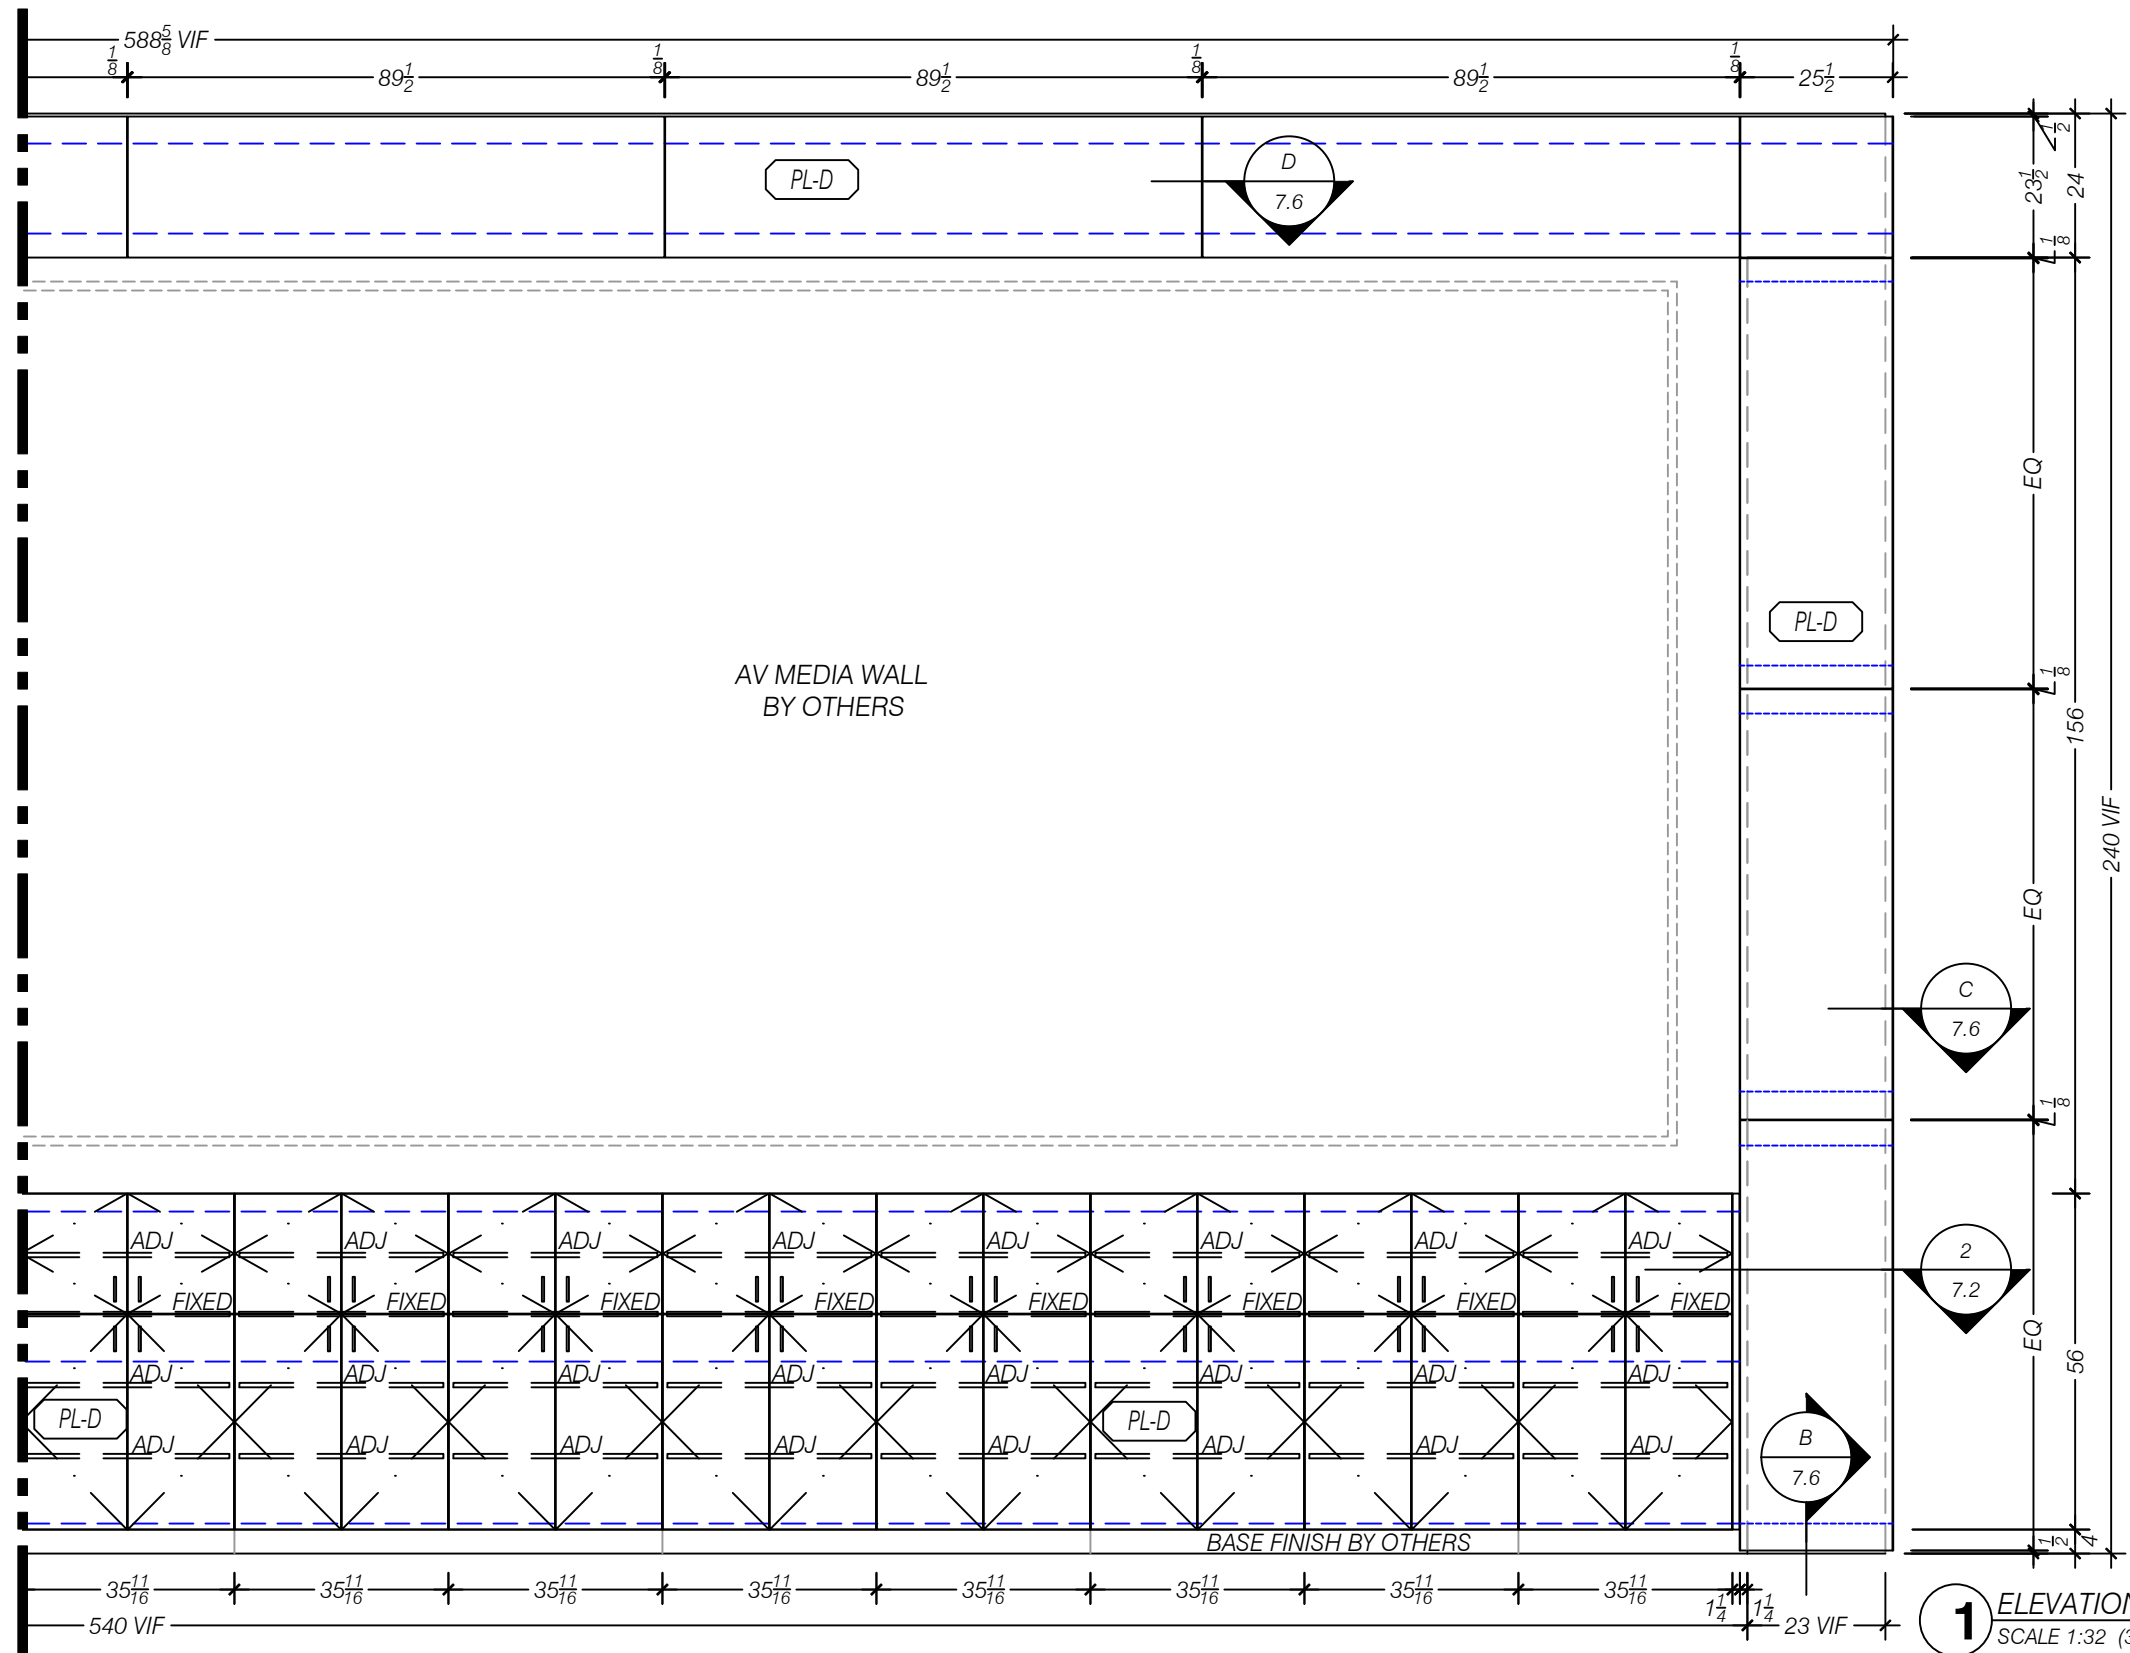


REFER TO 1/7.3 FOR  
CONTINUATION.

|  <b>CRESTMARK<br/>MILLWORK</b>                  |                     |                                       |  | 5640 WEST END ROAD<br>ARCATA, CA 95521<br>PH (707) 822-4034 FAX (707) 822-5478<br>WWW.CRESTMARKMILLWORK.COM |  |       |  |
|---|---------------------|---------------------------------------|--|---|--|-------|--|
| <h1 style="text-align: center;">DGS SREOC COSTA<br/>MESA</h1> <h2 style="text-align: center;">EMERGENCY OPERATIONS CENTER 120</h2> |                     |                                       |  |   |  |       |  |
| ISSUE   |                     |                                       |  |   |  |       |  |
| DATE   | DESCRIPTION         | BY                                    |  |   |  |       |  |
| 05/05/2026   | REV-A FOR SUBMITTAL | Q-AS                                  |  |   |  |       |  |
| -   | -                   | -                                     |  |   |  |       |  |
| -   | -                   | -                                     |  |   |  |       |  |
| <b>SITE ADDRESS</b>   |                     |                                       |  |   |  |       |  |
| <b>STREET</b>   |                     | 2301 South Shelley Circle BLDG. A & B |  |   |  |       |  |
| <b>CITY</b>   |                     | Costa Mesa                            |  |   |  |       |  |
| <b>STATE</b>   |                     | CA                                    |  | <b>ZIP</b>                                                                                                  |  | 92626 |  |
| <b>JOB #:</b> 26034   |                     |                                       |  | <b>REV:</b> A                                                                                               |  |       |  |
| <b>MOD #:</b> 7   |                     |                                       |  | <b>REL:</b> N/A                                                                                             |  |       |  |
| <h1>7.4</h1>   |                     |                                       |  |   |  |       |  |

ARCHITECT NOTE:  
WE HAVE PROVIDED THE 20" DEPTH CABINET  
BASED ON THE ARCH PLAN AE101.1.PLEASE  
CONFORM.

CENTERLINE OF IN-WALL STRAPPING  
(STRAPPING BY OTHERS)

|        |   | MATERIALS                                                            |
|--------|---|----------------------------------------------------------------------|
| (MM-A) |   | WHITE MELAMINE                                                       |
| (PL-D) |   | (PL-2) PIONITE "FOLKSTONE GRAY", SG241-SD, TEXTURED/SUEDE FINISH     |
| QTY.   |   | HARDWARE                                                             |
| H-1.2  | X | SALICE 0mm CLIP-ON HINGE PLATE EURO SCREW, BARGR09/16                |
| H-1.3  | X | SALICE 110° FO SOFT-CLOSE, LOGICA SILENTIA, C7J6AE9                  |
| H-3.0  | X | BERENSON WIRE PULL, BN6131-2SC-P, 96mm CTC, SATIN CHROME FINISH      |
| H-4.0  | X | HAFELE SHELF SUPPORT, 282.04.711, 5mm SHELF PIN, STEEL NICKEL-PLATED |
| H-7.1  | X | ORANGE ALUMINUM Z-CLIP HD PANEL RAIL                                 |
| H-7.3  | X | EAGLE ALUMINUM 1/8" CORNER ACCENT, MILL FINISH                       |

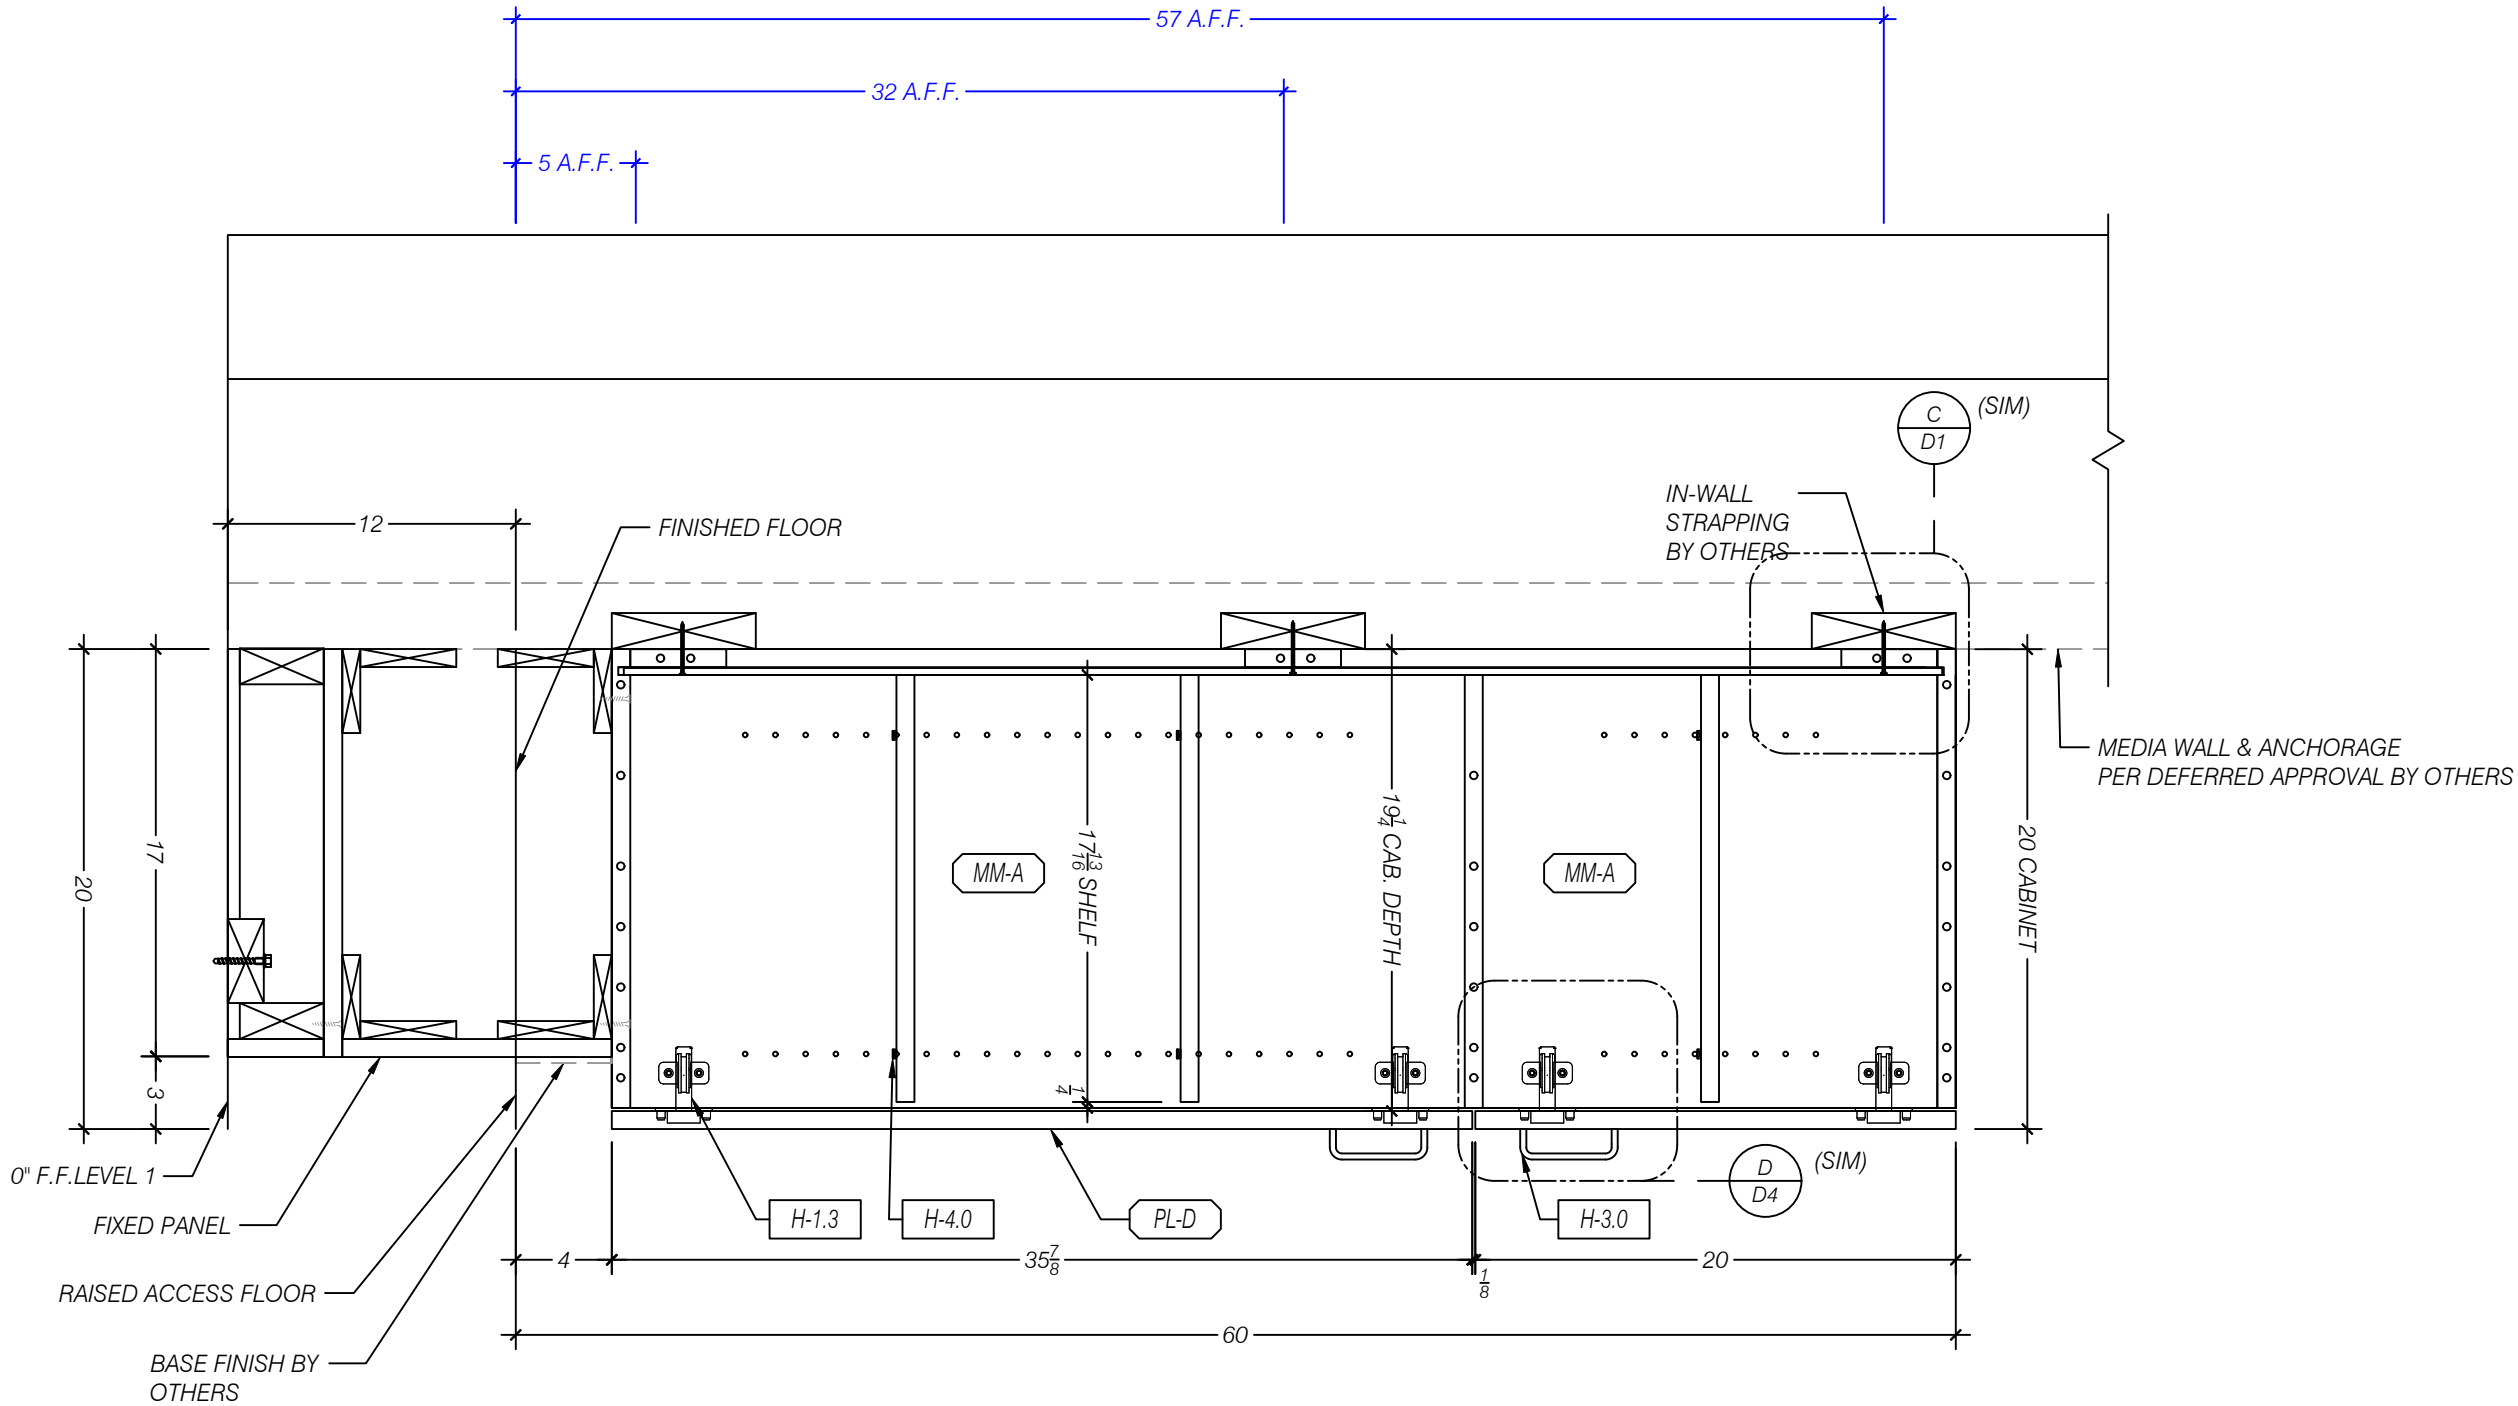


**A** SECTION - AV MEDIA WALL CABINET  
SCALE 1:8 (1 1/2"=1'-0")  
ARCH REF: 8/AE583


**DGS SREOC COSTA**  
**MESA**  
**EMERGENCY OPERATIONS CENTER 120**

| ISSUE | DATE       | DESCRIPTION         | BY   |
|-------|------------|---------------------|------|
|       | 05/05/2026 | REV-A FOR SUBMITTAL | Q-AS |
|       |            |                     |      |
|       |            |                     |      |
|       |            |                     |      |
|       |            |                     |      |


| SITE ADDRESS |                                       |      |       |
|--------------|---------------------------------------|------|-------|
| STREET       | 2301 South Shelley Circle BLDG. A & B |      |       |
| CITY         | Costa Mesa                            |      |       |
| STATE        | CA                                    | ZIP  | 92626 |
| JOB #:       | 26034                                 | REV: | A     |
| MOD #:       | 7                                     | REL: | N/A   |

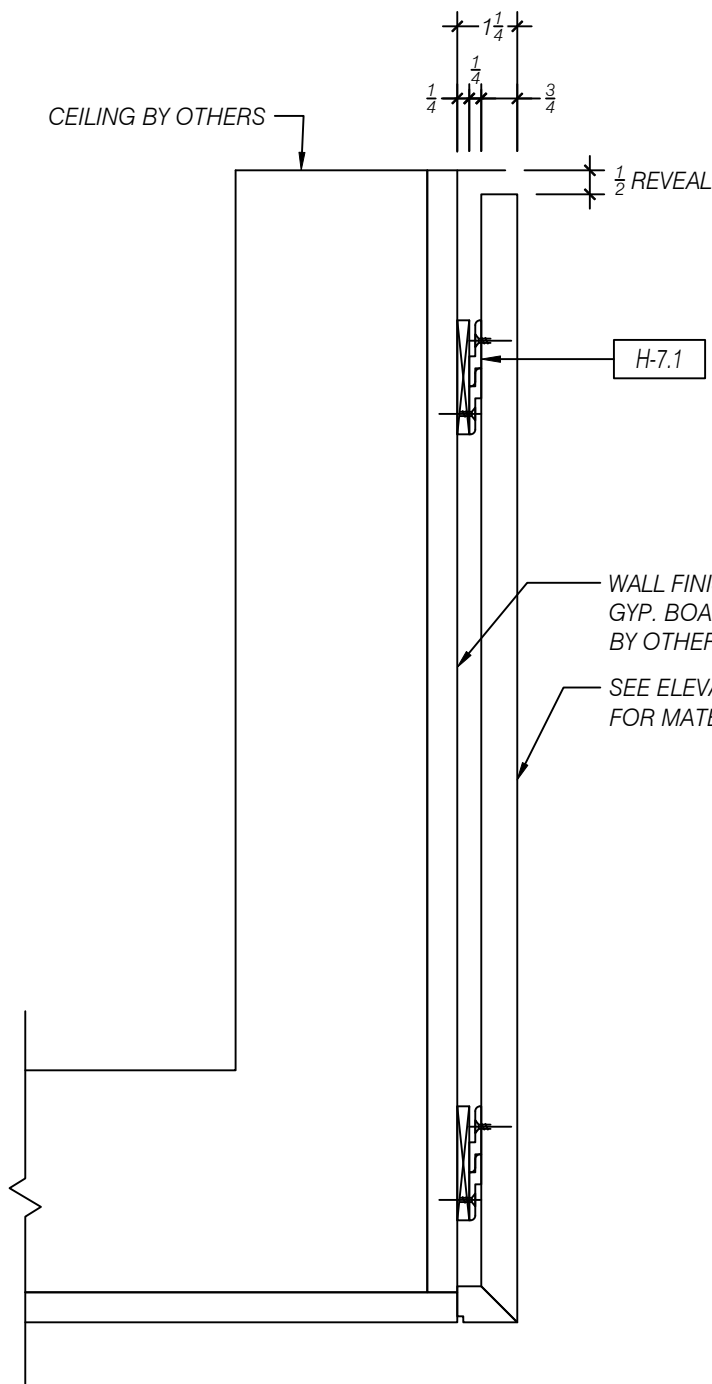


**A** ENLARGED DETAIL - WALL PANELING  
SCALE 1:4 (3"=1'-0")  
ARCH REF: NA

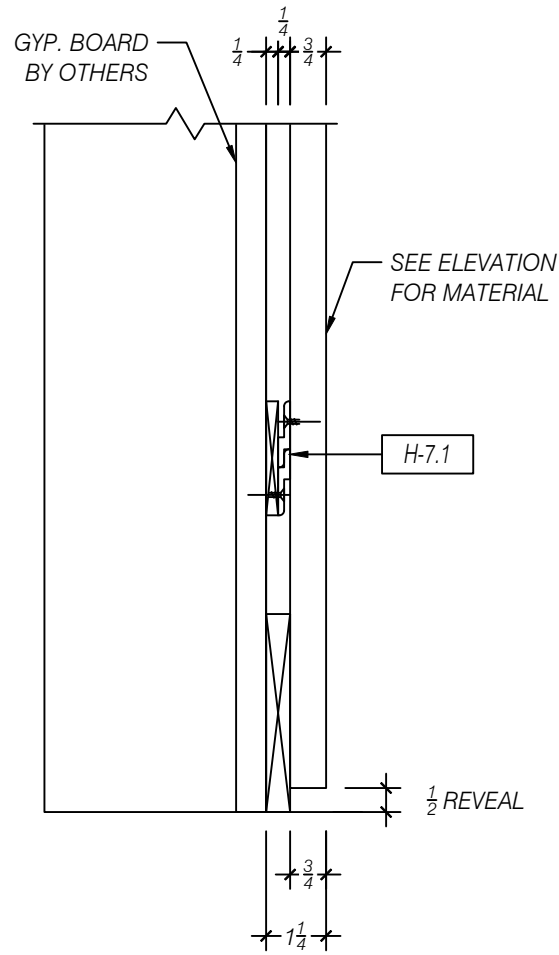

**B** ENLARGED DETAIL - PANEL TO BASE  
SCALE 1:4 (3"=1'-0")  
ARCH REF: NA

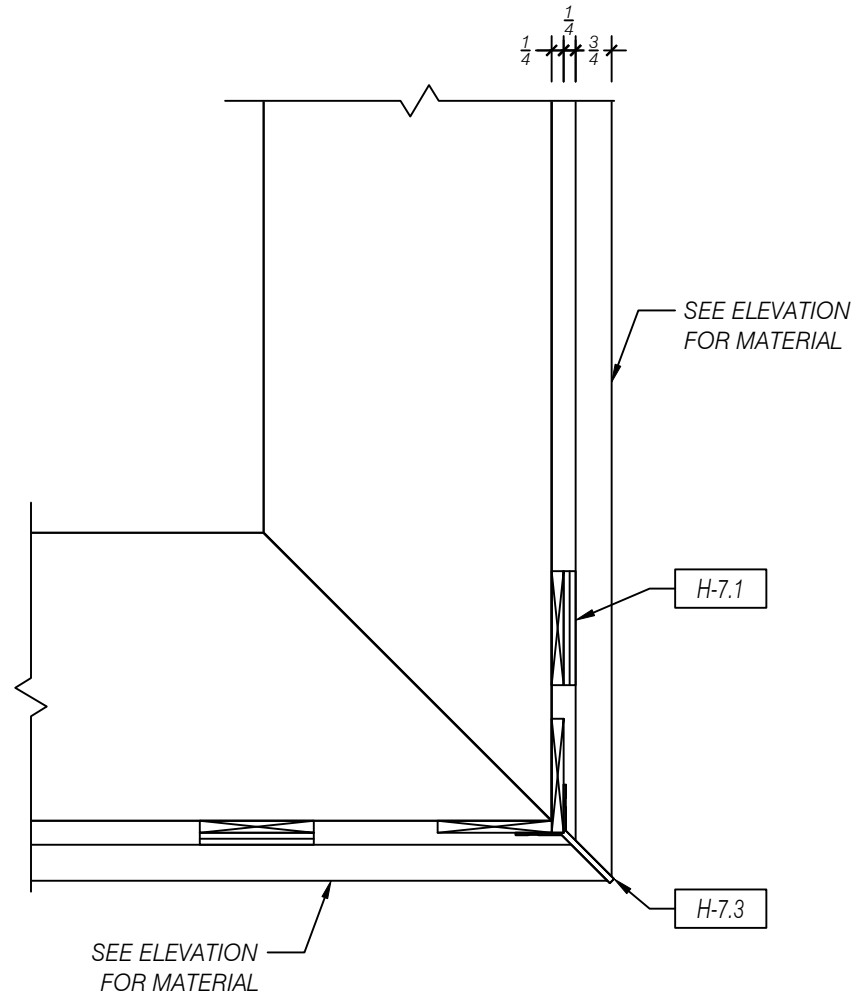

**C** ENLARGED DETAIL - P-LAM VERTICAL CORNER TRIM  
SCALE 1:4 (3"=1'-0")  
ARCH REF: 9/584

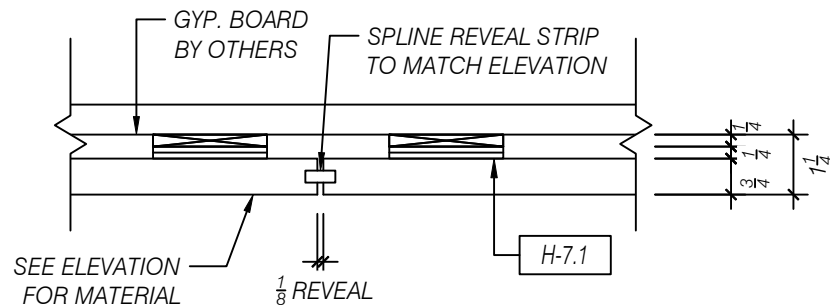

**D** ENLARGED DETAIL - PANEL TO PANEL REVEAL  
SCALE 1:4 (3"=1'-0")  
ARCH REF: NA

|        |      | MATERIALS                                                            |
|--------|------|----------------------------------------------------------------------|
| (MM-A) |      | WHITE MELAMINE                                                       |
| (PL-D) |      | (PL-2) PIONITE "FOLKSTONE GRAY", SG241-SD, TEXTURED/SUEDE FINISH     |
|        | QTY. | HARDWARE                                                             |
| H-1.2  | X    | SALICE 0mm CLIP-ON HINGE PLATE EURO SCREW, BARGR09/16                |
| H-1.3  | X    | SALICE 110° FO SOFT-CLOSE, LOGICA SILENTIA, C7J6AE9                  |
| H-3.0  | X    | BERENSON WIRE PULL, BN6131-2SC-P, 96mm CTC, SATIN CHROME FINISH      |
| H-4.0  | X    | HAFELE SHELF SUPPORT, 282.04.711, 5mm SHELF PIN, STEEL NICKEL-PLATED |
| H-7.1  | X    | ORANGE ALUMINUM Z-CLIP HD PANEL RAIL                                 |
| H-7.3  | X    | EAGLE ALUMINUM 1/8" CORNER ACCENT, MILL FINISH                       |


# **DGS SREOC COSTA MESA**

**EMERGENCY OPERATIONS CENTER 120**

| ISSUE | DESCRIPTION        | BY   |
|-------|--------------------|------|
|       | REVA FOR SUBMITTAL | Q-AS |
| DATE  | 05/05/2026         |      |
|       |                    |      |
|       |                    |      |
|       |                    |      |

| SITE ADDRESS |                                       |      |       |
|--------------|---------------------------------------|------|-------|
| STREET       | 2301 South Shelley Circle BLDG. A & B |      |       |
| CITY         | Costa Mesa                            |      |       |
| STATE        | CA                                    | ZIP  | 92626 |
| JOB #:       | 26034                                 | REV: | A     |
| MOD #:       | 7                                     | REL: | N/A   |

**7.6**

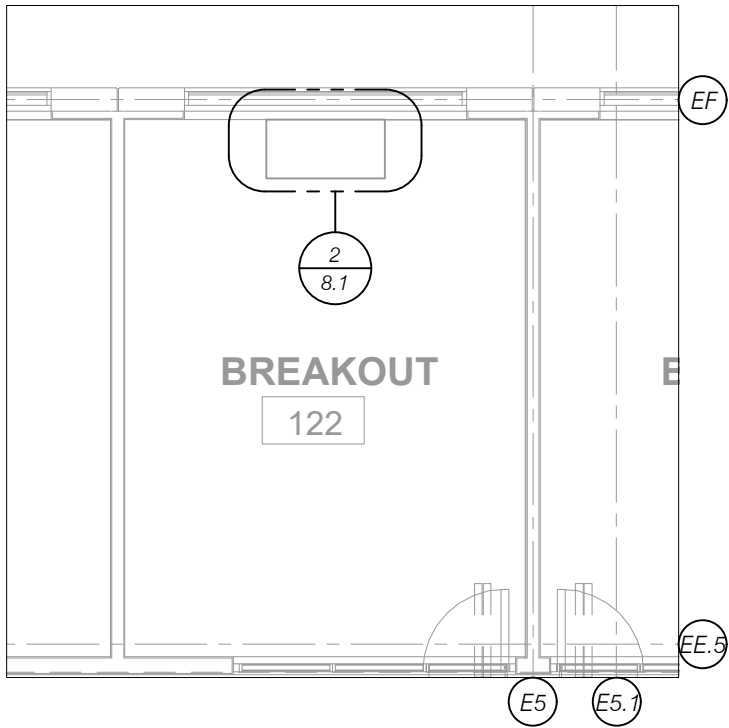


**1** KEY PLAN  
SCALE: NTS  
ARCH REF: 1/AE101.1


| NOTES |   |
|-------|---|
| 1     | ALL DIMENSIONS TO BE FIELD VERIFIED                                                                                          |
| 2     | GENERAL CONTRACTOR TO COORDINATE ALL FRAMING REQUIREMENTS WITH CMI                                                           |
| 3     | GENERAL CONTRACTOR TO COORDINATE ALL WALL TYPES, THICKNESSES AND ROUGH OPENINGS                                              |
| 4     | GENERAL CONTRACTOR & ELECTRICAL CONTRACTOR TO COORDINATE ALL ELECTRICAL BOX LOCATIONS & REQUIREMENTS WITH MILLWORK DRAWINGS  |
| 5     | GENERAL CONTRACTOR & ELECTRICAL CONTRACTOR TO COORDINATE ALL LIGHT FIXTURE FEED & SWITCHING LOCATIONS WITH MILLWORK DRAWINGS |
| 6     | GENERAL CONTRACTOR & PLUMBING CONTRACTOR TO COORDINATE ALL PLUMBING FIXTURES & INSTALLATION REQUIREMENTS                     |

| MATERIALS |                                                                      |                                                                                     |
|-----------|----------------------------------------------------------------------|-------------------------------------------------------------------------------------|
| (MM-A)    | WHITE MELAMINE                                                       |                                                                                     |
| (PL-C)    | (PL-1, WB-2) WILSONART "HARVEST MAPLE", 7953-38, FINE VELVET TEXTURE |                                                                                     |
| QTY.      | HARDWARE                                                             |                                                                                     |
| H-1.2     | X                                                                    | SALICE 0mm CLIP-ON HINGE PLATE EURO SCREW, BARGR09/16                               |
| H-1.3     | X                                                                    | SALICE 110° FO SOFT-CLOSE, LOGICA SILENTIA, C7J6AE9                                 |
| H-3.0     | X                                                                    | BERENSON WIRE PULL, BN6131-2SC-P, 96mm CTC, SATIN CHROME FINISH                     |
| H-4.0     | X                                                                    | HAFELE SHELF SUPPORT, 282.04.711, 5mm SHELF PIN, STEEL NICKEL-PLATED                |
| H-9.5     | X                                                                    | MOCKETT, GT-METAL AIR VENT GRILLE, 17W" x 4"H OPENING, MATTE BLACK FINISH W/ MESH/3 |

| BREAKOUT TYPICAL SCHEDULE |       |           |                |                     |           |           |
|---------------------------|-------|-----------|----------------|---------------------|-----------|-----------|
| LEVEL                     | ROOM# | ROOM NAME | ARCH PLAN REF. | ARCH ELEVATION REF. | PLAN REF. | DIRECTION |
| 1                         | 121   | BREAKOUT  | 1/AE101.1      | 6/AE407 (SIM)       | 1/FP.1    | NORTH     |
| 1                         | 122   | BREAKOUT  | 1/AE101.1      | 6/AE407             | 1/FP.1    | NORTH     |
| 1                         | 123   | BREAKOUT  | 1/AE101.1      | 6/AE407 (SIM)       | 1/FP.1    | NORTH     |
| 1                         | 124   | BREAKOUT  | 1/AE101.1      | 6/AE407 (SIM)       | 1/FP.1    | NORTH     |

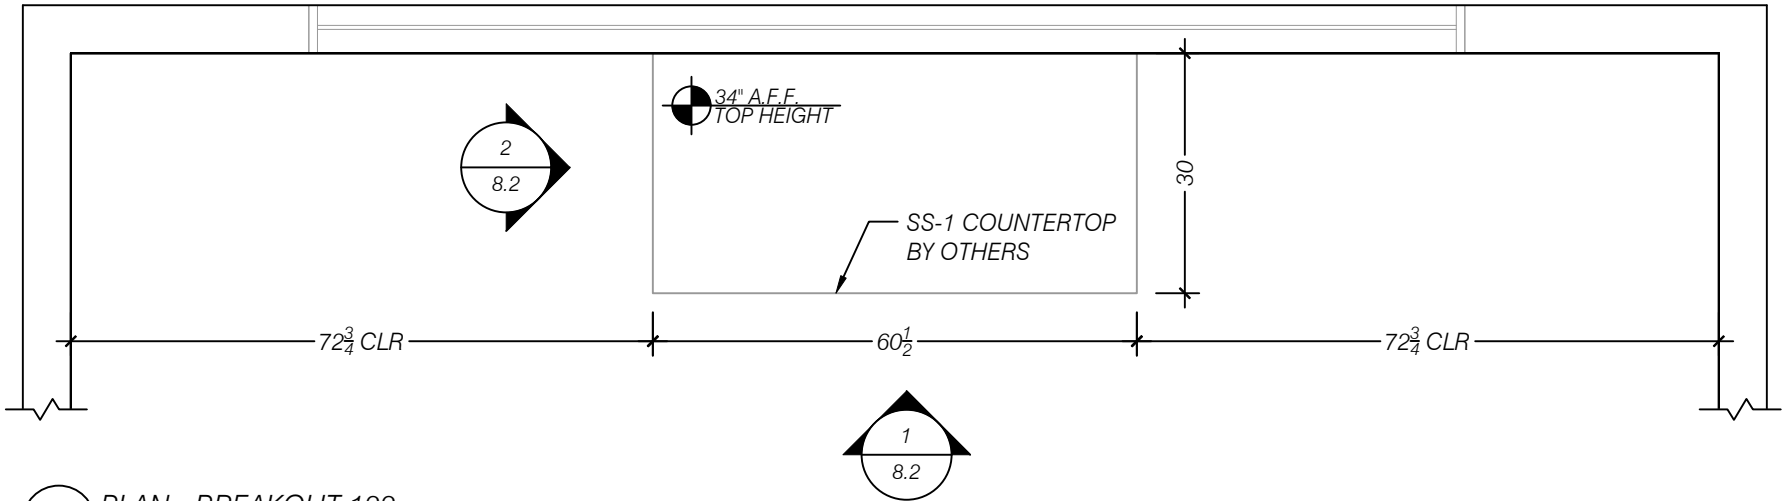

**2** PLAN - BREAKOUT 122  
SCALE 1:12 (1"=1'-0")  
ARCH REF: 6/AE407

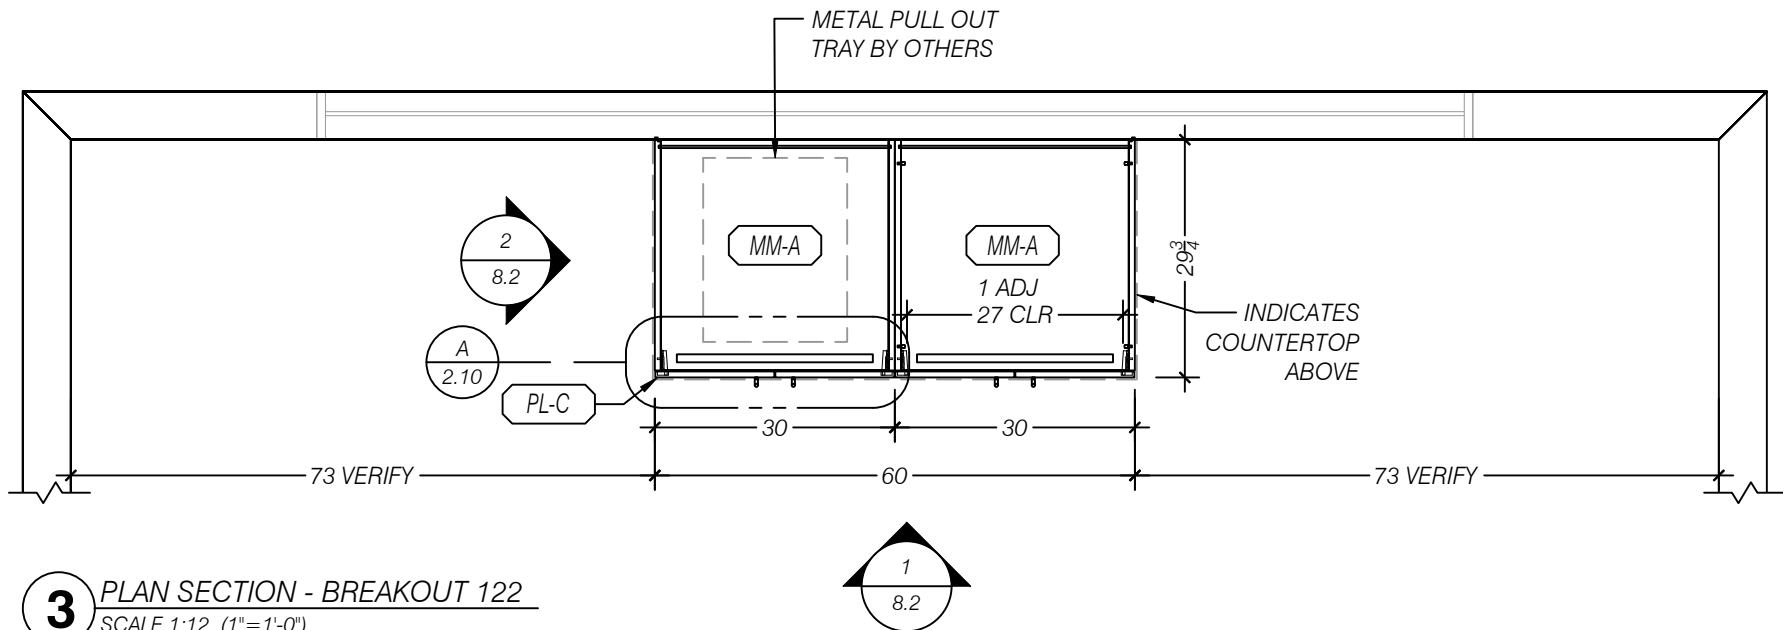

**3** PLAN SECTION - BREAKOUT 122  
SCALE 1:12 (1"=1'-0")  
ARCH REF: NA

DGS SREOC COSTA


MESA

BREAKOUT 121,122,123 & 124

| ISSUE        |                                       |      |       |  |
|--------------|---------------------------------------|------|-------|--|
| DATE         | DESCRIPTION                           | BY   |       |  |
| 05/05/2026   | REV-A FOR SUBMITTAL                   | Q-AS |       |  |
|              |                                       |      |       |  |
|              |                                       |      |       |  |
|              |                                       |      |       |  |
|              |                                       |      |       |  |
| SITE ADDRESS |                                       |      |       |  |
| STREET       | 2301 South Shelley Circle Bldg. A & B |      |       |  |
| CITY         | Costa Mesa                            |      |       |  |
| STATE        | CA                                    | ZIP  | 92626 |  |
| JOB #:       | 26034                                 | REV: | A     |  |
| MOD #:       | 8                                     | REL: | N/A   |  |
| 8.1          |                                       |      |       |  |


CENTERLINE OF IN-WALL STRAPPING  
(STRAPPING BY OTHERS)

31 A.F.F.  
5 A.F.F.

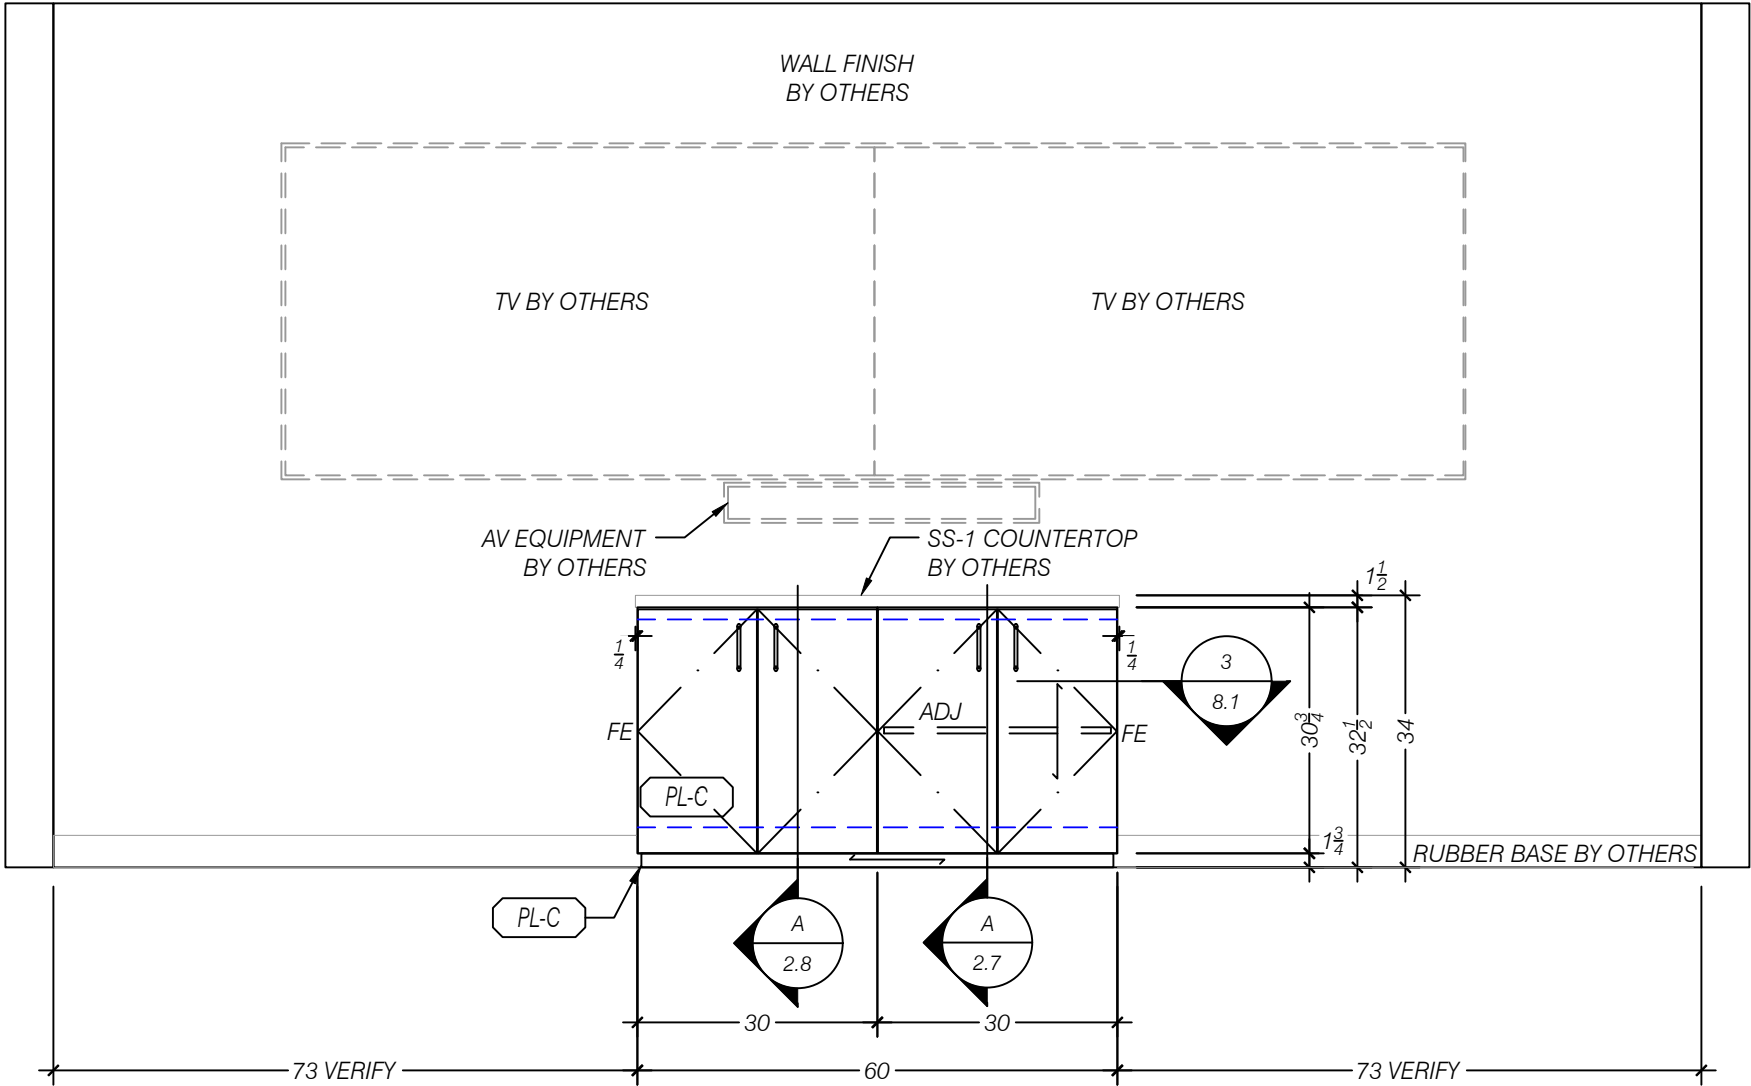

**1** ELEVATION NORTH - BREAKOUT 122  
SCALE 1:12 (1"=1'-0")  
ARCH REF: 7/AE407

|        |      | MATERIALS                                                                           |
|--------|------|-------------------------------------------------------------------------------------|
| (MM-A) |      | WHITE MELAMINE                                                                      |
| (PL-C) |      | (PL-1, WB-2) WILSONART "HARVEST MAPLE", 7953-38, FINE VELVET TEXTURE                |
|        | QTY. | HARDWARE                                                                            |
| H-1.2  | X    | SALICE 0mm CLIP-ON HINGE PLATE EURO SCREW, BARGR09/16                               |
| H-1.3  | X    | SALICE 110° FO SOFT-CLOSE, LOGICA SILENTIA, C7J6AE9                                 |
| H-3.0  | X    | BERENSON WIRE PULL, BN6131-2SC-P, 96mm CTC, SATIN CHROME FINISH                     |
| H-4.0  | X    | HAFELE SHELF SUPPORT, 282.04.711, 5mm SHELF PIN, STEEL NICKEL-PLATED                |
| H-9.5  | X    | MOCKETT, GT-METAL AIR VENT GRILLE, 17W" x 4"H OPENING, MATTE BLACK FINISH W/ MESH/3 |

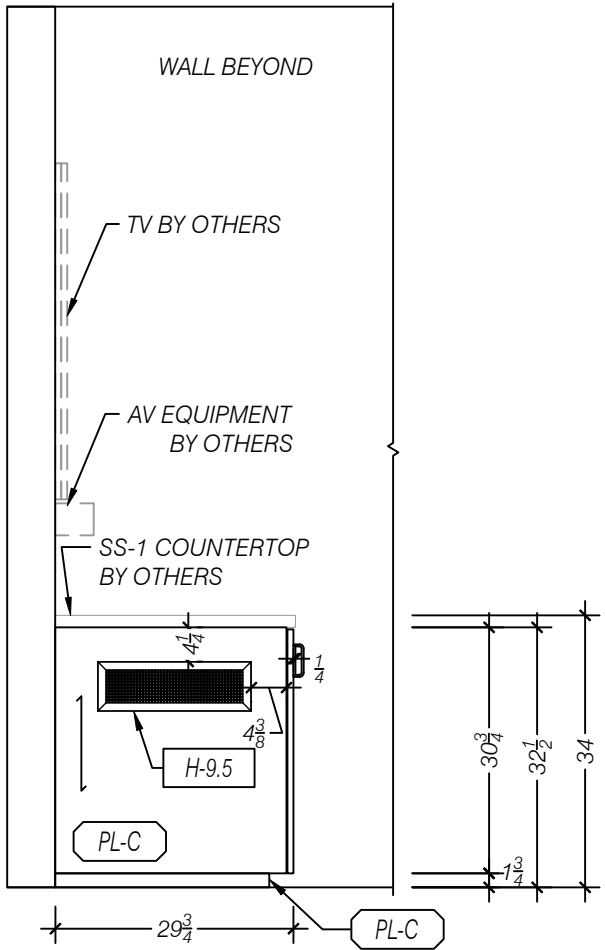


**2** ELEVATION WEST - BREAKOUT 122  
SCALE 1:12 (1"=1'-0")  
ARCH REF: NA

**DGS SREOC COSTA  
MESA  
BREAKOUT 121,122,123 & 124**

| DATE       | DESCRIPTION         | BY | Q-AS |
|------------|---------------------|----|------|
|            |                     |    |      |
| 05/05/2026 | REV-A FOR SUBMITTAL | -  | -    |
| -          | -                   | -  | -    |
| -          | -                   | -  | -    |
| -          | -                   | -  | -    |
| -          | -                   | -  | -    |


| SITE ADDRESS |                                       |      |       |
|--------------|---------------------------------------|------|-------|
| STREET       | 2301 South Shelley Circle Bldg. A & B |      |       |
| CITY         | Costa Mesa                            |      |       |
| STATE        | CA                                    | ZIP  | 92626 |
| JOB #:       | 26034                                 | REV: | A     |
| MOD #:       | 8                                     | REL: | N/A   |

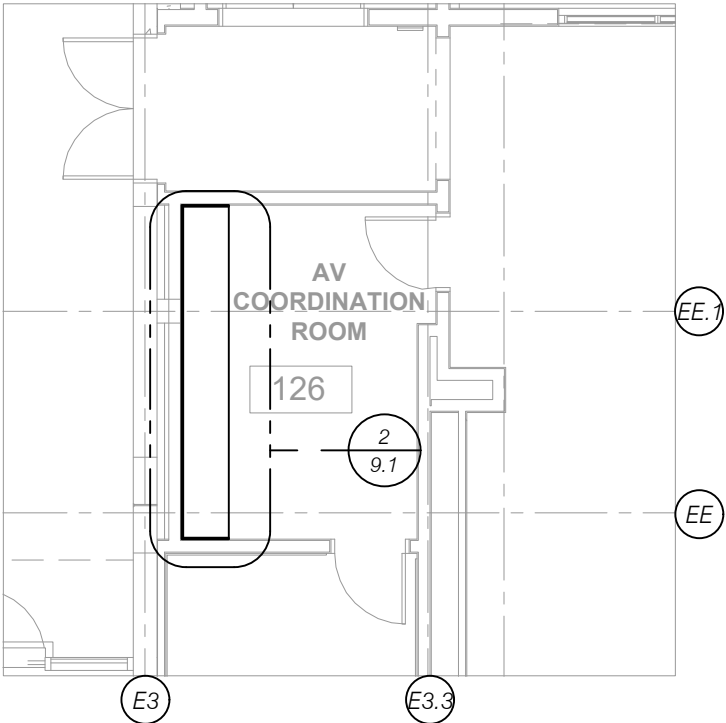


**1** KEY PLAN  
SCALE : NTS  
ARCH REF: 1/AE101.1

| NOTES |   |
|-------|---|
| 1     | ALL DIMENSIONS TO BE FIELD VERIFIED                                                                                          |
| 2     | GENERAL CONTRACTOR TO COORDINATE ALL FRAMING REQUIREMENTS WITH CMI                                                           |
| 3     | GENERAL CONTRACTOR TO COORDINATE ALL WALL TYPES, THICKNESSES AND ROUGH OPENINGS                                              |
| 4     | GENERAL CONTRACTOR & ELECTRICAL CONTRACTOR TO COORDINATE ALL ELECTRICAL BOX LOCATIONS & REQUIREMENTS WITH MILLWORK DRAWINGS  |
| 5     | GENERAL CONTRACTOR & ELECTRICAL CONTRACTOR TO COORDINATE ALL LIGHT FIXTURE FEED & SWITCHING LOCATIONS WITH MILLWORK DRAWINGS |
| 6     | GENERAL CONTRACTOR & PLUMBING CONTRACTOR TO COORDINATE ALL PLUMBING FIXTURES & INSTALLATION REQUIREMENTS                     |

|         | MATERIALS                                                    |
|---------|--------------------------------------------------------------|
| (PL-F)  | (PL-4) WILSONART "CARBON MESH", 4880-38, FINE VELVET TEXTURE |
| QTY.    | HARDWARE                                                     |
| H-4.1.1 | X BRACKET, A&M CFLAT 21 (2.0)                                |
| H-7.0   | X 1/8" x 1-1/4" x 1-1/4" ALUMINUM L-ANGLE, MILL FINISH       |

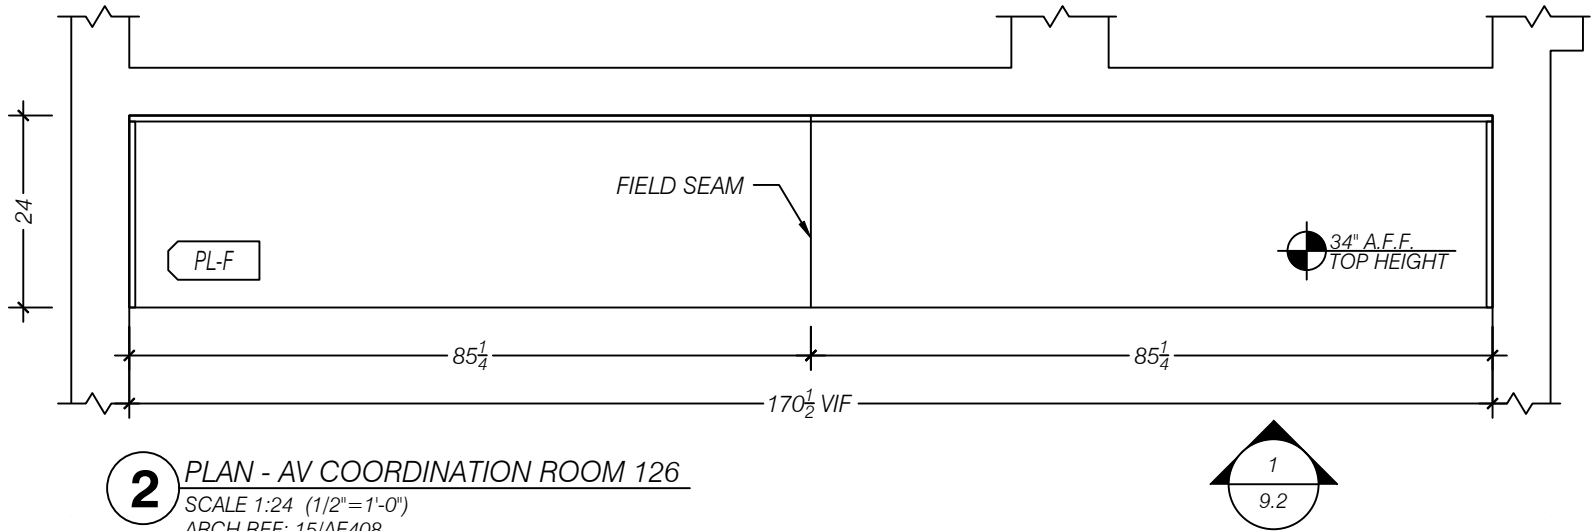

**2** PLAN - AV COORDINATION ROOM 126  
SCALE 1:24 (1/2"=1'-0")  
ARCH REF: 15/AE408

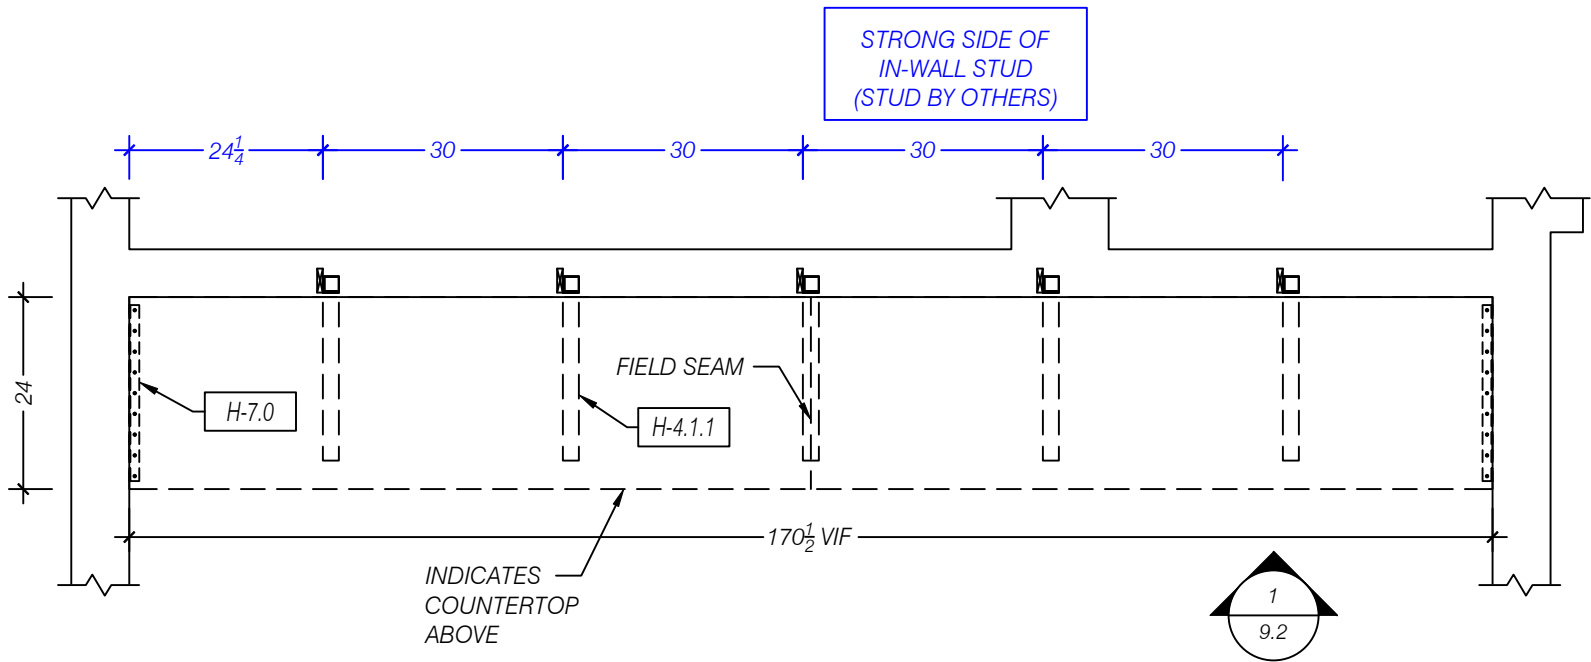


**3** PLAN SECTION BASE - AV COORDINATION ROOM 126  
SCALE 1:24 (1/2"=1'-0")  
ARCH REF: NA

DGS SREOC CCOSTA

MESA

AV COORDINATION ROOM 126

| ISSUE        |       | BY                                    | DATE       | DESCRIPTION           | Q-AS |
|--------------|-------|---------------------------------------|------------|-----------------------|------|
|              |       |                                       | 05/05/2026 | REV-A - FOR SUBMITTAL | -    |
|              |       |                                       | -          | -                     | -    |
|              |       |                                       | -          | -                     | -    |
|              |       |                                       | -          | -                     | -    |
|              |       |                                       | -          | -                     | -    |
| SITE ADDRESS |       |                                       |            |                       |      |
| STREET       |       | 2301 South Shelley Circle Bldg. A & B |            |                       |      |
| CITY         |       | Costa Mesa                            |            |                       |      |
| STATE        | CA    | ZIP                                   | 92626      |                       |      |
| JOB #:       | 26034 | REV:                                  | A          |                       |      |
| MOD #:       | 9     | REL:                                  | N/A        |                       |      |

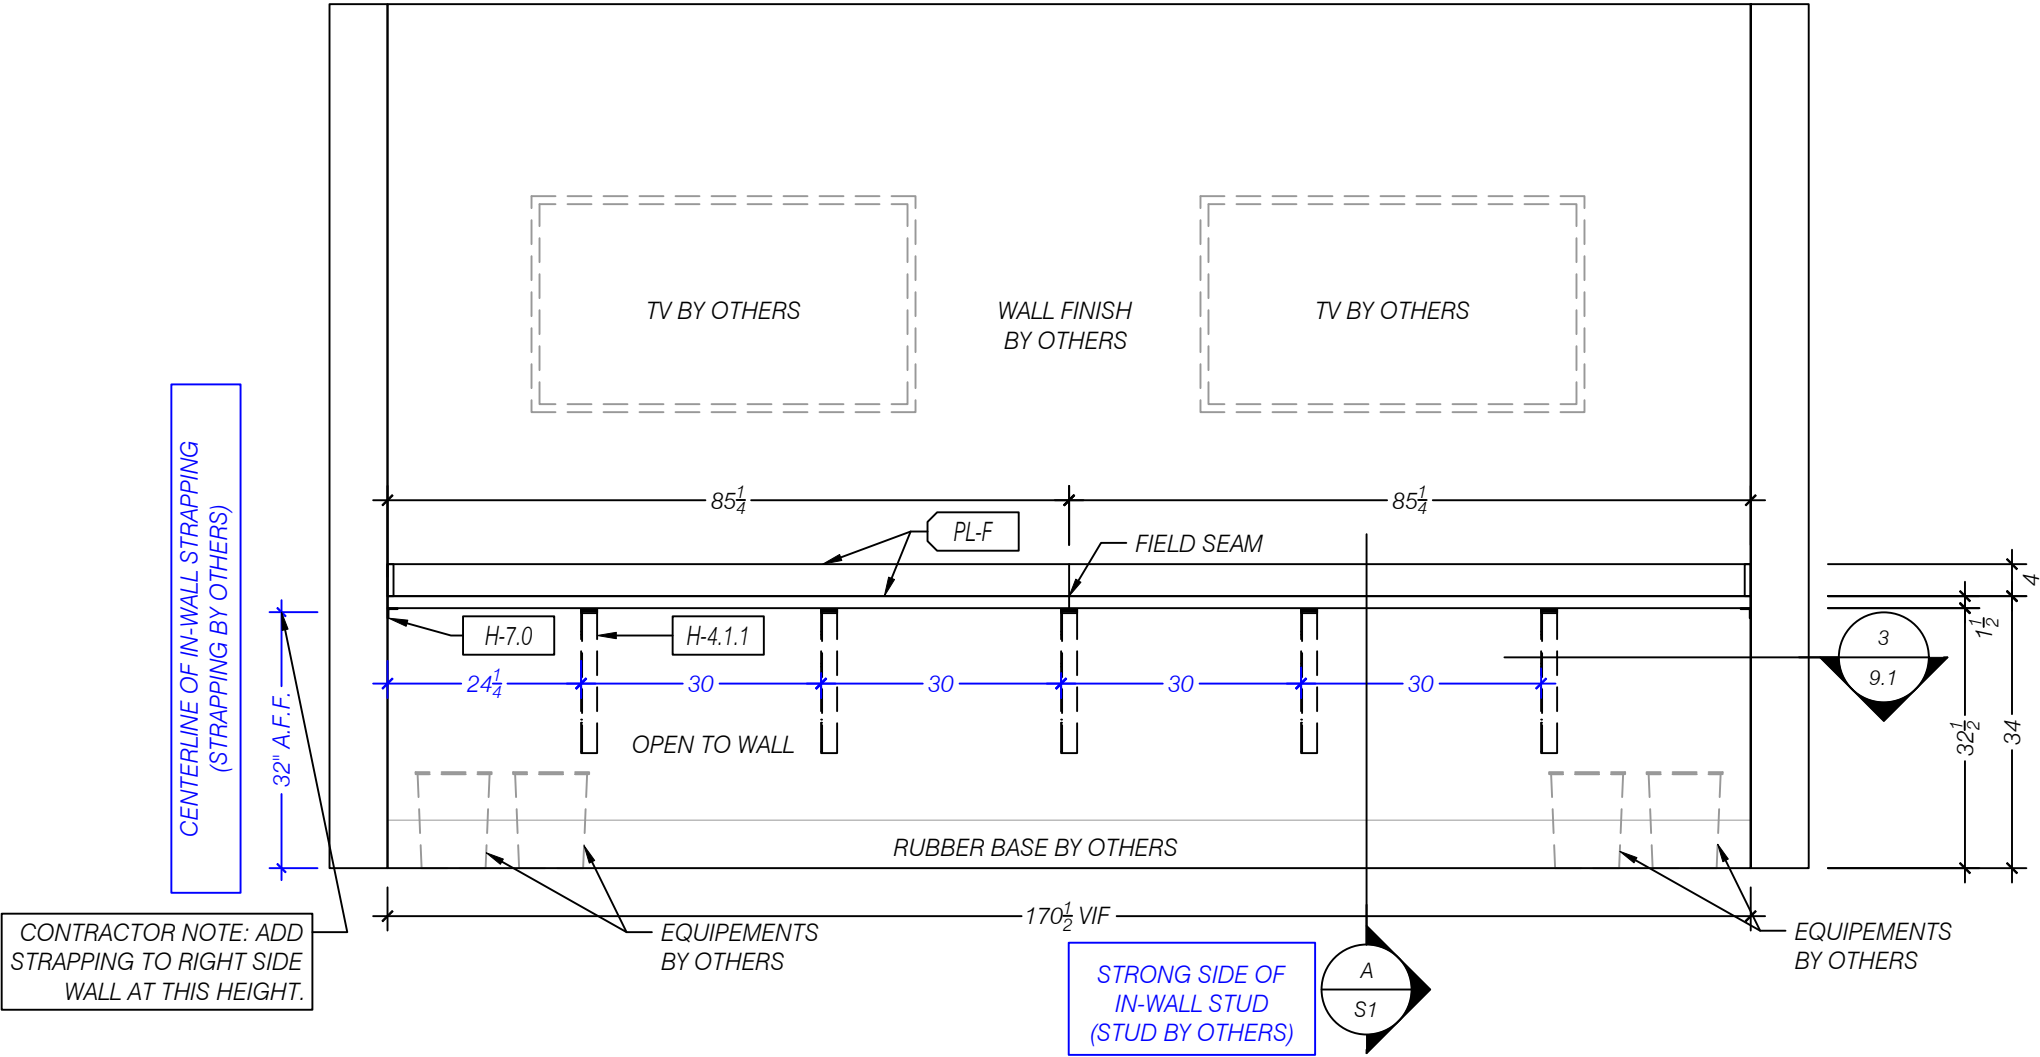

|         | MATERIALS                                                    |
|---------|--------------------------------------------------------------|
| (PL-F)  | (PL-4) WILSONART "CARBON MESH", 4880-38, FINE VELVET TEXTURE |
|         | QTY. HARDWARE                                                |
| H-4.1.1 | X BRACKET, A&M CFLAT 21 (2.0)                                |
| H-7.0   | X 1/8" x 1-1/4" x 1-1/4" ALUMINUM L-ANGLE, MILL FINISH       |

CONTRACTOR NOTE: ADD STRAPPING TO RIGHT SIDE WALL AT THIS HEIGHT.

**1** ELEVATION WEST - AV COORDINATION ROOM 126  
SCALE 1:24 (1/2"=1'-0")  
ARCH REF: 16/AE408



**CRESTMILLWORK**

5640 WEST END ROAD  
ARCATA, CA 95521  
PH (707) 822-4034 FAX (707) 822-5478  
WWW.CRESTMILLWORK.COM


DGS SREOC CCOSTA

MESA

AV COORDINATION ROOM 126

| ISSUE      |                       | BY   |
|------------|-----------------------|------|
| DATE       | DESCRIPTION           | Q-AS |
| 05/05/2026 | REV-A - FOR SUBMITTAL | -    |
| -          | -                     | -    |
| -          | -                     | -    |
| -          | -                     | -    |
| -          | -                     | -    |

| SITE ADDRESS |       |                                       |       |
|--------------|-------|---------------------------------------|-------|
| STREET       |       | 2301 South Shelley Circle Bldg. A & B |       |
| CITY         |       | Costa Mesa                            |       |
| STATE        | CA    | ZIP                                   | 92626 |
| JOB #:       | 26034 | REV:                                  | A     |
| MOD #:       | 9     | REL:                                  | N/A   |

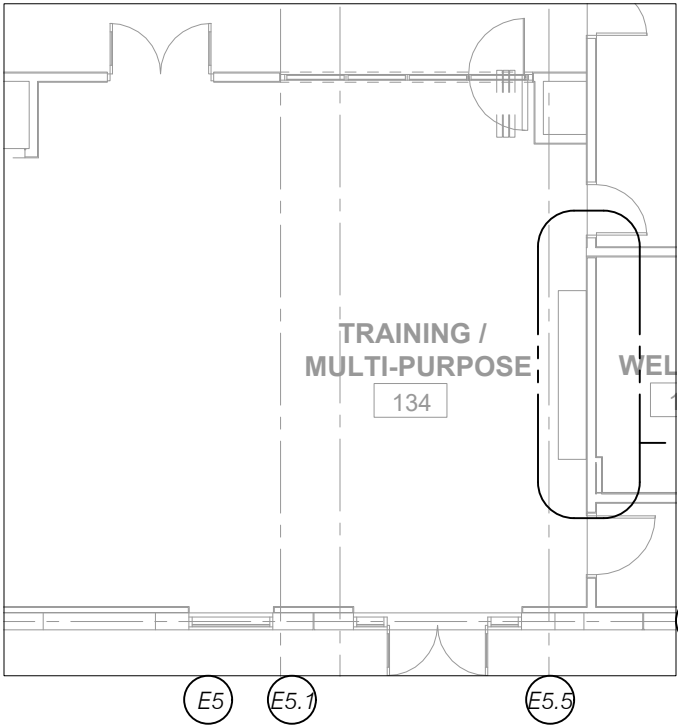


**1** KEY PLAN  
SCALE: NTS  
ARCH REF: 1/AE101.1


| NOTES |   |
|-------|---|
| 1     | ALL DIMENSIONS TO BE FIELD VERIFIED                                                                                          |
| 2     | GENERAL CONTRACTOR TO COORDINATE ALL FRAMING REQUIREMENTS WITH CMI                                                           |
| 3     | GENERAL CONTRACTOR TO COORDINATE ALL WALL TYPES, THICKNESSES AND ROUGH OPENINGS                                              |
| 4     | GENERAL CONTRACTOR & ELECTRICAL CONTRACTOR TO COORDINATE ALL ELECTRICAL BOX LOCATIONS & REQUIREMENTS WITH MILLWORK DRAWINGS  |
| 5     | GENERAL CONTRACTOR & ELECTRICAL CONTRACTOR TO COORDINATE ALL LIGHT FIXTURE FEED & SWITCHING LOCATIONS WITH MILLWORK DRAWINGS |
| 6     | GENERAL CONTRACTOR & PLUMBING CONTRACTOR TO COORDINATE ALL PLUMBING FIXTURES & INSTALLATION REQUIREMENTS                     |

| MATERIALS     |   |                                                                      |
|---------------|---|----------------------------------------------------------------------|
| (MM-A)        |   | WHITE MELAMINE                                                       |
| (PL-C)        |   | (PL-1, WB-2) WILSONART "HARVEST MAPLE", 7953-38, FINE VELVET TEXTURE |
| QTY. HARDWARE |   |                                                                      |
| H-1.2         | X | SALICE 0mm CLIP-ON HINGE PLATE EURO SCREW, BARGR09/16                |
| H-1.3         | X | SALICE 110° FO SOFT-CLOSE, LOGICA SILENTIA, C7J6AE9                  |
| H-3.0         | X | BERENSON WIRE PULL, BN6131-2SC-P, 96mm CTC, SATIN CHROME FINISH      |
| H-4.0         | X | HAFELE SHELF SUPPORT, 282.04.711, 5mm SHELF PIN, STEEL NICKEL-PLATED |

| TRAINING TYPICAL SCHEDULE |     |       |                               |                |                     |           |           |
|---------------------------|-----|-------|-------------------------------|----------------|---------------------|-----------|-----------|
| LEVEL                     | QTY | ROOM# | ROOM NAME                     | ARCH PLAN REF. | ARCH ELEVATION REF. | PLAN REF. | DIRECTION |
| 1                         | 1   | 132   | TRAINING / MULTI-PURPOSE ROOM | 1/AE101.1      | 5/AE415             | 1/FP.1    | WEST      |
| 1                         | 1   | 134   | TRAINING / MULTI-PURPOSE ROOM | 1/AE101.1      | 5/AE415             | 1/FP.1    | EAST      |

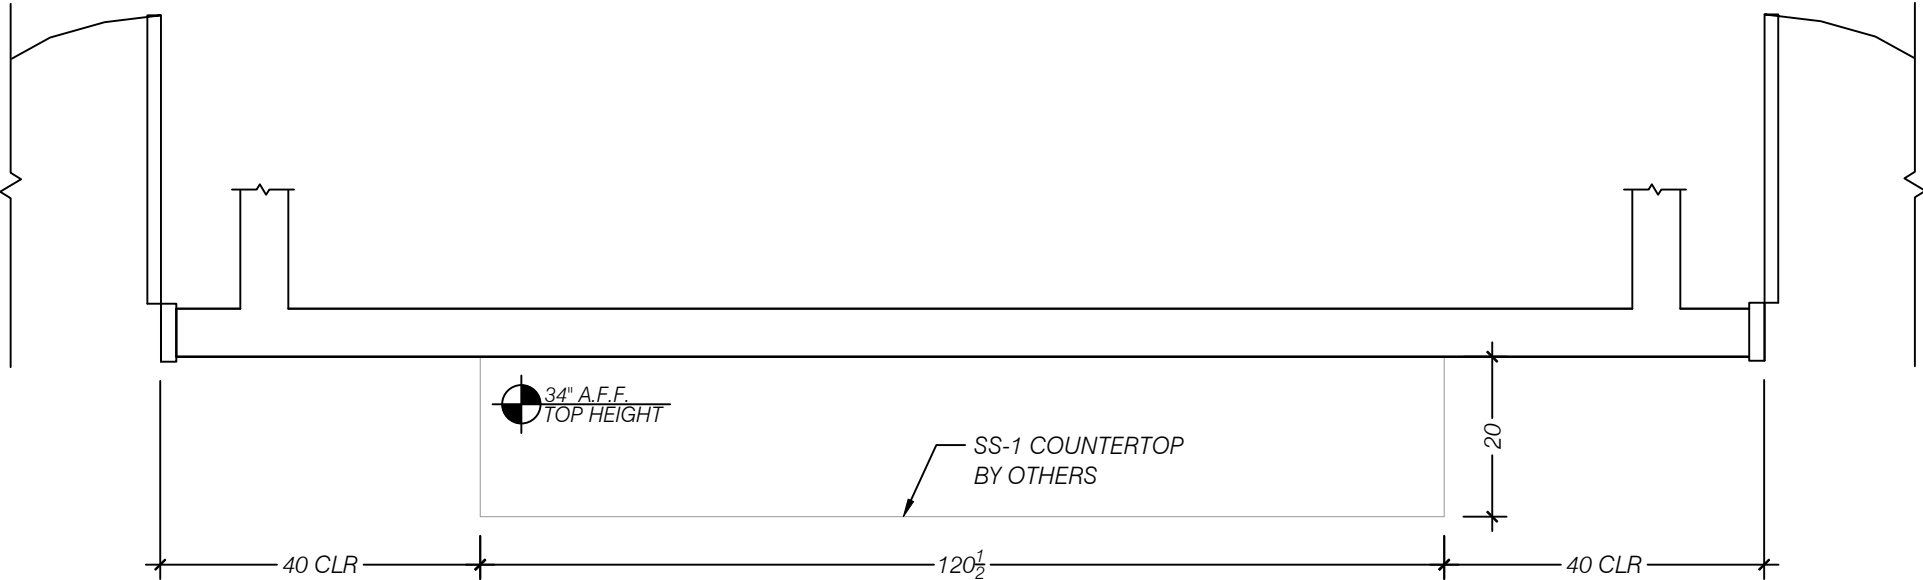

**2** PLAN - TRAINING/MULTI-PURPOSE ROOM 134  
SCALE 1:24 (1/2"=1'-0")  
ARCH REF: 1/AE415

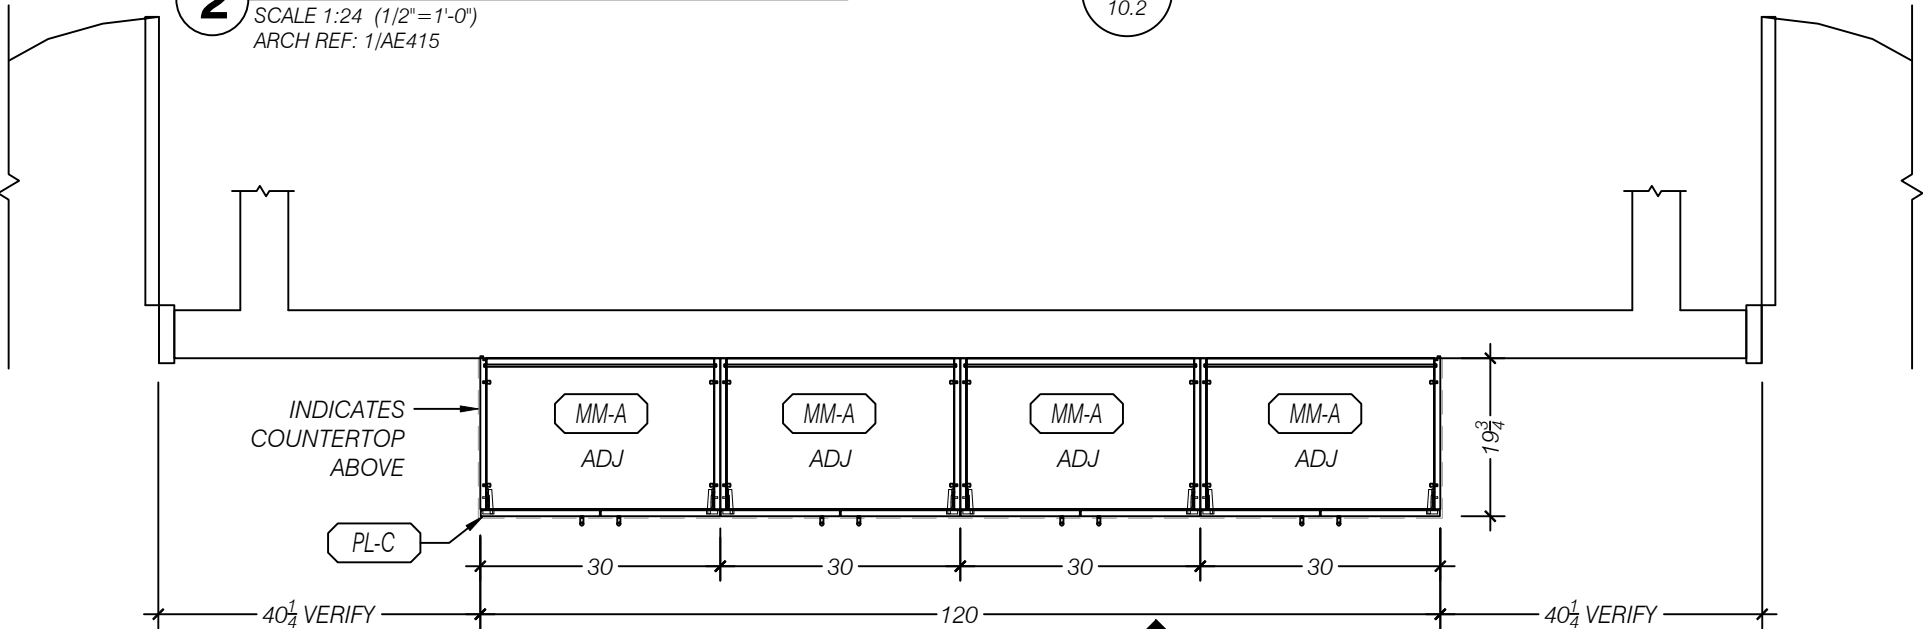

**3** PLAN SECTION BASE - TRAINING/MULTI-PURPOSE ROOM 134  
SCALE 1:24 (1/2"=1'-0")  
ARCH REF: NA

CRESTMARK

MILLWORK

5640 WEST END ROAD  
ARCATA, CA 95521  
PH (707) 822-4034 FAX (707) 822-5478  
WWW.CRESTMARKMILLWORK.COM


DGS SREOC COSTA

MESA


TRAINING / MULTI-PURPOSE ROOMS 132 & 134

| ISSUE        |                                       | BY        |
|--------------|---------------------------------------|-----------|
| DATE         | DESCRIPTION                           | Q-AS      |
| 05/05/2026   | REV-A FOR SUBMITTAL                   | -         |
| -            | -                                     | -         |
| -            | -                                     | -         |
| -            | -                                     | -         |
| -            | -                                     | -         |
| SITE ADDRESS |                                       |           |
| STREET       | 2301 South Shelley Circle Bldg. A & B |           |
| CITY         | Costa Mesa                            |           |
| STATE        | CA                                    | ZIP 92626 |
| JOB #:       | 26034                                 | REV: A    |
| MOD #:       | 10                                    | REL: N/A  |
| 10.1         |                                       |           |

5640 WEST END ROAD  
ARCATA, CA 95521  
(707) 822-4034 FAX (707) 822-5478  
WWW.CRESTMARKMILLWORK.COM

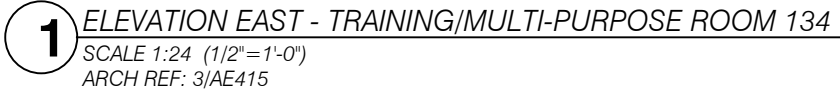

| SITE ADDRESS |                                |     |          |
|--------------|--------------------------------|-----|----------|
| STREET       | 2301 South Shelley Bldg. A & B |     |          |
| CITY         | Costa Mesa                     |     |          |
| STATE        | CA                             | ZIP | 92626    |
| JOB #:       | 26034                          |     | REV: A   |
| MOD #:       | 10                             |     | REL: N/A |

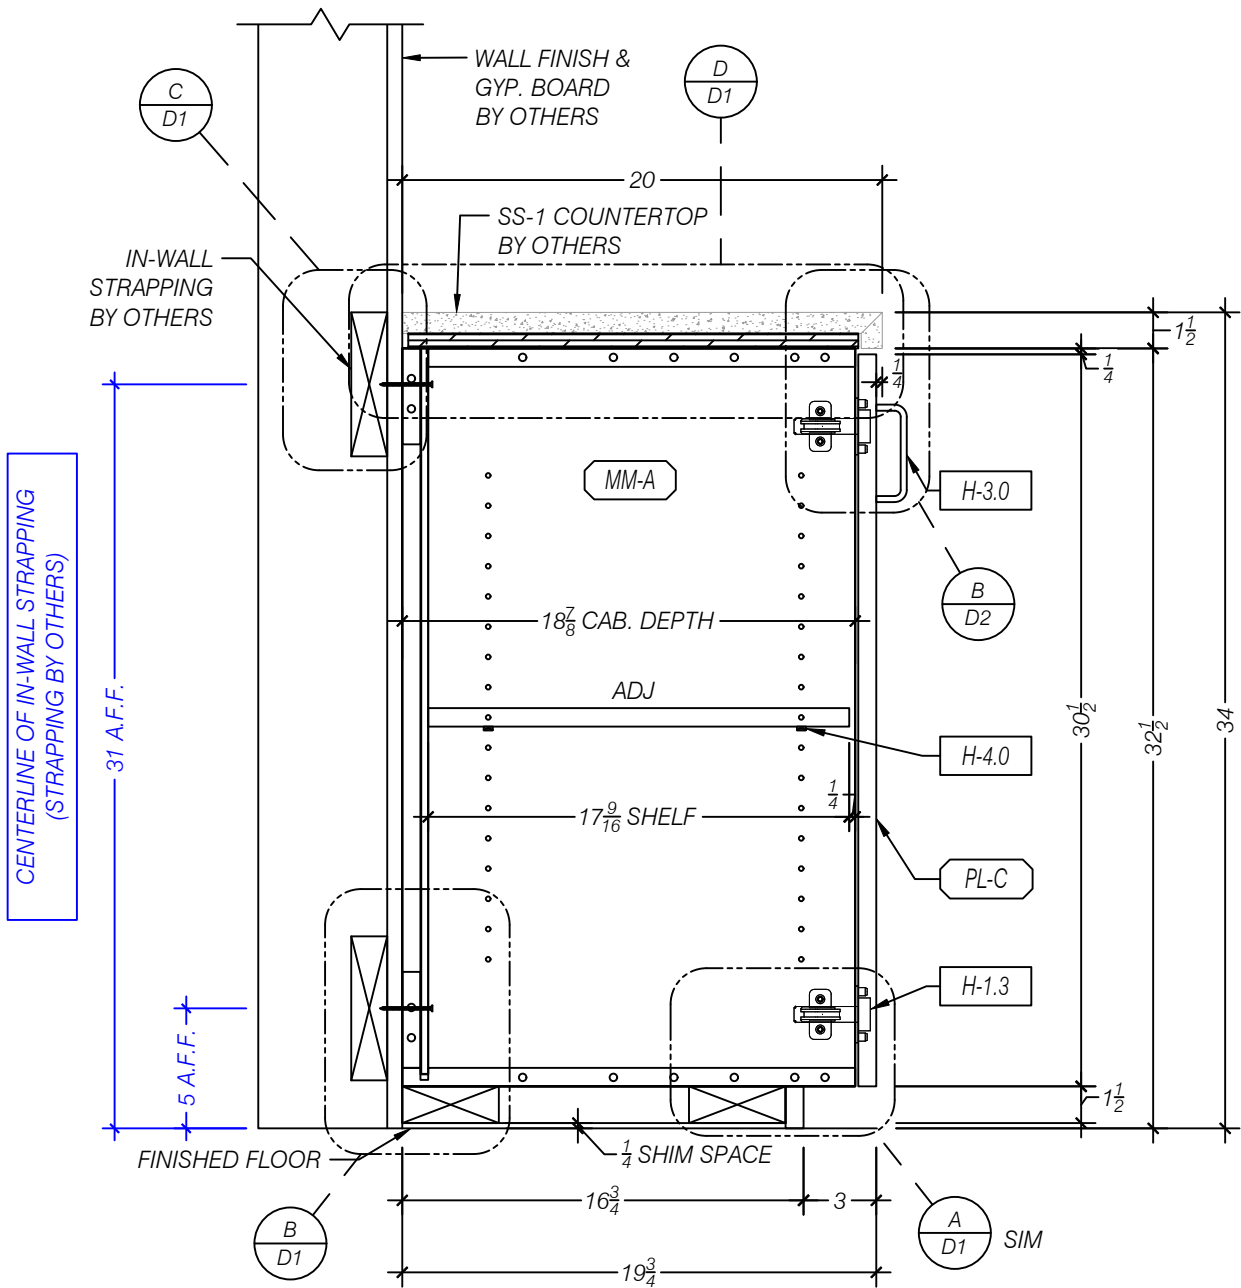

**A** SECTION - BASE CABINET  
SCALE 1:8 (1 1/2"=1'-0")  
ARCH REF: 15/AE581 (SIM)

|       |      | MATERIALS                                                            |
|-------|------|----------------------------------------------------------------------|
|       |      | WHITE MELAMINE                                                       |
|       |      | (PL-1, WB-2) WILSONART "HARVEST MAPLE", 7953-38, FINE VELVET TEXTURE |
|       | QTY. | HARDWARE                                                             |
| H-1.2 | X    | SALICE 0mm CLIP-ON HINGE PLATE EURO SCREW, BARGR09/16                |
| H-1.3 | X    | SALICE 110° FO SOFT-CLOSE, LOGICA SILENTIA, C7J6AE9                  |
| H-3.0 | X    | BERENSON WIRE PULL, BN6131-2SC-P, 96mm CTC, SATIN CHROME FINISH      |
| H-4.0 | X    | HAFELE SHELF SUPPORT, 282.04.711, 5mm SHELF PIN, STEEL NICKEL-PLATED |




5640 WEST END ROAD  
ARCATA, CA 95521  
PH (707) 822-4034 FAX (707) 822-5478  
WWW.CRESTMARKMILLWORK.COM


**DGS SREOC COSTA**  
**MESA**  
**TRAINING / MULTI-PURPOSE ROOMS 132 & 134**

| ISSUE        |  |                                |      |          |
|--------------|--|--------------------------------|------|----------|
| DATE         |  | DESCRIPTION                    | BY   |          |
| 05/05/2026   |  | REV-A FOR SUBMITTAL            | Q-AS |          |
|              |  |                                |      |          |
|              |  |                                |      |          |
| SITE ADDRESS |  |                                |      |          |
| STREET       |  | 2301 South Shelley Bldg. A & B |      |          |
| CITY         |  | Costa Mesa                     |      |          |
| STATE        |  | CA                             | ZIP  | 92626    |
| JOB #:       |  | 26034                          |      | REV: A   |
| MOD #:       |  | 10                             |      | REL: N/A |
| 10.3         |  |                                |      |          |

NOTE:  
REFER TO SPECIFICATION PAGE  
FOR MATERIAL, HARDWARE AND JOINERY

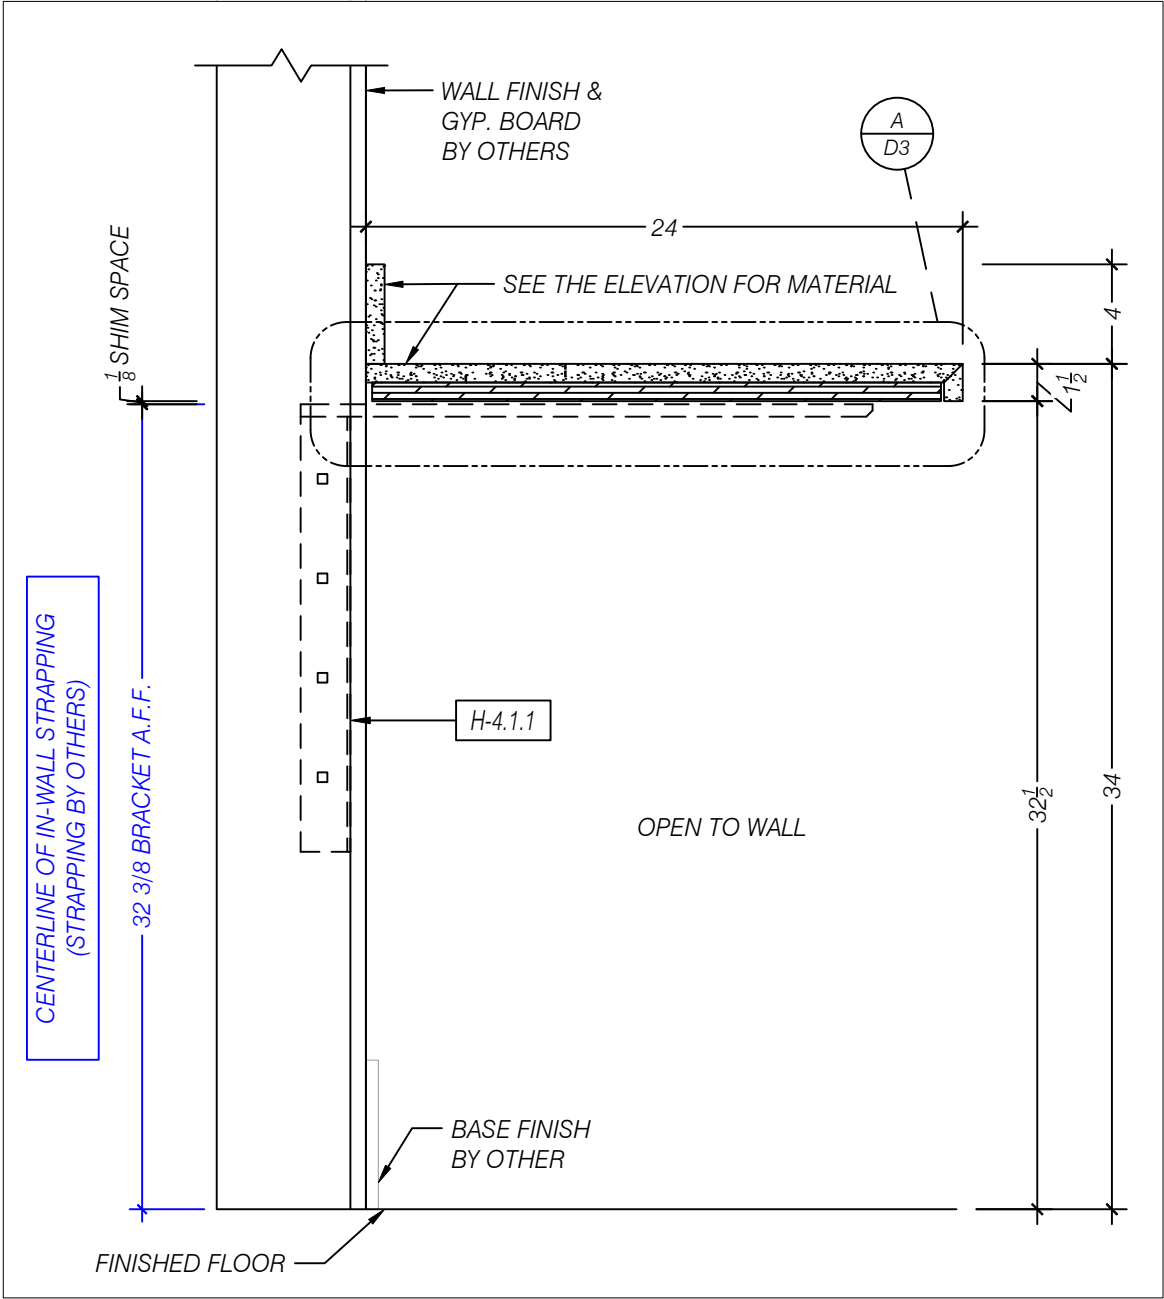

**A** SECTION - COUNTERTOP W/ BRACKET  
SCALE 1:8 (1 1/2"=1'-0")  
ARCH REF: 6/AE583

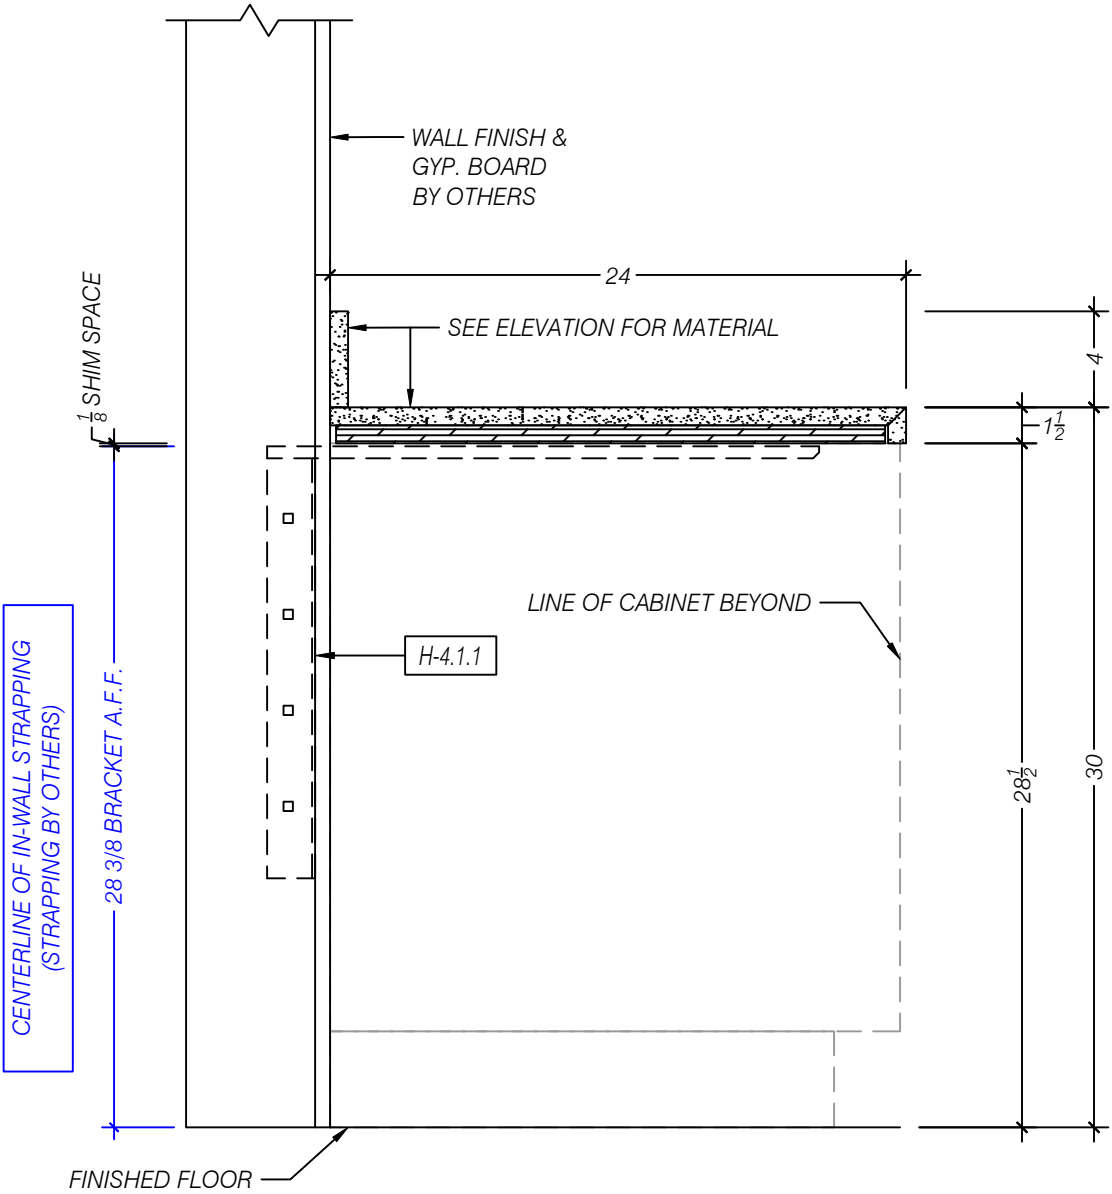


**B** SECTION - COUNTERTOP w/ BRACKET  
SCALE 1:8 (1 1/2"=1'-0")  
ARCH REF: 8/AE581



5640 WEST END ROAD  
ARCATA, CA 95521  
PH (707) 822-4034 FAX (707) 822-5478  
WWW.CRESTMARKMILLWORK.COM


**DGS SREOC COSTA  
MESA**  
**SECTION DETAILS**

| ISSUE        |                                       | BY        |
|--------------|---------------------------------------|-----------|
| DATE         | DESCRIPTION                           |           |
| 05/05/2026   | REV-A FOR SUBMITTAL                   | Q-AS      |
| -            | -                                     | -         |
| -            | -                                     | -         |
| SITE ADDRESS |                                       |           |
| STREET       | 2301 South Shelley Circle Bldg. A & B |           |
| CITY         | Costa Mesa                            |           |
| STATE        | CA                                    | ZIP 92626 |
| JOB #:       | 26034                                 | REV: -    |
| MOD #:       | -                                     | REL: -    |
| <b>S1</b>    |                                       |           |

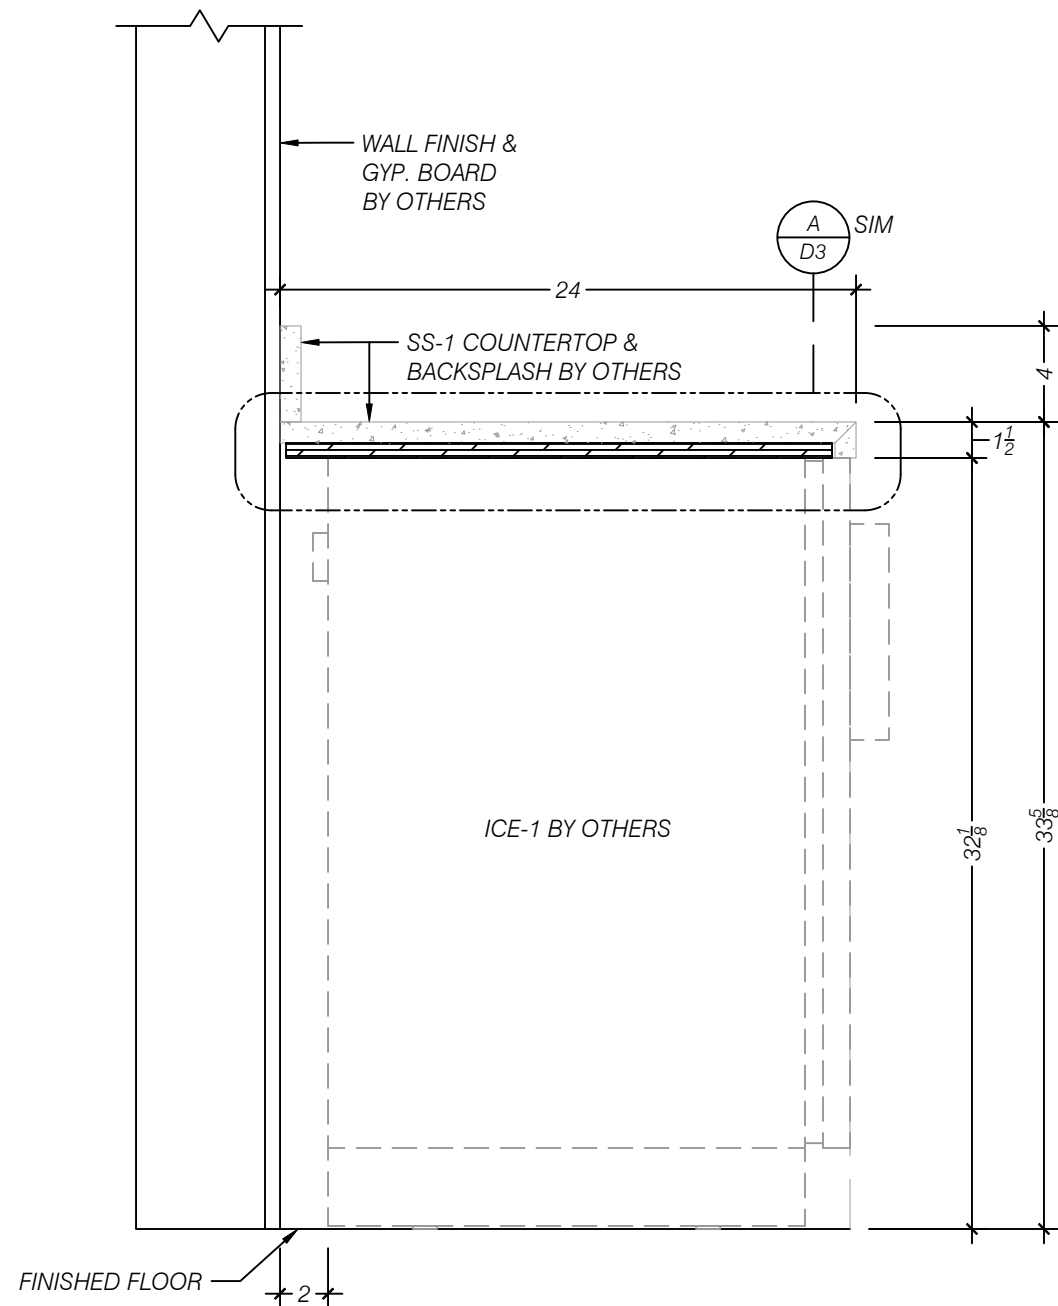

**A** SECTION - COUNTERTOP w/ EQUIPMENT  
SCALE 1:8 (1 1/2"=1'-0")  
ARCH REF: 8/AE581

NOTE:  
REFER TO SPECIFICATION PAGE  
FOR MATERIAL, HARDWARE AND JOINERY

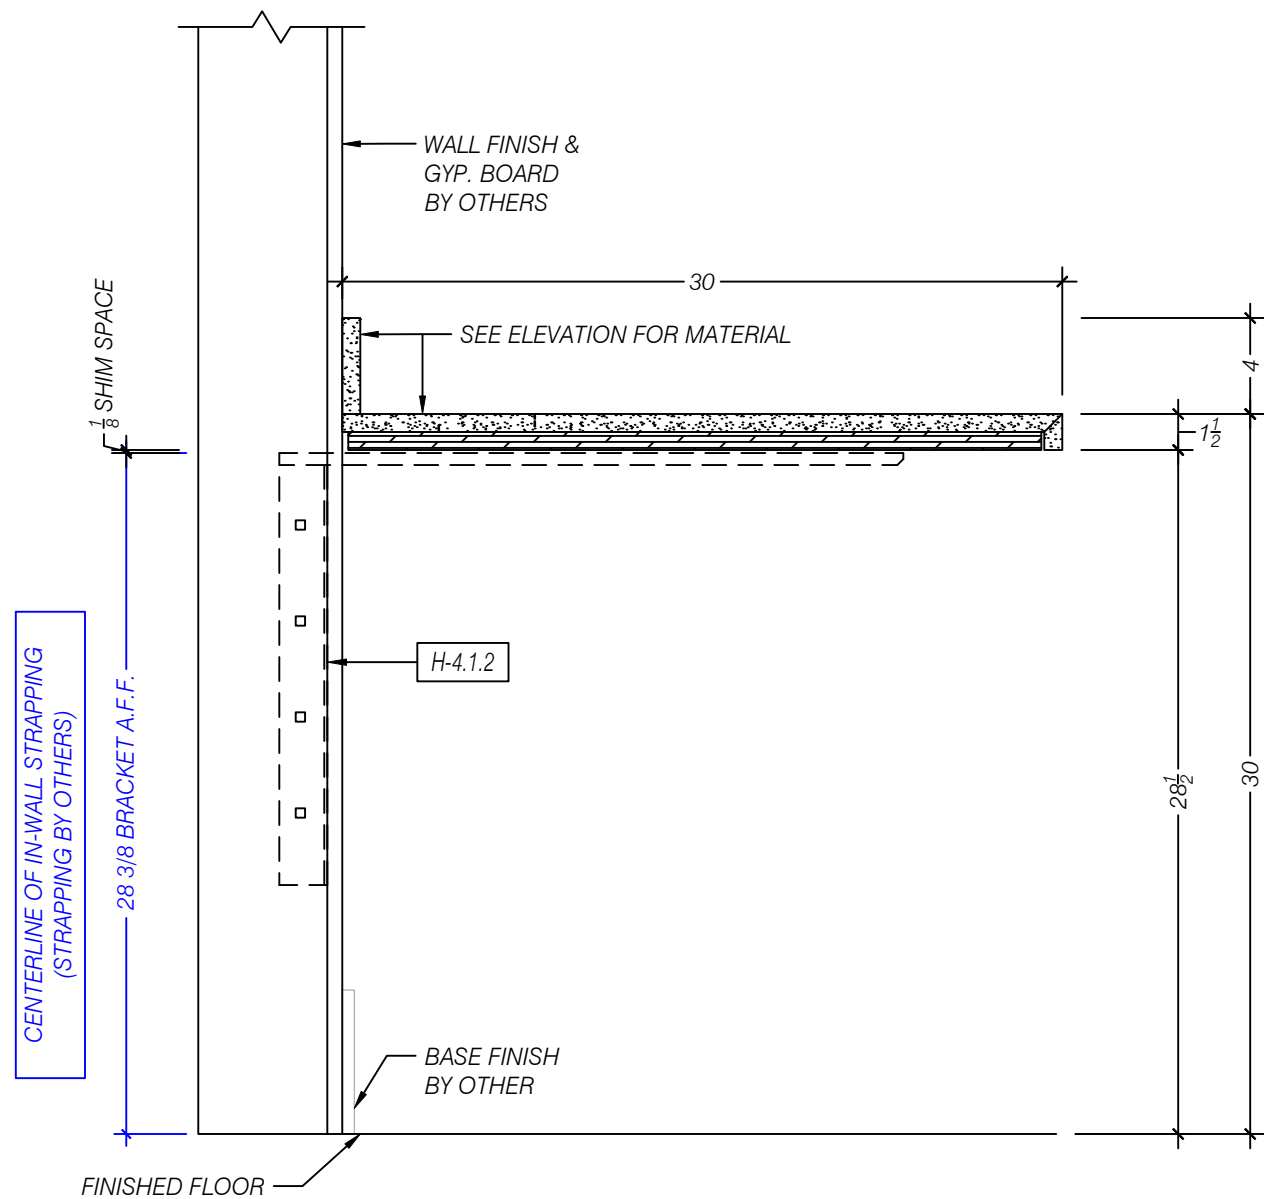


**B** SECTION - COUNTERTOP w/ BRACKET  
SCALE 1:8 (1 1/2"=1'-0")  
ARCH REF: 10/AE583



5640 WEST END ROAD  
ARCATA, CA 95521  
PH (707) 822-4034 FAX (707) 822-5478  
WWW.CRESTMARKMILLWORK.COM

# **DGS SREOC COSTA** **MESA** **SECTION DETAILS**

| ISSUE        |                                       | BY        |
|--------------|---------------------------------------|-----------|
| DATE         | DESCRIPTION                           |           |
| 05/05/2026   | REV-A FOR SUBMITTAL                   | Q-AS      |
| -            | -                                     | -         |
| -            | -                                     | -         |
| SITE ADDRESS |                                       |           |
| STREET       | 2301 South Shelley Circle Bldg. A & B |           |
| CITY         | Costa Mesa                            |           |
| STATE        | CA                                    | ZIP 92626 |
| JOB #:       | 26034                                 | REV: -    |
| MOD #:       | -                                     | REL: -    |
| <b>S2</b>    |                                       |           |

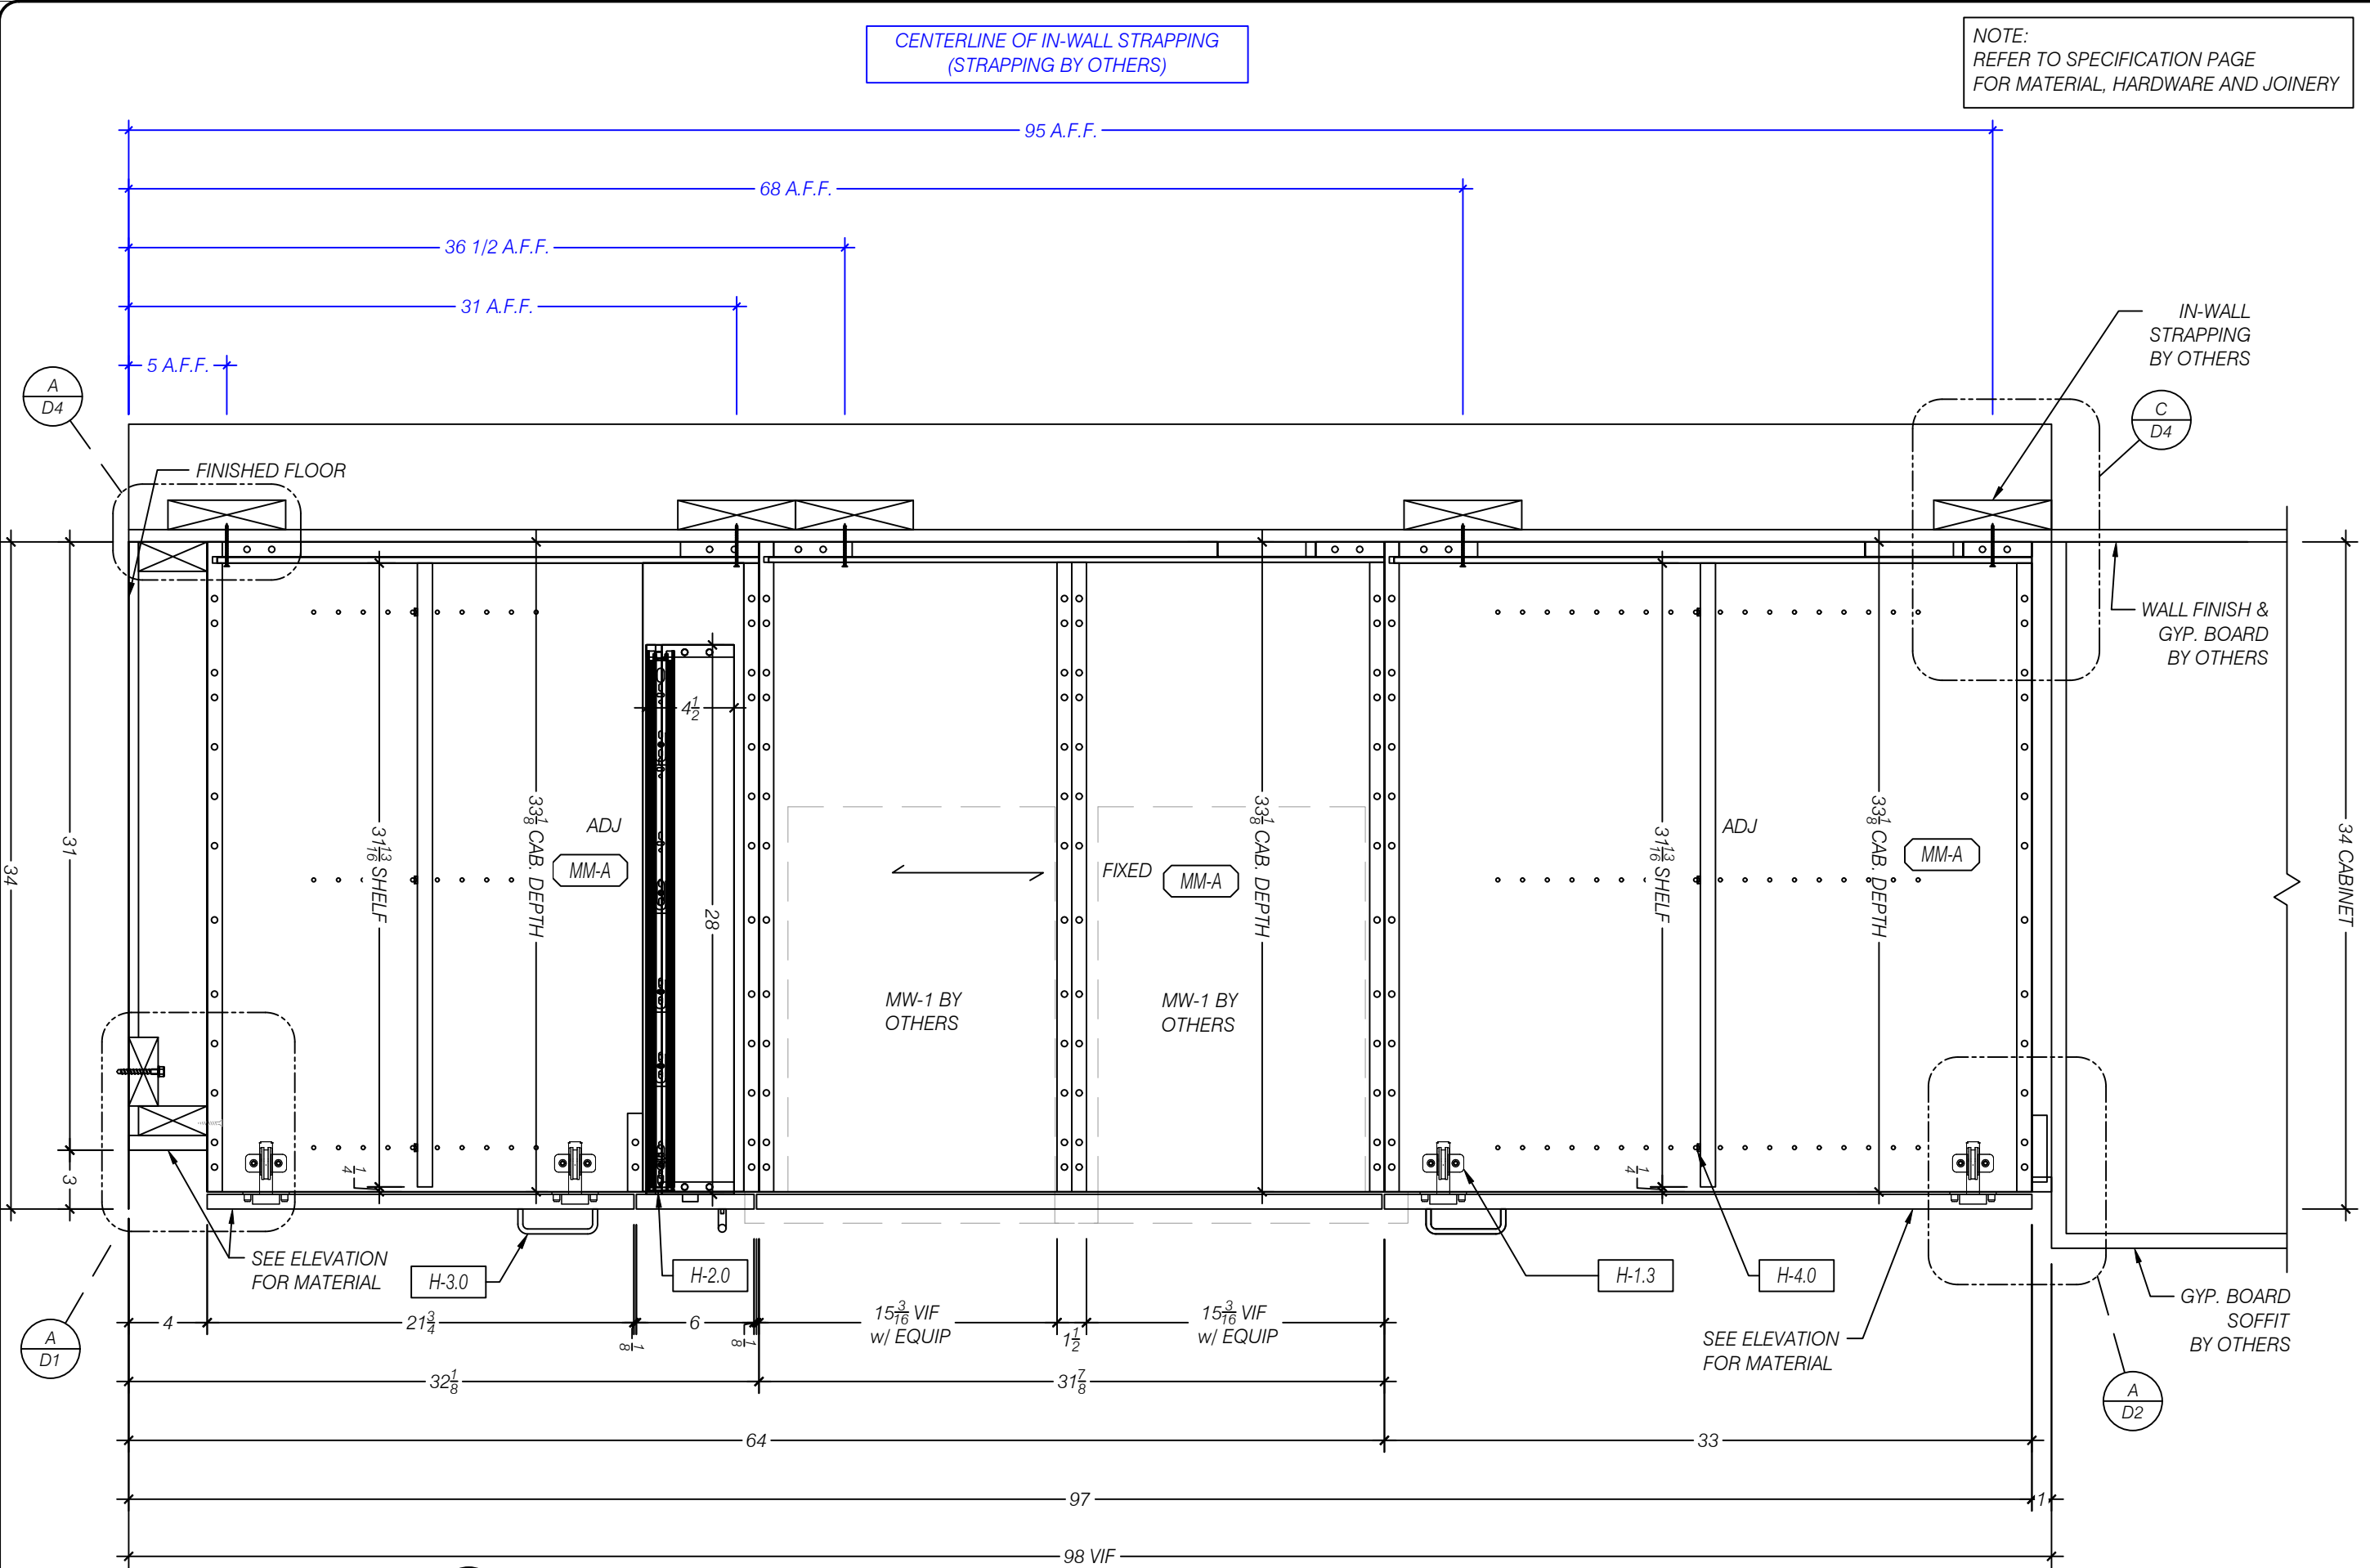

**A** SECTION - TALL CABINET  
SCALE 1:8 (1 1/2"=1'-0")  
ARCH REF: 22/AE582



**CRESTMARK**  
MILLWORK

5640 WEST END ROAD  
ARCATA, CA 95521  
PH (707) 822-4034 FAX (707) 822-5478  
WWW.CRESTMARKMILLWORK.COM

**DGS SREOC COSTA**  
**MESA**

**SECTION DETAILS**

| ISSUE      |                     | BY   |
|------------|---------------------|------|
| DATE       | DESCRIPTION         | Q-AS |
| 05/05/2026 | REV-A FOR SUBMITTAL | -    |
| -          | -                   | -    |
| -          | -                   | -    |
| -          | -                   | -    |
| -          | -                   | -    |

**SITE ADDRESS**


|        |                                       |     |       |
|--------|---------------------------------------|-----|-------|
| STREET | 2301 South Shelley Circle Bldg. A & B |     |       |
| CITY   | Costa Mesa                            |     |       |
| STATE  | CA                                    | ZIP | 92626 |

|        |       |      |   |
|--------|-------|------|---|
| JOB #: | 26034 | REV: | - |
| MOD #: | -     | REL: | - |


**S3**

© CRESTMARK MILLWORK, INC.

NOTE:  
REFER TO SPECIFICATION PAGE  
FOR MATERIAL, HARDWARE AND JOINERY

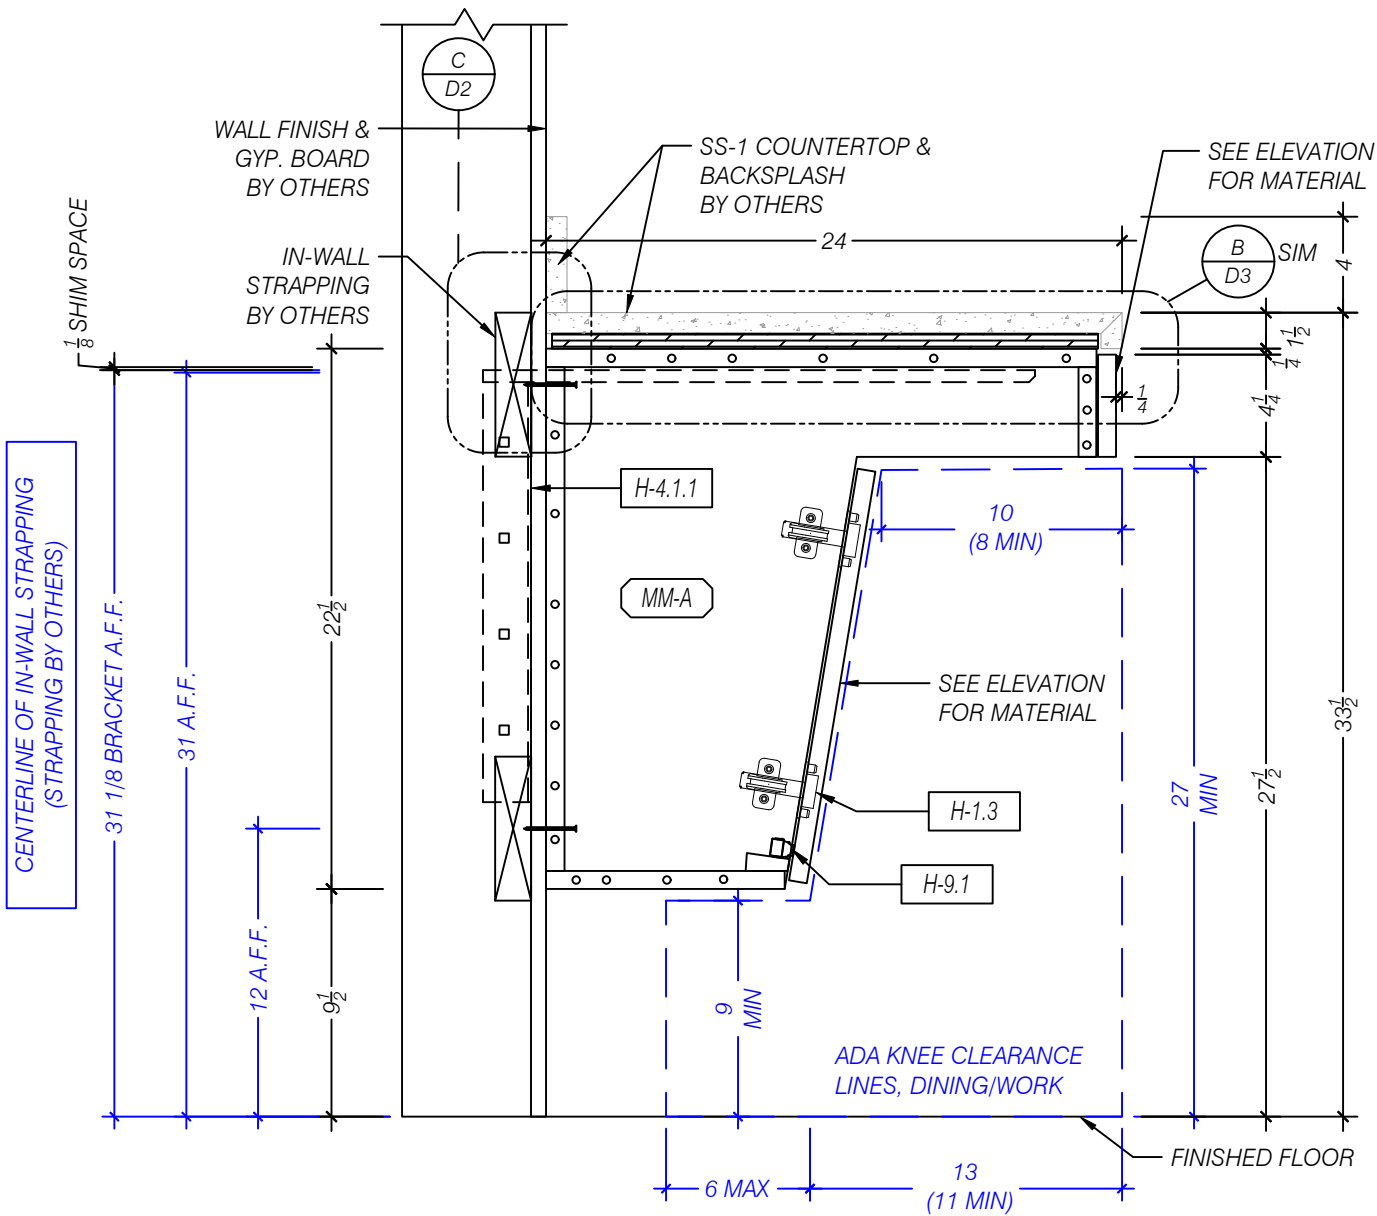

**A** SECTION - SHROUD CABINET  
SCALE 1:8 (1 1/2"=1'-0")  
ARCH REF: 9/AE583

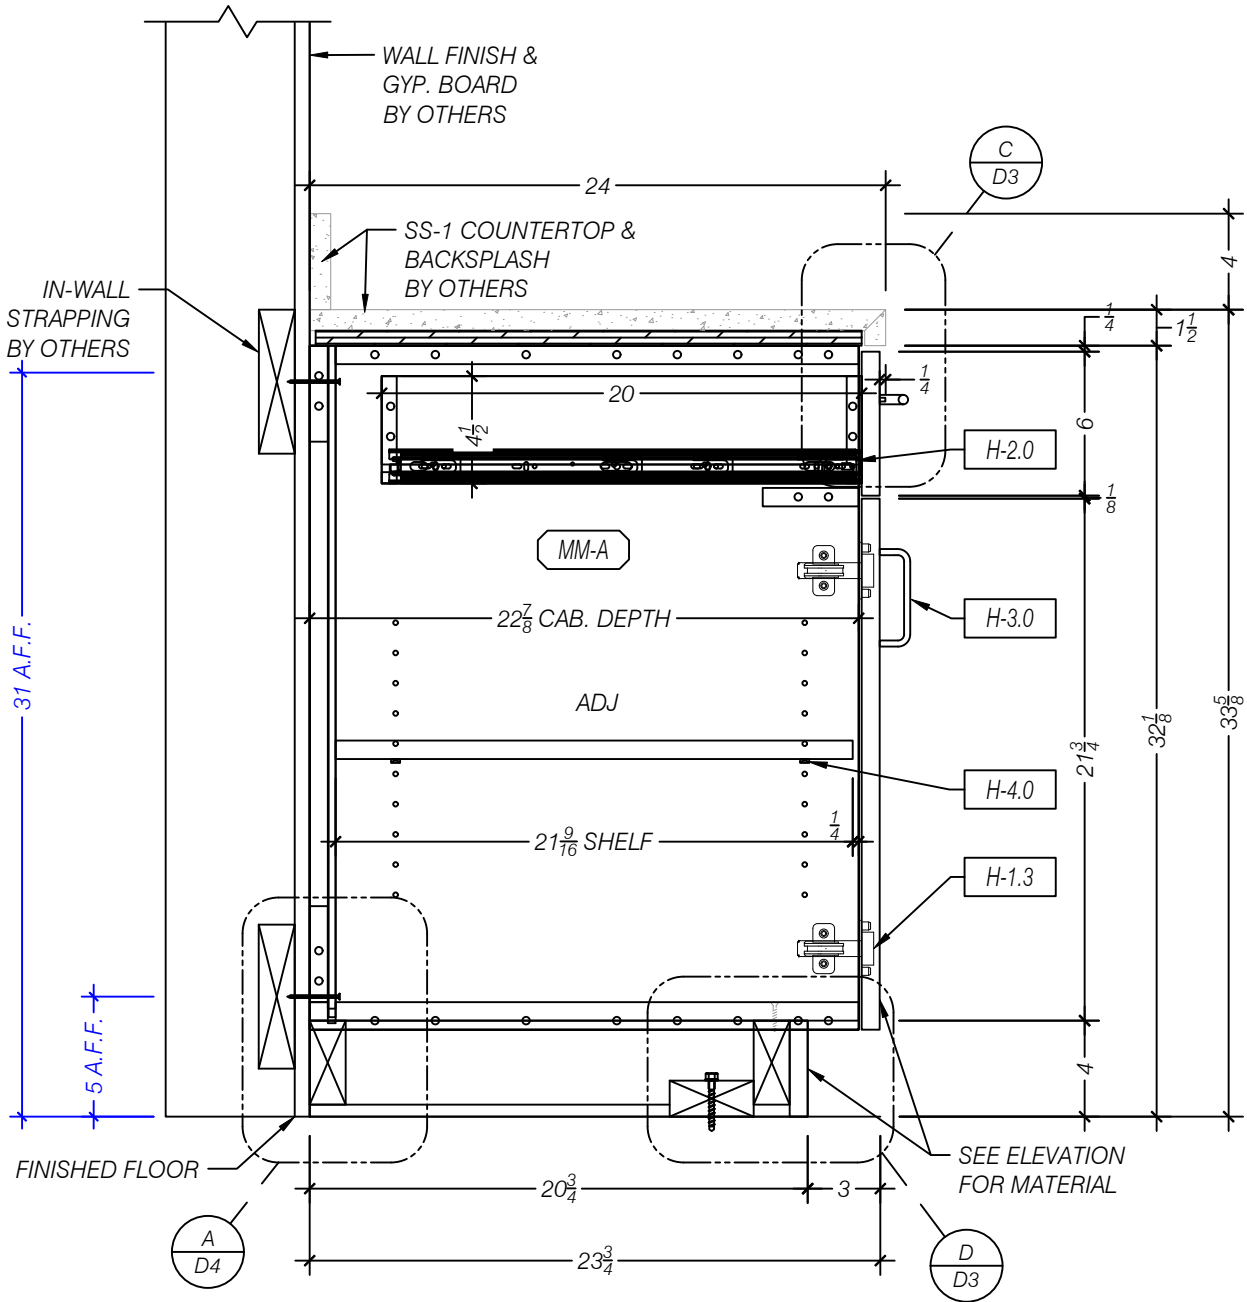

**B** SECTION - DOOR/DRAWER CABINET  
SCALE 1:8 (1 1/2"=1'-0")  
ARCH REF: 7/AE581

**DGS SREOC COSTA**  
**MESA**  
**SECTION DETAILS**

| ISSUE      |                     | BY   |
|------------|---------------------|------|
| DATE       | DESCRIPTION         |      |
| 05/05/2026 | REV-A FOR SUBMITTAL | Q-AS |
| -          | -                   | -    |
| -          | -                   | -    |
| -          | -                   | -    |
| -          | -                   | -    |

| SITE ADDRESS |                                       |      |       |
|--------------|---------------------------------------|------|-------|
| STREET       | 2301 South Shelley Circle Bldg. A & B |      |       |
| CITY         | Costa Mesa                            |      |       |
| STATE        | CA                                    | ZIP  | 92626 |
| JOB #:       | 26034                                 | REV: | -     |
| MOD #:       | -                                     | REL: | -     |

NOTE:  
REFER TO SPECIFICATION PAGE  
FOR MATERIAL, HARDWARE AND JOINERY

DGS SREOC COSTA



MESA

SECTION DETAILS


| ISSUE      |                     | BY   |
|------------|---------------------|------|
| DATE       | DESCRIPTION         |      |
| 05/05/2026 | REV-A FOR SUBMITTAL | Q-AS |
| -          | -                   | -    |
| -          | -                   | -    |
| -          | -                   | -    |
| -          | -                   | -    |

| SITE ADDRESS |                                       |      |       |
|--------------|---------------------------------------|------|-------|
| STREET       | 2301 South Shelley Circle Bldg. A & B |      |       |
| CITY         | Costa Mesa                            |      |       |
| STATE        | CA                                    | ZIP  | 92626 |
| JOB #:       | 26034                                 | REV: | -     |
| MOD #:       | -                                     | REL: | -     |


S5

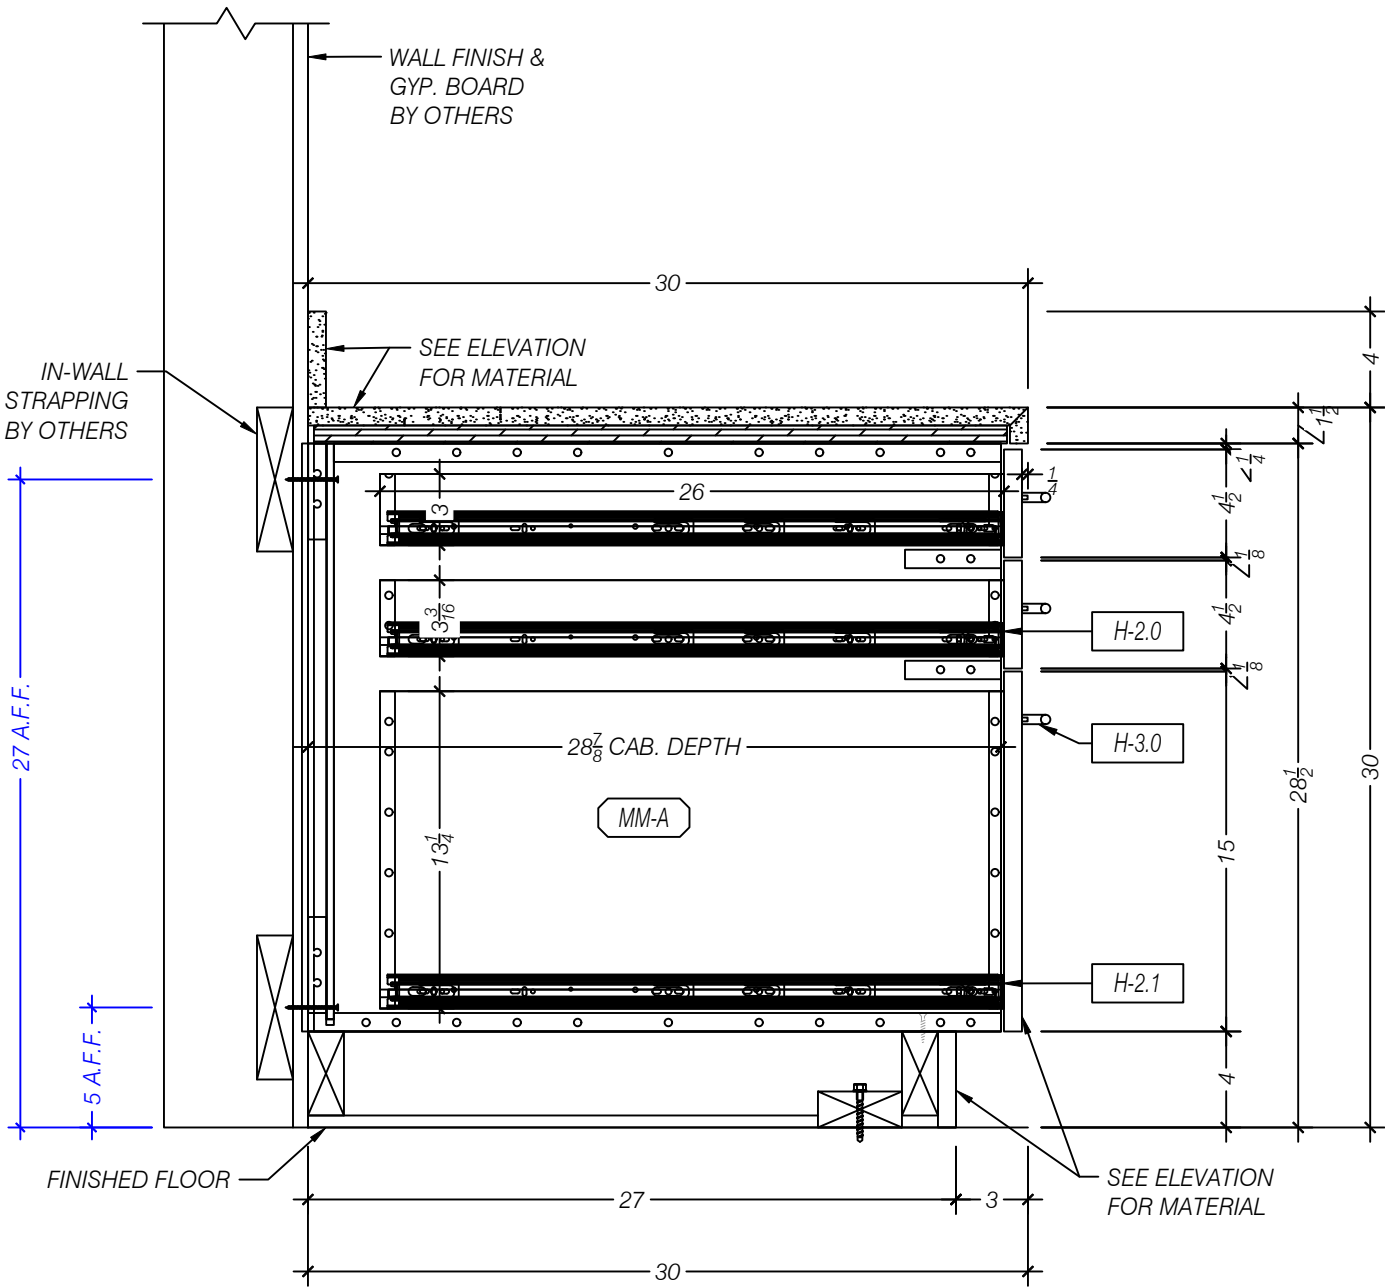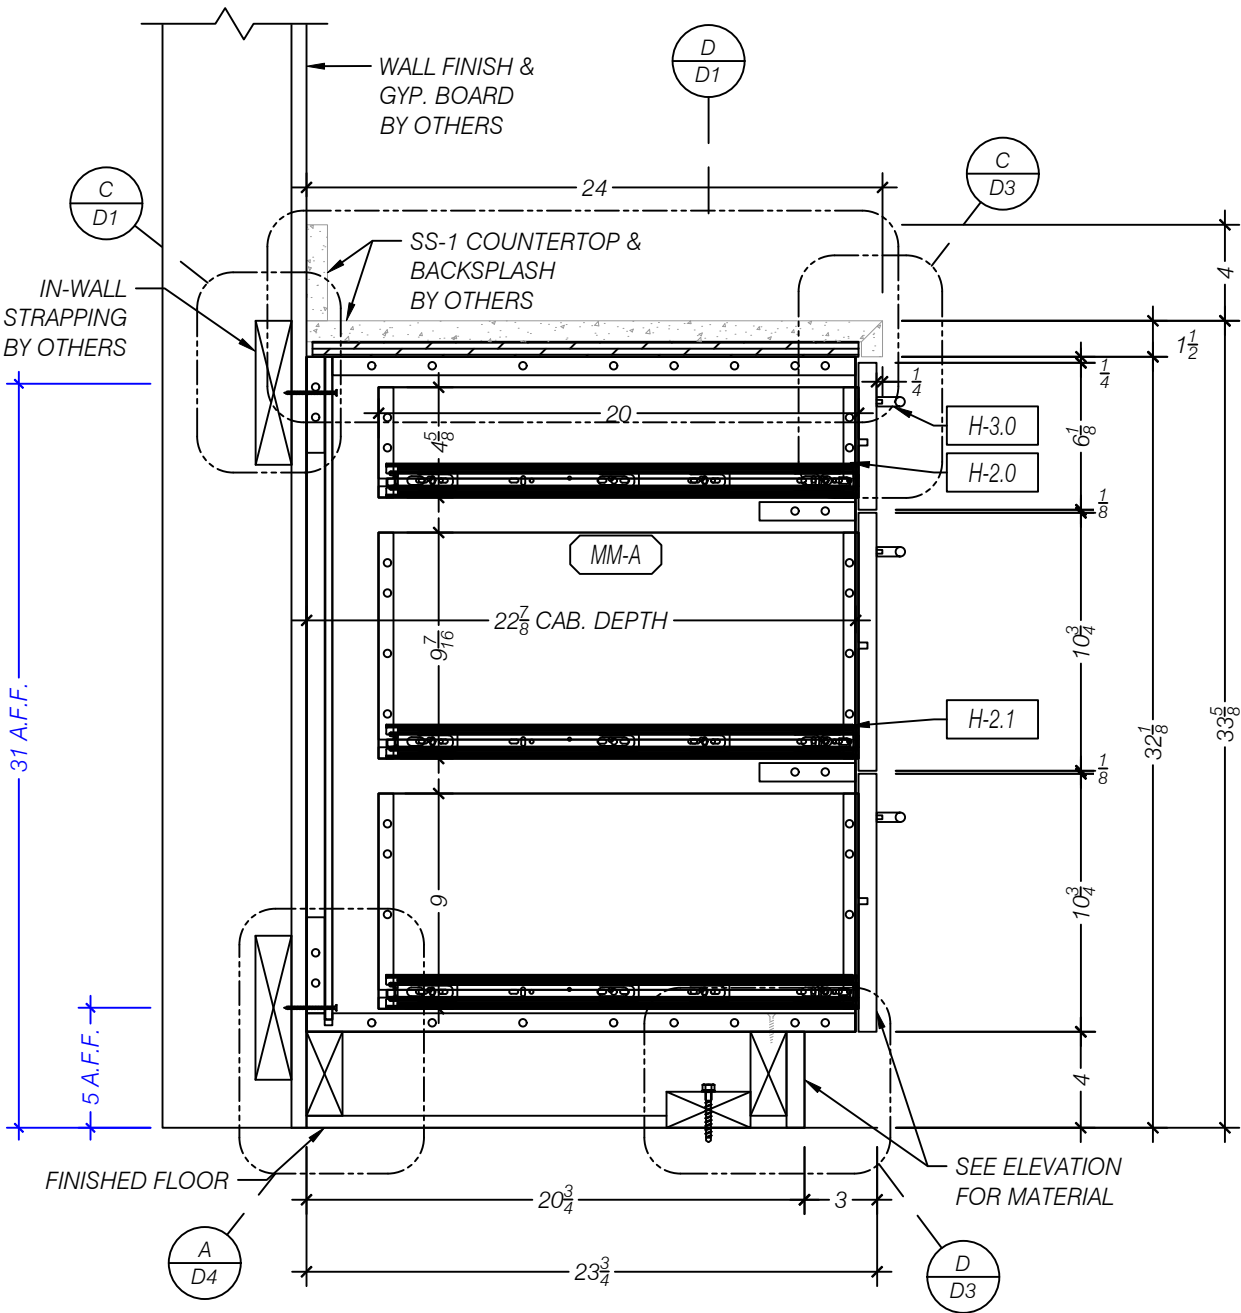

NOTE:  
REFER TO SPECIFICATION PAGE  
FOR MATERIAL, HARDWARE AND JOINERY

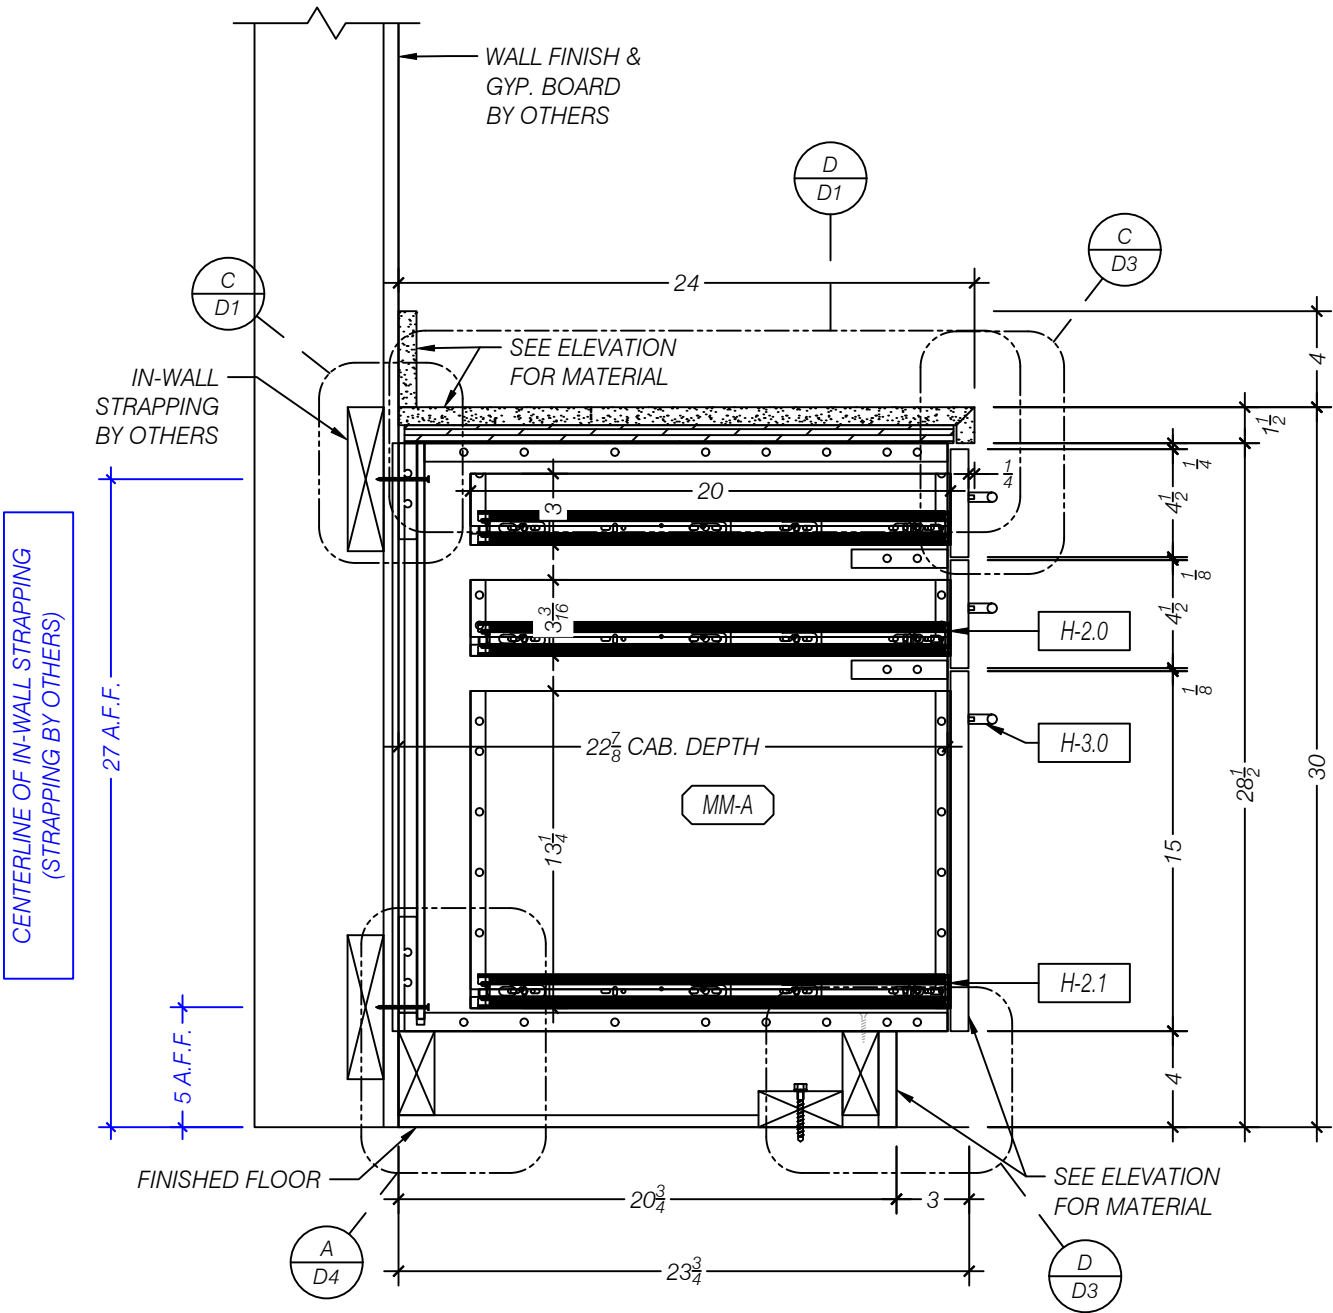

**A** SECTION - 3 DRAWER CABINET  
SCALE 1:8 (1 1/2"=1'-0")  
ARCH REF: 2/AE583

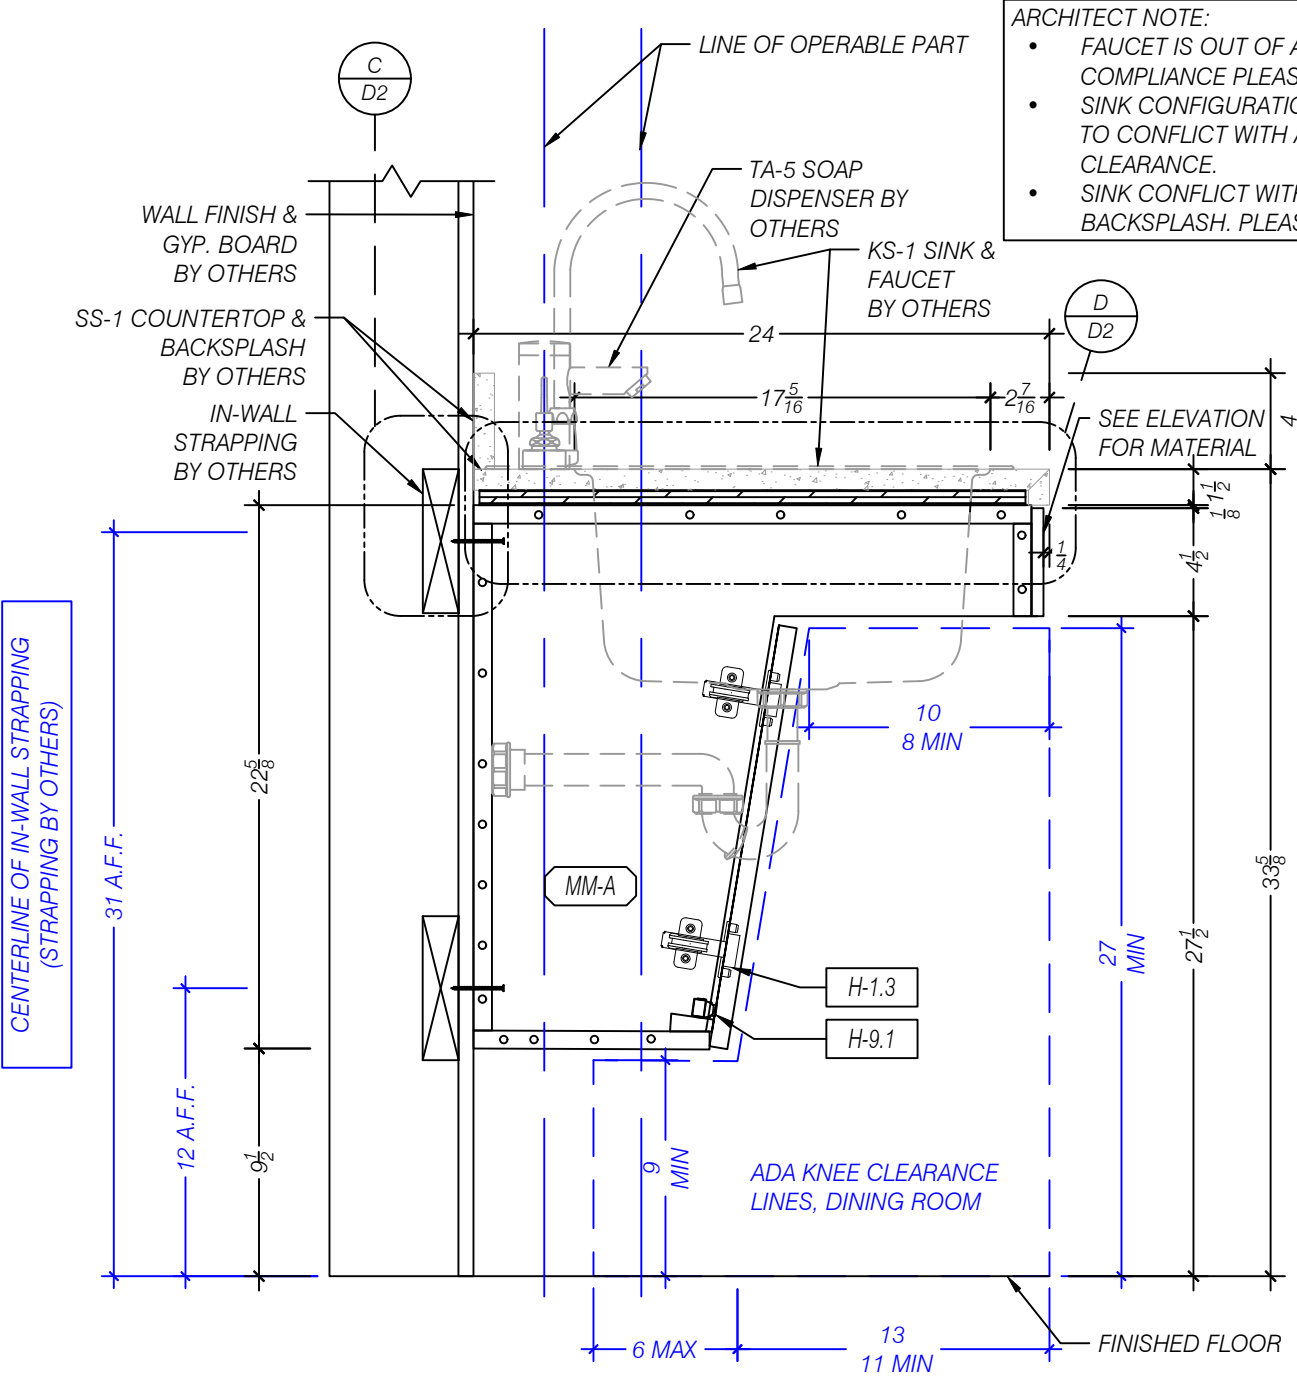

**B** SECTION - ACCESSIBLE SINK CABINET  
SCALE 1:8 (1 1/2"=1'-0")  
ARCH REF: 12/AE581

ARCHITECT NOTE:

- FAUCET IS OUT OF ADA REACH COMPLIANCE PLEASE ADVISE.
- SINK CONFIGURATION APPEARS TO CONFLICT WITH ADA CLEARANCE.
- SINK CONFLICT WITH BACKSPLASH. PLEASE CONFIRM.

**DGS SREOC COSTA  
MESA**




5640 WEST END ROAD  
ARCATA, CA 95521  
PH (707) 822-4034 FAX (707) 822-5478  
WWW.CRESTMARKMILLWORK.COM


**SECTION DETAILS**

| ISSUE        |                                       | BY        |
|--------------|---------------------------------------|-----------|
| DATE         | DESCRIPTION                           |           |
| 05/05/2026   | REV-A FOR SUBMITTAL                   | Q-AS      |
| -            | -                                     | -         |
| -            | -                                     | -         |
| -            | -                                     | -         |
| -            | -                                     | -         |
| SITE ADDRESS |                                       |           |
| STREET       | 2301 South Shelley Circle Bldg. A & B |           |
| CITY         | Costa Mesa                            |           |
| STATE        | CA                                    | ZIP 92626 |
| JOB #:       | 26034                                 | REV: -    |
| MOD #:       | -                                     | REL: -    |
| S6           |                                       |           |

NOTE:  
REFER TO SPECIFICATION PAGE  
FOR MATERIAL, HARDWARE AND JOINERY

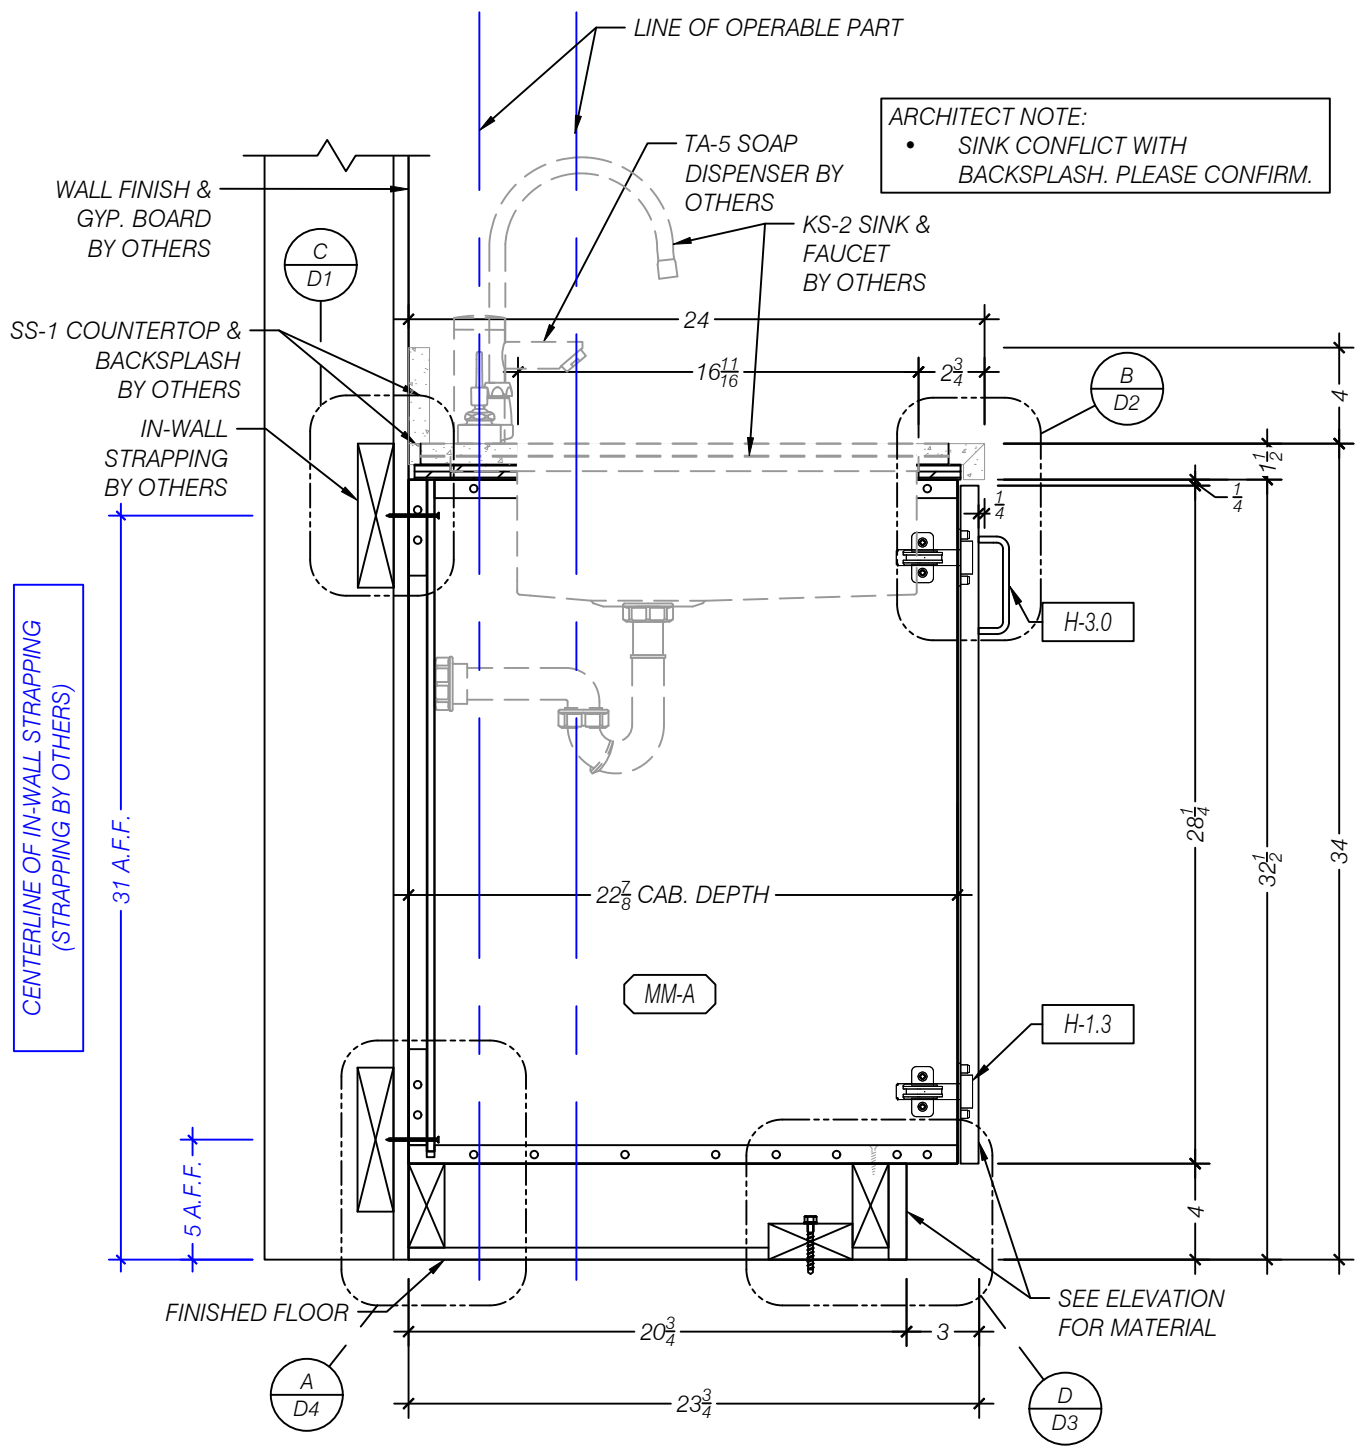

**A** SECTION - DRAWER CABINET  
SCALE 1:8 (1 1/2"=1'-0")  
ARCH REF: 2/AE583

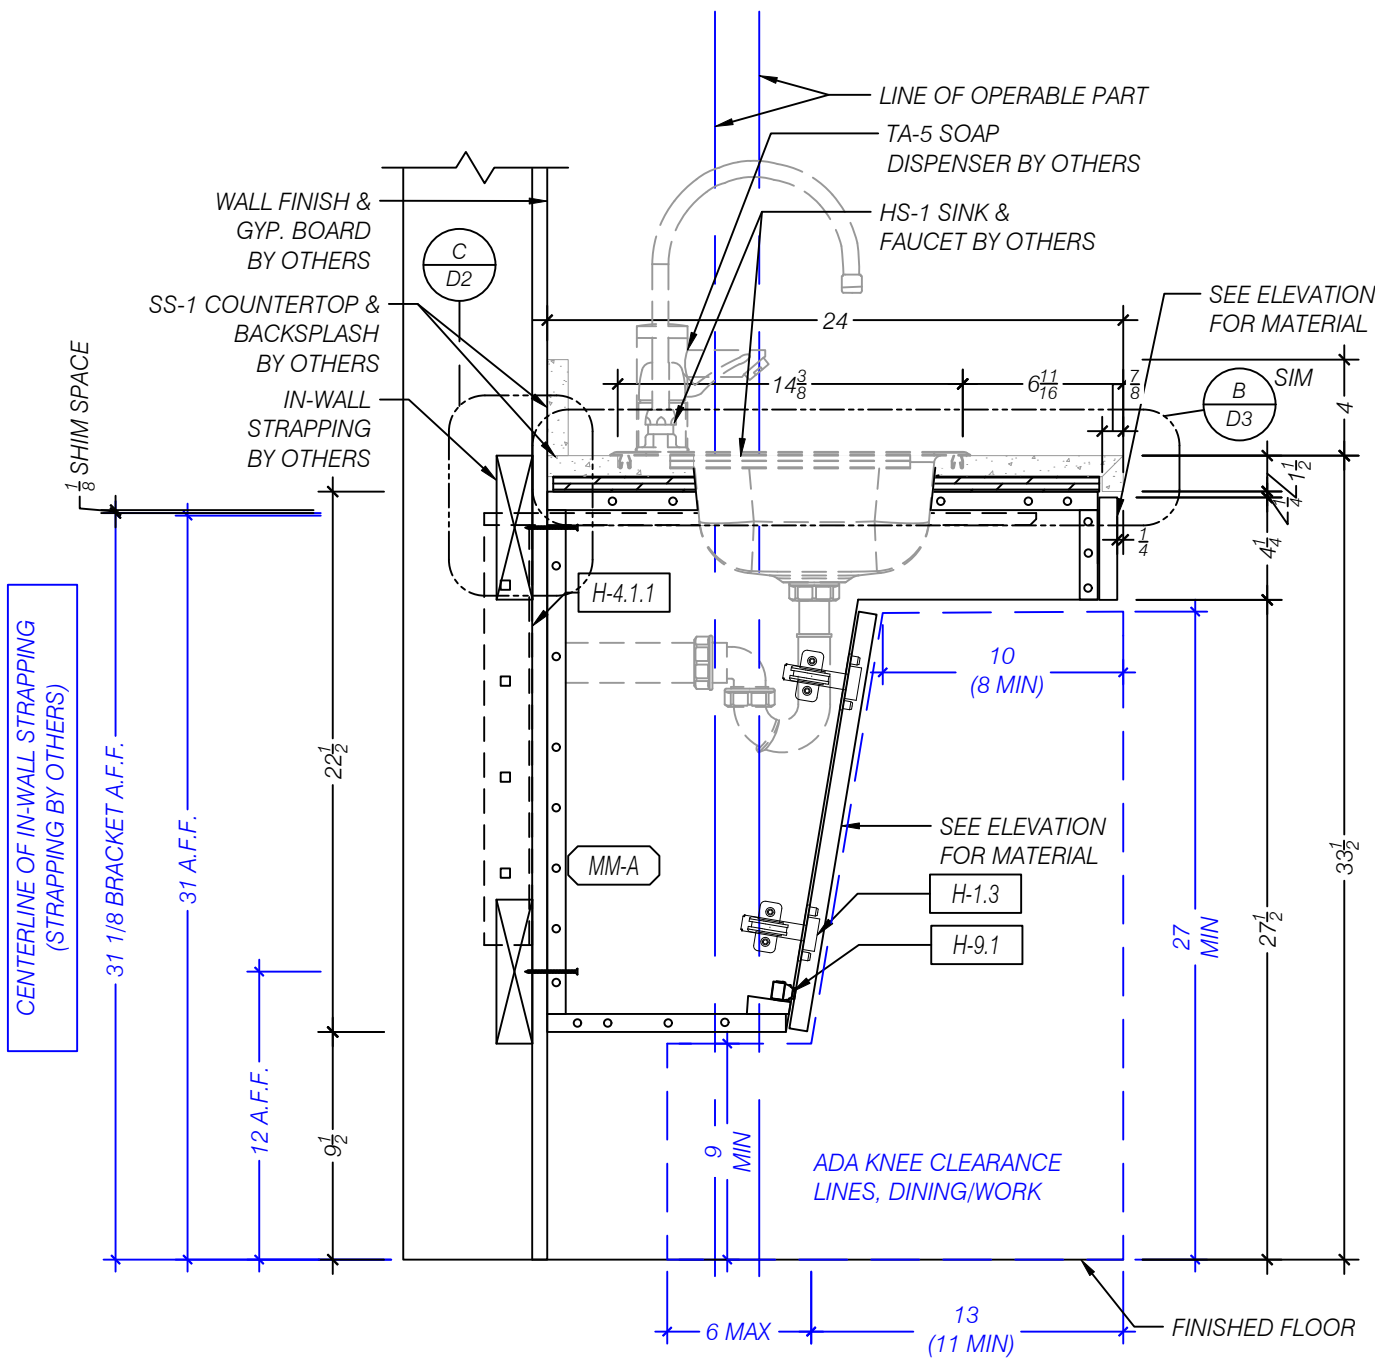



**B** SECTION - ACCESSIBLE SINK CABINET  
SCALE 1:8 (1 1/2"=1'-0")  
ARCH REF: 12/AE581

**DGS SREOC COSTA  
MESA**

**SECTION DETAILS**

| ISSUE        |                                       | BY        |
|--------------|---------------------------------------|-----------|
| DATE         | DESCRIPTION                           | Q-AS      |
| 05/05/2026   | REV-A FOR SUBMITTAL                   | -         |
| -            | -                                     | -         |
| -            | -                                     | -         |
| -            | -                                     | -         |
| -            | -                                     | -         |
| SITE ADDRESS |                                       |           |
| STREET       | 2301 South Shelley Circle Bldg. A & B |           |
| CITY         | Costa Mesa                            |           |
| STATE        | CA                                    | ZIP 92626 |
| JOB #:       | 26034                                 | REV: -    |
| MOD #:       | -                                     | REL: -    |
| <b>S7</b>    |                                       |           |


NOTE: OUTLINE OF SINK IS FOR GRAPHIC PURPOSE ONLY. ADA COMPLIANCE OF SINK TO BE CONFIRMED & COORDINATED BY OTHERS.

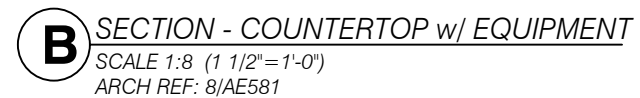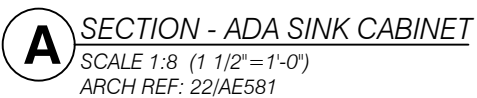


**DGS SREOC COSTA  
MESA  
SECTION DETAILS**

| ISSUE        |                                       |       |        |
|--------------|---------------------------------------|-------|--------|
| DATE         | DESCRIPTION                           | BY    |        |
| 05/05/2026   | REV-A FOR SUBMITTAL                   | Q-AS  |        |
|              |                                       |       |        |
|              |                                       |       |        |
| SITE ADDRESS |                                       |       |        |
| STREET       | 2301 South Shelley Circle Bldg. A & B |       |        |
| CITY         | Costa Mesa                            |       |        |
| STATE        | CA                                    | ZIP   | 92626  |
| JOB #:       |                                       | 26034 | REV: - |
| MOD #:       |                                       | -     | REL: - |
| S8           |                                       |       |        |

NOTE:  
REFER TO SPECIFICATION PAGE  
FOR MATERIAL, HARDWARE AND JOINERY

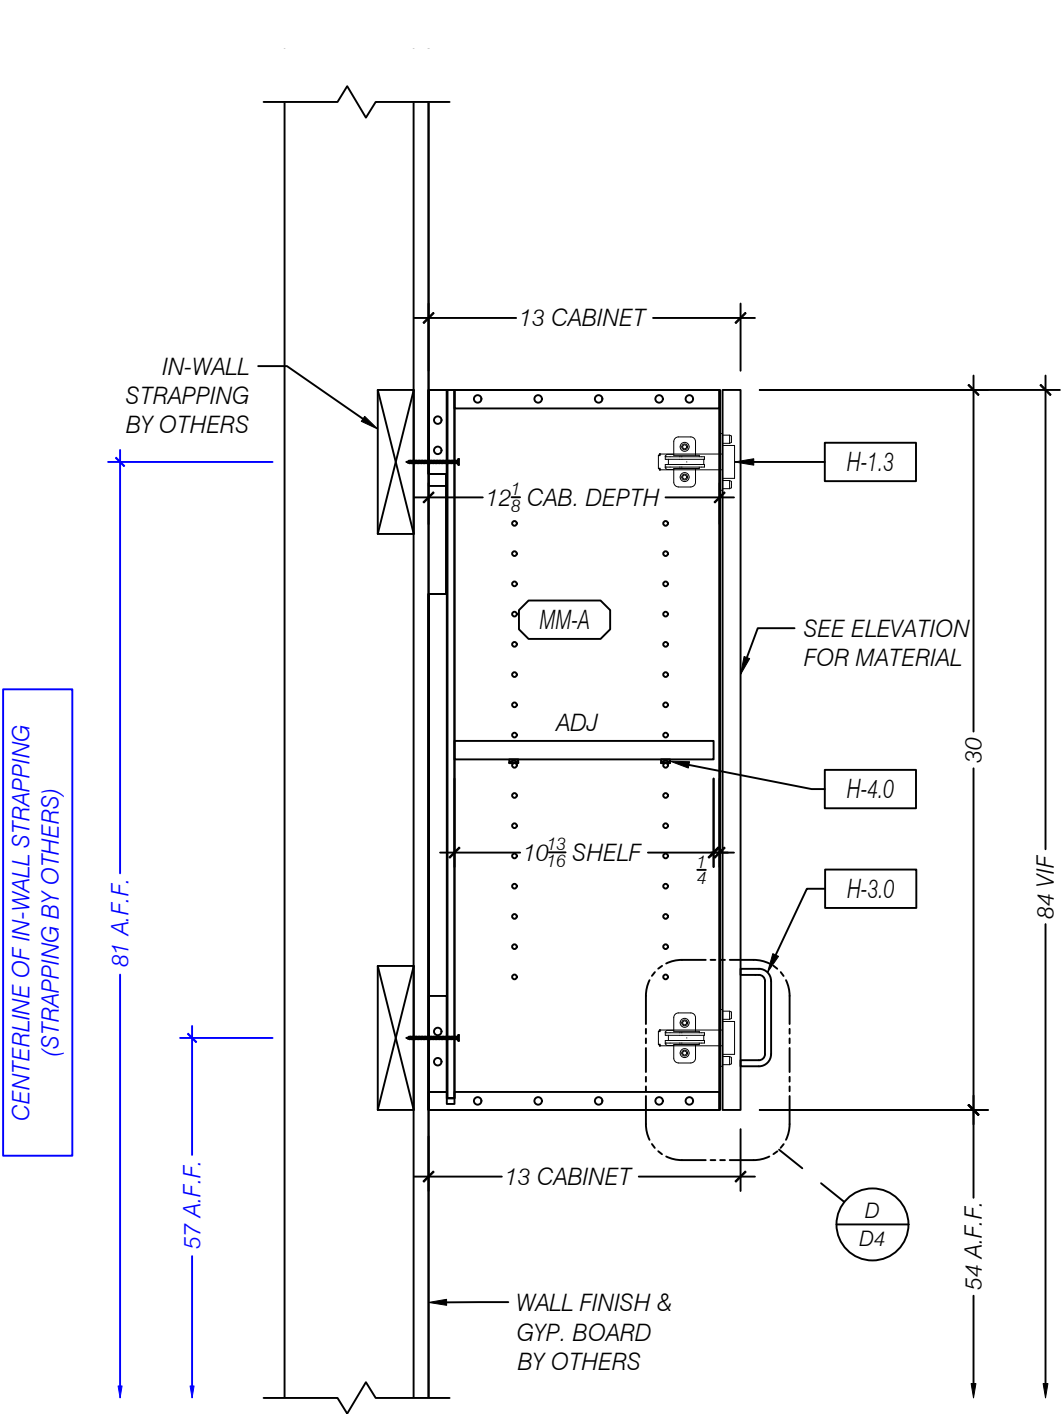

**A** SECTION - WALL CABINET  
SCALE 1:8 (1 1/2"=1'-0")  
ARCH REF: 13/AE581

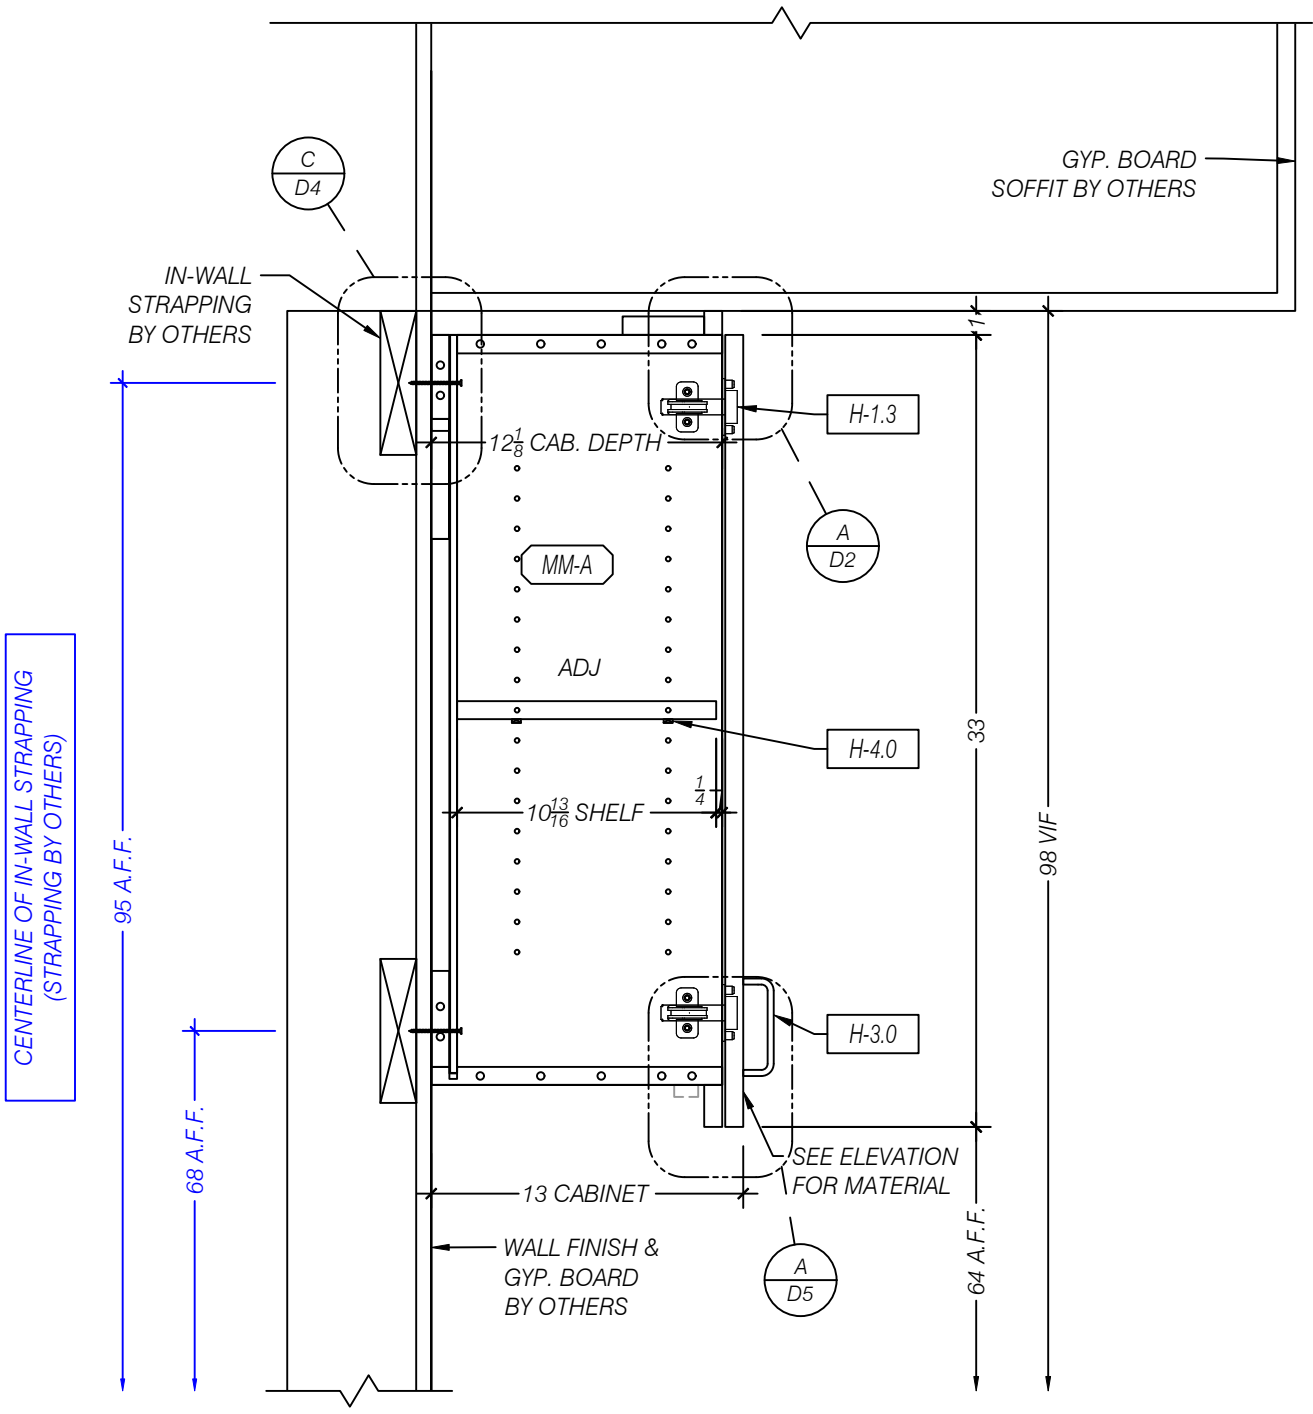


**B** SECTION - WALL CABINET w/ LIGHT VALANCE  
SCALE 1:8 (1 1/2"=1'-0")  
ARCH REF: 13/AE581

**DGS SREOC COSTA**  
**MESA**  
**SECTION DETAILS**

| ISSUE      |                     | BY   |
|------------|---------------------|------|
| DATE       | DESCRIPTION         |      |
| 05/05/2026 | REV-A FOR SUBMITTAL | Q-AS |
| -          | -                   | -    |
| -          | -                   | -    |
| -          | -                   | -    |
| -          | -                   | -    |

| SITE ADDRESS |                                       |      |       |
|--------------|---------------------------------------|------|-------|
| STREET       | 2301 South Shelley Circle Bldg. A & B |      |       |
| CITY         | Costa Mesa                            |      |       |
| STATE        | CA                                    | ZIP  | 92626 |
| JOB #:       | 26034                                 | REV: | -     |
| MOD #:       | -                                     | REL: | -     |

NOTE:  
REFER TO SPECIFICATION PAGE  
FOR MATERIAL, HARDWARE AND JOINERY

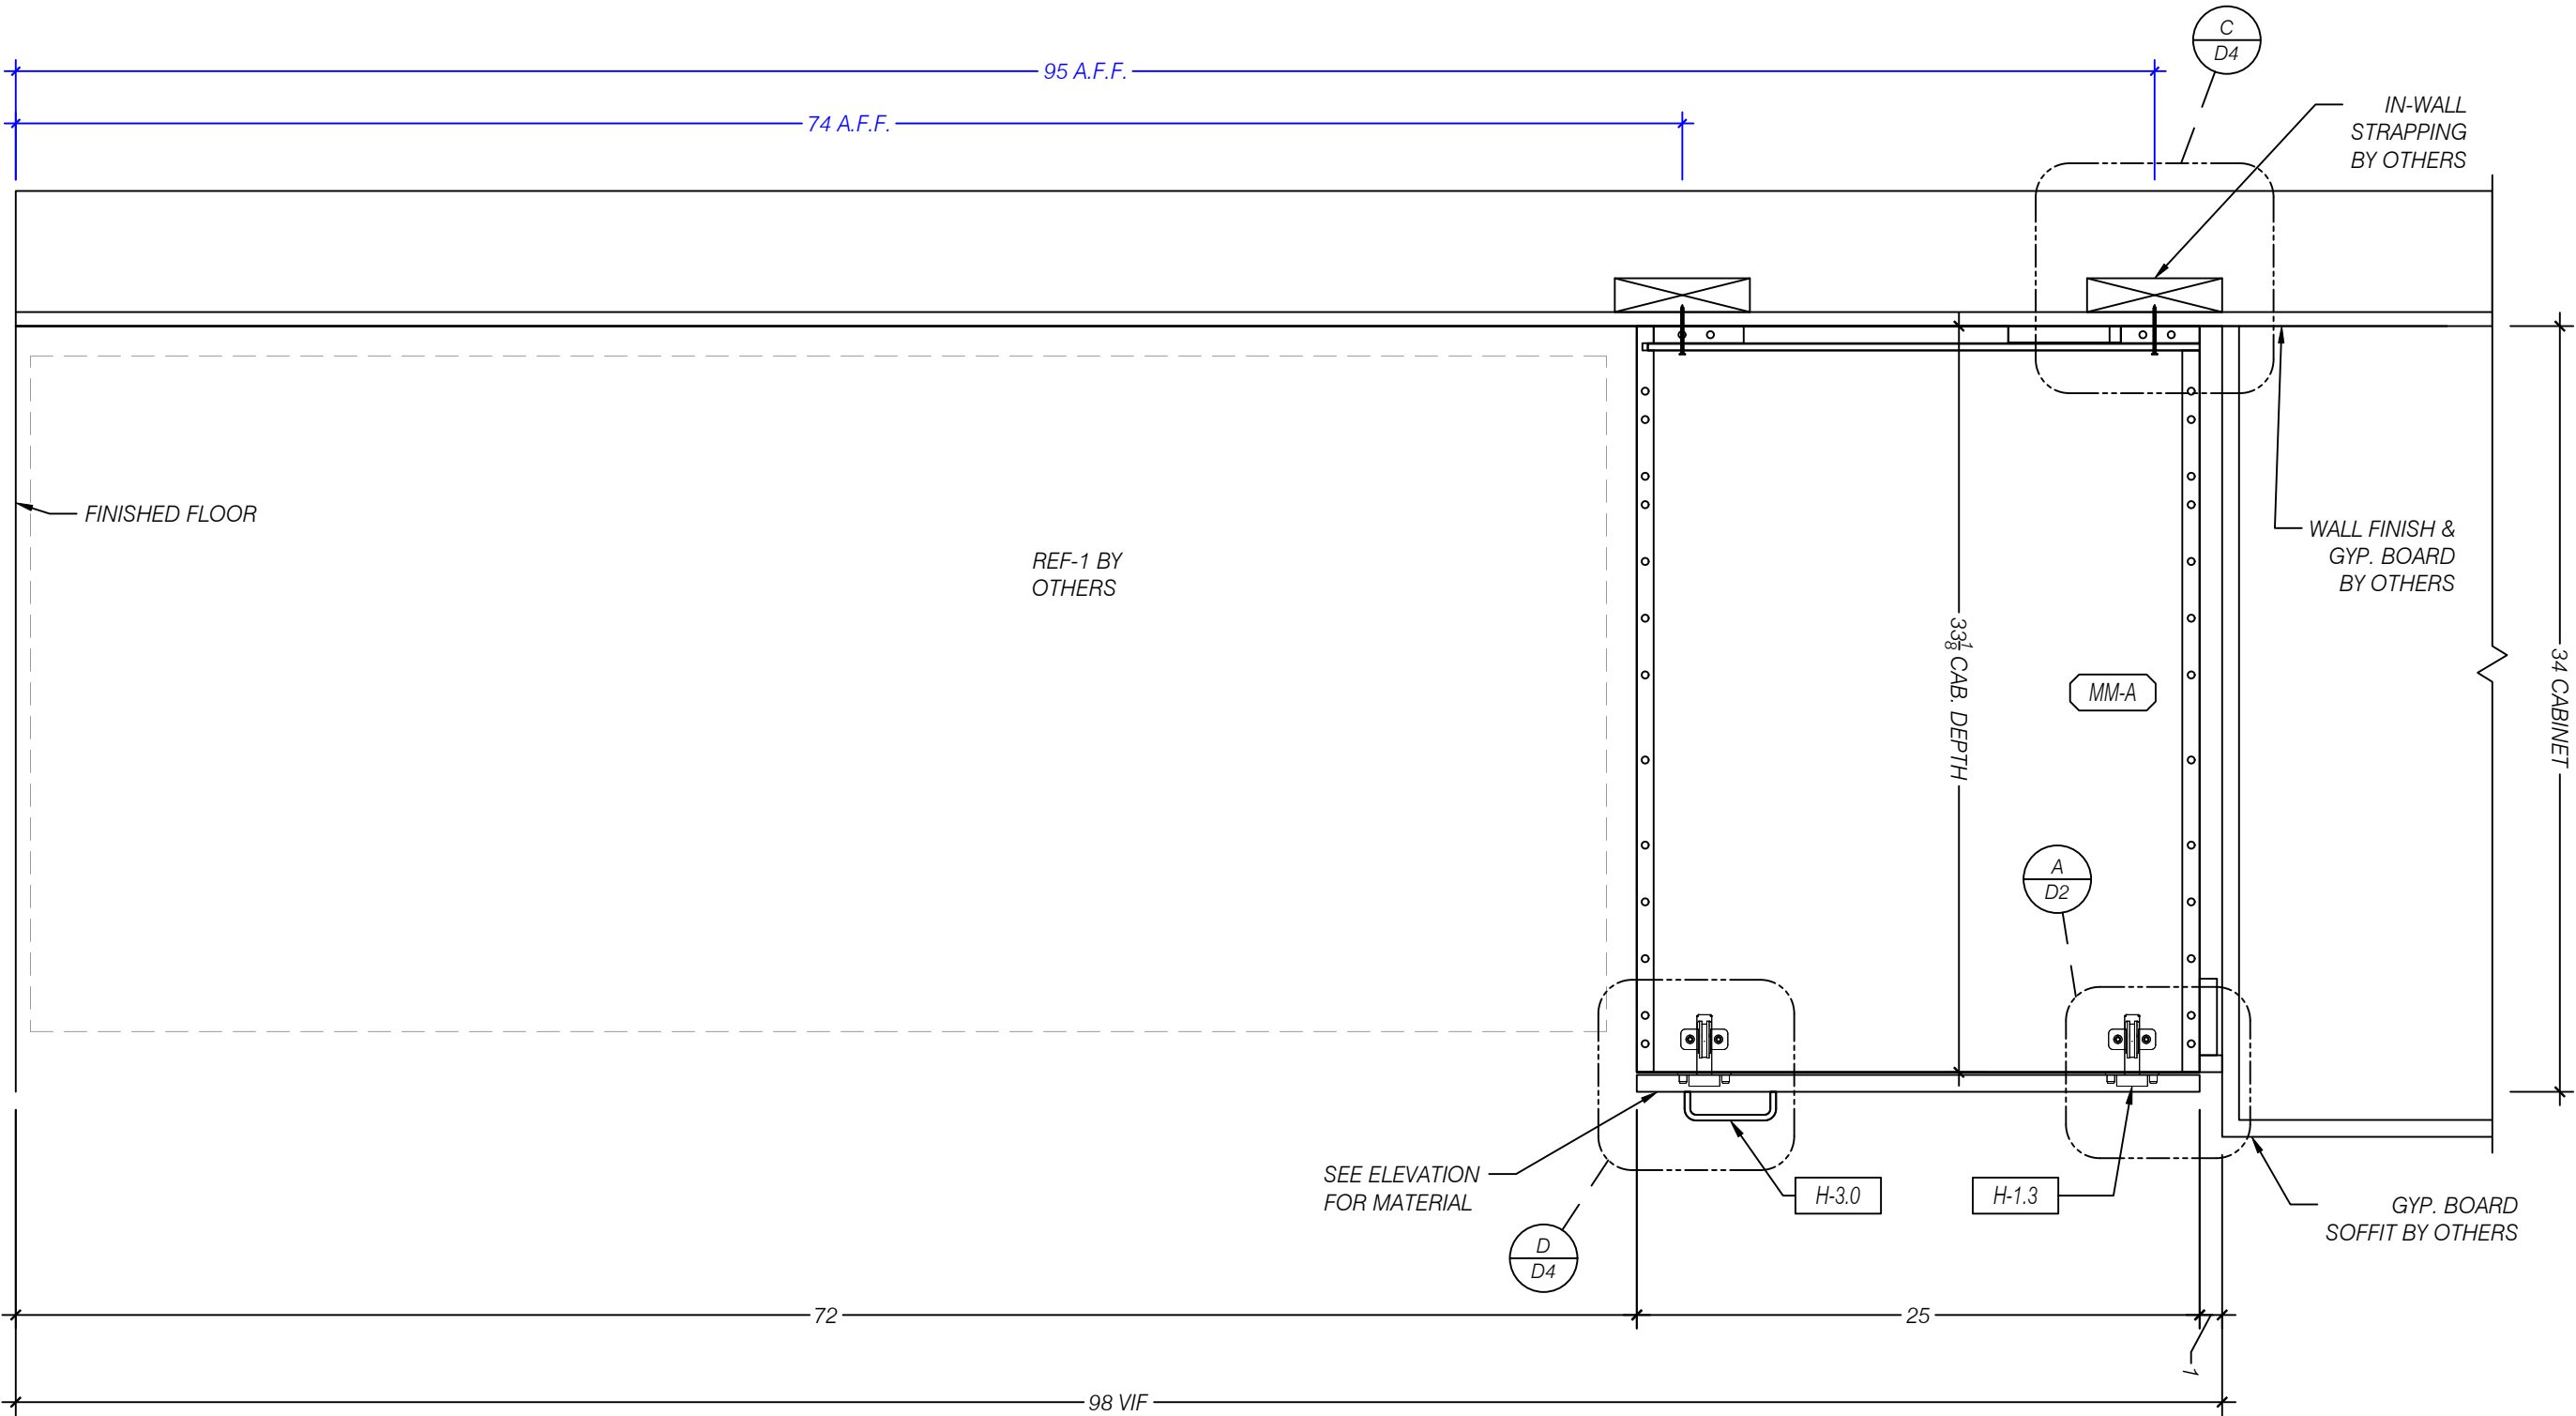


**A** SECTION - UPPER CABINET WITH EQUIPMENT  
SCALE 1:8 (1 1/2" = 1'-0")  
ARCH REF: 8/AE582

**DGS SREOC COSTA**  
**MESA**  
**SECTION DETAILS**

| ISSUE      |                     | BY   |
|------------|---------------------|------|
| DATE       | DESCRIPTION         |      |
| 05/05/2026 | REV-A FOR SUBMITTAL | Q-AS |
| -          | -                   | -    |
| -          | -                   | -    |
| -          | -                   | -    |
| -          | -                   | -    |

| SITE ADDRESS |                                       |      |       |
|--------------|---------------------------------------|------|-------|
| STREET       | 2301 South Shelley Circle Bldg. A & B |      |       |
| CITY         | Costa Mesa                            |      |       |
| STATE        | CA                                    | ZIP  | 92626 |
| JOB #:       | 26034                                 | REV: | -     |
| MOD #:       | -                                     | REL: | -     |

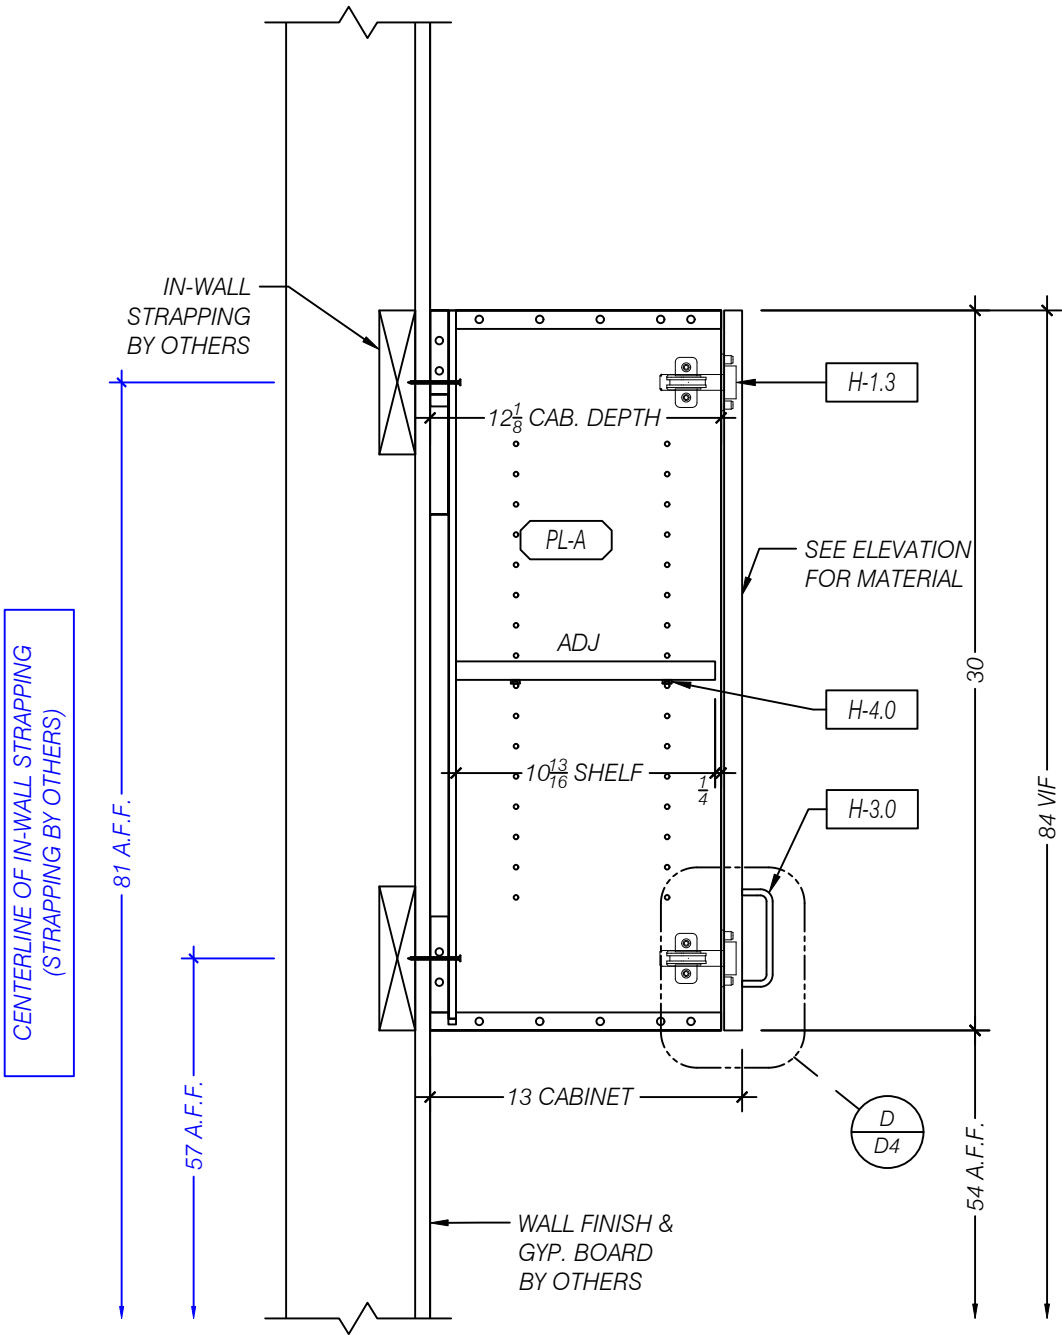

**A** SECTION - WALL CABINET  
SCALE 1:8 (1 1/2"=1'-0")  
ARCH REF: 13/AE581



**CRESTMARK**  
MILLWORK

5640 WEST END ROAD  
ARCATA, CA 95521  
PH (707) 822-4034 FAX (707) 822-5478  
WWW.CRESTMARKMILLWORK.COM

**DGS SREOC COSTA  
MESA**


**SECTION DETAILS**

| ISSUE      |                     | BY   |
|------------|---------------------|------|
| DATE       | DESCRIPTION         |      |
| 05/05/2026 | REV-A FOR SUBMITTAL | Q-AS |
| -          | -                   | -    |
| -          | -                   | -    |
| SITE ADDRESS |                                       |      |       |
|--------------|---------------------------------------|------|-------|
| STREET       | 2301 South Shelley Circle Bldg. A & B |      |       |
| CITY         | Costa Mesa                            |      |       |
| STATE        | CA                                    | ZIP  | 92626 |
| JOB #:       | 26034                                 | REV: | -     |
| MOD #:       | -                                     | REL: | -     |


**S11**

TYPICAL TOE KICK DETAILS SET TO INDUSTRY STANDARDS BY DEFAULT (U.O.N.)  
IF TOE IS SET TO SUB FLOOR, GC TO SPECIFY LOCATION OF LEVEL / CONTROL MARK  
TO BE USED, AND INSTALLER TO ADD FINISHED FLOOR THICKNESS  
TO FINISH OUT TOE AT SPECIFIED HEIGHT

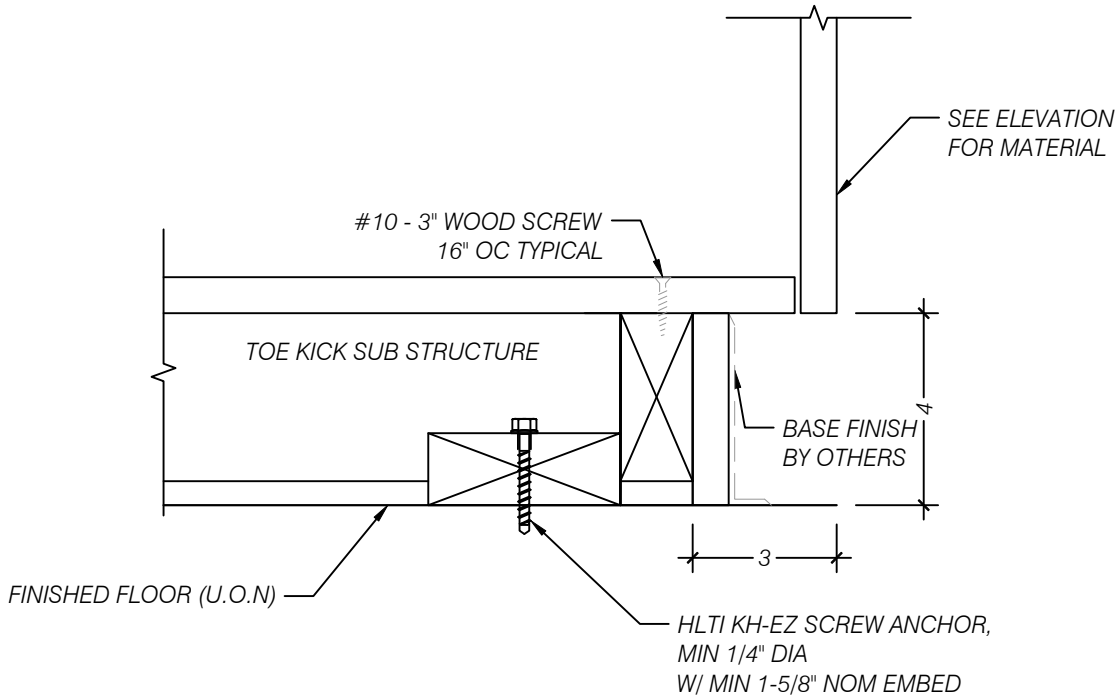


**A** ENLARGED DETAIL - TYPICAL TOE KICK FACE  
SCALE 1:4 (3"=1'-0")  
ARCH REF: 11/AE584

SHIMMING/SURFACE BLOCKING IS THE RESPONSIBILITY OF THE INSTALLER  
SURFACE BLOCKING/WALL CLEATS/Z-CLIPS WILL BE PROVIDED BY CRESTMARK (U.O.N.)  
CRESTMARK IS NOT RESPONSIBLE FOR GAPS DUE TO IRREGULAR WALL SURFACES  
IN THE EVENT OF EXTREME GAPS, A SURFACE MOUNT FLAT MOLDING WILL BE USED (U.O.N.)

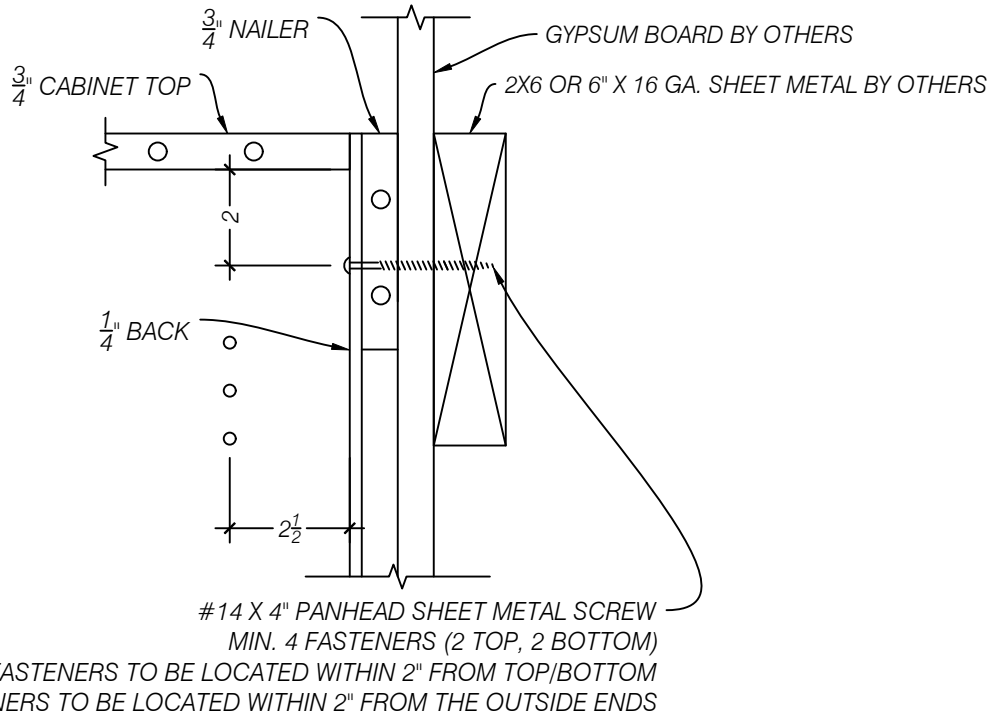


**C** ENLARGED DETAIL - BASE CABINET ATTACHMENT @ WALL  
SCALE 1:4 (3"=1'-0")  
ARCH REF: NA

SCRIBES ARE TO BE FLUSH WITH FRONT EDGE OF CABINET (U.O.N.)  
GRAIN DIRECTION ON SCRIBE FILLERS TO BE CONSISTENT WITH CABINET FACE

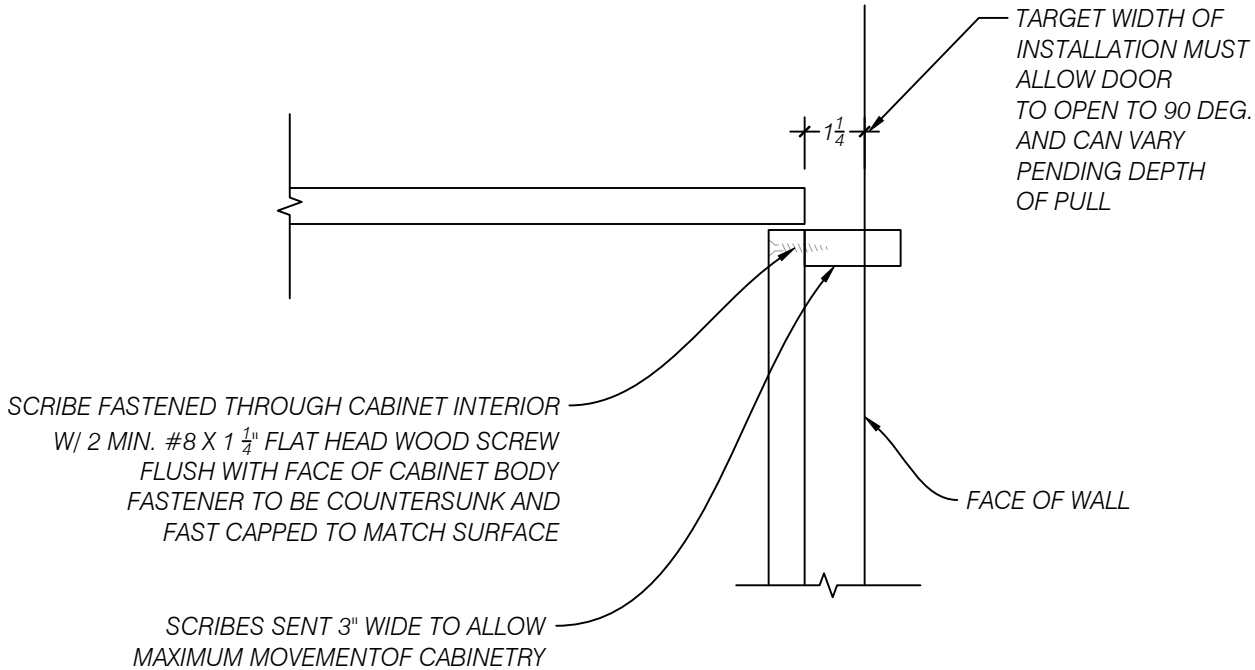

**B** ENLARGED DETAIL - CASEWORK SCRIBE @ WALL  
SCALE 1:4 (3"=1'-0")  
ARCH REF: NA

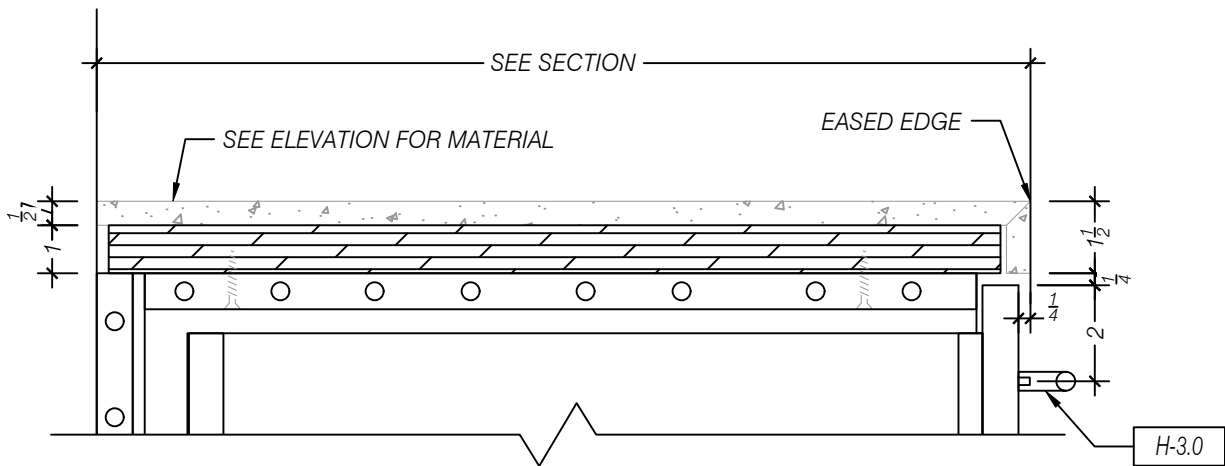


**D** ENLARGED DETAIL - COUNTERTOP DETAIL  
SCALE 1:4 (3"=1'-0")  
ARCH REF: NA

**DGS SREOC COSTA**  
**MESA**  
**ENLARGED DETAILS**

| ISSUE | DESCRIPTION | BY   | DATE       | REV-A - FOR SUBMITTAL |   |   |   |   |   |
|-------|-------------|------|------------|-----------------------|---|---|---|---|---|
|       |             |      |            |                       |   |   |   |   |   |
|       |             | Q-AS | 05/05/2026 | -                     | - | - | - | - | - |


| SITE ADDRESS |                                       |      |       |
|--------------|---------------------------------------|------|-------|
| STREET       | 2301 South Shelley Circle Bldg. A & B |      |       |
| CITY         | Costa Mesa                            |      |       |
| STATE        | CA                                    | ZIP  | 92626 |
| JOB #:       | 26034                                 | REV: | A     |
| MOD #:       | #                                     | REL: | N/A   |

**D1**

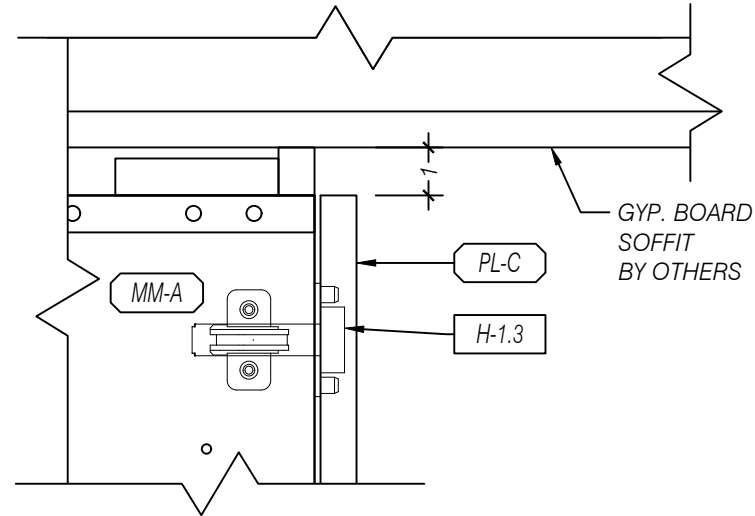


**A** ENLARGED DETAIL - SOFFIT SCRIBE  
SCALE 1:4 (3"=1'-0")  
ARCH REF: NA


SHIMMING/SURFACE BLOCKING IS THE RESPONSIBILITY OF THE INSTALLER  
SURFACE BLOCKING/WALL CLEATS/Z-CLIPS WILL BE PROVIDED BY CRESTMARK (U.O.N.)  
CRESTMARK IS NOT RESPONSIBLE FOR GAPS DUE TO IRREGULAR WALL SURFACES  
IN THE EVENT OF EXTREME GAPS, A SURFACE MOUNT FLAT MOLDING WILL BE USED (U.O.N.)

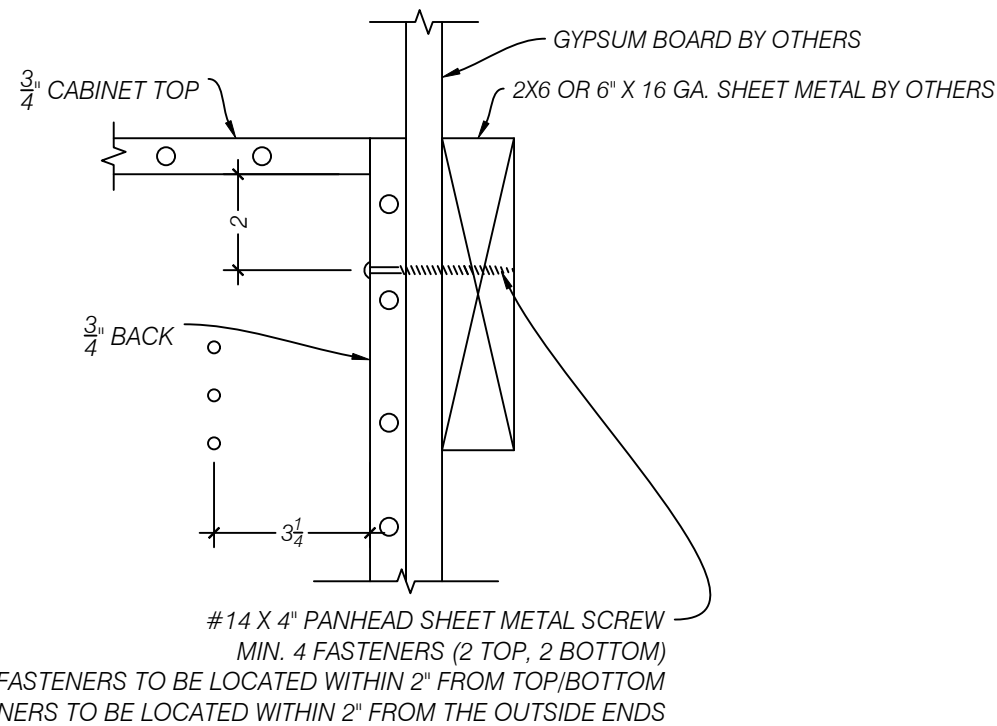

**C** ENLARGED DETAIL - THICK BACK CABINET ATTACHEMENT @ WALL  
SCALE 1:4 (3"=1'-0")  
ARCH REF: NA

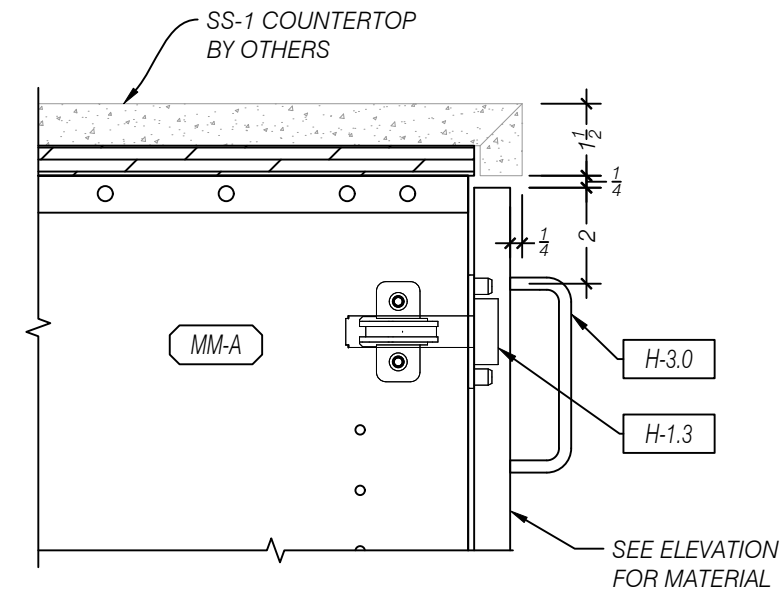

**B** ENLARGED DETAIL - DOOR PULL LOCATION  
SCALE 1:4 (3"=1'-0")  
ARCH REF: NA

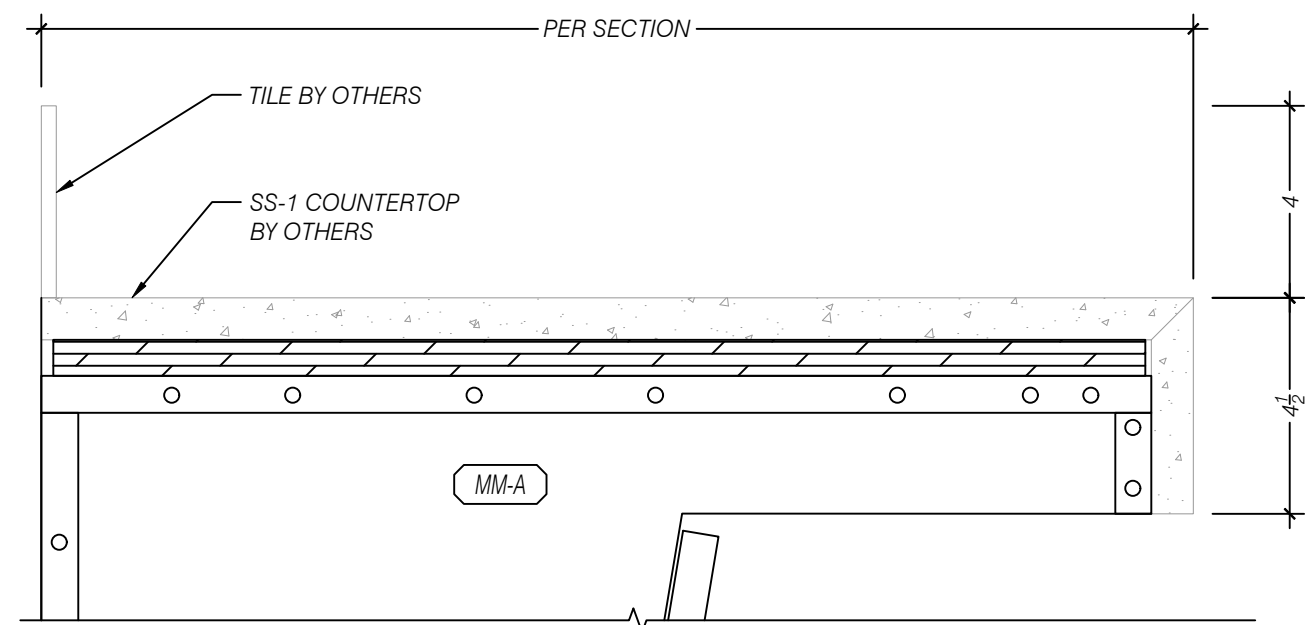


**D** ENLARGED DETAIL - COUNTERTOP DETAIL  
SCALE 1:4 (3"=1'-0")  
ARCH REF: NA

**DGS SREOC COSTA**  
**MESA**  
**ENLARGED DETAILS**




5640 WEST END ROAD  
ARCATA, CA 95521  
PH (707) 822-4034 FAX (707) 822-5478  
WWW.CRESTMARKMILLWORK.COM


| ISSUE        | DATE                                  | DESCRIPTION           | BY       |
|--------------|---------------------------------------|-----------------------|----------|
|              | 05/05/2026                            | REV-A - FOR SUBMITTAL | Q-AS     |
|              |                                       |                       |          |
|              |                                       |                       |          |
| SITE ADDRESS |                                       |                       |          |
| STREET       | 2301 South Shelley Circle Bldg. A & B |                       |          |
| CITY         | Costa Mesa                            |                       |          |
| STATE        | CA                                    | ZIP                   | 92626    |
| JOB #:       |                                       | 26034                 | REV: A   |
| MOD #:       |                                       | #                     | REL: N/A |
| D2           |                                       |                       |          |

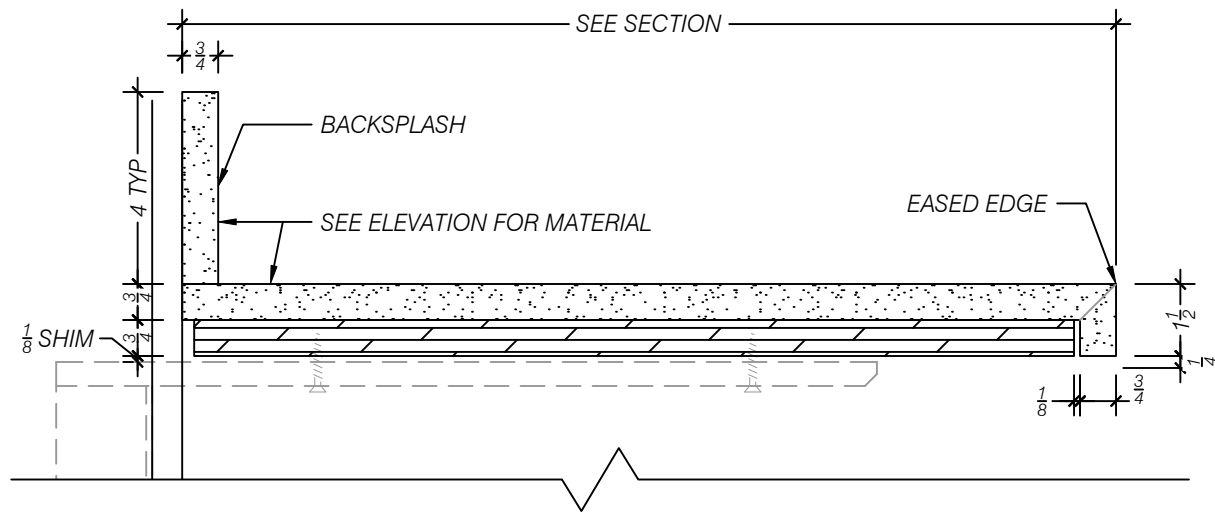


**A** ENLARGED DETAIL - P-LAM COUNTERTOP WITH BRACKETS  
SCALE 1:4 (3"=1'-0")  
ARCH REF: 11/AE584

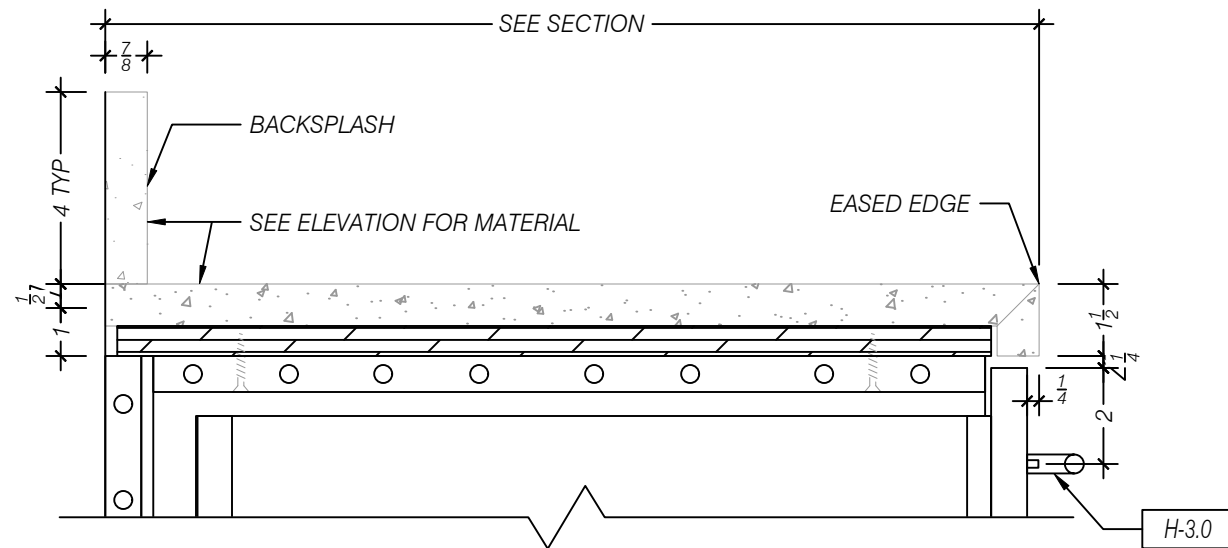

**B** ENLARGED DETAIL - COUNTERTOP DETAIL  
SCALE 1:4 (3"=1'-0")  
ARCH REF: 11/AE584

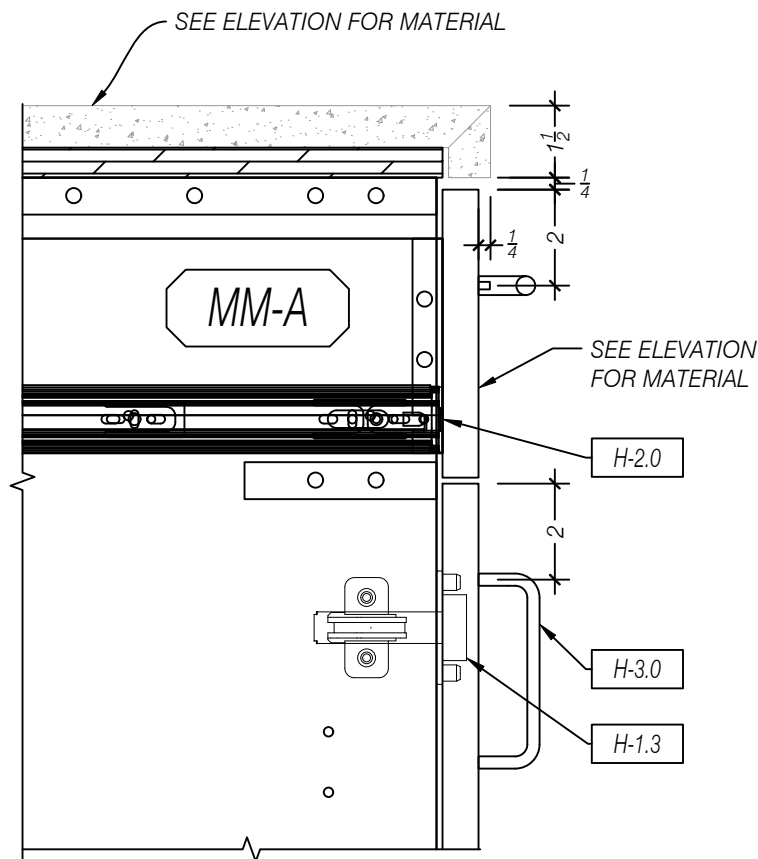

**C** ENLARGED DETAIL - DOOR/ DRAWER PULL LOCATION  
SCALE 1:4 (3"=1'-0")  
ARCH REF: NA

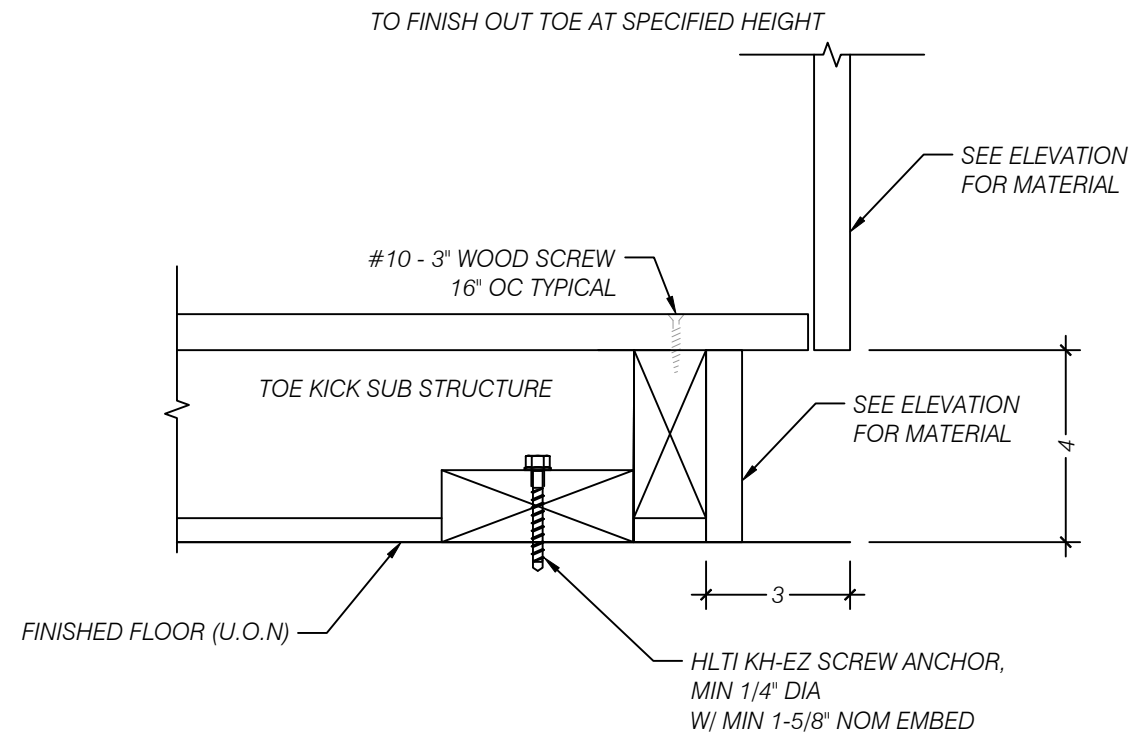

**D** ENLARGED DETAIL - TYPICAL TOE KICK FACE  
SCALE 1:4 (3"=1'-0")  
ARCH REF: 11/AE584

**DGS SREOC COSTA**  
**MESA**  
**ENLARGED DETAILS**

| ISSUE | DATE       | DESCRIPTION           | BY   |
|-------|------------|-----------------------|------|
|       | 05/05/2026 | REV-A - FOR SUBMITTAL | Q-AS |
|       |            |                       |      |
|       |            |                       |      |
|       |            |                       |      |
|       |            |                       |      |


| SITE ADDRESS |                                       |      |       |
|--------------|---------------------------------------|------|-------|
| STREET       | 2301 South Shelley Circle Bldg. A & B |      |       |
| CITY         | Costa Mesa                            |      |       |
| STATE        | CA                                    | ZIP  | 92626 |
| JOB #:       | 26034                                 | REV: | A     |
| MOD #:       | #                                     | REL: | N/A   |

**D3**



5640 WEST END ROAD  
ARCATA, CA 95521  
PH (707) 822-4034 FAX (707) 822-5478  
WWW.CRESTMARKMILLWORK.COM

ALL IN-WALL BLOCKING AND SUPPORT BRACKET PROVIDED BY GC/OTHERS (U.O.N.)  
CRESTMARK TO PROVIDE BLOCKING/SUPPORT BRACKET HEIGHTS ONLY  
CRESTMARK IS NOT RESPONSIBLE FOR INCORRECT BLOCKING HEIGHTS SET BY GC  
OR CHANGES MADE BY ARCHITECT AFTER BLOCKING IS SET

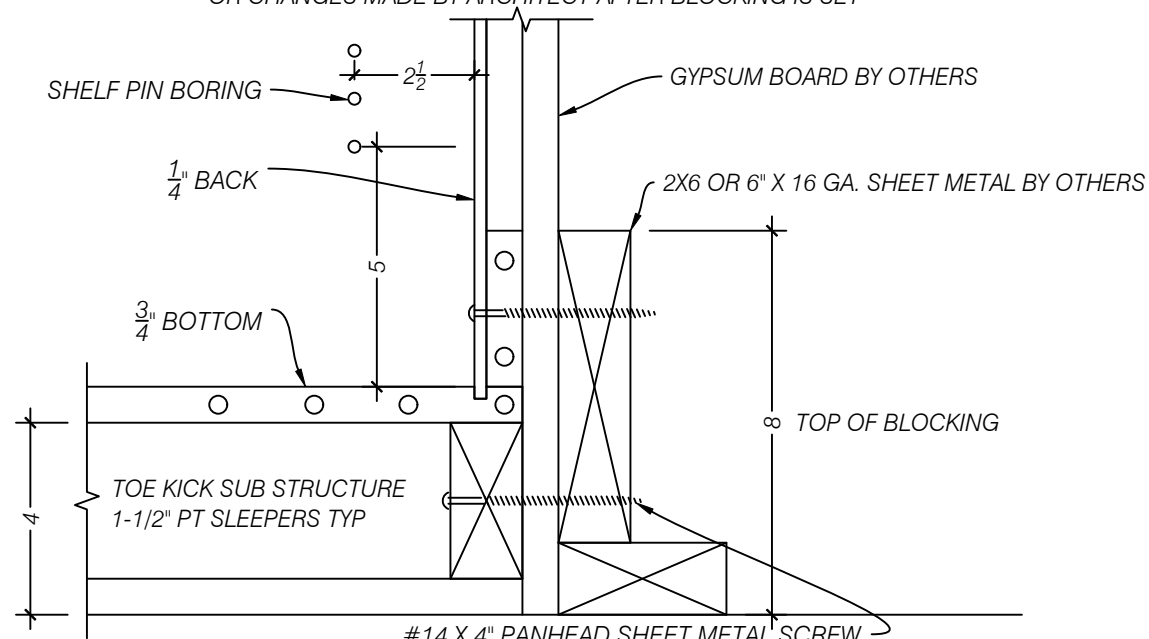


#14 X 4" PANHEAD SHEET METAL SCREW  
MIN. 4 FASTENERS (2 TOP, 2 BOTTOM)

FASTENERS TO BE LOCATED WITHIN 2" FROM TOP/BOTTOM  
FASTENERS TO BE LOCATED WITHIN 2" FROM THE OUTSIDE ENDS

**A** ENLARGED DETAIL - TYPICAL BASE CABINET ATTACHMENT @ WALL  
SCALE 1:4 (3"=1'-0")  
ARCH REF: NA


SHIMMING/SURFACE BLOCKING IS THE RESPONSIBILITY OF THE INSTALLER  
SURFACE BLOCKING/WALL CLEATS/Z-CLIPS WILL BE PROVIDED BY CRESTMARK (U.O.N.)  
CRESTMARK IS NOT RESPONSIBLE FOR GAPS DUE TO IRREGULAR WALL SURFACES  
IN THE EVENT OF EXTREME GAPS, A SURFACE MOUNT FLAT MOLDING WILL BE USED (U.O.N.)

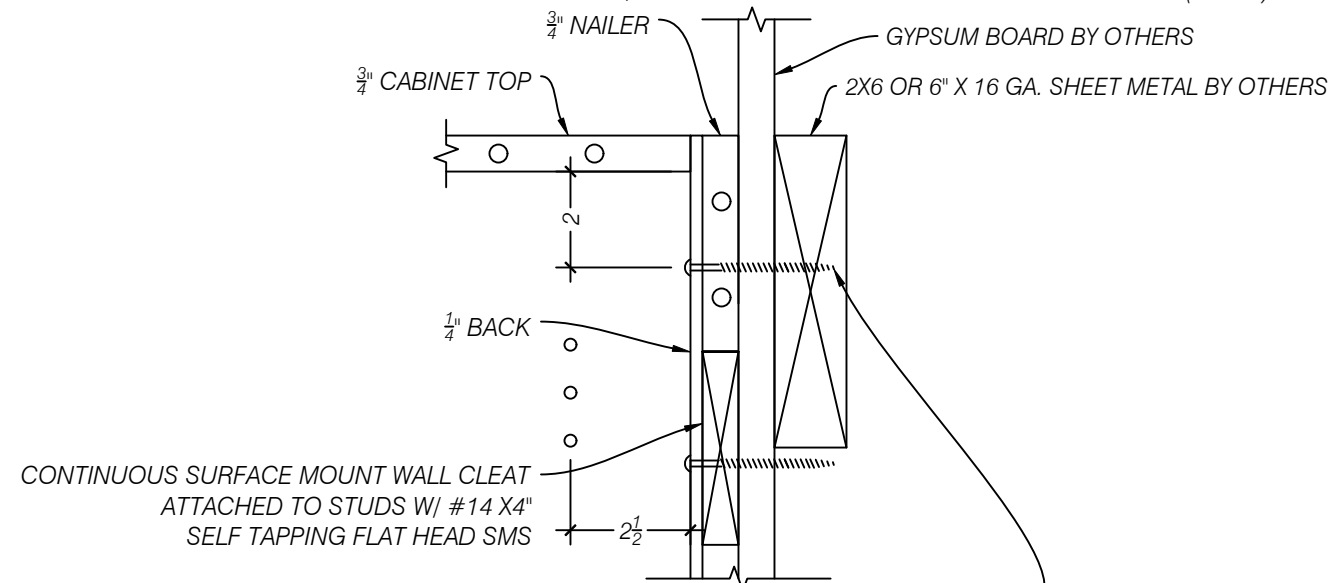


#14 X 4" PANHEAD SHEET METAL SCREW  
MIN. 4 FASTENERS (2 TOP, 2 BOTTOM)

FASTENERS TO BE LOCATED WITHIN 2" FROM TOP/BOTTOM  
FASTENERS TO BE LOCATED WITHIN 2" FROM THE OUTSIDE ENDS

**C** ENLARGED DETAIL - TYPICAL WALL CABINET ATTACHMENT @ WALL  
SCALE 1:4 (3"=1'-0")  
ARCH REF: NA

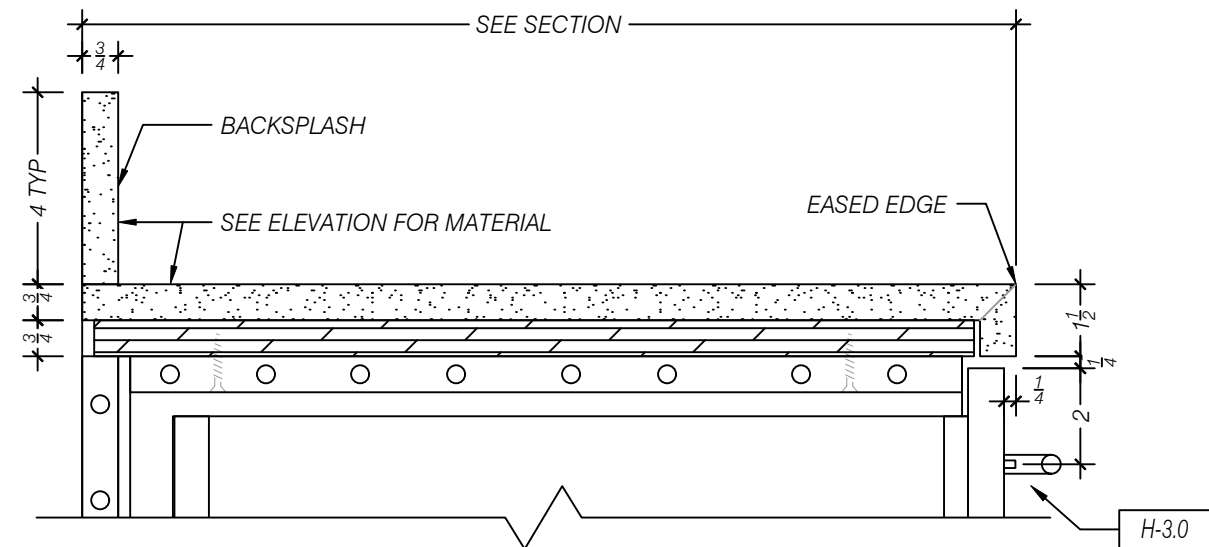


**B** ENLARGED DETAIL - COUNTERTOP DETAIL WITH PULL  
SCALE 1:4 (3"=1'-0")  
ARCH REF: NA

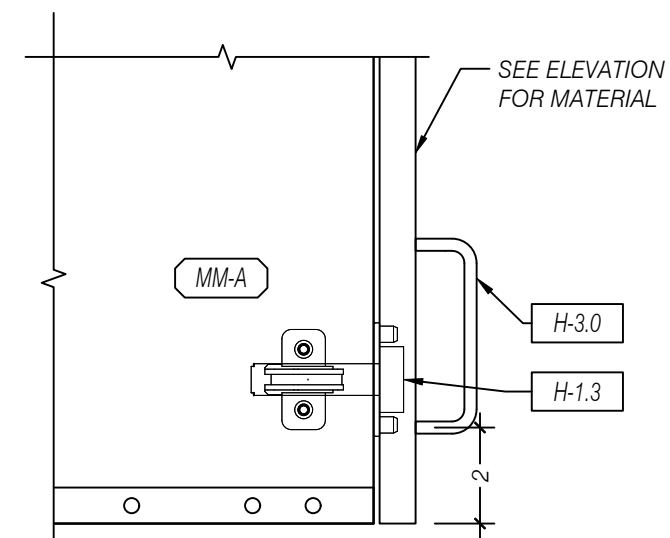

**D** ENLARGED DETAIL - UPPER CABINET PULL LOCATION  
SCALE 1:4 (3"=1'-0")  
ARCH REF: NA

**DGS SREOC COSTA  
MESA  
ENLARGED DETAILS**

| ISSUE        |                                          |       |       |  |
|--------------|------------------------------------------|-------|-------|--|
| DATE         | DESCRIPTION                              | BY    |       |  |
| 05/05/2026   | REV-A - FOR SUBMITTAL                    | Q-A-S |       |  |
|              |                                          |       |       |  |
|              |                                          |       |       |  |
| SITE ADDRESS |                                          |       |       |  |
| STREET       | 2301 South Shelley<br>Circle Bldg. A & B |       |       |  |
| CITY         | Costa Mesa                               |       |       |  |
| STATE        | CA                                       | ZIP   | 92626 |  |
| JOB #:       | 26034                                    | REV:  | A     |  |
| MOD #:       | #                                        | REL:  | N/A   |  |
| D4           |                                          |       |       |  |

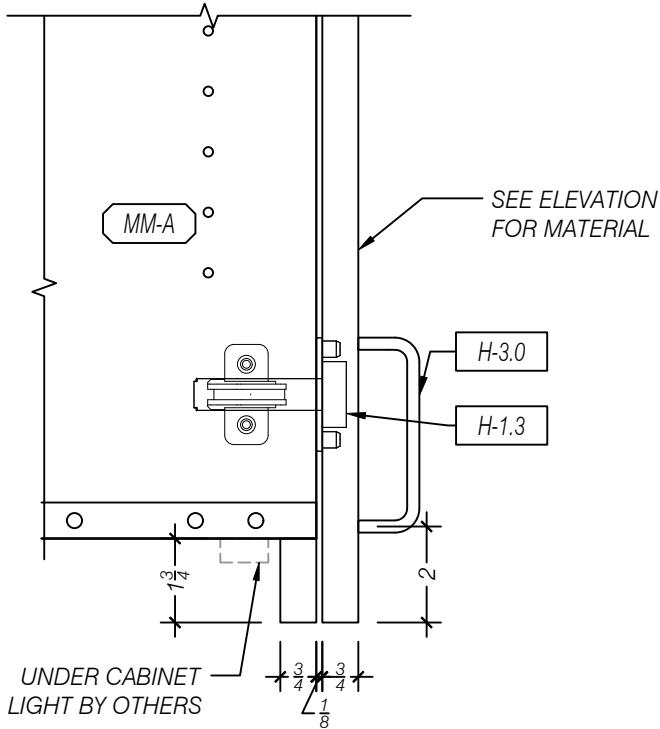

**A** ENLARGED DETAIL - UPPER CABINET PULL LOCATION w/ LIGHT VALANCE  
SCALE 1:4 (3"=1'-0")  
ARCH REF: NA

CRESTMARK

MILLWORK

5640 WEST END ROAD  
ARCATA, CA 95521  
PH (707) 822-4034 FAX (707) 822-5478  
WWW.CRESTMARKMILLWORK.COM

DGS SREOC COSTA

MESA

ENLARGED DETAILS

| ISSUE      |                       | BY   |  |
|------------|-----------------------|------|--|
| DATE       | DESCRIPTION           | BY   |  |
| 05/05/2026 | REV-A - FOR SUBMITTAL | Q-AS |  |
| -          | -                     | -    |  |
| -          | -                     | -    |  |
SITE ADDRESS

STREET

2301 South Shelley Circle Bldg. A & B

CITY

Costa Mesa

STATE

CA

ZIP

92626

JOB #:

26034

REV:

A

MOD #:

#

REL:

N/A

D5

M:\Libraries\Foundation Library 25\Factory Database\26034 - DGS\Details Room.dwg 05/05/26 - 7:28pm

© CRESTMARK MILLWORK, INC.